การประกอบเลขที่ 3707 B
ASSEMBLY NO. 3707 B

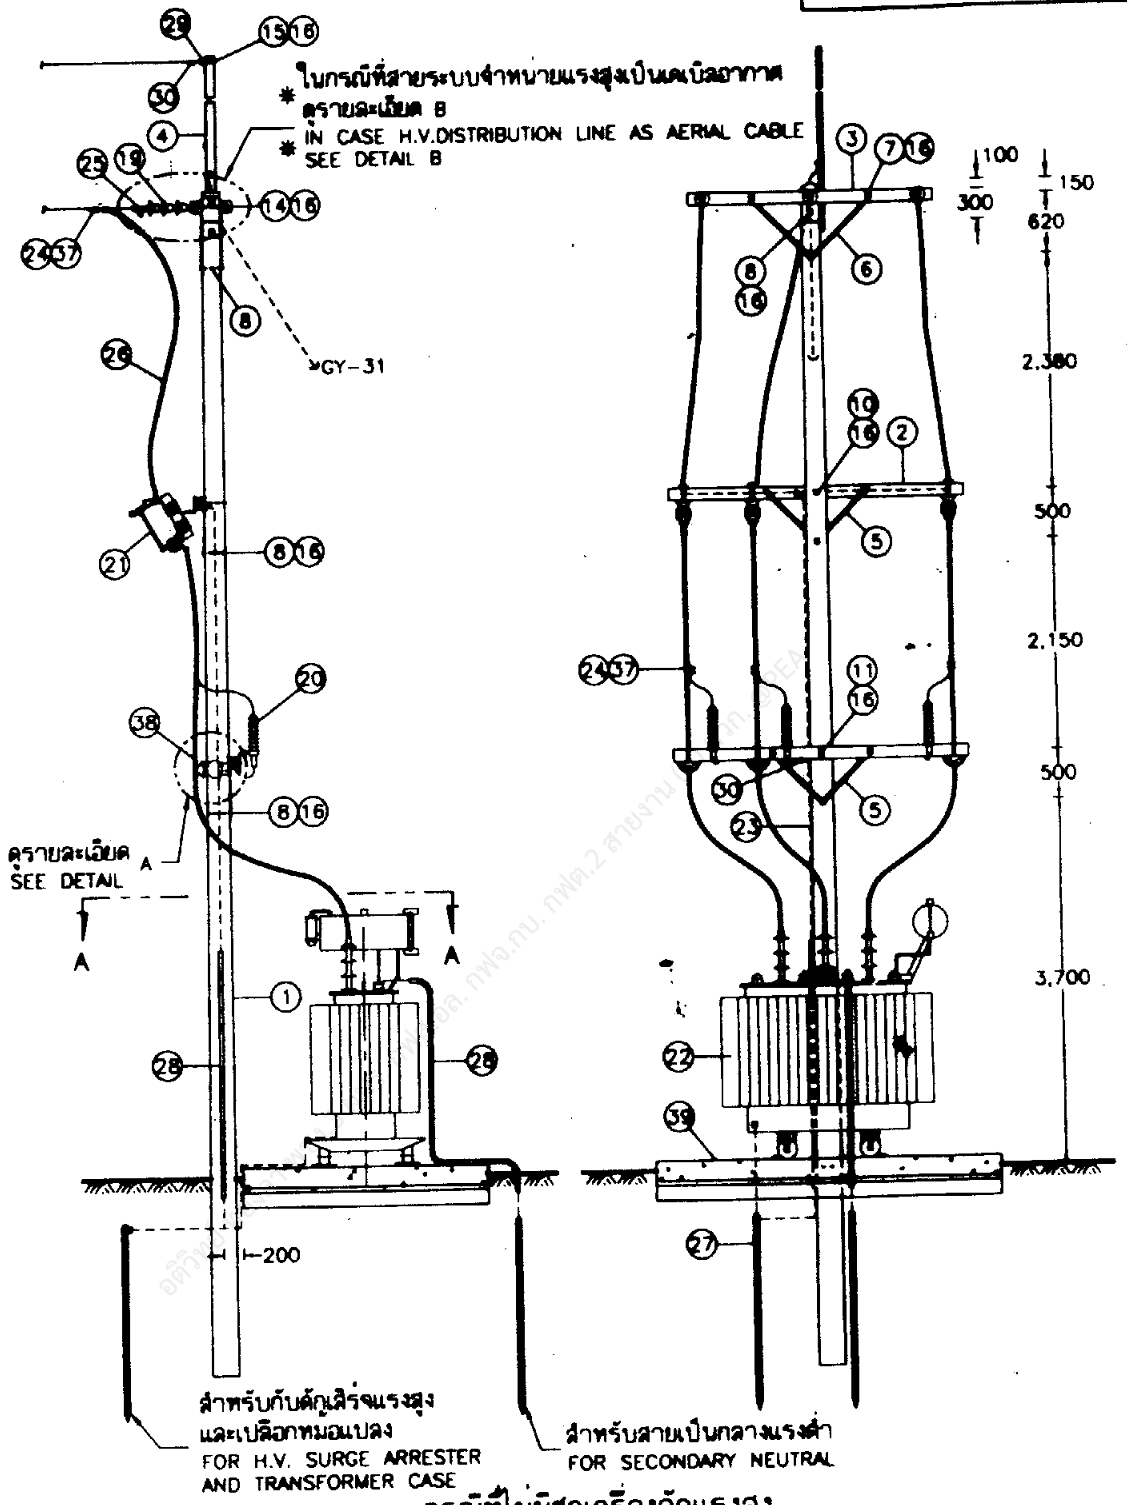

I กรณีที่ไม่มีชุดเครื่องวัดแรงสูง
WITHOUT H.V. METERING

กองมาตรฐานระบบไฟฟ้า
ฝ่ายมาตรฐานและความปลอดภัย

การไฟฟ้าส่วนภูมิภาค

ผู้เขียน Supphakit Boonruang
ผู้สำรวจ ....
วิศวกร ....
หัวหน้าแผนก ....
ผู้อำนวยการกอง ....
ผู้อำนวยการฝ่าย ....
รองผู้ว่าการวางแผนและพัฒนาระบบไฟฟ้า

ผู้ว่าการ ....

การติดตั้งหม้อแปลง ระบบ 33 kV ขนาด 315-2,000 kVA บนแท่น

33 kV 315-2,000 kVA TRANSFORMER INSTALLATION ON FOUNDATION

ใช้แทนแบบ SA1-015/35016
ถูกแทนโดยแบบ ....
เขียนเสร็จวันที่ 13 ก.พ. 2545
แก้แบบวันที่ ....
มิติเป็น มิลลิเมตร
มาตราส่วน 1 : 75
แบบเลขที่ SA2-015/45005
แผ่นที่ 1 ของจำนวน 8 แผ่น

การประกอบเลขที่ ASSEMBLY NO.	3707 B

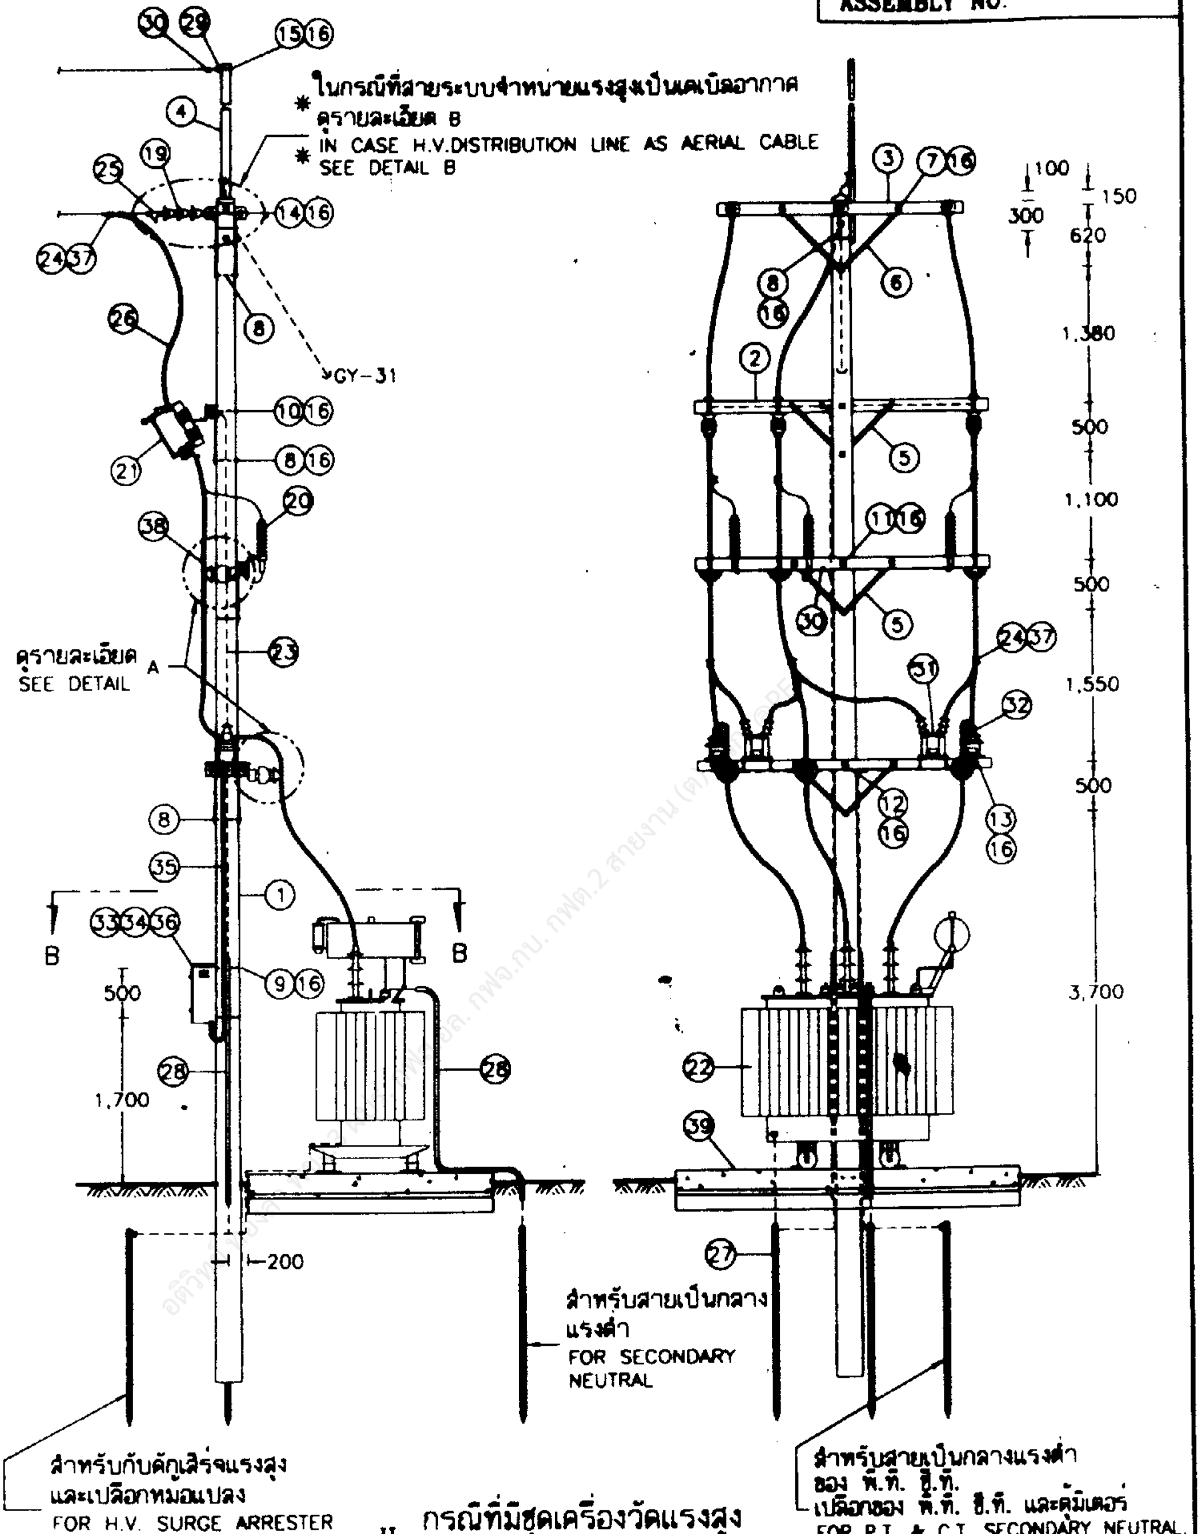
㉚㉙
⑮⑯
④
⑲
㉕
⑭⑯
㉔㊲
⑧
GY-31
㉖
⑩⑯
㉑
⑧⑯
⑳
㊳
㉓
ดูรายละเอียด A
SEE DETAIL
⑧
㉟
①
㉝㉞㊱
⑨⑯
B
B
500
1,700
㉘
㉘
200
* ในกรณีที่สายระบบจำหน่ายแรงสูงเป็นเคเบิลอากาศ ดูรายละเอียด B
* IN CASE H.V.DISTRIBUTION LINE AS AERIAL CABLE SEE DETAIL B
③
⑦⑯
⑧⑯
⑥
②
⑤
⑪⑯
㉚
⑤
㉔㊲
㉛
㉜
⑫⑯
⑬⑯
㉒
㊴
㉗
100
150
300
620
1,380
500
1,100
500
1,550
500
3,700
สำหรับสายเป็นกลางแรงต่ำ
FOR SECONDARY NEUTRAL
สำหรับกับดักเสิร์จแรงสูงและเปลือกหม้อแปลง
FOR H.V. SURGE ARRESTER AND TRANSFORMER CASE
สำหรับสายเป็นกลางแรงต่ำของ พี.ที. ซี.ที. เปลือกของ พี.ที. ซี.ที. และตู้มิเตอร์
FOR P.T. & C.T. SECONDARY NEUTRAL, P.T. & C.T. CASE AND METER CABINET

II กรณีที่มีชุดเครื่องวัดแรงสูง
WITH H.V. METERING

กองมาตรฐานระบบไฟฟ้า ฝ่ายมาตรฐานและความปลอดภัย	การไฟฟ้าส่วนภูมิภาค	ใช้แทนแบบ SA1-015/35016 ถูกแทนโดยแบบ ....
ผู้เขียน Supphakit Boonrung ผู้สำรวจ .... วิศวกร .... หัวหน้าแผนก .... ผู้อำนวยการกอง .... ผู้อำนวยการฝ่าย	ผู้ว่าการ .... การติดตั้งหม้อแปลง ระบบ 33 kV ขนาด 315-2,000 kVA บนแท่น	เขียนเสร็จวันที่ 13 ก.พ. 2545 แก้แบบวันที่ .... มิติเป็น มิลลิเมตร มาตราส่วน 1 : 75
รองผู้ว่าการวางแผนและพัฒนาระบบไฟฟ้า	33 kV 315-2,000 kVA TRANSFORMER INSTALLATION ON FOUNDATION	แบบเลขที่ SA2-015/45005 แผ่นที่ 2 ของจำนวน 8 แผ่น

การประกอบเลขที่ ASSEMBLY NO. 3707 B

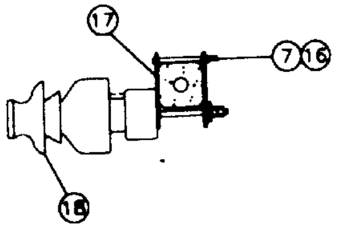

รายละเอียด A
DETAIL

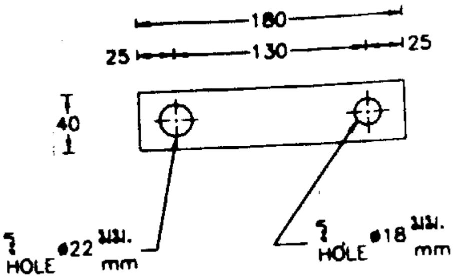

วัสดุลำดับที่ ⑰
MAT. ITEM

(อาจทำจากเหล็กประกับ
วัสดุเลขที่ 01200002 ได้)
(MAY BE MADE FROM BRACE
MAT. No. 01200002)

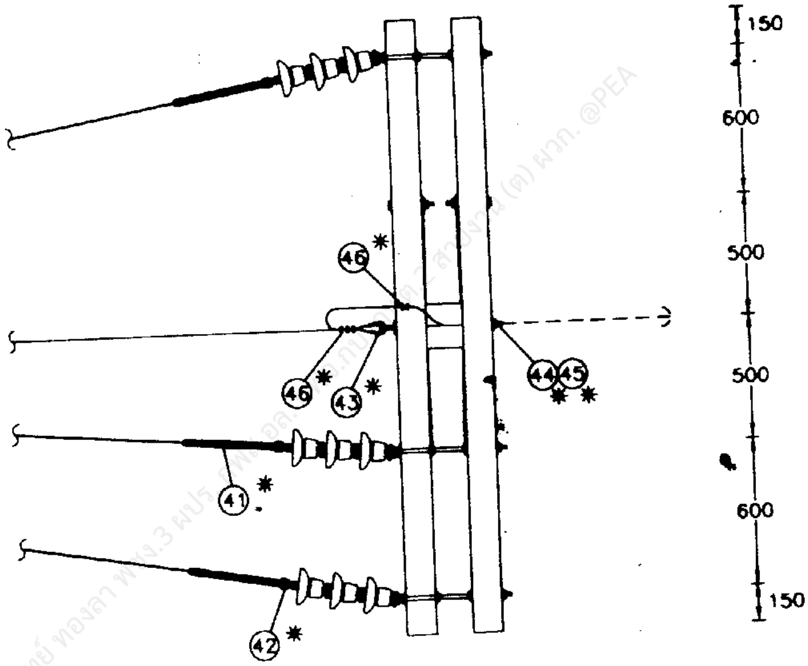

รายละเอียด B
DETAIL

กรณีสายระบบจำหน่ายแรงสูงเป็นเคเบิลอากาศ
IN CASE H.V.DISTRIBUTION LINE AS SPACE AERIAL CABLE

กองมาตรฐานระบบไฟฟ้า ฝ่ายมาตรฐานและความปลอดภัย	การไฟฟ้าส่วนภูมิภาค	ใช้แทนแบบ SA1-015/35016 ถูกแทนโดยแบบ เขียนเสร็จวันที่ 13 ก.พ. 2545
ผู้เขียน Supphakit Boonrung ผู้สำรวจ วิศวกร เกียรติไกร หัวหน้าแผนก ผู้อำนวยการกอง ผู้อำนวยการฝ่าย	ผู้ว่าการ	แก้แบบวันที่ มิติเป็น มิลลิเมตร มาตราส่วน –
	การติดตั้งหม้อแปลง ระบบ 33 kV ขนาด 315–2,000 kVA บนแท่น	
รองผู้ว่าการวางแผน และพัฒนาระบบไฟฟ้า	33 kV 315–2,000 kVA TRANSFORMER INSTALLATION ON FOUNDATION	แบบเลขที่ SA2-015/45005 แผ่นที่ 3 ของจำนวน 8 แผ่น

การประกอบเลขที่ ASSEMBLY NO. 3707 B

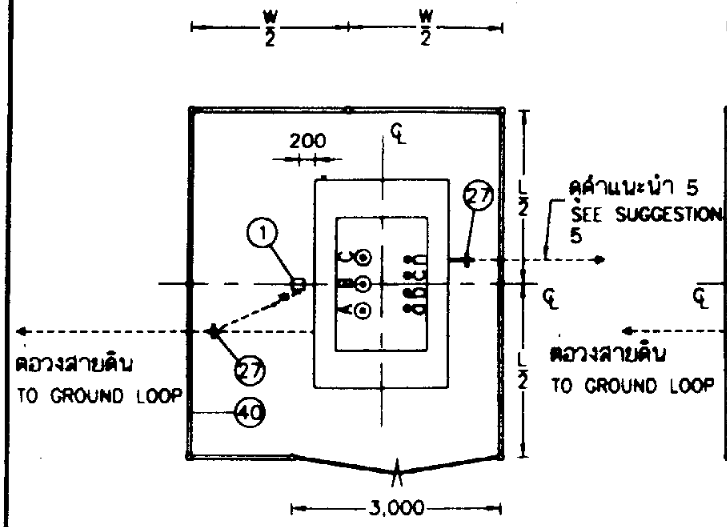

รูปตัด SECTION A–A

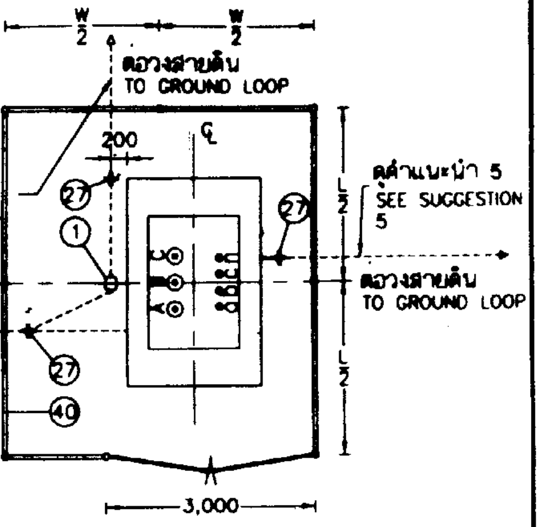

รูปตัด SECTION B–B

ไดอะแกรมการต่อลงดิน
EARTHING DIAGRAM

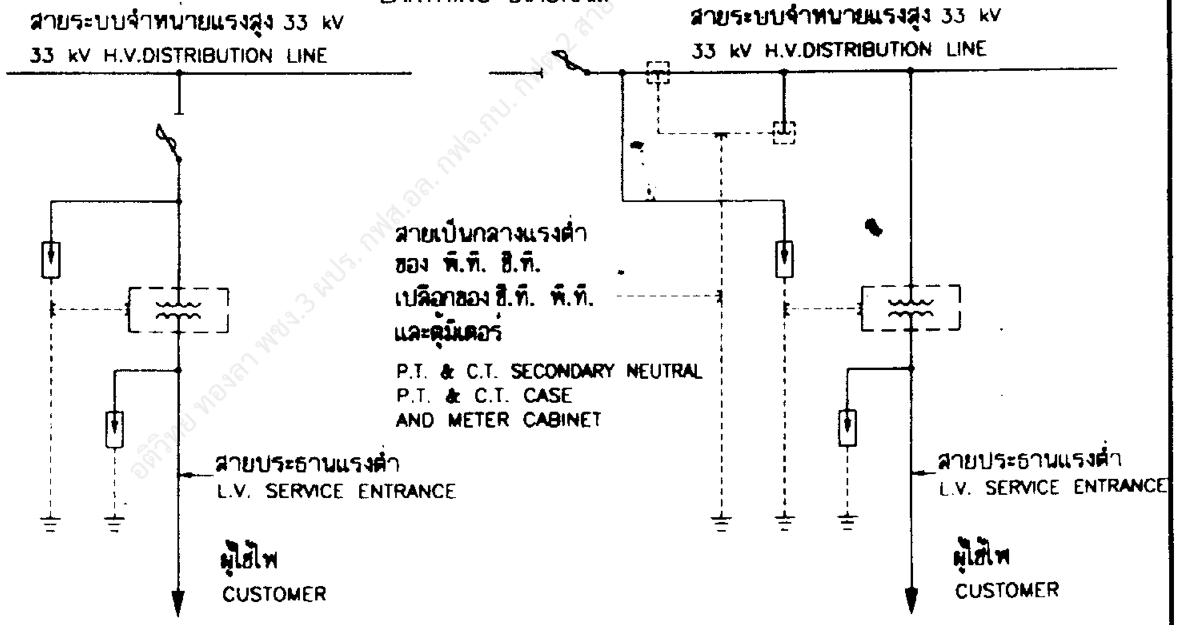
สายระบบจำหน่ายแรงสูง 33 kV
33 kV H.V.DISTRIBUTION LINE
สายระบบจำหน่ายแรงสูง 33 kV
33 kV H.V.DISTRIBUTION LINE
สายเป็นกลางแรงต่ำของ พี.ที. ซี.ที. เปลือกของ ซี.ที. พี.ที. และตู้มิเตอร์
P.T. & C.T. SECONDARY NEUTRAL
P.T. & C.T. CASE
AND METER CABINET
สายประธานแรงต่ำ
L.V. SERVICE ENTRANCE
ผู้ใช้ไฟ
CUSTOMER
สายประธานแรงต่ำ
L.V. SERVICE ENTRANCE
ผู้ใช้ไฟ
CUSTOMER

I กรณีที่ไม่มีชุดเครื่องวัดแรงสูง
WITHOUT H.V. METERING

II กรณีที่มีชุดเครื่องวัดแรงสูง
WITH H.V. METERING

อดิวิชย ทองลา พชง.3 ฝปร. กฟส.อล. กฟจ.กบ. กฟต.2 สายงาน (ต) ผวก.

กองมาตรฐานระบบไฟฟ้า
ฝ่ายมาตรฐานและความปลอดภัย
ผู้เขียน Supphakit Boonruang
ผู้สำรวจ ....
วิศวกร ....
หัวหน้าแผนก ....
ผู้อำนวยการกอง ....
ผู้อำนวยการฝ่าย ....

รองผู้ว่าการวางแผนและพัฒนาระบบไฟฟ้า

การไฟฟ้าส่วนภูมิภาค

ผู้ว่าการ ....

การติดตั้งหม้อแปลง ระบบ 33 kV
ขนาด 315–2,000 kVA บนแท่น

33 kV 315–2,000 kVA TRANSFORMER
INSTALLATION ON FOUNDATION

ใช้แทนแบบ SA1-015/35016
ถูกแทนโดยแบบ ....
เขียนเสร็จวันที่ 13 ก.พ. 2545
แก้แบบวันที่ ....
มิติเป็น มิลลิเมตร
มาตราส่วน -
แบบเลขที่ SA2-015/45005
แผ่นที่ 4 ของจำนวน 8 แผ่น

การประกอบเลขที่ ASSEMBLY NO.	3707 B

บัญชีวัสดุ
BILL OF MATERIAL

ลำดับที่ ITEM	รายละเอียด DESCRIPTION	จำนวน REQ'D I	 II	วัสดุเลขที่ MAT. NO.
1	เสาคอนกรีต 12 เมตร POLE, CONCRETE, 12 m LONG	1	1	00010004
2	คอน คอร. สปัน ขนาด 120x120x3,000 มม. CROSSARM, SPUN PRESTRESSED CONCRETE, 120x120x3,000 mm	2	4	00110002
3	คอน คอร. สปัน (สำหรับเข้าปลายสาย) 120x120x2,500 มม. CROSSARM, SPUN PRESTRESSED CONCRETE (FOR DEADEND), 120x120x2,500 mm	2	2	00110004
4	เหล็กรูปรางน้ำรับสายล่อฟ้า ต้นเข้าปลายสาย ขนาด 100x50x5 มม. ยาว 2.25 ม. OVERHEAD GROUND WIRE DEADEND BAYONET, CHANNEL STEEL, 100x50x5 mm, 2.25 m LONG	1	1	01000100
5	เหล็กประกับคอน 30x6x760 มม. BRACE, FLAT, FOR CROSSARM, 30x6x760 mm	4	8	01200001
6	เหล็กประกับคอน 40x6x1,000 มม. BRACE, FLAT, FOR CROSSARM, 40x6x1,000 mm	4	4	01200002
7	สลักเกลียว M 16x170 มม. BOLT, MACHINE, M 16x170 mm	11	18	01110201
8	สลักเกลียว M 16x250 มม. BOLT, MACHINE, M 16x250 mm	5	6	01110203
9	สลักเกลียว M 16x300 มม. BOLT, MACHINE, M 16x300 mm	–	2	01110204
10	สลักเกลียว M 16x350 มม. BOLT, MACHINE, M 16x350 mm	1	1	01110205
11	สลักเกลียว M 16x400 มม. BOLT, MACHINE, M 16x400 mm	1	1	01110206
12	สลักเกลียว M 16x500 มม. BOLT, MACHINE, M 16x500 mm	–	1	01110208
13	สลักเกลียวตลอด M 16x450 มม. BOLT, DOUBLE ARMING, M 16x450 mm	–	2	01120001
14	สลักเกลียวหัวงกลม M 16x450 มม. BOLT, DOUBLE ARMING, ROUND EYE, M 16x450 mm	3	3	01130000
15	สลักหัวงกลม M 16x200 มม. BOLT, ROUND EYE, M 16x200 mm	1	1	01140001
16	แหวนสี่เหลี่ยมแบน 52x52x4.5 มม. รู ø18 มม. มอก. 258 WASHER, SQUARE, FLAT, 52x52x4.5 mm, HOLE. ø18 mm, TIS 258	31	60	01180100
17	แผ่นเหล็ก 40x6 มม. ยาว 200 มม. เจาะรูตามแบบ แผ่นที่ 3 STEEL, PLATE, 40x6 mm, 200 mm LONG ; PUNCH HOLE AS DWG.,ON SHEET No.3	6	12	–
18	ลูกถ้วยแท่งหรือลูกถ้วยแท่งก้านตรง 33 kV ชนิดตามต้องการ INSULATOR, LINE POST TYPE OR PIN-POST TYPE, 33 kV, TYPE AS REQ.	3	6	03000003 03010102 03010103
19	ลูกถ้วยแขวน มอก 354 แบบ ง (แบบ 52-4) INSULATOR, SUSPENSION TYPE, TIS 354, TYPE D (CLASS 52-4)	9	9	03020002
20	กับดักเสิร์จแรงสูง 30 kV 5 กิโลแอมป์ H.V. SURGE ARRESTER, 30 kV, 5 kA	3	3	04000100

กองมาตรฐานระบบไฟฟ้า ฝ่ายมาตรฐานและความปลอดภัย	การไฟฟ้าส่วนภูมิภาค	ใช้แทนแบบ SA1-015/35016 ถูกแทนโดยแบบ ....
ผู้เขียน Supphakit Boonrueng ผู้สำรวจ .... วิศวกร .... หัวหน้าแผนก .... ผู้อำนวยการกอง .... ผู้อำนวยการฝ่าย	ผู้ว่าการ	เขียนเสร็จวันที่ 13 ก.พ. 2545 แก้แบบวันที่ ....
	การติดตั้งหม้อแปลง ระบบ 33 kV ขนาด 315-2,000 kVA บนแท่น	มิติเป็น .... มาตราส่วน ....
รองผู้ว่าการวางแผน และพัฒนาระบบไฟฟ้า	33 kV 315-2,000 kVA TRANSFORMER INSTALLATION ON FOUNDATION	แบบเลขที่ SA2-015/45005 แผ่นที่ 5 ของจำนวน 8 แผ่น

การประกอบเลขที่
ASSEMBLY NO. 3707 B

บัญชีวัสดุ
BILL OF MATERIAL

ลำดับที่ ITEM	รายละเอียด DESCRIPTION	จำนวน REQ'D		วัสดุเลขที่ MAT. NO.
		I	II	
21	ดรอพเอาต์ ฟิวส์คัตเอาต์ หนึ่ง อินซูเลเตอร์ 33 kV, 100 A CUTOUT, FUSE, OPEN TYPE, SINGLE INSULATOR, DROPOUT, 33 kV, 100 A.	3	3	04010101
22	หม้อแปลง 3 เฟส 33 kV ขนาดตามต้องการ TRANSFORMER, 3-PHASE, 33 kV, SIZE AS REQUIRED	1	1	05010107 _ 05010113
23	ลวดเหล็กตีเกลียว 50/7 ต.มม. มอก. 404 ความยาวตามต้องการ WIRE, STEEL STRANDED, 50/7 mm^2 TIS 404 ; LENGTH AS REQUIRED	ม. m	ม. m	01100004
24	พี.จี. คอนเนคเตอร์สลักคู่ สำหรับสายอะลูมิเนียม ขนาด 25-95 ต.มม. CONNECTOR, PARALLEL GROOVE, DOUBLE BOLTS, Al, 25-95 mm^2	9	13	02300102
25	สเตรนแคลมป์ สำหรับสายอะลูมิเนียม ขนาด 35-95 ต.มม. อะลูมิเนียมแกนเหล็ก 35-70 ต.มม. CLAMP, STRAIN, FOR 35-95 mm^2 Al COND., AND 35-70 mm^2 ACSR	3	3	03110000 03110001 03110101
26	สาย PIC หรือเคเบิลอากาศ อะลูมิเนียม 33 kV ขนาด 50-95 ต.มม. PARTIALLY INSULATED CONDUCTOR OR SPACE AERIAL CABLE, Al, 33 kV, 50-95 mm^2	ม. 30 m	ม. 36 m	02060101-2 02050100-1
27	หลักดิน 60x60x5 มม. ยาว 2 ม. GROUND ROD 60x60x5 mm, 2 m LONG	2.	3	01220002
28	ท่อ PVC แข็ง ขนาด ø20x2,500-4,000 มม. พร้อมอุปกรณ์ยึด CONDUIT, PVC RIGID, ø20x2,500-4,000 mm ; COMP. WITH FIXING ACCESSORIES	2	3	08040001-2
29	กายทิมเบิล สำหรับสายยึดโยง 50-95 ต.มม. THIMBLE, GUY, FOR 50-95 mm^2	1	1	01210304
30	ยูแคลมป์ สลัก 1 ตัว M 8 CLAMP, SINGLE U-BOLT, M 8	18	24	01230000
31	พี.ที.หนึ่งเฟสใช้นอกอาคาร 33,000-110 V พร้อมอุปกรณ์ติดตั้ง TRANSFORMER, POTENTIAL, 1-ø, OUTDOOR, 33,000-110 V ; COMP. WITH MOUNTING ACCESS	–	2	06020100
32	ซี.ที. ใช้นอกอาคาร 33 kV เรโชตามต้องการ พร้อมอุปกรณ์ติดตั้ง TRANSFORMER, CURRENT, OUTDOOR, 33 kV, RATIO AS REQ'D ; COMP. WITH MOUNTING ACCESS.	–	2	06040101 _ 06040104
33	ตู้ใส่มิเตอร์แรงสูง พร้อมแป้นไม้ ALUMINIUM METER CABINET, FOR H.V. METER ; COMP. WITH METER PLATE	–	1	06100007
34	ดีมานด์มิเตอร์ ชนิดสะสม 3 เฟส 3 สาย DEMAND METER, CUMULATIVE, 3-PHASE, 3-WIRE	–	1	06000203
35	เคเบิลควบคุม ขนาด 7x2.5 ต.มม. มอก. 838 CONTROL CABLE, SIZE 7x2.5 mm^2 TIS. 838	–	ม. 8 m	02080402
36	ตะปูเกลียวชุบโครมเมี่ยม ขนาด 15-20 มม. SCREW, CHROME-PLATED, SIZE 15-20 mm	–	3	–
37	เทปพันสายเคเบิลอากาศแรงสูง ขนาด 3/4"x30' ELECTRICAL, SPLICING TAPE, FOR H.T. AERIAL CABLE; SIZE 3/4"x30'	ม้วน roll	ม้วน roll	02180003
38	ลวดอะลูมิเนียมกลม ø4 มม. ความยาวตามต้องการ TIE WIRE, Al ø4 mm; LENGTH AS REQUIRED	ม. m	ม. m	02200002
39	แท่นตั้งหม้อแปลง ขนาดตามต้องการ TRANSFORMER FOUNDATION ; SIZE AS REQUIRED	1	1	–
40	รั้วตาข่ายล้อมหม้อแปลง ขนาดตามต้องการ TRANSFORMER WIRE-MESH FENCE ; SIZE AS REQUIRED	1	1	–

กองมาตรฐานระบบไฟฟ้า
ฝ่ายมาตรฐานและความปลอดภัย

ผู้เขียน Supphakit Boonrung
ผู้สำรวจ
วิศวกร
หัวหน้าแผนก
ผู้อำนวยการกอง
ผู้อำนวยการฝ่าย

รองผู้ว่าการวางแผน
และพัฒนาระบบไฟฟ้า

การไฟฟ้าส่วนภูมิภาค

ผู้ว่าการ

การติดตั้งหม้อแปลง ระบบ 33 kV
ขนาด 315-2,000 kVA บนแท่น

33 kV 315-2,000 kVA TRANSFORMER
INSTALLATION ON FOUNDATION

ใช้แทนแบบ SA1-015/35016
ถูกแทนโดยแบบ
เขียนเสร็จวันที่ 13 ก.พ. 2545
แก้แบบวันที่
มิติเป็น
มาตราส่วน

แบบเลขที่ SA2-015/45005
แผ่นที่ 6 ของจำนวน 8 แผ่น

การประกอบเลขที่ ASSEMBLY NO.	3707 B

บัญชีวัสดุ
BILL OF MATERIAL

ลำดับที่ ITEM	รายละเอียด DESCRIPTION	จำนวน REQ'D I	II	วัสดุเลขที่ MAT NO.
	กรณีสายระบบจำหน่ายแรงสูงเป็นเคเบิลอากาศ IN CASE H.V. DISTRIBUTION LINE AS SPACE AERIAL CABLE			
41 *	ปรีฟอร์มเข้าปลายสาย สำหรับเคเบิลอากาศอะลูมิเนียม ขนาดตามต้องการ PREFORMED DEAD END FOR SPACE AERIAL CABLE, Al ; SIZE AS REQUIRED	3	3	02250101 02250200
42 *	ทิมเบิลเคลวิส สำหรับปรีฟอร์มเข้าปลายสาย CLEVIS THIMBLE FOR PREFORMED DEAD END	3	3	03140011
43 *	กายทิมเบิล สำหรับสายยึดโยง 50-95 ต.มม. THIMBLE GUY FOR STEEL WIRE 50-95 mm^2	1	1	06100007
44 *	สลักเกลียวหางกลม M 16x450 มม. BOLT, DOUBLE ARMING, ROUND EYE, M 16x450 mm	1	1	01130000
45 *	แหวนสี่เหลี่ยมแบน 52x52x4.5 มม. รู ø18 มม. มอก. 258 WASHER, SQUARE, FLAT, 52x52x4.5 mm, HOLE ø18 mm, TIS 258	2	2	01180100
46 *	ยูแคลมป์ สลัก 1 ตัว M 8 CLAMP, SINGLE U-BOLT, M 8	5	5	01230000

หมายเหตุ

บัญชีวัสดุ :-

สดมภ์ I : สำหรับกรณีที่ไม่มีชุดเครื่องวัดแรงสูง

สดมภ์ II : สำหรับกรณีที่มีชุดเครื่องวัดแรงสูง

NOTES

BILL OF MATERIAL :-

COLUMN I : FOR USE IN CASE OF WITHOUT H.V. METERING

COLUMN II : FOR USE IN CASE OF WITH H.V. METERING

	แบบอ้างอิง REFERENCE DRAWING	แบบเลขที่ DWG.No.	การประกอบเลขที่ ASSEMBLY No.
1	แท่นตั้งหม้อแปลง TRANSFORMER FOUNDATION	I41-015/090466	8504
2	แบบรั้วตาข่ายล้อมหม้อแปลง และการต่อลงดิน TRANSFORMER WIRE-MESH FENCE AND GROUNDING	SA1-015/23061	8505
3	รหัสสีของเคเบิลควบคุม สำหรับมิเตอร์แรงสูง 11-33 kV COLOUR CODE OF CONTROL CABLE, FOR 11-33 kV, H.V. METER	S02-015/16005	0506
4	การต่อลงดิน ระบบแรงสูง และแรงต่ำ แผ่นที่ 6 และ 17 H.V. AND L.V. EARTHING SYSTEM, SHEET NO. 6 AND 17	S02-015/20039	9701
5	การประกอบสายลงดิน วิธียึดลวดเหล็ก GROUND LEAD ASSEMBLY, STEEL WIRE FITTING	S02-015/19166 SA1-015/31012	9703 9703 A
6	การประกอบที่ยึดท่อ PVC สำหรับสายดิน PVC PIPE FITTING ASSEMBLY, FOR GROUND WIRE	S02-015/19128 SA1-015/31013	9704 9704 A
7	เหล็กรับสายล่อฟ้า สำหรับระบบจำหน่าย 22 kV และ 33 kV OVERHEAD GROUND WIRE BAYONET FOR 22 kV AND 33 kV DISTRIBUTION SYSTEMS	SA1-015/31050	2424 3201 A

กองมาตรฐานระบบไฟฟ้า ฝ่ายมาตรฐานและความปลอดภัย	การไฟฟ้าส่วนภูมิภาค	ใช้แทนแบบ SA1-015/35016 ถูกแทนโดยแบบ .... เขียนเสร็จวันที่ 13 ก.พ. 2545 แก้แบบวันที่ .... มิติเป็น .... มาตราส่วน ....
ผู้เขียน Supphakit Boonrung ผู้สำรวจ .... วิศวกร .... หัวหน้าแผนก .... ผู้อำนวยการกอง .... ผู้อำนวยการฝ่าย	ผู้ว่าการ .... การติดตั้งหม้อแปลง ระบบ 33 kV ขนาด 315-2,000 kVA บนแท่น	
รองผู้ว่าการวางแผนและพัฒนาระบบไฟฟ้า	33 kV 315-2,000 kVA TRANSFORMER INSTALLATION ON FOUNDATION	แบบเลขที่ SA2-015/45005 แผ่นที่ 7 ของจำนวน 8 แผ่น

การประกอบเลขที่ ASSEMBLY NO.	3707 B

คำแนะนำ

1. ล้อหม้อแปลงทั้งหมด ต้องจัดทำที่สำหรับกั้นไม่ให้หม้อแปลงเคลื่อนที่ได้
2. เลือกตำแหน่งประตูรั้วล้อมหม้อแปลงตามความเหมาะสม
3. ด้านแรงต่ำ ผู้ใช้ไฟเป็นผู้จัดทำ
4. กรณีสายระบบจำหน่ายแรงสูงเป็นสายเคเบิลอากาศ ให้ตัดวัสดุในบัญชีวัสดุ ลำดับที่ 4, 15, และ 28 ออก และลดจำนวนวัสดุลำดับที่ 8, 16 และ 30 ลง 2, 3 และ 4 ตามลำดับ
5. สายต่อลงดินด้านแรงต่ำ สามารถต่อเข้ารวมกับวงสายดินได้ ถ้าความต้านทานรวมของวงสายดินไม่เกิน 2 โอห์ม (กรณีดินเปียกชื้น) และไม่เกิน 5 โอห์ม (กรณีดินแห้ง) นอกเหนือจากนี้ สายต่อลงดินด้านแรงต่ำให้ร้อยในท่อ พีวีซี. และต่อเข้ากับหลักดินที่ปักอยู่ห่างจากวงสายดินไม่น้อยกว่า 3 เมตร

หมายเหตุ :

1. กรณีพาดสายช่วงเสาไม่รับแรงดึง (ไม่มีสายยึดโยง) :
   - สำหรับสายอะลูมิเนียมเปลือย ขนาด 50-95 ต.มม.
     ระยะช่วงเสาสูงสุด : 20 ม.
     ระยะหย่อนยานของสายต่ำสุด : 0.90 ม.
   - สำหรับเคเบิลอากาศ ขนาด 50-95 ต.มม.
     ระยะช่วงเสาสูงสุด : 10 ม.
     ระยะหย่อนยานของสายทุกเส้นต่ำสุด : 0.80 ม.
2. กรณีพาดสายช่วงเสารับแรงดึง (มีสายยึดโยง) :
   - สำหรับสายอะลูมิเนียมเปลือย ขนาด 50 ต.มม.
     ระยะช่วงเสาสูงสุด : 50 ม.
     ระยะหย่อนยานของสายต่ำสุด : 0.50 ม.
   - สำหรับสายอะลูมิเนียมเปลือย ขนาด 95 ต.มม.
     ระยะช่วงเสาสูงสุด : 80 ม.
     ระยะหย่อนยานของสายต่ำสุด : 1.00 ม.
   - สำหรับเคเบิลอากาศ ขนาด 50-95 ต.มม.
     ระยะช่วงเสาสูงสุด : 40 ม.
     ระยะหย่อนยานของสายแขวนเคเบิลสเปเซอร์ : ตามมาตรฐาน กฟภ.

SUGGESTIONS

1. ALL TRANSFORMER'S ROLLERS SHALL BE PROVIDED WITH STOPPER, TO PREVENT TRANSFORMER MOVING.
2. SUITABLE POSITION FOR FENCE'S GATE.
3. LOW TENSION SIDE SHALL BE PROVIDED BY CUSTOMER
4. FOR H.V. DISTRIBUTION LINE AS SPACE AERIAL CABLE : THE MATERIALS ITEMS 4, 15 AND 29 MUST BE OMITED AND ITEMS 8, 16 AND 30 MUST BE REDUCED BY 2, 3 AND 4 RESPECTIVELY, IN THE BILL OF MATERIAL
5. L.V. GROUNDING CONDUCTOR CAN BE CONNECT WITH GROUND LOOP WHEN TOTAL GROUND RESISTANCE OF GROUND LOOP NOT EXCEED 2 OHM (MOIST SOIL) OR NOT EXCEED 5 OHM (DRY SOIL). IN THE OTHER CASE L.V. GROUNDING CONDUCTOR SHALL BE INSERTED IN PVC CONDUIT AND CONNECT WITH GROUND ROD WHICH HAVE DISTANCE NO LESS THAN 3 METER FROM GROUND LOOP.

NOTES :

1. IN CASE OF SLACK SPAN SECTION (WITHOUT GUY) :
   - FOR 50-95 mm^2 BARED Al CONDUCTORS
     MAX. SPAN LENGTH : 20 m
     MIN. SAG OF CONDUCTORS : 0.90 m
   - FOR 50-95 mm^2 SAC CABLES
     MAX. SPAN LENGTH : 10 m
     MIN. SAG OF ALL CONDUCTORS : 0.80 m
2. IN CASE OF TENSION SPAN SECTION (WITH GUY) :
   - FOR 50 mm^2 BARED Al CONDUCTOR
     MAX. SPAN LENGTH : 50 m
     MIN. SAG OF CONDUCTORS : 0.50 m
   - FOR 95 mm^2 BARED Al CONDUCTOR
     MAX. SPAN LENGTH : 80 m
     MIN. SAG OF CONDUCTORS : 1.00 m
   - FOR 50-95 mm^2 SAC CABLES
     MAX. SPAN LENGTH : 40 m
     MIN. SAG OF MESSENGER : AS PER PEA STANDARD

คำเตือน

ในการติดตั้งตู้ใส่มิเตอร์ ให้ดำเนินการตามมาตรการ และวิธีปฏิบัติเกี่ยวกับการละเมิดสิทธิการใช้ไฟฟ้า โดยการเลี่ยงมิเตอร์ ตามบันทึกที่ มต. 2145 ลว. 31 พ.ค. 2528 (อนุมัติ ผวก. ลว. 28 พ.ค. 2528) ดังนี้ :

(1) การยึดแป้นไม้มิเตอร์ และตู้ใส่มิเตอร์ ให้ยึดด้วยสลักเกลียว 2 ชุด โดยให้แป้นเกลียวของสลักเกลียวอยู่ในตู้
(2) ให้เจาะรูร้อยลวด ติดราตะกั่วที่ปลายสลัก ตามข้อ (1) ทั้ง 2 ชุด
(3) ให้ร้อยลวดติดราตะกั่ว ที่ฝาตู้ใส่มิเตอร์ ทั้ง 2 ชุด

กองมาตรฐานระบบไฟฟ้า ฝ่ายมาตรฐานและความปลอดภัย	การไฟฟ้าส่วนภูมิภาค	ใช้แทนแบบ SA1-015/35016 ถูกแทนโดยแบบ ....
ผู้เขียน Supphakit Boonrung ผู้สำรวจ .... วิศวกร .... หัวหน้าแผนก .... ผู้อำนวยการกอง .... ผู้อำนวยการฝ่าย	ผู้ว่าการ	เขียนเสร็จวันที่ 13 ก.พ. 2545 แก้แบบวันที่ ....
	การติดตั้งหม้อแปลง ระบบ 33 kV ขนาด 315-2,000 kVA บนแท่น	มิติเป็น .... มาตราส่วน ....
รองผู้ว่าการวางแผน และพัฒนาระบบไฟฟ้า	33 kV 315-2,000 kVA TRANSFORMER INSTALLATION ON FOUNDATION	แบบเลขที่ SA2-015/45005 แผ่นที่ 8 ของจำนวน 8 แผ่น