การประกอบเลขที่ ASSEMBLY NO. 3412

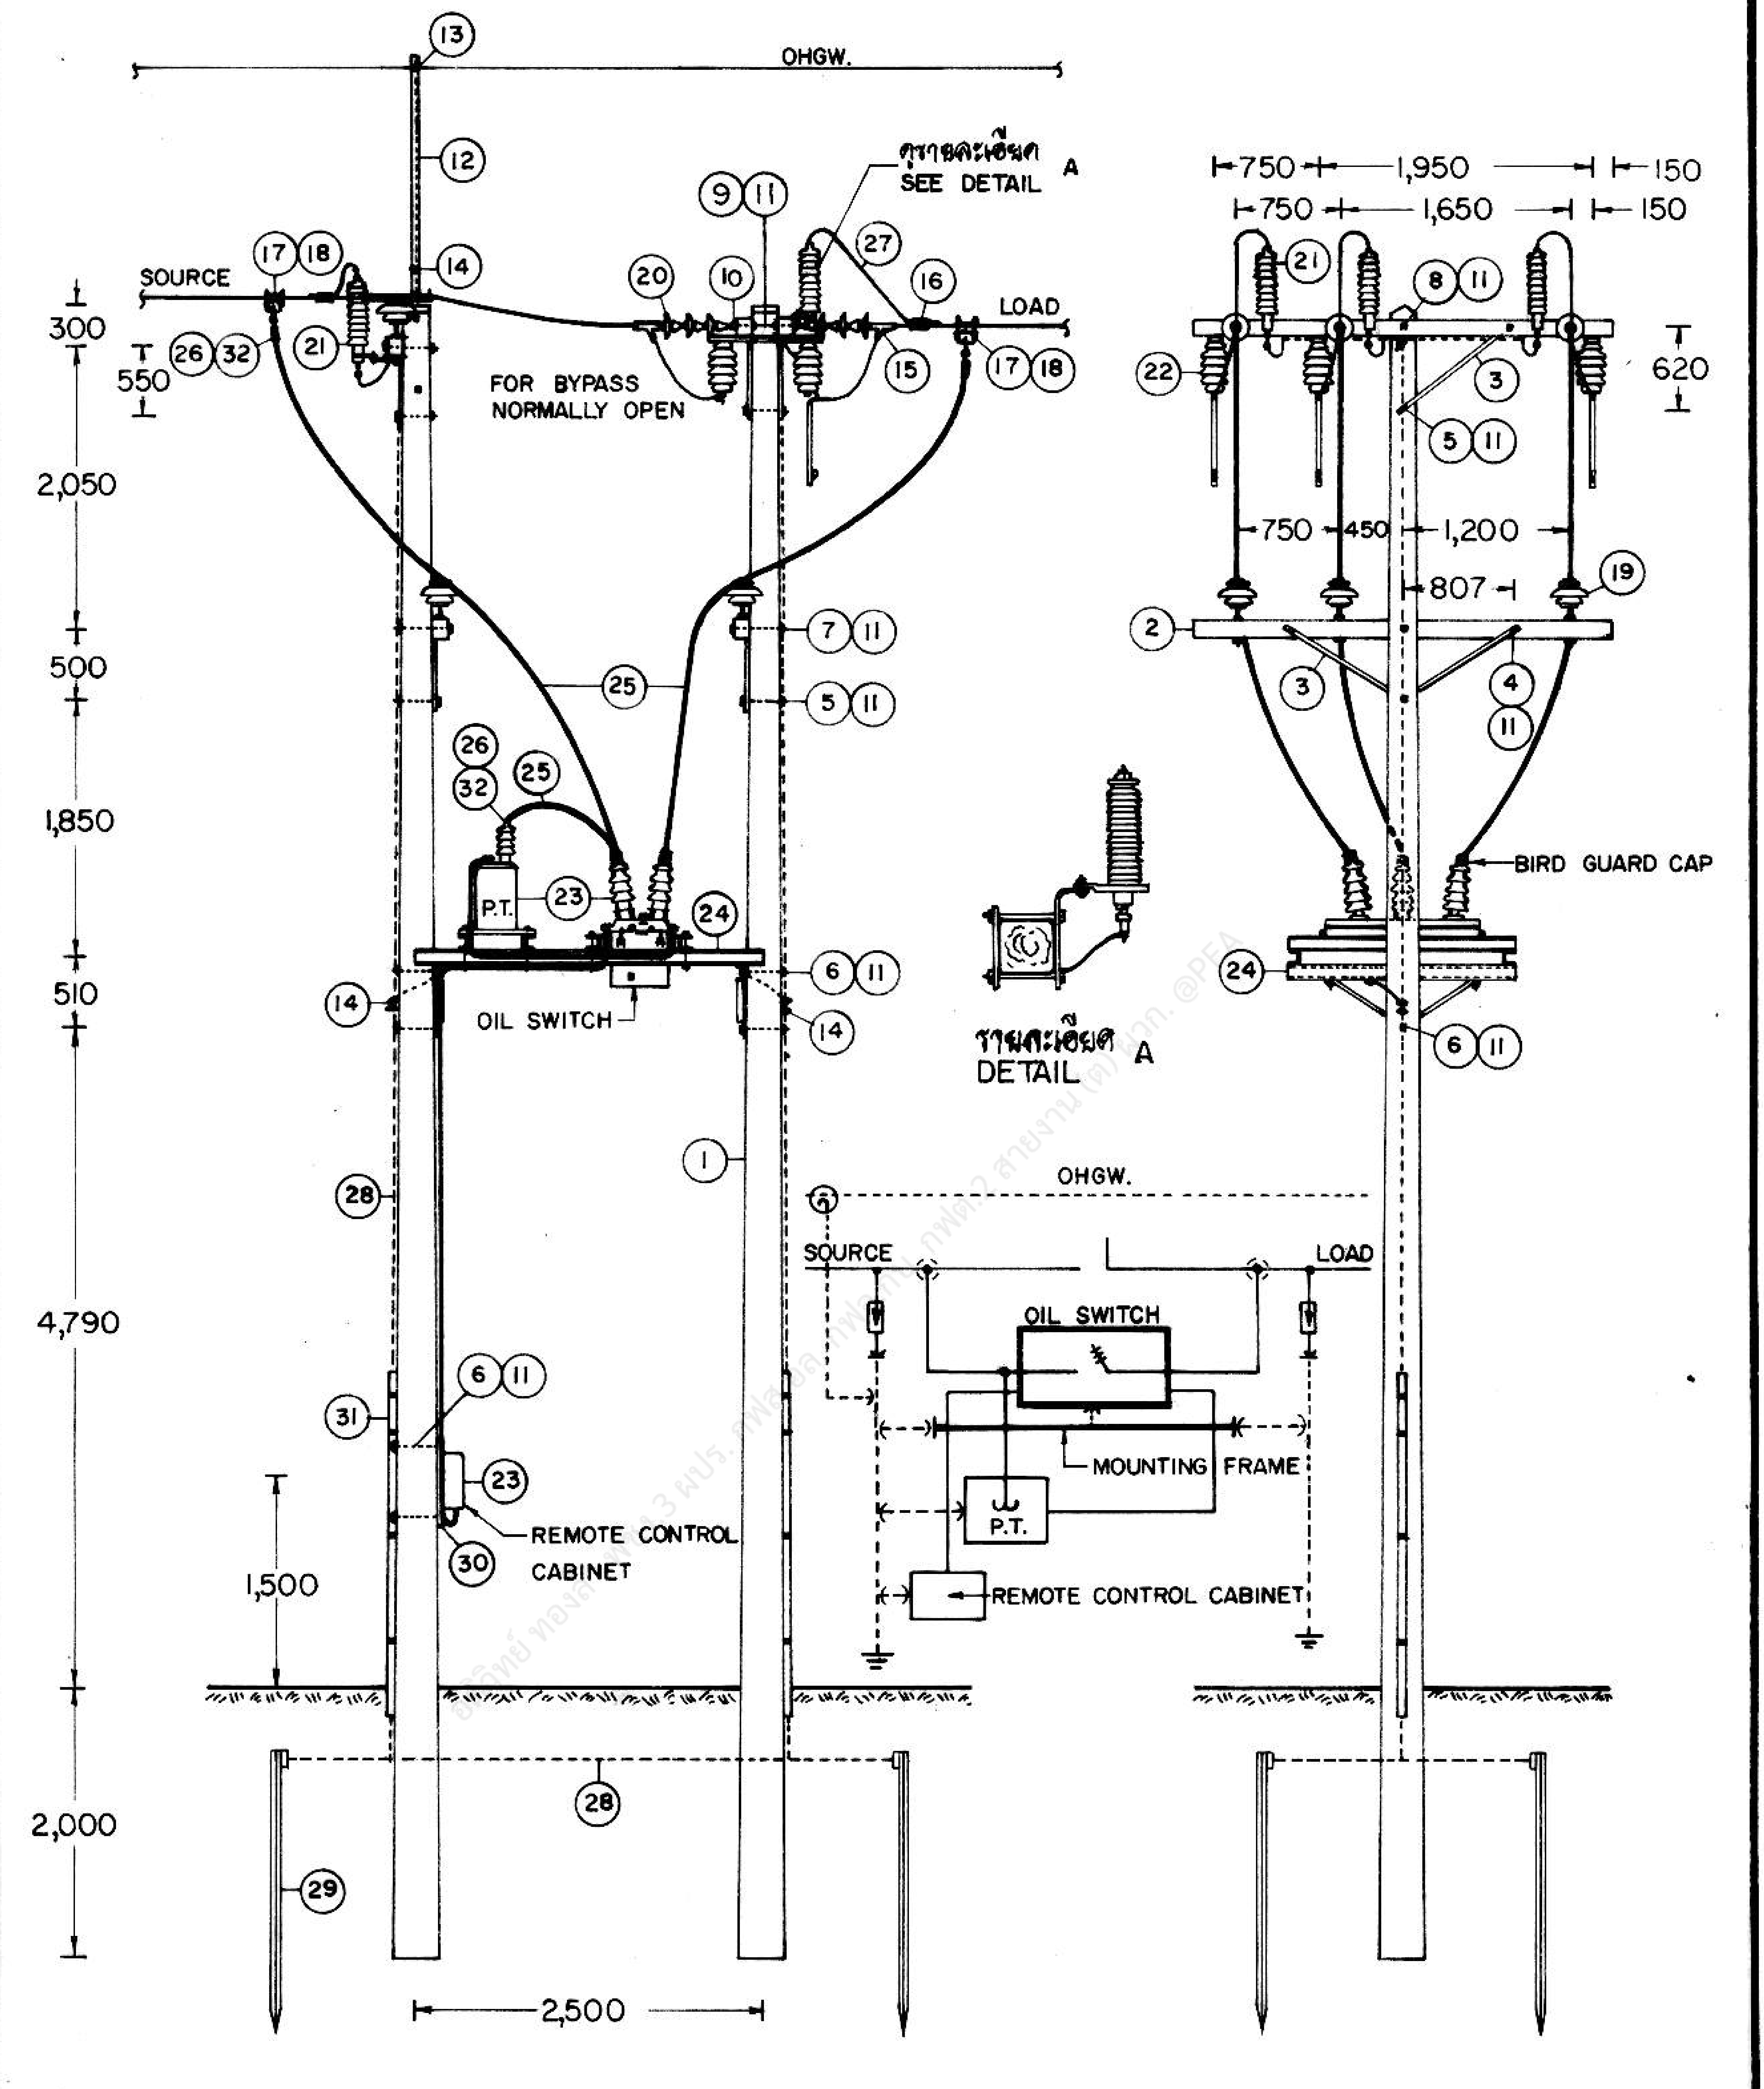

กองวิศวกรรมไฟฟ้าและเครื่องกล ฝ่ายวิศวกรรม	การไฟฟ้าส่วนภูมิภาค	ใช้แทนแบบ ถูกแทนโดยแบบ เขียนเสร็จวันที่ 8 มิ.ย.22 แก้แบบวันที่ มิติเป็น มม. มาตราส่วน 1 : 75
ผู้เขียน ผู้สำรวจ วิศวกร หัวหน้าแผนก หัวหน้ากอง ผู้อำนวยการฝ่าย	ผู้ว่าการ 22 พ.ย.22	
	การติดตั้งออยล์สวิตช์ 33 kV บนเสาคู่ ในสายระบบจำหน่าย	
รองผู้ว่าการฝ่ายเทคนิค	33 kV OIL SWITCH INSTALLATION ON DOUBLE POLE IN DISTRIBUTION LINE	แบบเลขที่ SAI-015/22031 แผ่นที่ 1 ของจำนวน 3 แผ่น

21 พ.ย. 2522

การประกอบเลขที่ ASSEMBLY NO.	3412

บัญชีวัสดุ
BILL OF MATERIAL

ลำดับที่ ITEM	รายละเอียด DESCRIPTION	จำนวน REQ'D	วัสดุเลขที่ MAT. NO.
1	เสาคอนกรีต 12 ม. POLE, CONCRETE 12 m LONG	2	00010004
2	ไม้คอนสายแรงสูง 100 X 120 X 3,000 มม. CROSSARM, WOOD, H.T. 100 X 120 X 3,000 mm	5	00100003
3	เหล็กประกับไม้คอน 40 X 6 X 1,000 มม. BRACE, FLAT, FOR CROSSARM 40 X 6 X 1,000 mm	8	01200002
4	สลักเกลียว M 16 X 130 มม. BOLT, MACHINE, M 16 X 130 mm	8	01110200
5	สลักเกลียว M 16 X 200 มม. BOLT, MACHINE, M 16 X 200 mm	4	01110202
6	สลักเกลียว M 16 X 250 มม. BOLT, MACHINE, M 16 X 250 mm	8	01110203
7	สลักเกลียว M 16 X 300 มม. BOLT, MACHINE, M 16 X 300 mm	3	01110204
8	สลักเกลียว M 16 X 400 มม. BOLT, MACHINE, M 16 X 400 mm	1	01110206
9	สลักเกลียวห่วงกลม M 16 X 400 มม. BOLT, DOUBLE ARMING, ROUND EYE, M 16 X 400 mm	3	01130000
10	นัทรูปห่วง M 16 ดิน 582 NUT, EYE, M 16 DIN 582	3	01180001
11	แหวนสี่เหลี่ยมแบน 52X52X4.5 มม. รู Ø 18 มม. มอก. 258 WASHER, SQUARE, FLAT 52X52X4.5 mm HOLE Ø 18 mm TIS 258	39	01180100
12	เหล็กฉากรับสายล่อฟ้า OVERHEAD GROUND WIRE BAYONET	1	01010006
13	กราวด์ไวร์แคล้มป์ แบบ J 1152 GROUND WIRE CLAMP, J 1152	1	01230205
14	ยูแคล้มป์ สลัก 1 ตัว M 8 (ไวร์ โร้ป คลิ๊พ) CLAMP, SINGLE U-BOLT M 8 (WIRE ROPE CLIP)	14	01230000
15	สเตรนแคล้มป์ สำหรับสายอะลูมิเนียม 120 ต.มม. CLAMP, STRAIN FOR Al 120 mm^2	6	03110002
16	พีจี. คอนเนคเตอร์ สำหรับสายอะลูมิเนียม 70-185 ต.มม. CONNECTOR, PARALLEL GROOVE, FOR Al 70-185 mm^2	8	02300103
17	ฮอทไลน์แคล้มป์ สำหรับสายอะลูมิเนียม 50-120 ต.มม. CLAMP, HOT LINE, FOR Al 50-120 mm^2	6	02330101
18	สเตอร์รัพแคล้มป์ หรือเบลแคล้มป์ฮอทไลน์ สำหรับสายอะลูมิเนียม 70-185 ต.มม. CLAMP, STIRRUP OR BAIL, HOT LINE, FOR Al 70-185 mm^2	6	02330001
19	ลูกถ้วยก้านตรง 33 kV มอก. 279 แบบ ค (แบบ 56-3) พร้อมก้าน INSULATOR, PIN TYPE, 33 kV TIS 279 TYPE C (CLASS 56-3) COMP. WITH PIN	9	03000002 03100001
20	ลูกถ้วยแขวน มอก. 354 แบบ ง (แบบ 52-4) INSULATOR, SUSPENSION TYPE, TIS 354 TYPE D (CLASS 52-4)	18	03020002

กองวิศวกรรมไฟฟ้าและเครื่องกล ฝ่ายวิศวกรรม	**การไฟฟ้าส่วนภูมิภาค**	ใช้แทนแบบ ถูกแทนโดยแบบ เขียนเสร็จวันที่ 8 มิ.ย.22 แก้แบบวันที่ มิติเป็น มาตราส่วน
ผู้เขียน ผู้ตรวจ วิศวกร หัวหน้าแผนก หัวหน้ากอง ผู้อำนวยการฝ่าย	ผู้ว่าการ 23 พ.ย.22 การติดตั้งออยล์สวิตช์ 33 kV บนเสาคู่ ในสายระบบจำหน่าย	
รองผู้ว่าการฝ่ายเทคนิค 21 พ.ย. 2522	33 kV OIL SWITCH INSTALLATION ON DOUBLE POLE IN DISTRIBUTION LINE	แบบเลขที่ SAI-015/22031 แผ่นที่ 2 ของจำนวน 3 แผ่น

การประกอบเลขที่
ASSEMBLY NO. 3412

บัญชีวัสดุ
BILL OF MATERIAL

ลำดับที่ ITEM	รายละเอียด DESCRIPTION	จำนวน REQ'D	วัสดุเลขที่ MAT. NO.
21	ล่อฟ้า 30 kV, 5 กิโลแอมป์ LIGHTNING ARRESTER, 30 kV, 5 kA	6	04000100
22	สวิตช์ธรรมดาหนึ่งขา 33 kV, 600 แอมป์ SWITCH, DISCONNECTING, SINGLE POLE, 33 kV, 600 A	3	04050100
23	ออยล์สวิตช์ 33 kV ขนาด 300 แอมป์ พร้อมพี.ที. 33,000/230 โวลต์ 750 vA , คอนโทรลเคเบิล และตู้อุปกรณ์ควบคุม 33 kV LOAD BREAK OIL SWITCH 300 A COMPLETE WITH P.T. 33,000/230 V, 750 vA, CONTROL CABLE, AND REMOTE CONTROL CABINET	1 ชุด set	
24	ที่แขวนออยล์สวิตช์และ พี.ที. กับเสาคู่ แบบเลขที่ SAI-015/22032 DOUBLE-POLE MOUNTING FRAME FOR LOAD BREAK OIL SWITCH AND P.T. ACCORDING TO DWG. NO. SAI-015/22032	1	
25	เคเบิลอากาศอะลุมิเนียม 22 kV ขนาด 1X120 ต.มม. หรือ 33 kV ขนาดตามต้องการ CABLE, AERIAL, Al 22 kV, 1X120 mm² OR 33 kV SIZE AS REQUIRED	32 ม. m	02050002
26	เทปพันเคเบิลอากาศแรงสูง ELECTRICAL SPLICING TAPE, FOR H.T. AERIAL CABLE	3 ม้วน rolls	02180003
27	สายอะลุมิเนียมเปลือย ขนาด 95 ต.มม. มอก. 85 CONDUCTOR, Al 95 mm² TIS 85	6 ม. m	02010004
28	ลวดเหล็กตีเกลียว 50/7 ต.มม. มอก. 404 WIRE, STEEL STRANDED, 50/7 mm² TIS 404	48 ม. m	01100004
29	**หลักดิน** 60 X 60 X 5 มม. ยาว 2 ม. ROD, GROUND 60 X 60 X 5 mm, 2 m LONG	2	01220002
30	ไม้รองรับตู้อุปกรณ์ควบคุม ขนาด 600 X 200 X 20 มม. WOOD, PLATE SIZE 600 X 200 X 20 mm	1	—
31	ท่อ PVC แข็ง ขนาด 20X2,500 มม. พร้อมอุปกรณ์ติดตั้ง แบบเลขที่ S02-015/19128 PIPE, RIGID PVC 20X2,500 mm COMP. WITH FIXER DWG. NO. S02-015/19128	2	08040001
32	เทปไฟฟ้า PVC หรือเทปไฟฟ้ายาง ซิลิโคน PVC PLASTIC OR SILICONE RUBBER ELECTRICAL TAPE	10 ม. m	02180002 or 02180004

อติวิทย์ ทองลา พชง.3
กฟต.2 สายงาน (ต) ผวภ. @PEA

กองวิศวกรรมไฟฟ้าและเครื่องกล
ฝ่ายวิศวกรรม

ผู้เขียน
ผู้สำรวจ
วิศวกร
หัวหน้าแผนก ชัยรัตน์
หัวหน้ากอง
ผู้อำนวยการฝ่าย

รองผู้ว่าการฝ่ายเทคนิค

21 พ.ย. 2522

การไฟฟ้าส่วนภูมิภาค

ผู้ว่าการ 23 พ.ย.22.

การติดตั้งออยล์สวิตช์ 33 kV บนเสาคู่
ในสายระบบจำหน่าย

33 kV OIL SWITCH INSTALLATION ON DOUBLE POLE
IN DISTRIBUTION LINE

ใช้แทนแบบ
ถูกแทนโดยแบบ
เขียนเสร็จวันที่ 8 มิ.ย.22
แก้แบบวันที่
มิติเป็น
มาตราส่วน

แบบเลขที่ SAI-015/22031
แผ่นที่ 3 ของจำนวน 3 แผ่น

*