


การประกอบเลขที่ ASSEMBLY NO. 0705

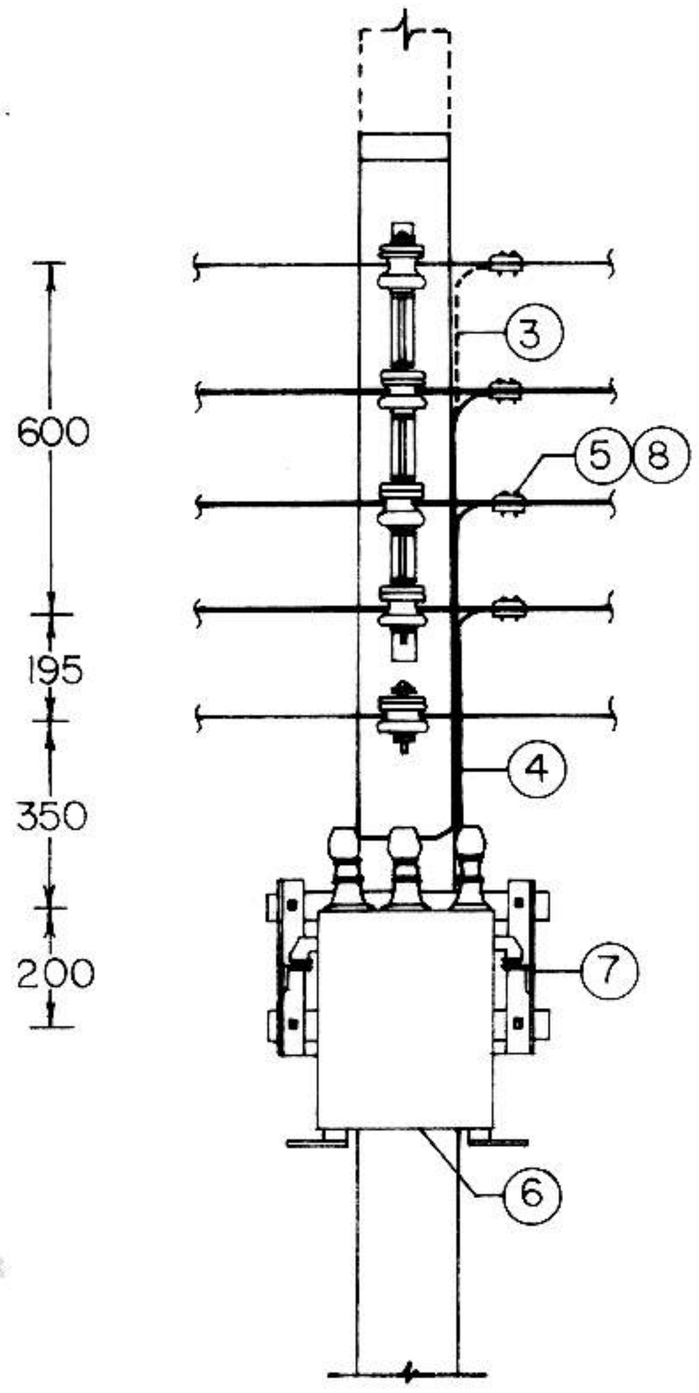

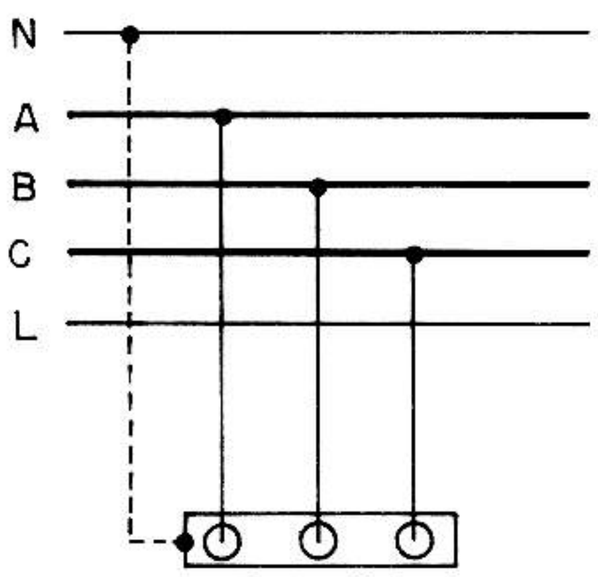

แผนผังแสดงการต่อ
CONNECTION DIAGRAM

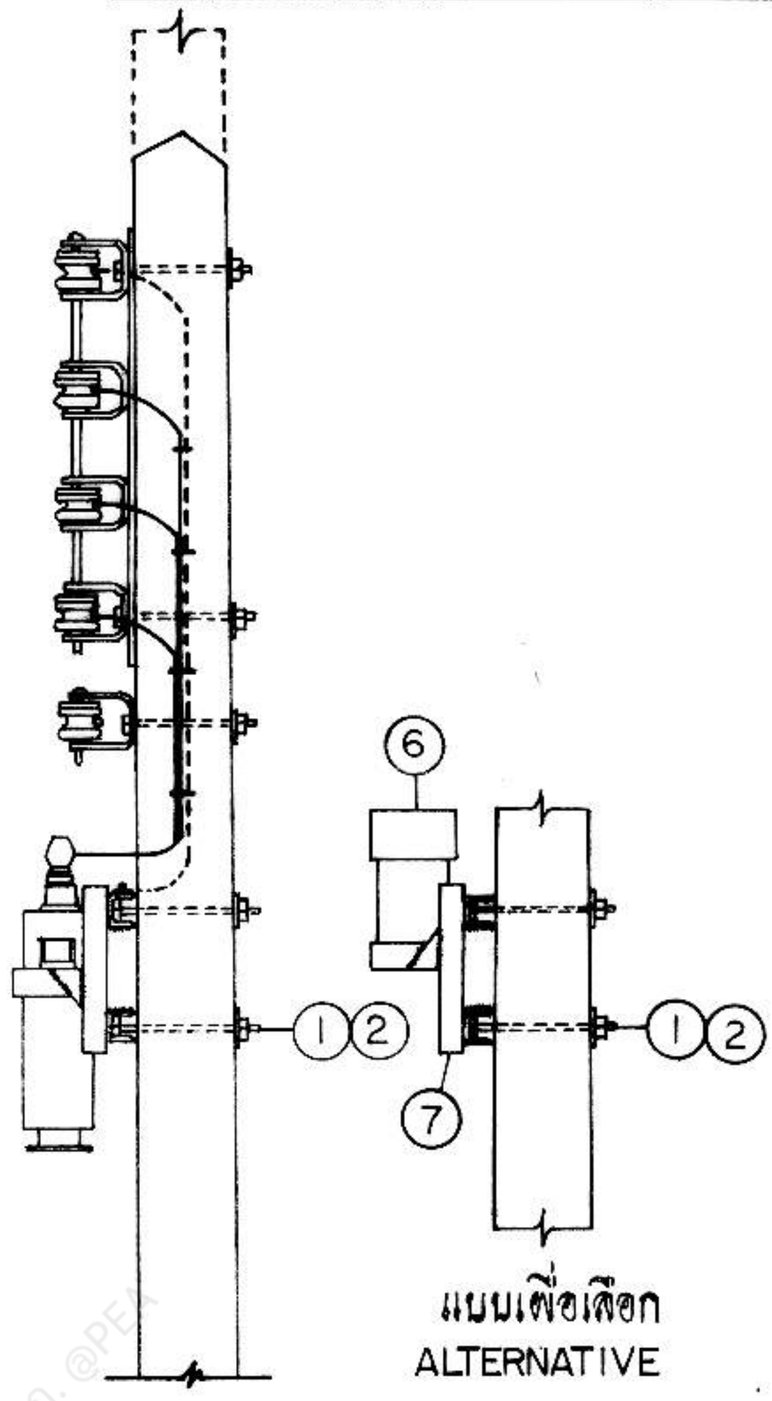

แบบเผื่อเลือก
ALTERNATIVE

บัญชีวัสดุ
BILL OF MATERIAL

ลำดับที่ ITEM	รายละเอียด DESCRIPTION	จำนวน REQ'D	วัสดุเลขที่ MAT. NO.
1	สลักเกลียว M 16 X 200 มม. BOLT, MACHINE, M 16 X 200 mm	2	01110202
2	แหวนสี่เหลี่ยมแบน 52X52X4.5 มม. รู Ø 18 มม. มอก. 258 WASHER, SQUARE, FLAT 52 X 52 X 4.5 mm HOLE Ø 18 mm TIS 258	4	01180100
3	ลวดเหล็กตีเกลียว 50/7 ต.มม. มอก. 404 WIRE, STEEL STRANDED 50/7mm² TIS 404	1.5 ม. m	01100004
4	สายอะลูมิเนียมหุ้มฉนวนใช้ภายนอก 0.6/1 kV 25-35 ต.มม. CONDUCTOR, INSULATED, WEATHER-PROOF, Al 0.6/1 kV, 25-35 mm²	3 ม. m	02070000-1
5	พีจี. คอนเนคเตอร์ สลักคู่ สำหรับสายอะลูมิเนียม 16-70 ต.มม. CONNECTOR, PARALLEL GROOVE, DOUBLE BOLT, Al 16-70 mm²	4	02300101
6	คะแปซิเตอร์สามเฟส ใช้นอกอาคาร 400 โวลต์ 20-45 กิโลวาร์ CAPACITOR, POWER, 3-PHASE, OUTDOOR 400 V, 20-45 kVar	1	05040202-4
7	ที่แขวนคะแปซิเตอร์แรงต่ำ แบบเลขที่ SAI-015/21003 (การประกอบเลขที่ 0708) L.T. CAPACITOR HANGER DWG. NO. SAI-015/21003 (ASSEMBLY NO. 0708)	1	
8	PVC เทป กว้าง 19 มม. (ใช้ความยาว 2 ม. ต่อจุด) มอก. 386 PVC TAPE 19 mm WIDE (2 m LONG PER POINT) TIS 386		02180001 or 02180002
1a	สลักเกลียว M 16 X 300 มม. สำหรับเสาคอนกรีต 12 ม. BOLT, MACHINE, M 16 X 300 mm FOR 12 m CONCRETE POLE	2	01110204

กองวิศวกรรมไฟฟ้าและเครื่องกล ฝ่ายวิศวกรรม	การไฟฟ้าส่วนภูมิภาค	ใช้แทนแบบ ถูกแทนโดยแบบ เขียนเสร็จวันที่ 5 ม.ค. 21 แก้แบบวันที่ มิติเป็น มม. มาตราส่วน 1 : 25
ผู้เขียน ผู้สำรวจ วิศวกร หัวหน้าแผนก หัวหน้ากอง ผู้อำนวยการฝ่าย	ผู้ว่าการ 16 ม.ค. 21 การติดตั้งคะแปซิเตอร์ 3 เฟส 400 โวลต์ สำหรับสายระบบจำหน่ายแรงต่ำ	
รองผู้ว่าการฝ่ายเทคนิค	3-Ø 400 V CAPACITOR INSTALLATION FOR L.T. DISTRIBUTION LINE	แบบเลขที่ SAI-015/21002 แผ่นที่ 1 ของจำนวน 1 แผ่น