

การประกอบเลขที่ ASSEMBLY NO. **0524 A**

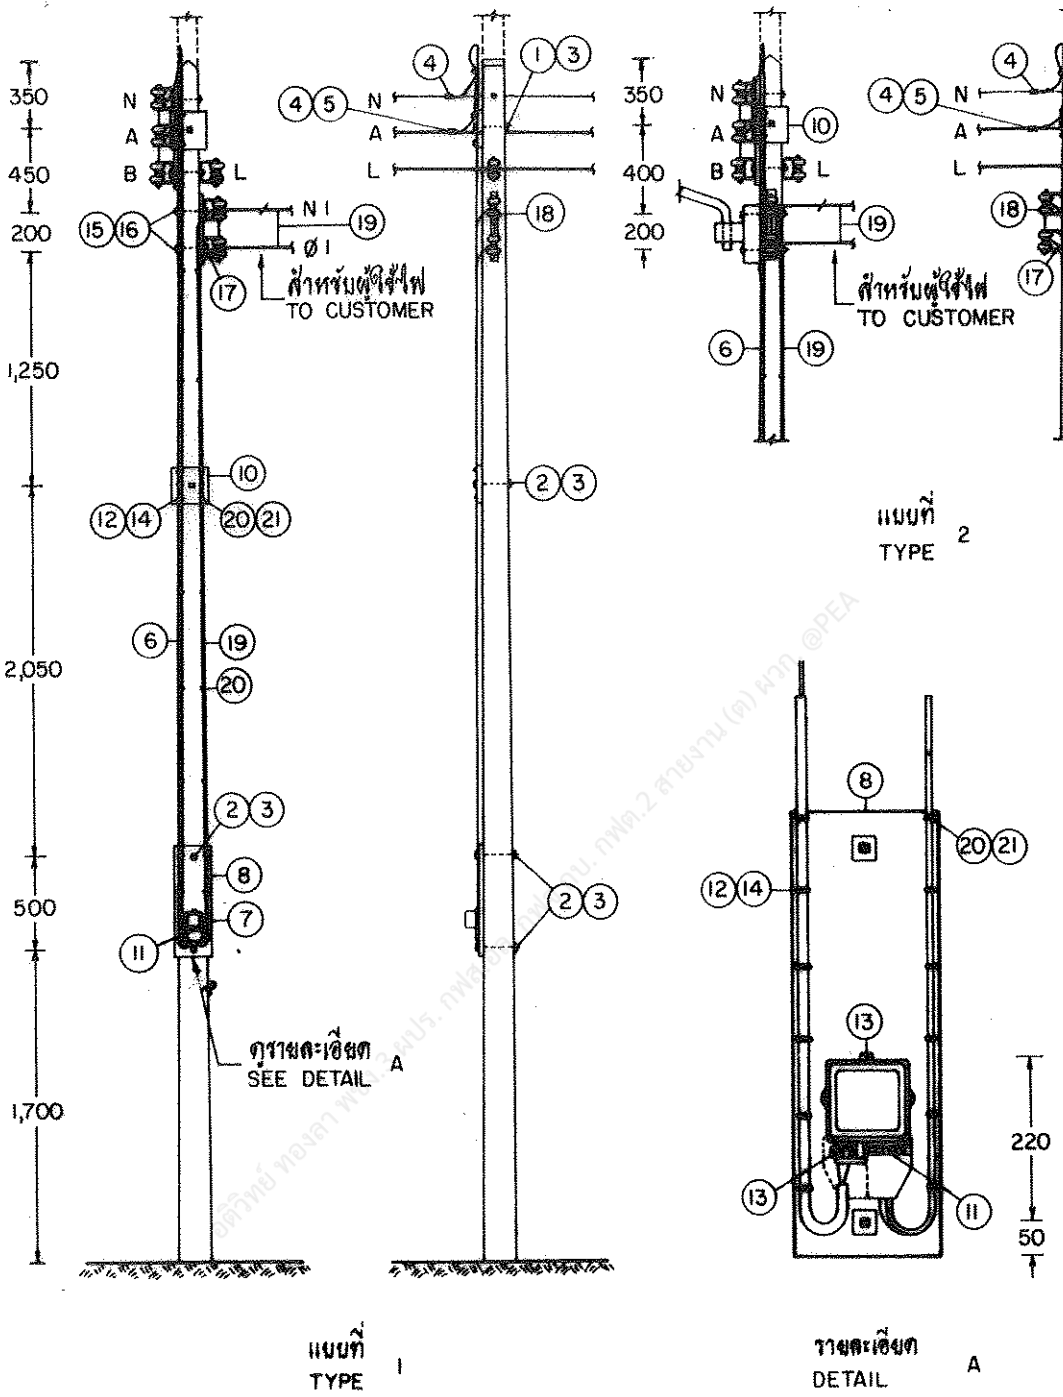



COPY

| | | |
|---|---|---|
| กองวิศวกรรมไฟฟ้าและเครื่องกล<br>ฝ่ายวิศวกรรม | การไฟฟ้าส่วนภูมิภาค | ใช้แทนแบบ<br>ถูกแทนที่โดยแบบ |
| ผู้เขียน<br>ผู้สำรวจ<br>วิศวกร<br>หัวหน้าแผนก<br>ผู้อำนวยการกอง<br>ผู้อำนวยการฝ่าย | ผู้ว่าการ 10 มิถุนายน 2538<br>การติดตั้งมิเตอร์ 1 เฟส 220 โวลต์ ขนาด 3-15 แอมป์<br>บนเสาคอนกรีต 8 ม. ( สายเข้ามิเตอร์ทองแดง )<br>1 จำนวน 1 เครื่อง | เขียนเสร็จวันที่ 19 ธ.ค.37<br>แก้แบบวันที่ 12 พ.ค. 41<br>มิติเป็น มิลลิเมตร<br>มาตราส่วน 1 : 40 |
| รองผู้ว่าการฝ่ายเทคนิค<br>นายไพศาล | 3-15 A, 1-Ø, 220V METER INSTALLATION<br>ON 8 m CONCRETE POLE ( Cu SERVICE ENTRANCE CABLE )<br>1 1 UNIT | แบบเลขที่ SA4-015/37030<br>แผ่นที่ 1 ของจำนวน 6 แผ่น |


การประกอบเลขที่ ASSEMBLY NO. 0524 A

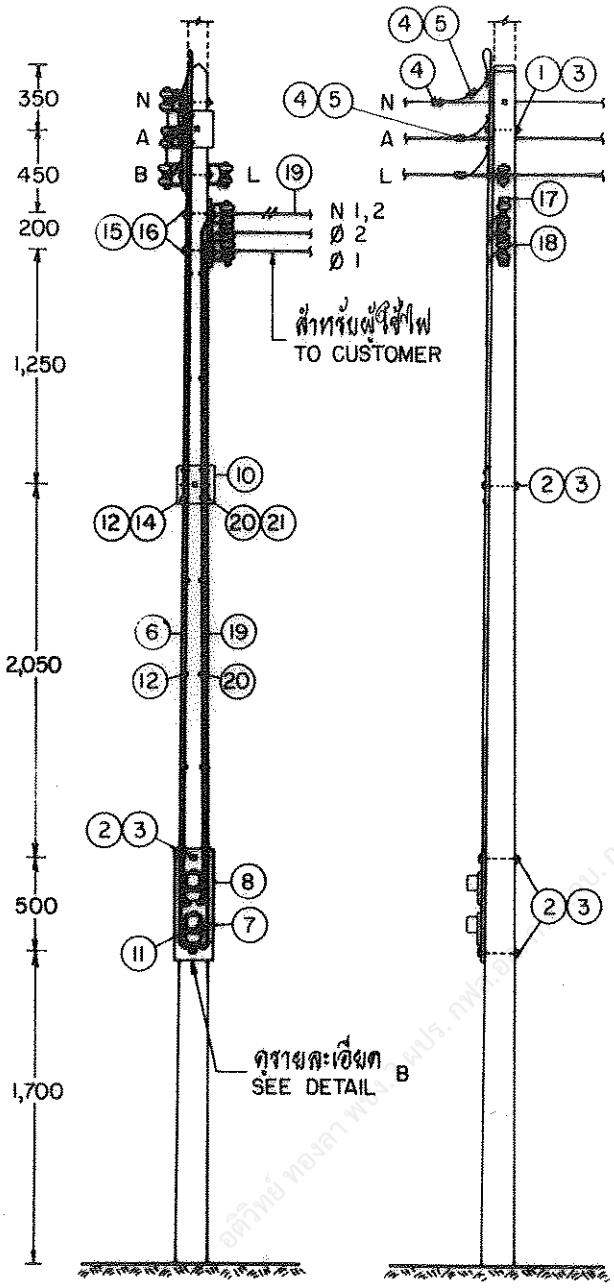


แบบที่ 1
TYPE 1

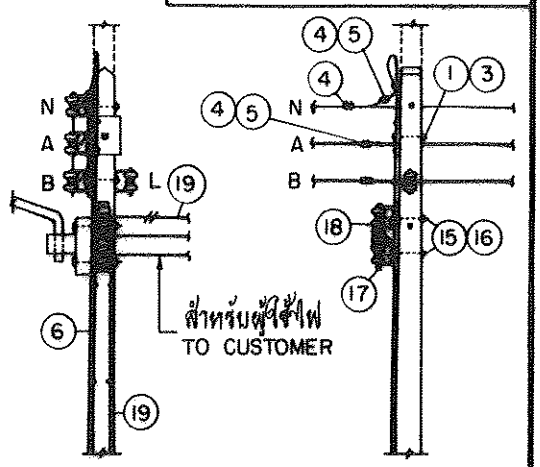


แบบที่ 2
TYPE 2

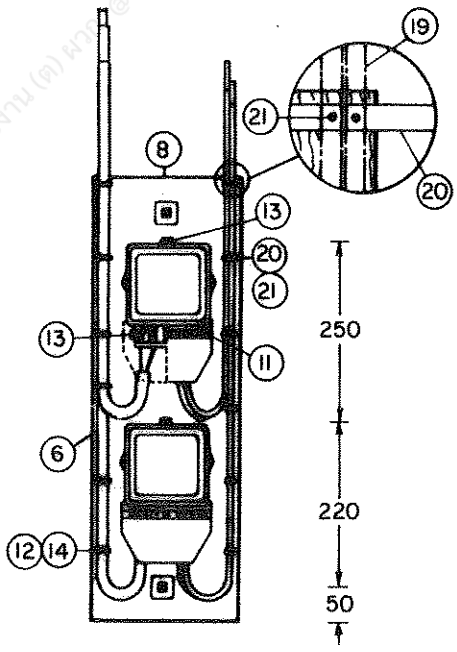



รายละเอียด B
DETAIL B

COPY


| | | |
|---|---|---|
| กองวิศวกรรมไฟฟ้าและเครื่องกล<br>ฝ่ายวิศวกรรม | การไฟฟ้าส่วนภูมิภาค | ใช้แทนแบบ<br>ถูกแทนโดยแบบ |
| ผู้เขียน<br>ผู้สำรวจ<br>วิศวกร<br>หัวหน้าแผนก<br>ผู้อำนวยการกอง<br>ผู้อำนวยการฝ่าย | ตู้ว่าการ 18 มิถุนายน 2538<br>การติดตั้งมิเตอร์ 1 เฟส 220 โวลต์ ขนาด 3-15 แอมป์ บนเสาคอนกรีต 8 ม. ( สายเข้ามิเตอร์ทองแดง )<br>2. จำนวน 2 เครื่อง | เขียนเสร็จวันที่ 19 ก.ค. 37<br>แก้แบบวันที่ 12 พ.ค. 41<br>มิติเป็น มิลลิเมตร<br>มาตราส่วน 1 : 40 |
| ของตู้ว่าการฝ่ายบูรณะ | 3-15 A, 1-Ø, 220 V METER INSTALLATION ON 8 m CONCRETE POLE ( Cu SERVICE ENTRANCE CABLE )<br>2. 2 UNITS | แบบมาตรฐานที่ SA4-015/37030<br>แต่งที่ 2 รวมจำนวน 6 แผ่น |

การประกอบเลขที่ ASSEMBLY NO. 0524 A

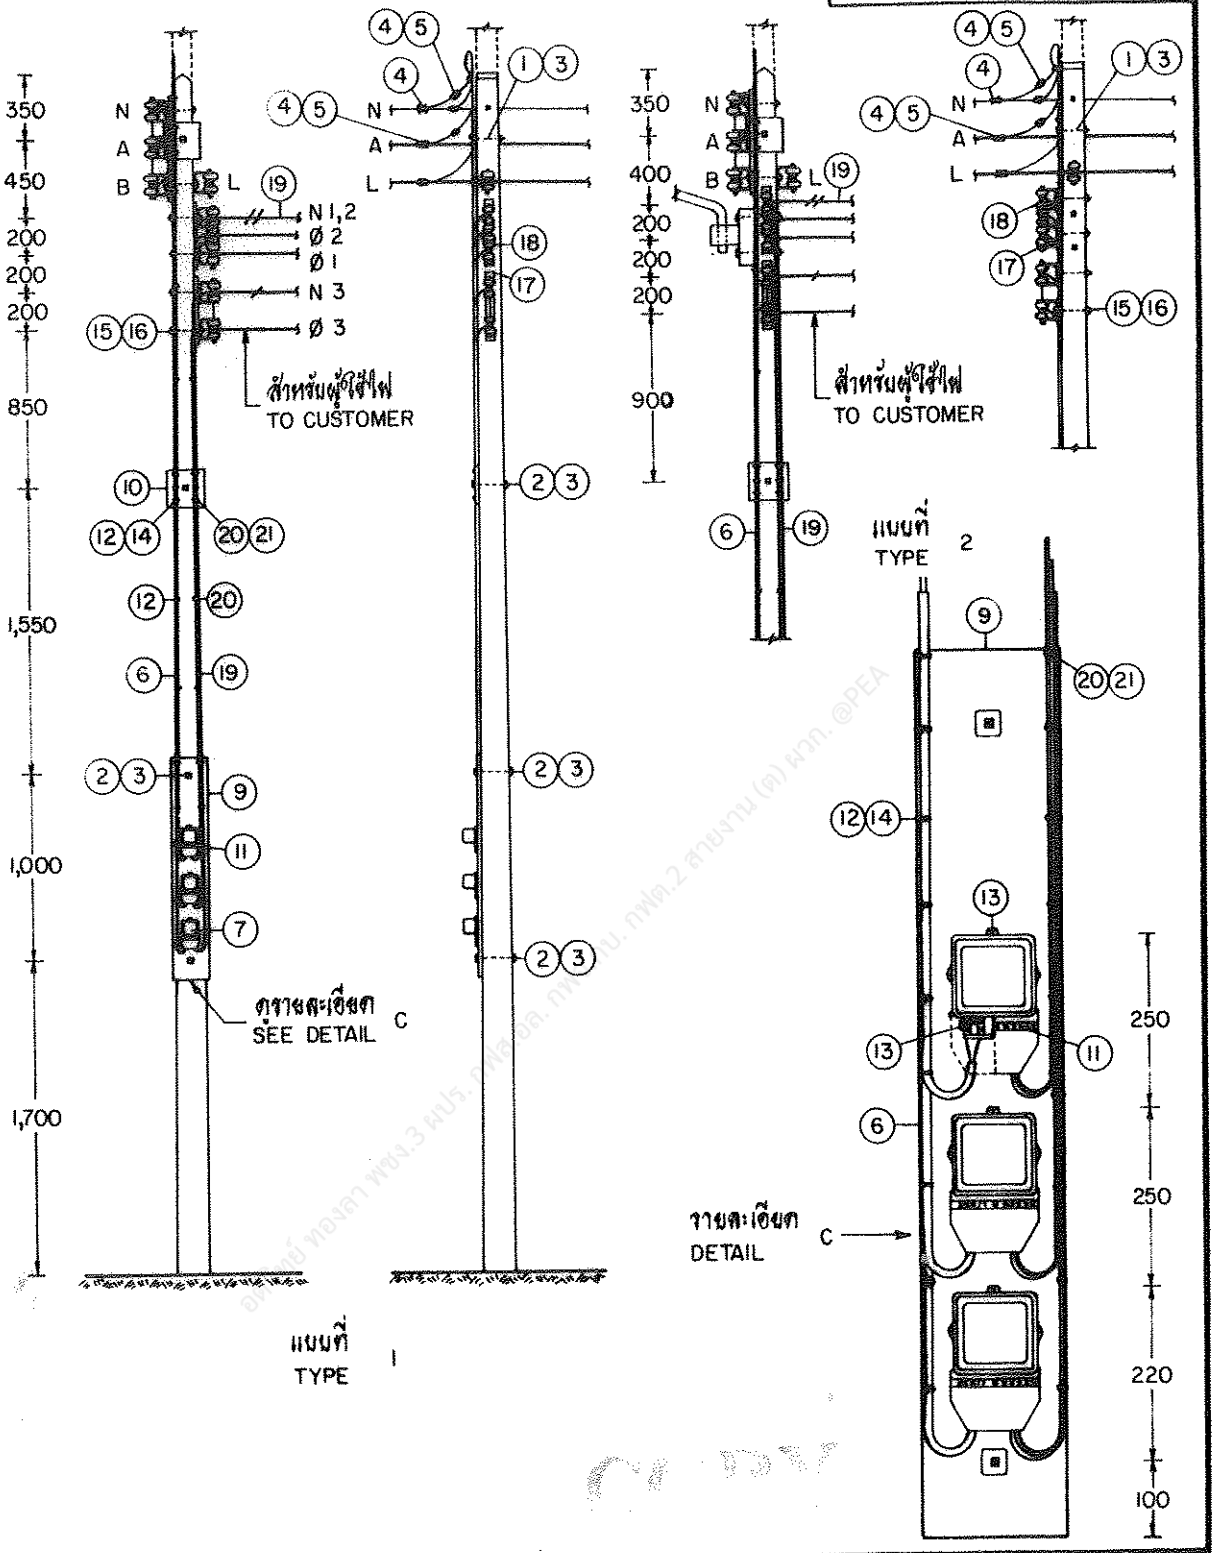


| | | |
|---|---|---|
| กองวิศวกรรมไฟฟ้าและเครื่องกล<br>ฝ่ายวิศวกรรม | การไฟฟ้าส่วนภูมิภาค | ใช้แทนแบบ<br>ถูกแทนโดยแบบ |
| ผู้เขียน<br>ผู้สำรวจ<br>วิศวกร<br>หัวหน้าแผนก<br>ผู้อำนวยการกอง<br>ผู้อำนวยการฝ่าย | ผู้ว่าการ 16 มิ.ย. 2538<br>การติดตั้งมิเตอร์ 1 เฟส 220 โวลต์ ขนาด 3-15 แอมป์<br>บนเสาคอนกรีต 8 ม. ( สายเข้ามิเตอร์ทองแดง )<br>3. จำนวน 3 เครื่อง | เขียนเสร็จวันที่ 19 มิ.ย. 37<br>แก้แบบวันที่ 12 ม.ค. 41<br>มิติเป็น มิลลิเมตร<br>มาตราส่วน 1 : 40 |
| รองผู้ว่าการฝ่ายเทคนิค | 3-15 A, 1-Ø, 220V METER INSTALLATION<br>ON 8 m CONCRETE POLE ( Cu SERVICE ENTRANCE CABLE )<br>3. 3 UNITS | แบบเลขที่ SA4-015/37030<br>แผ่นที่ 3 รวมจำนวน 6 แผ่น |

การประกอบเลขที่ ASSEMBLY NO. 0524 A

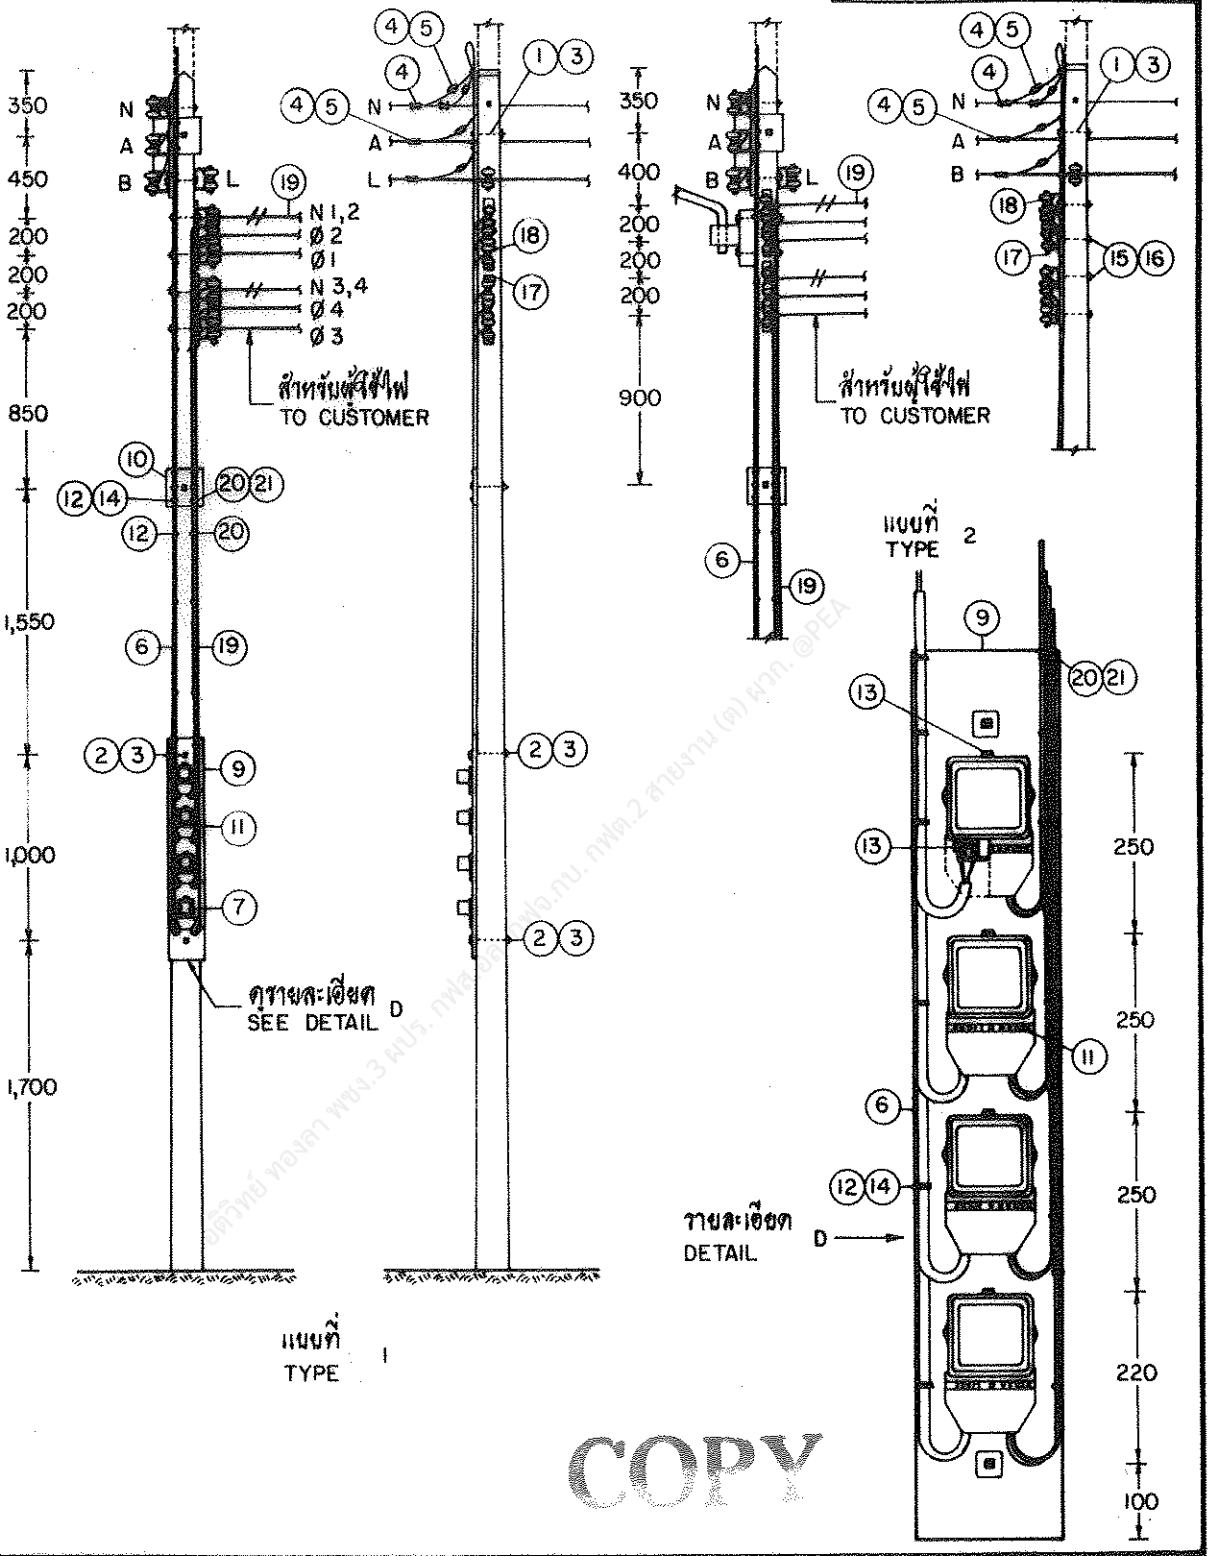


COPY

| | | |
|---|---|---|
| กองวิศวกรรมไฟฟ้าและเครื่องกล<br>ฝ่ายวิศวกรรม | การไฟฟ้าส่วนภูมิภาค | ใช้แทนแบบ<br>ถูกแทนโดยแบบ |
| ผู้เขียน<br>ตรวจสอบ<br>วิศวกร<br>หัวหน้าแผนก<br>ผู้อำนวยการกอง<br>ผู้อำนวยการฝ่าย | ผู้ว่าการ 16 มิ.ย. 2538<br>การติดตั้งมิเตอร์ 1 เฟส 220 โวลต์ ขนาด 3-15 แอมป์ บนเสาคอนกรีต 8 ม. ( สายเข้ามิเตอร์ทองแดง )<br>4. จำนวน 4 เครื่อง | เขียนเสร็จวันที่ 19 ธ.ค. 37<br>แก้แบบวันที่ 12 พ.ค. 41<br>มิติเป็น มิลลิเมตร<br>มาตราส่วน 1 : 40 |
| รองผู้ว่าการฝ่ายเทคนิค | 3-15 A, 1-ø, 220V METER INSTALLATION ON 8 m CONCRETE POLE ( Cu SERVICE ENTRANCE CABLE )<br>4. 4 UNITS | แบบเลขที่ SA4-015/37030<br>แผ่นที่ 4 จากจำนวน 6 แผ่น |

การประกอบเลขที่ ASSEMBLY NO. **0524 A**

บัญชีวัสดุในส่วนที่ กฟภ. ลงทุน
BILL OF MATERIAL FOR PEA

| ลำดับที่ ITEM | รายละเอียด DESCRIPTION | จำนวน REQ'D 1 | 2 | 3 | 4 | วัสดุเลขที่ MAT. NO. |
|---|---|---|---|---|---|---|
| 1 | สลักเกลียว M 16 X 200 มม.<br>BOLT, MACHINE, M 16 X 200 mm | 1 | 1 | 1 | 1 | 01110202 |
| | สลักเกลียว M 16 X 250 มม. สำหรับเสาคอนกรีต 12 ม.<br>BOLT, MACHINE, M 16 X 250 mm, FOR 12 m CONCRETE POLE | 1 | 1 | 1 | 1 | 01110203 |
| 2 | สลักเกลียว M 16 X 250 มม.<br>BOLT, MACHINE, M 16 X 250 mm | 3 | 3 | 3 | 3 | 01110203 |
| | สลักเกลียว M 16 X 300 มม. สำหรับเสาคอนกรีต 12 ม.<br>BOLT, MACHINE, M 16 X 300 mm, FOR 12 m CONCRETE POLE | 3 | 3 | 3 | 3 | 01110204 |
| 3 | แหวนสี่เหลี่ยมแบน 52X52X4.5 มม. รู Ø 18 มม. มอก. 258<br>WASHER, SQUARE, FLAT, 52X52X4.5 mm, HOLE Ø 18 mm TIS 258 | 8 | 8 | 8 | 8 | 01180100 |
| 4 | คอนเนคเตอร์ชนิดบีบ แบบ H ขนาดตามต้องการ<br>CONNECTOR, COMPRESSION, H TYPE, SIZE AS REQUIRED | 2 | 4 | 6 | 8 | 02320002-6 |
| 5 | PVC เทป กว้าง 19 มม. (ใช้ความยาว 2 ม. ต่อ 1 จุด (มอก. 386)<br>PVC TAPE, 19 mm WIDE (2 m LONG PER POINT) TIS 386 | ม. m | ม. m | ม. m | ม. m | 02180001 or 02180002 |
| 6* | สายทองแดงหุ้มฉนวนเข้ามิเตอร์แรงต่ำ 600 V, 2X6 ต.มม. หุ้มรวม 2X10 ต.มม.<br>CABLE, FOR SERVICE ENTRANCE, Cu, 600 V, 2X6 $mm^2$, OR 2X10 $mm^2$ | 5.5 ม. m | 11 ม. m | 16 ม. m | 21 ม. m | 02080500 or 02080501 |
| 7 | วัตต์อาวร์มิเตอร์ 1 เฟส 2 สาย 220 โวลต์ ใช้กลางแจ้ง<br>METER, WATTHOUR, SINGLE-PHASE, 2-WIRE 220 V, WEATHER PROOF | 1 | 2 | 3 | 4 | 06000000-1 or 06000000-9 |
| 8 | แป้นไม้รองมิเตอร์ไสเกลี้ยง ขนาด 60X20X2 ซม.<br>METER PLATE, HARD WOOD, SURFACE FINISHED, 60X20X2 cm | 1 | 1 | — | — | —— |
| 9 | แป้นไม้รองมิเตอร์ไสเกลี้ยง ขนาด 120X20X2 ซม.<br>METER PLATE, HARD WOOD, SURFACE FINISHED, 120X20X2 cm | — | — | 1 | 1 | —— |
| 10 | แป้นไม้สำหรับยึดสายเข้า และออกจากมิเตอร์ ไสเกลี้ยง ขนาด 20X20X2 ซม.<br>CABLE PLATE, HARD WOOD, SURFACE FINISHED, 20X20X2 cm | 2 | 2 | 2 | 2 | —— |
| 11 | หมายเลขผู้ใช้ไฟ (ดูตัวอย่างข้างล่าง)<br>NUMBER OF CUSTOMER | 1 | 2 | 3 | 4 | —— |
| 12 | เข็มขัดรัดสาย (ทำด้วยสลักอะลูมิเนียมแผน 1X10 มม.) ช่วงระยะ 50 ซม.<br>CABLE STRAP (MADE OF ARMOUR TAPE 1X10 mm) AT 50 cm INTERVALS | 2 ม. m | 3 ม. m | 5 ม. m | 5 ม. m | 02200000 |
| 13 | ตะปูเกลียวชุบโครเมี่ยม ขนาด 15-20 มม.<br>SCREW, CHROME PLATED, SIZE 15-20 mm | 3 | 6 | 9 | 12 | |
| 14 | ตะปูหัวกลมแบน ยาว 15-20 มม. Ø1 มม. มอก. 113<br>NAIL, ROUND, MILD STEEL WIRE 15-20 mm LONG Ø1 mm TIS 113 | 24 | 24 | 40 | 40 | |

* — สายทองแดง ขนาด 2X6 ต.มม. สำหรับมิเตอร์ ขนาด 3-5 แอมป์
สายทองแดง ขนาด 2X10 ต.มม. สำหรับมิเตอร์ ขนาด 15 แอมป์

COPY

แผ่นอะลูมิเนียม ขนาด 15 X 100 มม. หนา 0.5 มม.

รู Ø 3.5 มม.

322/1 25271

ใช้ที่ตอกตัวเลข ขนาดความสูง 10 มม. ตอก แล้วทาด้วยสีดำ ตามรอยตัวอักษร

**ตัวอย่างหมายเลขผู้ใช้ไฟ**

| | | |
|---|---|---|
| กองวิศวกรรมไฟฟ้าและเครื่องกล<br>ฝ่ายวิศวกรรม | **การไฟฟ้าส่วนภูมิภาค** | ใช้แทนแบบ<br>ถูกแทนโดยแบบ |
| ผู้เขียน<br>ผู้ตรวจ<br>วิศวกร<br>หัวหน้าแผนก<br>ผู้อำนวยการกอง<br>ผู้อำนวยการฝ่าย | ผู้ว่าการ 10 มิ.ย. 2538 | เขียนเสร็จวันที่ 19 มี.ค. 37<br>แก้แบบวันที่ 12 พ.ค. 41<br>มิติเป็น<br>หมายเหตุ |
| ของผู้ว่าการฝ่ายเทคนิค | การติดตั้งมิเตอร์ 1 เฟส 220 โวลต์ ขนาด 3-15 แอมป์ บนเสาคอนกรีต 8 ม. (สายเข้ามิเตอร์ทองแดง)<br>3-15 A, 1-Ø, 220 V METER INSTALLATION ON 8 m CONCRETE POLE (Cu SERVICE ENTRANCE CABLE) | แบบเลขที่ SA4-015/37030<br>แผ่นที่ 5 รวมจำนวน 6 แผ่น |

การประกอบเลขที่ ASSEMBLY NO. **0524 A**

บัญชีวัสดุในส่วนของผู้ใช้ไฟ
BILL OF MATERIAL FOR CUSTOMER

| ลำดับที่ ITEM | รายละเอียด DESCRIPTION | จำนวน REQ'D 1 | 2 | 3 | 4 | วัสดุเลขที่ MAT. NO. |
|---|---|---|---|---|---|---|
| 15 | สลักเกลียว M 16 X 200 มม.<br>BOLT, MACHINE, M 16 X 200 mm | 2 | 2 | 4 | 4 | 01110202 |
| | สลักเกลียว M 16 X 250 มม. สำหรับเสาคอนกรีต 12 ม.<br>BOLT, MACHINE, M 16 X 250 mm, FOR 12 m CONCRETE POLE | 2 | 2 | 4 | 4 | 01110203 |
| 16 | แหวนสี่เหลี่ยมแบน 52X52X4.5 มม. รู Ø 18 มม. มอก. 258<br>WASHER, SQUARE, FLAT, 52X52X4.5 mm, HOLE Ø 18 mm TIS 258 | 2 | 2 | 4 | 4 | 01180100 |
| 17 | แร็ค 2 X 200 มม. แบบหลังอีน<br>RACK, SECONDARY, MEDIUM PRESSED STEEL, 2X200 mm, EXTENDED RACK | 1 | 1 | 2 | 2 | 03130002 |
| 18 | ลูกรอกแรงต่ำ มอก. 227 แบบ ข (แบบ 53-2)<br>INSULATOR, SPOOL TYPE, L.T. TIS 227 TYPE B (CLASS 53-2) | 2 | 3 | 5 | 6 | 03030000 |
| 19 | สายอะลูมิเนียม หรือสายทองแดงหุ้มฉนวน PVC 750 โวลต์ 70°ซ.<br>CABLE, Al OR Cu, PVC-INSULATED, 750 V, 70°C | | | | | 02070100 or 02070101 |
| 20 | เข็มรัดรัดสาย (ทำด้วยลวดอะลูมิเนียม 1X10 มม.) ช่วงระยะ 50 ซม.<br>CABLE STRAP (MADE OF ARMOUR TAPE 1X10 mm) AT 50 cm INTERVALS | 3 M. m | 3 M. m | 6 M. m | 6 M. m | 02200000 |
| 21 | ตะปูหัวกลมแบน ยาว 15-20 มม. Ø1 มม. มอก. 113<br>NAIL, ROUND MILD STEEL WIRE 15-20 mm LONG Ø 1 mm TIS 113 | 24 | 24 | 40 | 40 | |

**ข้อแนะนำในการติดตั้งแร็คแรงต่ำรับสายหลังมิเตอร์**

ในกรณีที่ติดตั้งมิเตอร์ใหม่ จำนวน 3 หรือ 4 เครื่อง ในคราวเดียวกัน สามารถพิจารณาใช้แร็ค 4X200 มม. (วัสดุเลขที่ 03130002) แทนแร็ค 2X200 มม. วัสดุลำดับที่ 17 ได้ โดยลดจำนวนสลักเกลียว วัสดุลำดับที่ 15 คงเหลือ 2 ชุด และลดจำนวนแหวนสี่เหลี่ยมวัสดุลำดับที่ 16 คงเหลือ 2 อัน

**ข้อแนะนำในการจัดทำเข็มรัดรัดสายด้วยลวดอะลูมิเนียมแบน 1X10 มม.**

— ถ้าเป็นสายเข้า หรือ ออกจากมิเตอร์ จำนวน 1-2 เครื่อง ใช้ลวดอะลูมิเนียมแบน 1X10 มม. ยาว 15 ซม. ต่อหนึ่งจุด
— ถ้าเป็นสายเข้า หรือ ออกจากมิเตอร์ จำนวน 3-4 เครื่อง —"— —"— ยาว 20 ซม. —"—

**หมายเหตุ**

1 แบบนี้เหมาะสำหรับก่อสร้างในเขตเมือง หรือย่านชุมชน
2 การเข้าปลายสายอะลูมิเนียมหุ้ม PVC สีฟ้า และสายทองแดงหุ้มฉนวน ดูแบบเลขที่ SAI-015/21006 และ SAI-015/21005 (การประกอบเลขที่ 9529 และ 0520)

COPY

NOTES

1 THIS CONSTRUCTION DRAWING IS SUITABLE FOR URBAN AREA.
2 SKY BLUE PVC INSULATED ALUMINIUM CONDUCTOR AND INSULATED COPPER CONDUCTOR DEADENDING SEE DWG. NO. SAI-015/21006 AND SAI-015/21005 (ASSEMBLY NO. 9529 AND 0520)

| | | |
|---|---|---|
| กองวิศวกรรมไฟฟ้าและเครื่องกล<br>ฝ่ายวิศวกรรม | **การไฟฟ้าส่วนภูมิภาค** | ใช้แทนแบบ<br>ถูกแทนโดยแบบ |
| ผู้เขียน<br>ผู้ตรวจ<br>วิศวกร<br>หัวหน้าแผนก<br>ผู้อำนวยการกอง<br>ผู้อำนวยการฝ่าย | ผู้ว่าการ 18 มิ.ย. 2538 | เขียนเสร็จวันที่ 19 ธ.ค. 37<br>แก้เขียนวันที่ 12 ก.ค. 41<br>มิติเป็น<br>มาตราส่วน |
| ของผู้ว่าการฝ่ายเทคนิค | การติดตั้งมิเตอร์ 1 เฟส 220 โวลต์ ขนาด 3-15 แอมป์ บนเสาคอนกรีต 8 ม. (สายเข้ามิเตอร์ทองแดง)<br>3-15 A, 1-Ø, 220 V METER INSTALLATION ON 8 m CONCRETE POLE (Cu SERVICE ENTRANCE CABLE) | แบบเลขที่ SA4-015/37030<br>แผ่นที่ 6 ของจำนวน 6 แผ่น |