


การประกอบเลขที่ ASSEMBLY NO. 0604

แบบที่ TYPE I สำหรับระบบจำหน่ายแรงต่ำ 2 วงจร FOR SECONDARY LINE 2 CIRCUITS

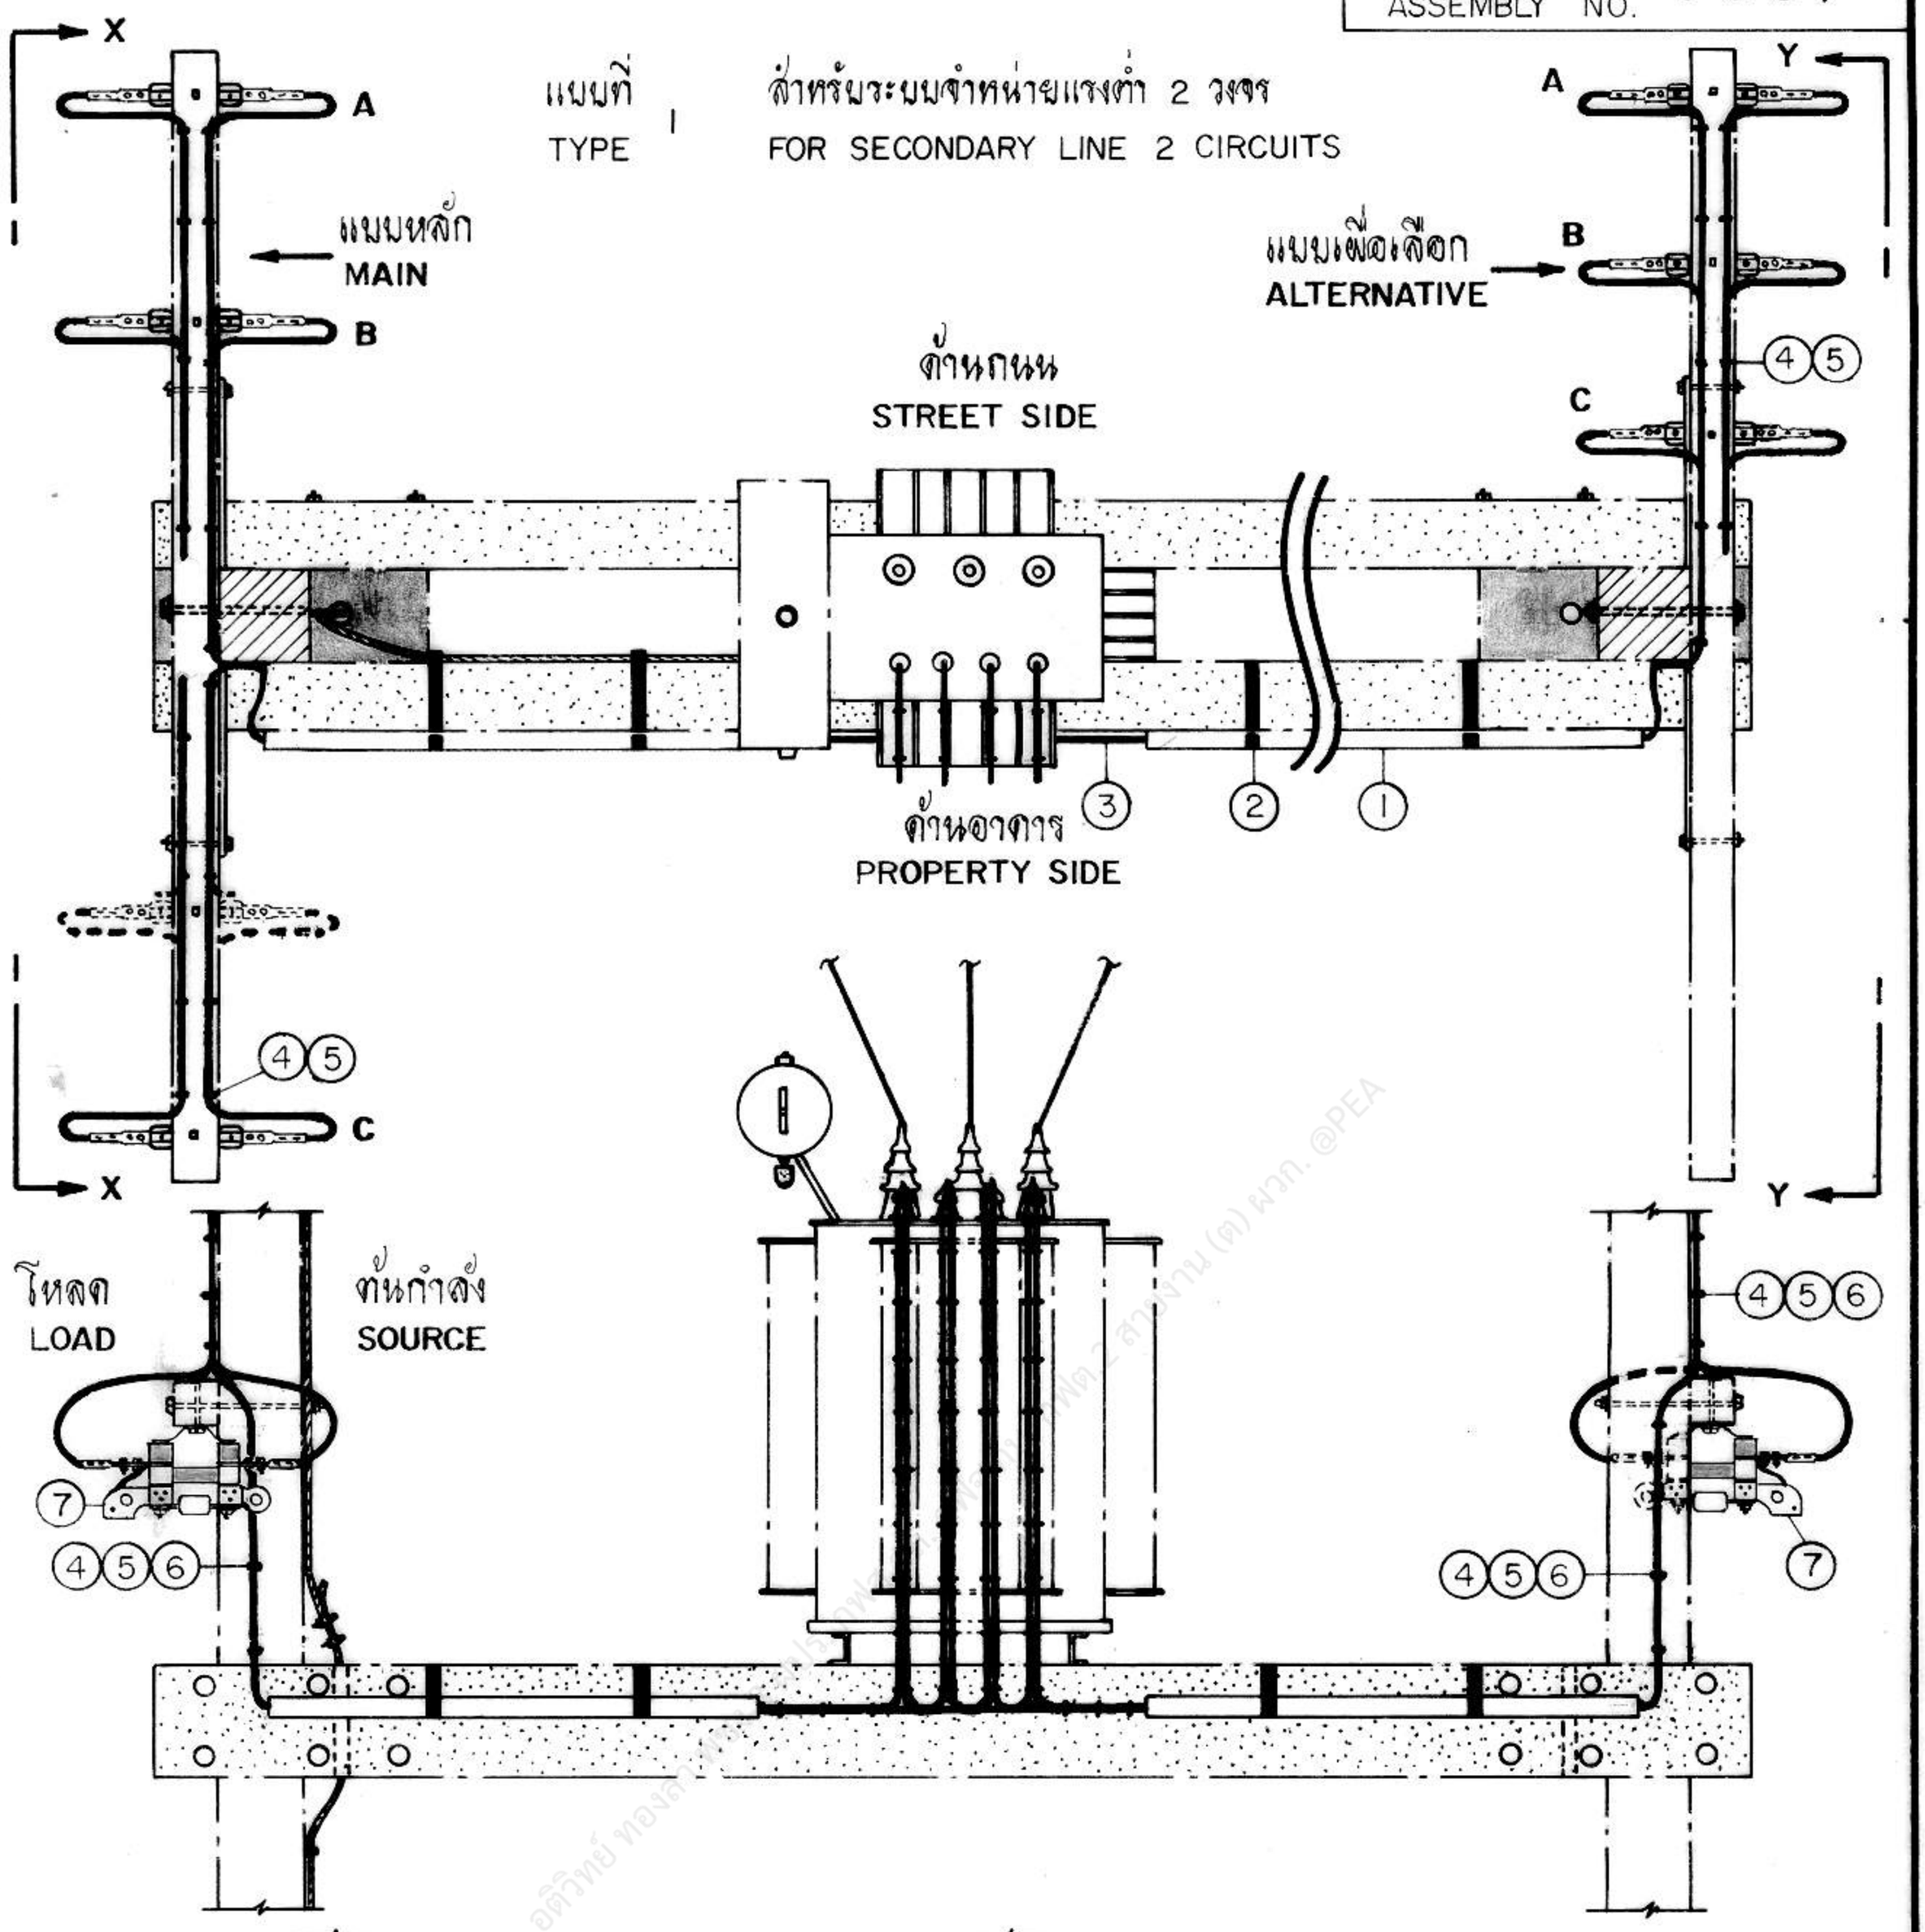

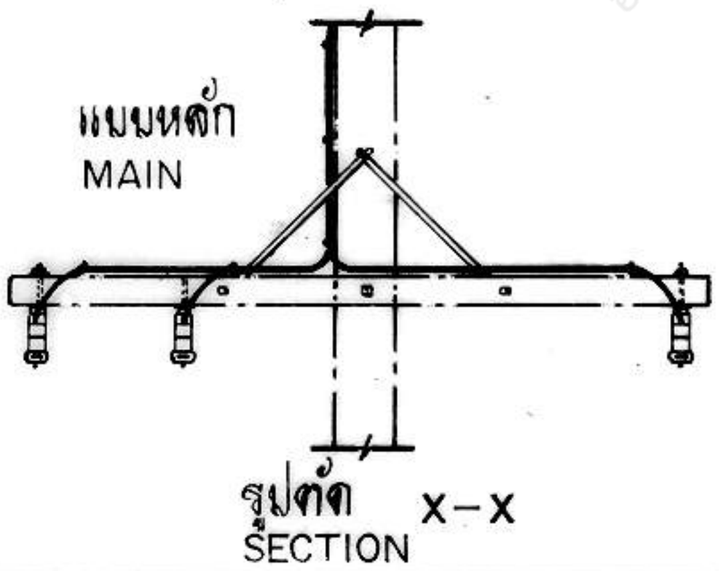

รูปตัด X–X
SECTION

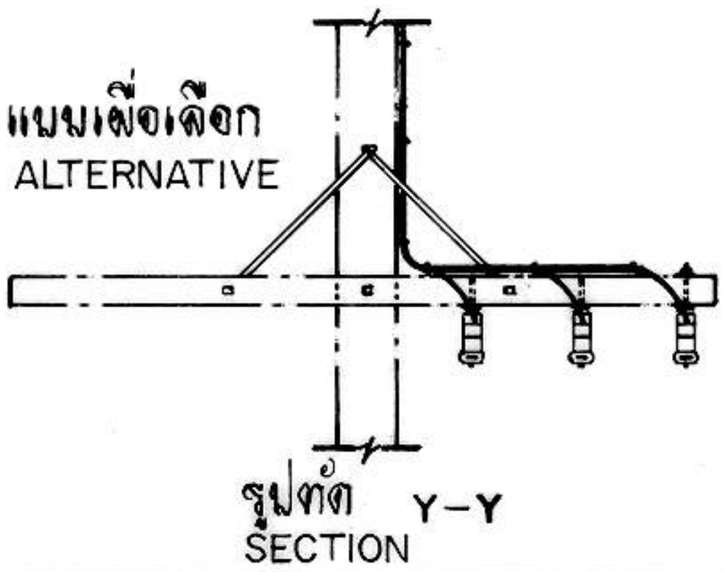

รูปตัด Y–Y
SECTION

แบบเผื่อเลือก


เหมาะสมสำหรับการติดตั้งในจุดที่มีแนวโน้มขยายโหลด เพื่อเพิ่มวงจรระบบจำหน่ายแรงต่ำในอนาคต.


กองวิศวกรรมไฟฟ้าและเครื่องกล ฝ่ายวิศวกรรม	การไฟฟ้าส่วนภูมิภาค	ใช้แทนแบบ ถูกแทนโดยแบบ เขียนเสร็จวันที่ 24 ม.ค. 21 แก้แบบวันที่ 18 ก.ค. 28 มิติเป็น มม. มาตราส่วน 1 : 25, 1 : 50
ผู้เขียน ผู้สำรวจ วิศวกร หัวหน้าแผนก หัวหน้ากอง ผู้อำนวยการฝ่าย	ผู้ว่าการ 23 ก.พ. 21	
รองผู้ว่าการฝ่ายเทคนิค	การต่อสายแรงต่ำออกจากหม้อแปลง ที่นั่งร้านหม้อแปลง คาน คอร. L.T. WIRING FROM TRANSFORMER AT PRESTRESSED CONCRETE PLATFORM	แบบเลขที่ SAI-015/21007 แผ่นที่ 1 ของจำนวน 3 แผ่น

การประกอบเลขที่ ASSEMBLY NO. 0604


แบบที่ TYPE 2

สำหรับระบบจำหน่ายแรงต่ำ 4 วงจร
FOR SECONDARY LINE 4 CIRCUITS

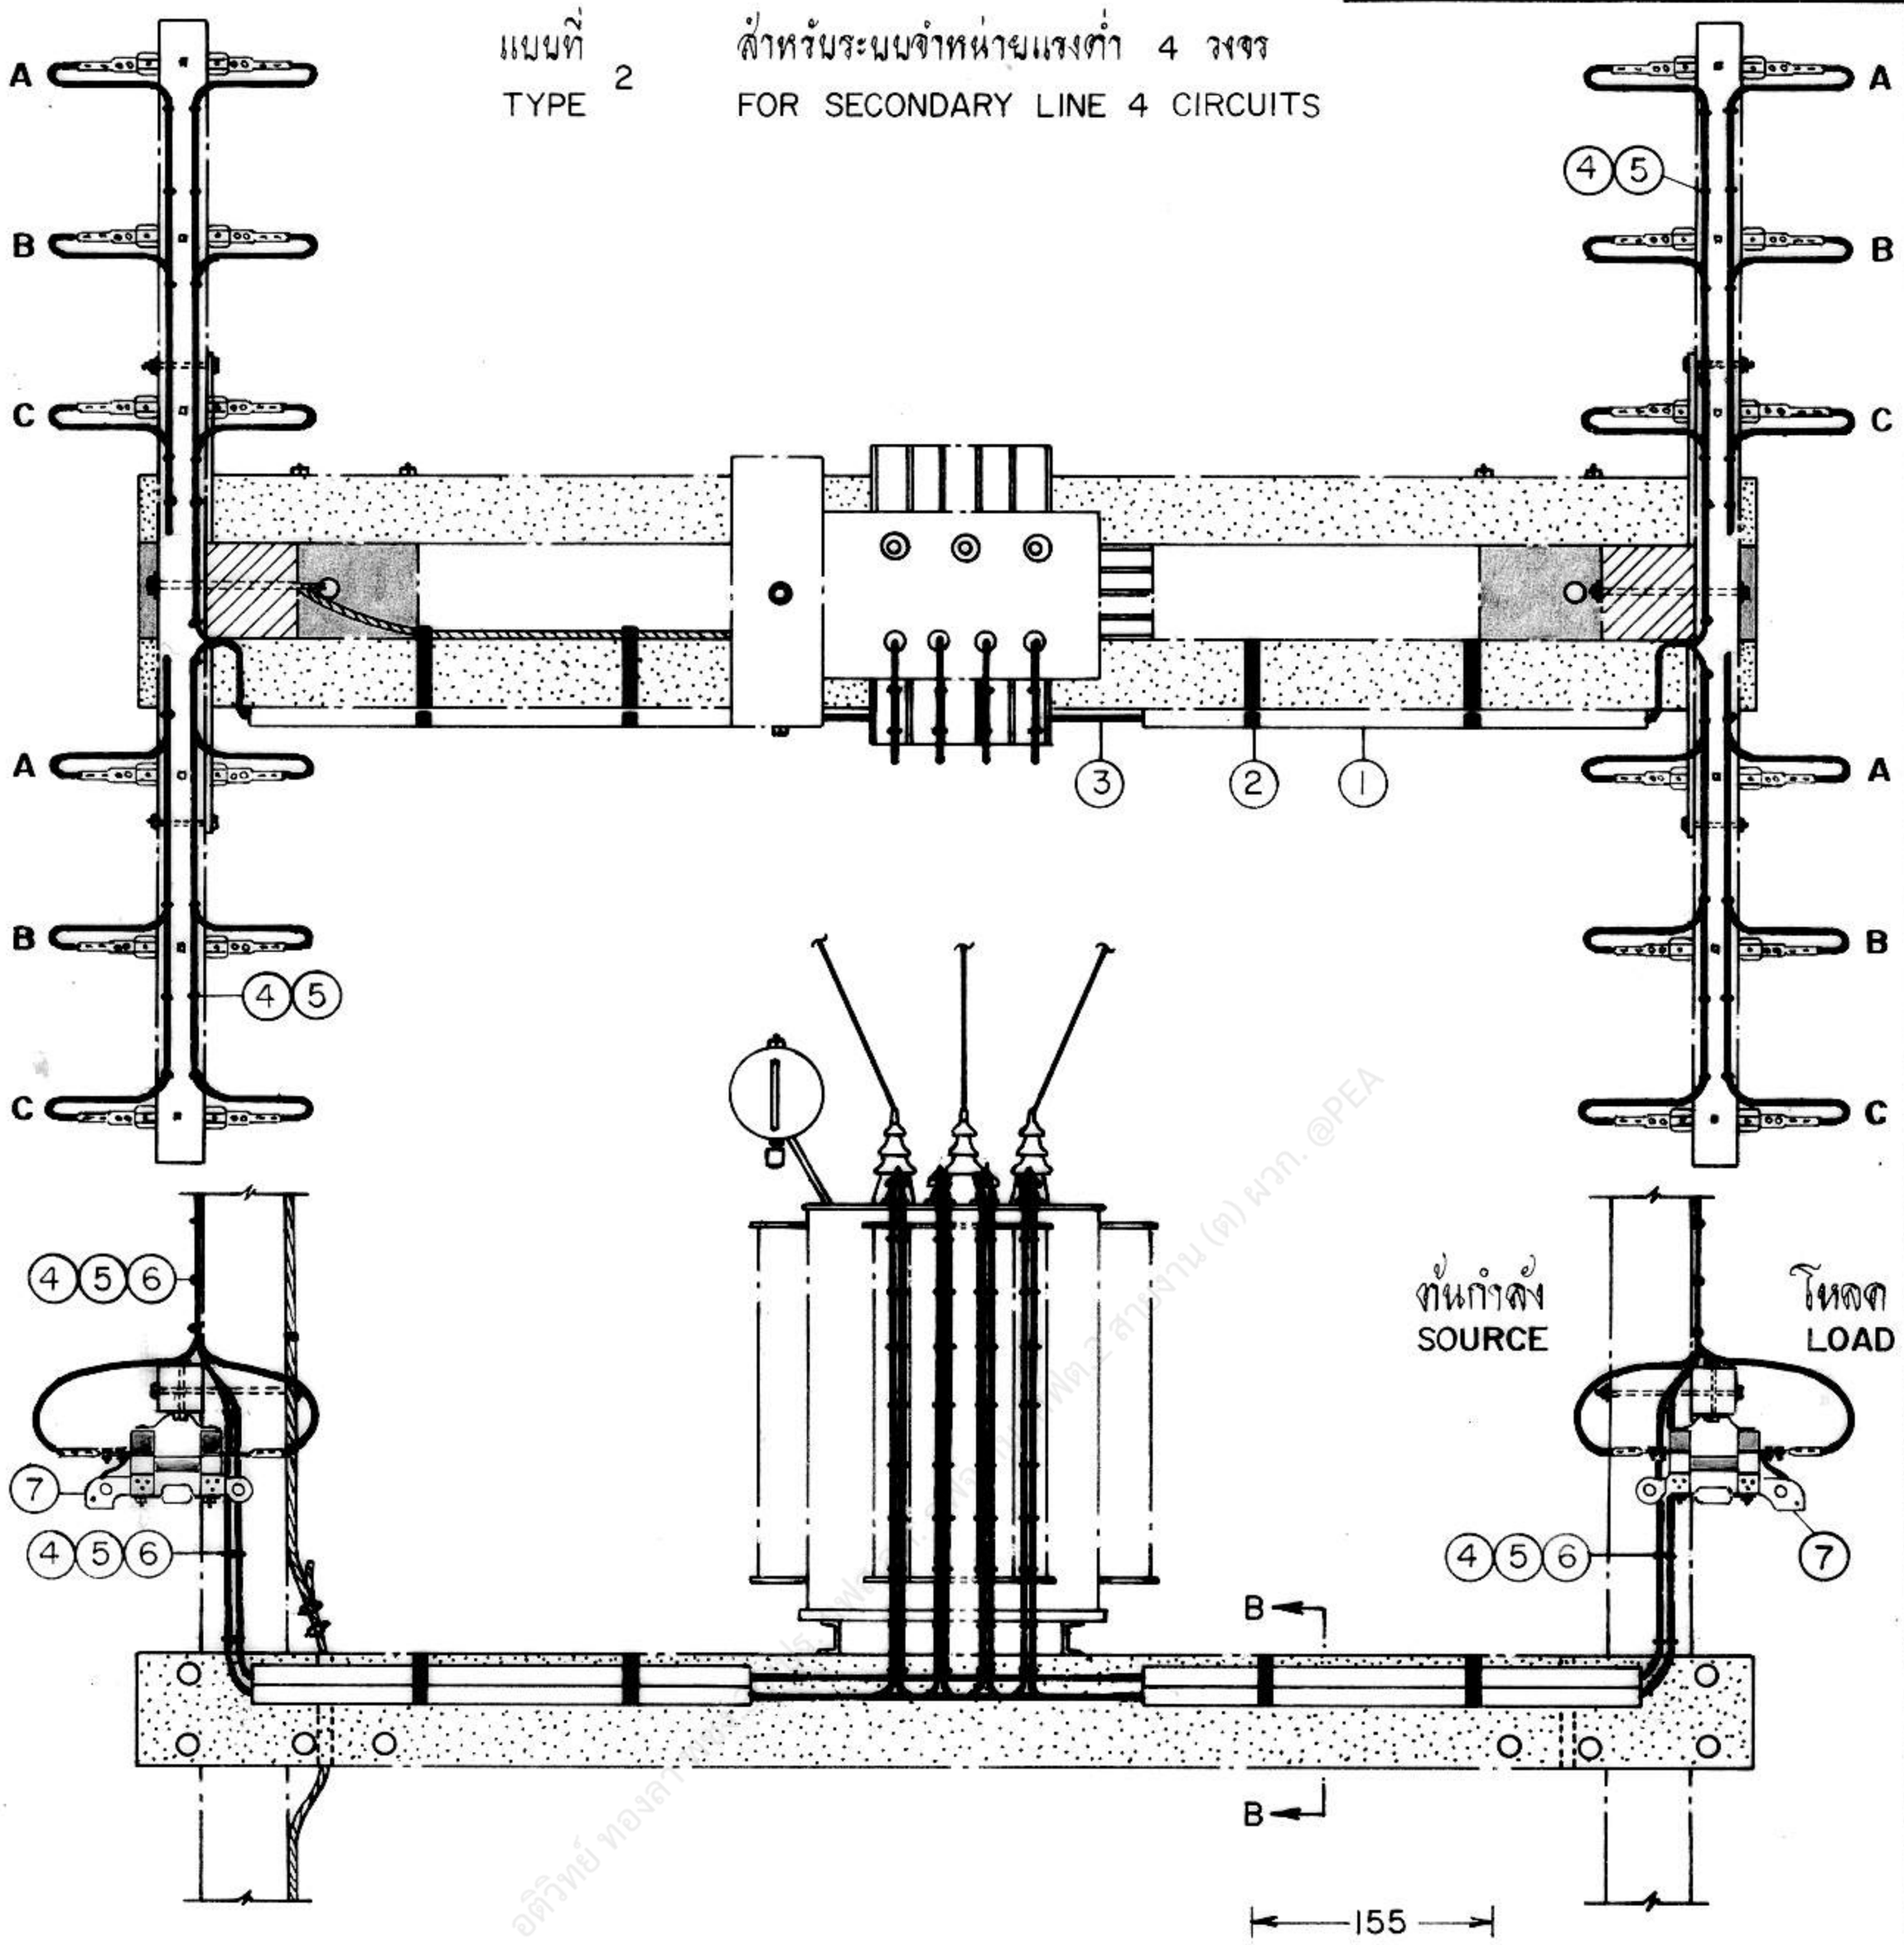

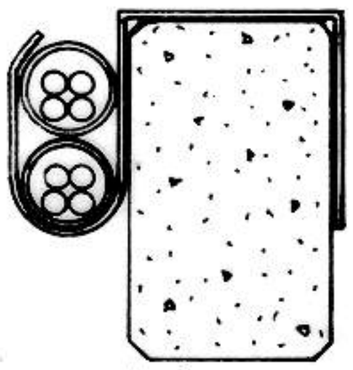

รูปตัด B–B
SECTION

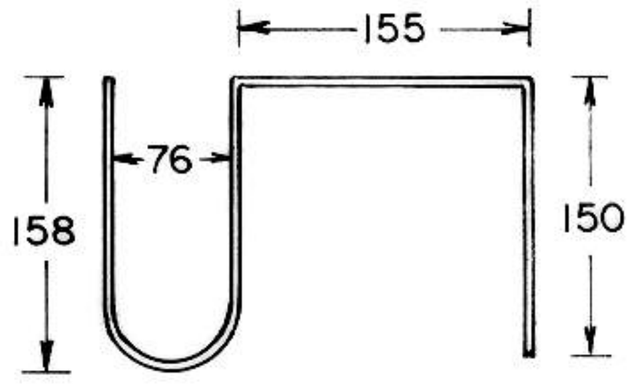

เหล็กแบน 30X4 มม.ยาว 665 มม.
FLAT IRON 30X4 mm, 665 mm LONG

กองวิศวกรรมไฟฟ้าและเครื่องกล ฝ่ายวิศวกรรม	การไฟฟ้าส่วนภูมิภาค	ใช้แทนแบบ ถูกแทนโดยแบบ เขียนเสร็จวันที่ 24 ม.ค. 21 แก้แบบวันที่ 18 ก.ค. 28 มิติเป็น มม. มาตราส่วน 1:25
ผู้เขียน ผู้สำรวจ วิศวกร หัวหน้าแผนก หัวหน้ากอง ผู้อำนวยการฝ่าย	ผู้ว่าการ 23 พ.ย. 21	
รองผู้ว่าการฝ่ายเทคนิค	การต่อสายแรงต่ำออกจากหม้อแปลง ที่หั่งร้านหม้อแปลง คาน คอร. L.T. WIRING FROM TRANSFORMER AT PRESTRESSED CONCRETE PLATFORM	แบบเลขที่ SAI-015/21007 แผ่นที่ 2 ของจำนวน 3 แผ่น

อติวิทย์ ทองสาย (ค) ผวก. @PEA

การประกอบเลขที่ ASSEMBLY NO. 0604

บัญชีวัสดุ
BILL OF MATERIAL

ลำดับที่ ITEM	รายละเอียด DESCRIPTION	จำนวน REQ'D 1	จำนวน REQ'D 2	วัสดุเลขที่ MAT. NO.
1	ท่อ PVC แข็ง ขนาด 65 X 1,000 มม. (มอก. 216) RIGID PVC CONDUIT 65 X 1,000 mm (TIS 216)	2	4	08040003
2	เหล็กแขวนท่อ PVC (เหล็กแผน 30 X 4 มม. มอก. 55) STEEL BRACKET (FLAT IRON 30 X 4 mm TIS 55)	4	4	05100002
3	สายอะลูมิเนียมหุ้มฉนวน ใช้ภายนอก 0.6/1 kV ขนาดตามต้องการ CONDUCTOR, INSULATED WEATHER PROOF 0.6/1 kV, AI SIZE AS REQ'D	50 ม. m	100 ม. m	02070002-4
4	เข็มขัดรัดสายไฟฟ้า (สเตอะลูมิเนียมแผน 1X10 มม.) STRAP, CABLE (ARMOUR TAPE 1 X 10 mm)	0.50 กก. kg	0.75 กก. kg	02200000
5	ตะปู ยาว 35 มม. NAIL, STEEL 35 mm LONG	50	60	01990000
6	หมุดไม้สำหรับอุดรูเสาคอนกรีต ขนาด Ø 19 X 21 มม. ยาว 60 มม. (ทำด้วยไม้เนื้อแข็ง) WOOD. PLUG, SIZE Ø 19 X 21 mm, 60 mm LONG (MADE OF HARD WOOD)	16	16	
7	ฟิวส์ สวิตช์แรงต่ำ 1 X 400 แอมป์ 500 โวลต์ L.T. FUSE SWITCHES 1X 400 A, 500 V	6	12	04020100

หมายเหตุ 1. ขนาดของสายไฟฟ้าที่ต่อลงหม้อแปลง (ด้านแรงสูง)

1.1 หม้อแปลงขนาดไม่เกิน 1,000 kVA ใช้สายอะลูมิเนียมขนาด 35-70 ต.มม. (ปกติใช้ขนาด 50 ต.มม.)

1.2 หม้อแปลงขนาดตั้งแต่ 1,000 kVA ขึ้นไป ใช้สายอะลูมิเนียมขนาด 70-95 ต.มม.

2. ขนาดของหม้อแปลง ที่ติดตั้งบนหนั่งร้าน ดูแบบเลขที่ S02-015/19159 (การประกอบเลขที่ 2706, 3706)

3. สายแรงต่ำที่ต่อออกจากหม้อแปลง ไปยังระบบจำหน่ายแรงต่ำ เป็นสายหุ้มฉนวนใช้ภายนอกทั้งสายเฟสและสายเป็นกลาง

4. ระยะห่างระหว่างเข็มขัดรัดสายประมาณ 200 มม.

5. เหล็กแขวนท่อ PVC สามารถนำเหล็กแผน 30 X 3.5 มม. อาบสังกะสี วัสดุเลขที่ 01220010 มาตัดทำได้

NOTES 1. RECOMMENDATION OF CONDUCTOR SIZE LEAD TO TRANSFORMER (H.T. SIDE)

1.1 TRANSFORMER CAPACITY NOT EXCEEDING 1,000 kVA, USE ALUMINIUM CONDUCTOR 35-70 mm^2 (50 mm^2 IS PREFERABLE)

1.2 TRANSFORMER CAPACITY 1,000 kVA AND ABOVE, USE ALUMINIUM CONDUCTOR 70-95 mm^2

2. RECOMMENDATION OF TRANSFORMER CAPACITY INSTALLED ON PLATFORM SEE DWG. NO. S02-015/19159 (ASSEMBLY NO. 2706, 3706)

3. BOTH PHASE AND NEUTRAL CONDUCTORS LEAD FROM TRANSFORMER TO SECONDARY LINE ARE INSULATED WEATHER PROOF CONDUCTORS.

4. STRAP (CABLE) AT APPROX. 200 mm INTERVAL.

5. STEEL BRACKET MAY BE MADE OF FLAT IRON 30 X 3.5 mm GALV. MAT. NO. 01220010.

กองวิศวกรรมไฟฟ้าและเครื่องกล ฝ่ายวิศวกรรม	การไฟฟ้าส่วนภูมิภาค	ใช้แทนแบบ ถูกแทนโดยแบบ เขียนเสร็จวันที่ 24 ม.ค. 21 แก้แบบวันที่ มิติเป็น มาตราส่วน
ผู้เขียน ผู้สำรวจ วิศวกร หัวหน้าแผนก หัวหน้ากอง ผู้อำนวยการฝ่าย	ผู้ว่าการ 23 ก.พ. 21	
รองผู้ว่าการฝ่ายเทคนิค	การต่อสายแรงต่ำออกจากหม้อแปลง ที่นั่งร้านหม้อแปลง คาน คอร. L.T. WIRING FROM TRANSFORMER AT PRESTRESSED CONCRETE PLATFORM	แบบเลขที่ SA1-015/21007 แผ่นที่ 3 ของจำนวน 3 แผ่น