
การประกอบเลขที่ ASSEMBLY NO. 0402

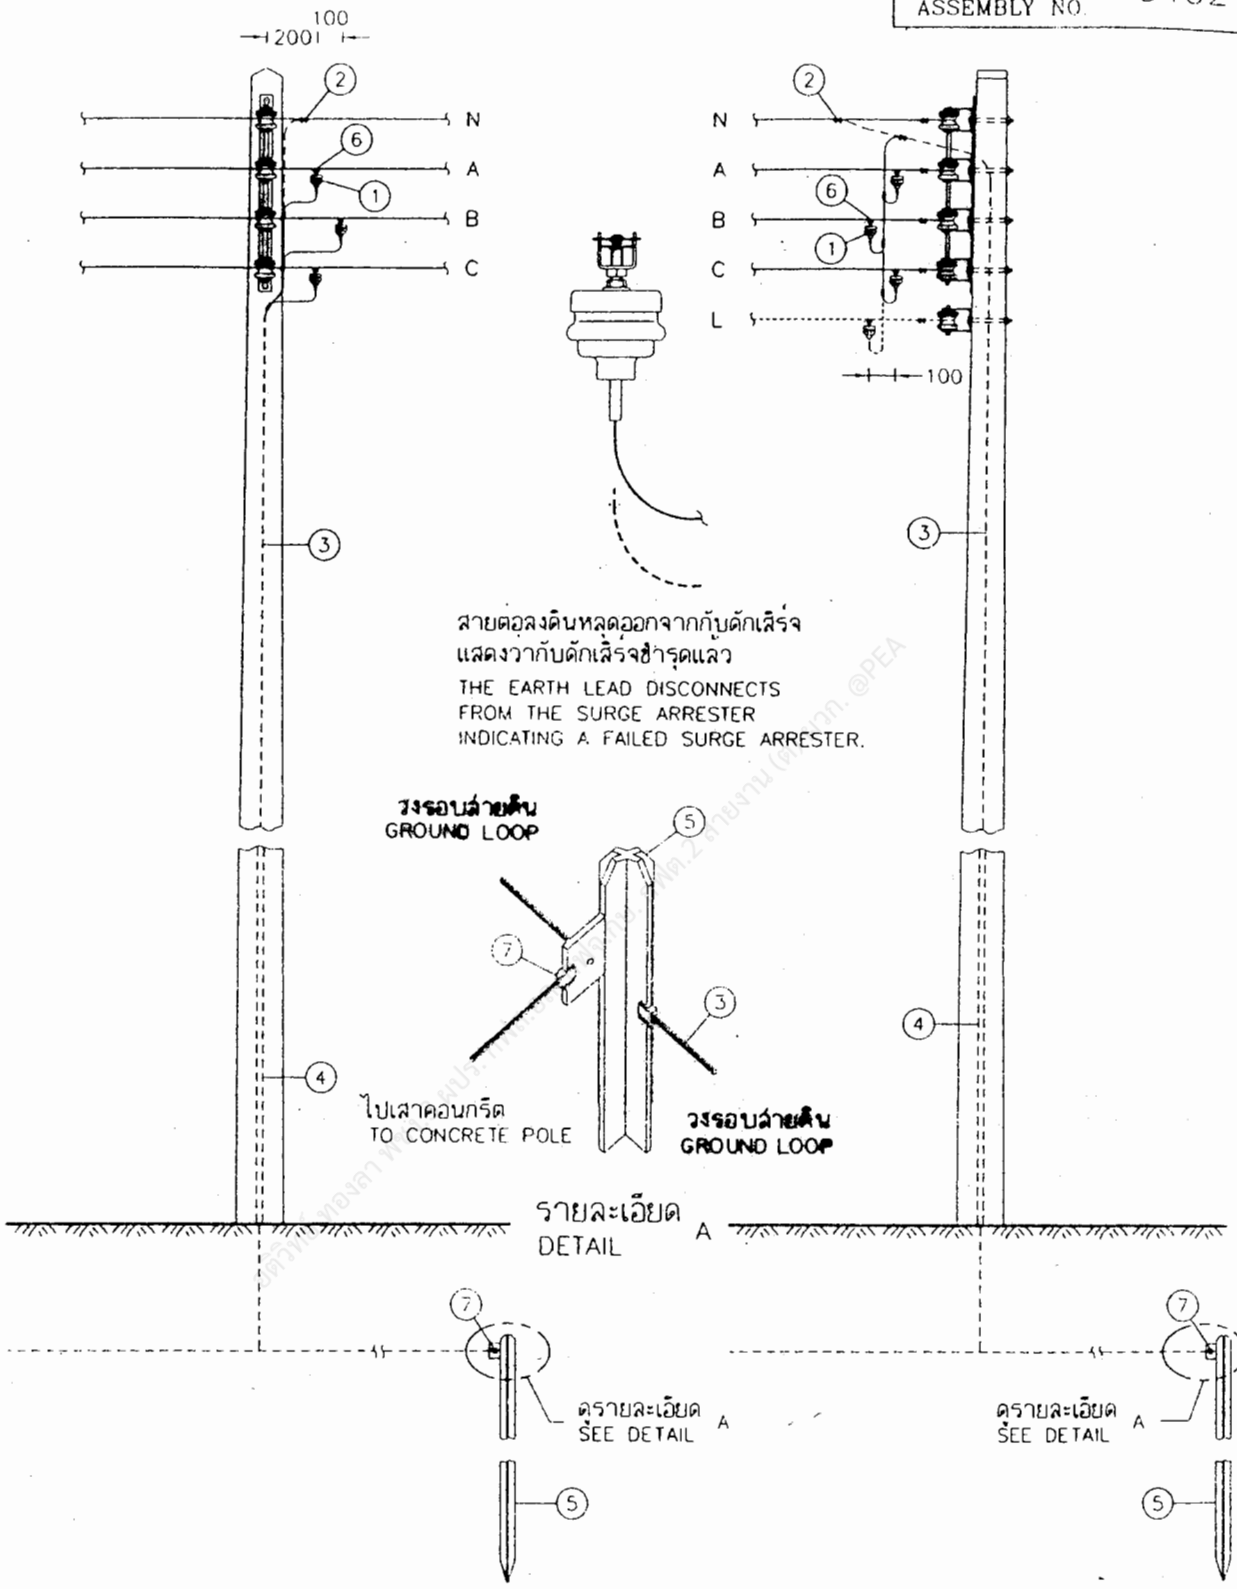

กองมาตรฐานระบบไฟฟ้า ฝ่ายมาตรฐานและความปลอดภัย	การไฟฟ้าส่วนภูมิภาค	ใช้แทนแบบ SA1-015/22040 ถูกแทนโดยแบบ .....
ผู้เขียน ..... ผู้สำรวจ ..... วิศวกร ..... หัวหน้าแผนก ..... ผู้อำนวยการกอง ..... ผู้อำนวยการฝ่าย	ผู้ว่าการ ..... 5 ม.ค. 2550 การติดตั้งกับดักเสิร์จแรงต่ำ ในระบบจำหน่ายแรงต่ำ	เขียนเสร็จวันที่ 3 เม.ย. 2550 แก้แบบวันที่ ..... มิติเป็น ..... มาตราส่วน .....
รองผู้ว่าการวางแผน และพัฒนาระบบไฟฟ้า ..... 5 ม.ค. 2550	L.V. SURGE ARRESTER INSTALLATION IN L.V. DISTRIBUTION LINE	แบบเลขที่ SA2-015/50004 แผ่นที่ 1 ของจำนวน 2 แผ่น

การประกอบเลขที่ ASSEMBLY NO 0402

บัญชีวัสดุ
BILL OF MATERIAL

ลำดับที่ ITEM	รายละเอียด DESCRIPTION	จำนวน REQ'D	วัสดุเลขที่ MAT. NO.
1	กับดักเสิร์จ 480 โวลต์ 5.0 กิโลแอมป์ SURGE ARRESTER 480 V, 5.0 kA		1040000300
2	คอนเนคเตอร์ชนิดบีบ สำหรับสายเมนอะลูมิเนียม 50-95 ต.มม. สายแยกลวดเหล็ก 50 ต.มม. CONNECTOR, COMPRESSION TYPE, MAIN LINE Al 50-95 mm^2 TAP OFF STEEL 50 mm^2	1	1023020003
3	ลวดเหล็กตีเกลียว 50/7 ต.มม. มอก. 404 WIRE, STEEL STRANDED 50/7 mm^2 TIS 404	20 ม. m	1010100004
4	ท่อ PVC แข็ง ขนาด ø 20x2,500-4,000 มม. พร้อมอุปกรณ์ยึด CONDUIT, PVC RIGID, ø 20x2,500-4,000 mm, COMP. WITH FIXING ACCESS.	1	1080040002 or 1080040001
5	หลักดิน 60x60x5 มม. ยาว 2 ม. ROD, GROUND, 60x60x5 mm, 2 m LONG	1	1010220002
6	PVC เทป กว้าง 19 มม. (ใช้ความยาว 2 ม. ต่อ จุด) มอก. 386 PVC TAPE 19 mm WIDE (2 m LONG PER POINT) TIS 286		1020180001 or 1020180002
7	จุดต่อสายดินกับหลักดินแบบเชื่อมด้วยความร้อน EXOTHERMIC WELDING POINT BETWEEN GROUND WIRE AND GROUND ROD	3	-

หมายเหตุ
1 ระยะห่างระหว่างจุดยึดสายลงดิน 500 มม.
2 ตำแหน่งติดตั้งกับดักเสิร์จในระบบจำหน่ายแรงต่ำ ดูแบบเลขที่ SA2-015/50003 (การประกอบเลขที่ 0401)
3 จำนวนกับดักเสิร์จที่ติดตั้ง :

ระบบ 1 เฟส 2 สาย ติดตั้งกับดักเสิร์จ 1 ชุด
ระบบ 1 เฟส 3 สาย ติดตั้งกับดักเสิร์จ 2 ชุด
ระบบ 3 เฟส 4 สาย ติดตั้งกับดักเสิร์จ 3 ชุด

ถ้ามีสายดับไฟถนน ให้เพิ่มกับดักเสิร์จอีก 1 ชุด
4 ก่อนเชื่อมให้ขัดเอาสังกะสีบริเวณที่จะเชื่อมออก และเมื่อเชื่อมเสร็จแล้วให้พ่น SPRAY ZINC ทับรอยเชื่อมด้วย

NOTES
1 GROUND LEAD CLAMPS AT 500 mm INTERVAL.
2 SURGE ARRESTER INSTALLATION IN L.V. DISTRIBUTION LINES SEE DWG. No. SA2-015/50003 (ASSEMBLY No. 0401)
3 NUMBER OF SURGE ARRESTERS :

1-ø 2-WIRE INSTALL 1 ARRESTER,
1-ø 3-WIRE INSTALL 2 ARRESTERS,
3-ø 4-WIRE INSTALL 3 ARRESTERS,

ONE ARRESTER SHALL BE ADDED FOR STREET LIGHT CONTROL WIRE.
4 BEFORE WELDING, ZINC COATED SURFACE HAS TO BE REMOVED.
THE WELDING POINT HAS TO BE ZINC SPRAYED AFTER FINISHING WELDING PROCESS.

กองมาตรฐานระบบไฟฟ้า ฝ่ายมาตรฐานและความปลอดภัย	การไฟฟ้าส่วนภูมิภาค	ใช้แทนแบบ SA1-015/22040 ถูกแทนโดยแบบ .....
ผู้เขียน ..... ผู้สำรวจ ..... วิศวกร ..... หัวหน้าแผนก ..... ผู้อำนวยการกอง ..... ผู้อำนวยการฝ่าย	ผู้ว่าการ ..... 5 เม.ย. 2550 การติดตั้งกับดักเสิร์จแรงต่ำ ในระบบจำหน่ายแรงต่ำ	เขียนเสร็จวันที่ 3 เม.ย. 2550 แก้แบบวันที่ ..... มิติเป็น ..... มาตราส่วน .....
รองผู้ว่าการวางแผน และพัฒนาระบบไฟฟ้า ..... 5 เม.ย. 2550	L.V. SURGE ARRESTER INSTALLATION IN L.V. DISTRIBUTION LINE	แบบเลขที่ SA2-015/50004 แผ่นที่ 2 ของจำนวน 2 แผ่น