

การประกอบเลขที่
ASSEMBLY NO. 5 2 3 3

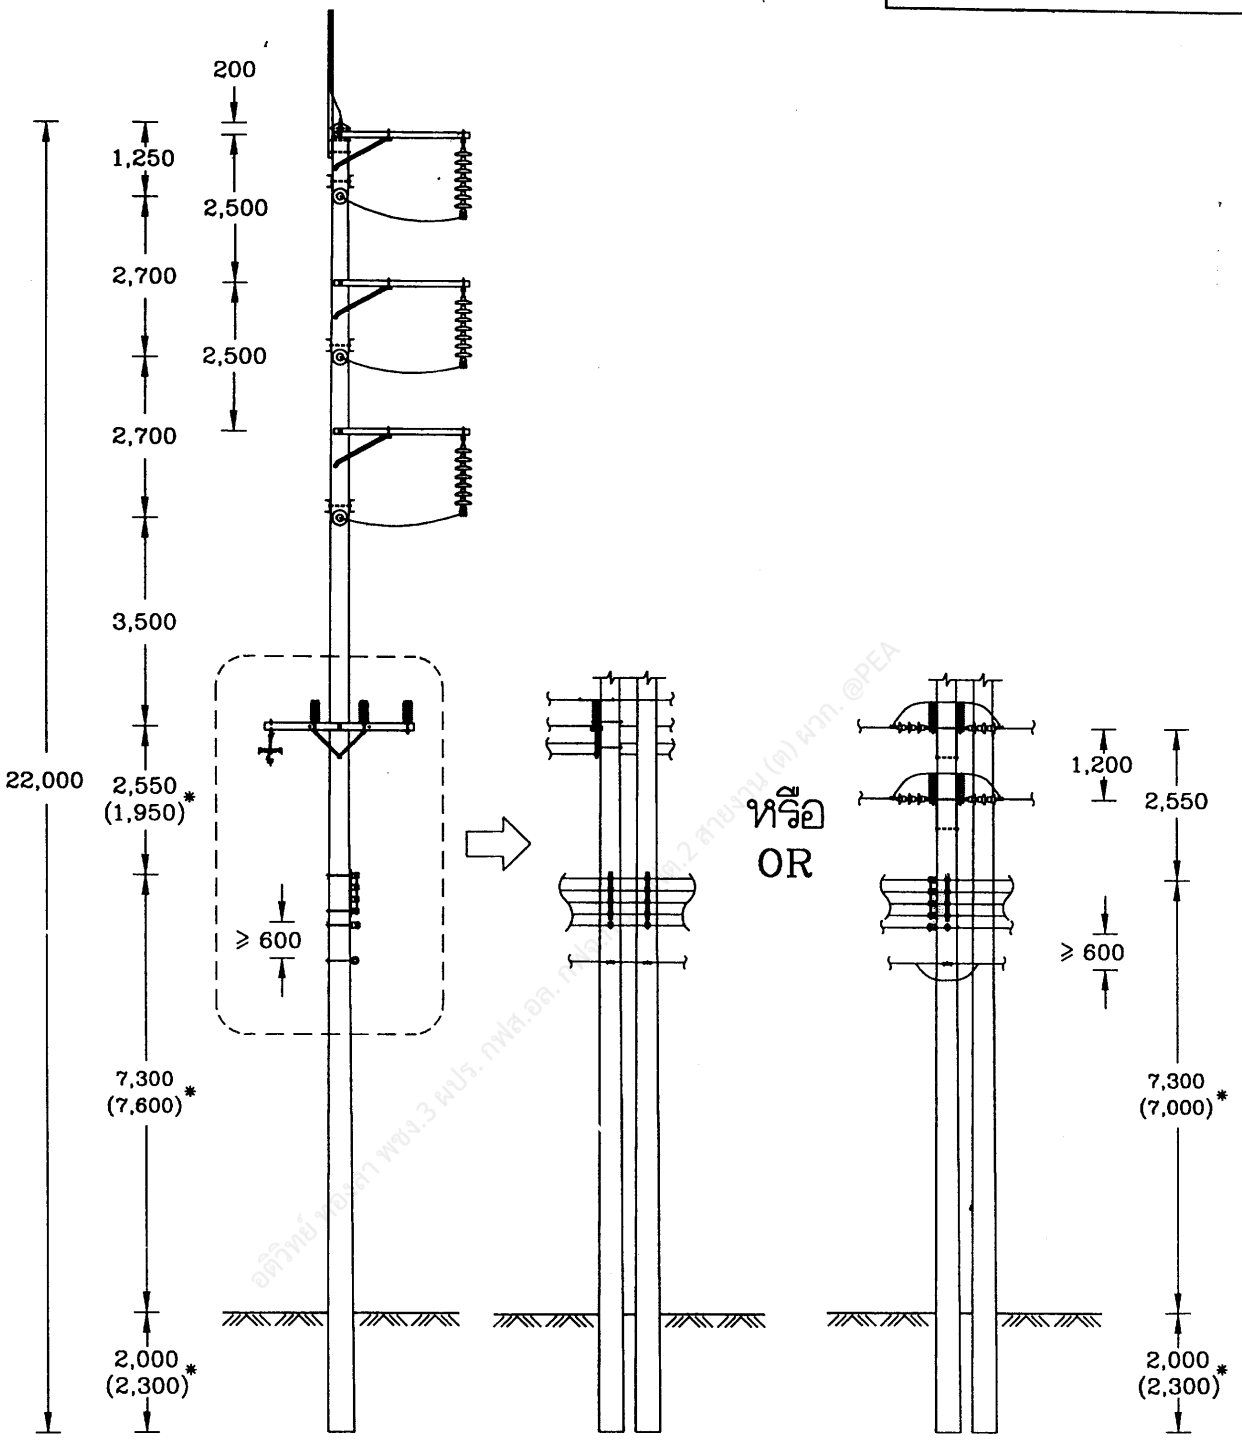


* ดูหมายเหตุ
SEE NOTE 1

กองมาตรฐานระบบไฟฟ้า ฝ่ายมาตรฐานและความปลอดภัย	การไฟฟ้าส่วนภูมิภาค	ใช้แทนแบบ ..... ถูกแทนโดยแบบ .....
ผู้เขียน ...ลมชาย..... ผู้สำรวจ ..... วิศวกร ..... หัวหน้าแผนก ..... ผู้อำนวยการกอง ..... ผู้อำนวยการฝ่าย	ผู้ว่าการ	เขียนเสร็จวันที่ 16 พ.ค. 2550 แก้แบบวันที่ ..... มิติเป็น ...มิลลิเมตร..... มาตราส่วน ...1:125.....
รองผู้ว่าการวางแผนและวิศวกรระบบไฟฟ้า	115 kV วงจรเดี่ยว สายไฟฟ้าเดี่ยว เสาคู่ สำหรับเข้าปลายสายสองข้าง แบบ SS-DD-4	
	115 kV SINGLE CIRCUIT SINGLE CONDUCTOR DOUBLE POLE, DEAD END STRUCTURE TYPE SS-DD-4	แบบเลขที่ SA1-015/50011 แผ่นที่ 1 ของจำนวน 5 แผ่น

การประกอบเลขที่ ASSEMBLY NO. 5 2 3 3

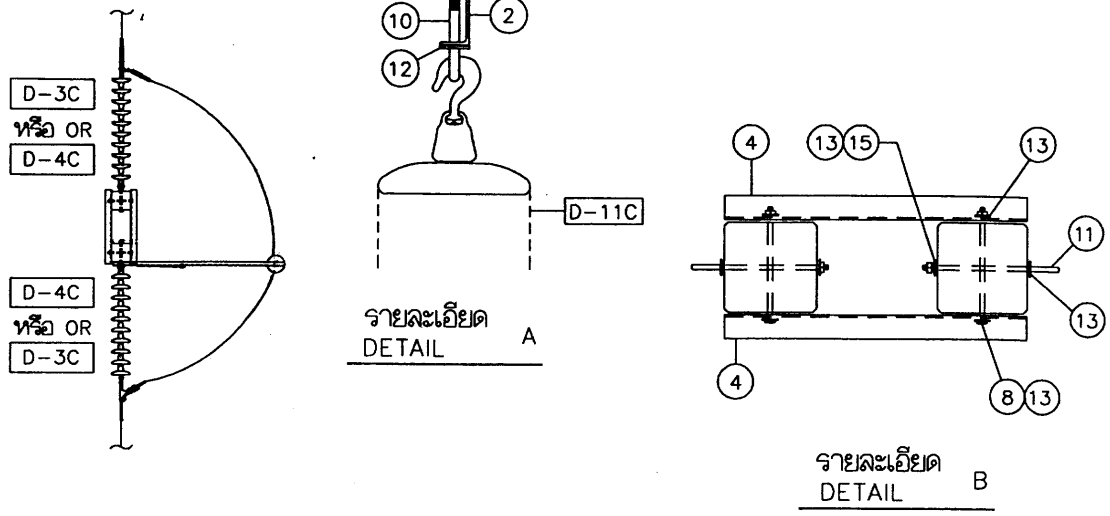

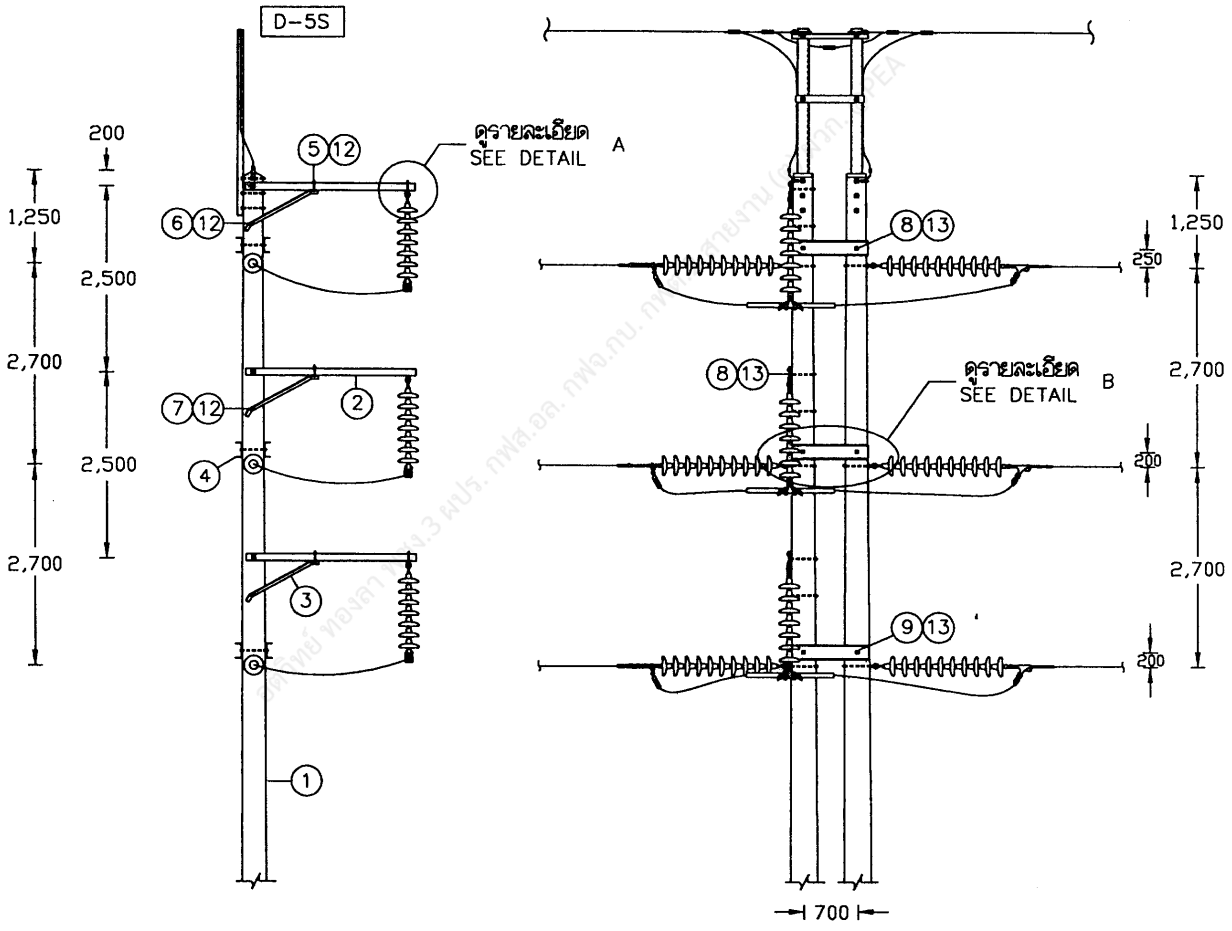

กองมาตรฐานระบบไฟฟ้า ฝ่ายมาตรฐานและความปลอดภัย	การไฟฟ้าส่วนภูมิภาค	ใช้แทนแบบ ..... ถูกแทนโดยแบบ .....
ผู้เขียน ลมชาย ..... ผู้สำรวจ ..... วิศวกร ..... หัวหน้าแผนก ..... ผู้อำนวยการกอง ..... ผู้อำนวยการฝ่าย	ผู้ว่าการ ..... 115 kV วงจรเดี่ยว สายไฟฟ้าเดี่ยว เสาคู่ สำหรับเข้าปลายสายสองข้าง แบบ SS-DD-4	เขียนเสร็จวันที่ 16 พ.ค. 2550 แก้แบบวันที่ ..... มิติเป็น มิลลิเมตร มาตราส่วน 1:100
รองผู้ว่าการวางแผนและพัฒนาระบบไฟฟ้า	115 kV SINGLE CIRCUIT SINGLE CONDUCTOR DOUBLE POLE, DEAD END STRUCTURE TYPE SS-DD-4	แบบเลขที่ SA1-015/50011 แผ่นที่ 2 ของจำนวน 5 แผ่น

การประกอบเลขที่
ASSEMBLY NO. 5 2 3 3

ลำดับที่ ITEM	วงจรไฟฟ้า SYSTEM CIRCUIT	ขนาดสายสูงสุด (ต.มม.) MAX.COND.SIZE (mm^2)	จำนวน (เส้น) QUANTITY (WIRE)	ระยะหย่อนยานของสายไม่น้อยกว่า (ม.) (m) MINIMUM SAG ช่วง SECTION (A)	ช่วง SECTION (B)
I	สายล่อฟ้า OHGW	35	1	0.10	0.15
II	สายเปลือย 115 kV 115 kV Al CONDUCTOR	400	3	0.20	0.35
III	22.33 kV สายเปลือย หรือ เคเบิลอากาศ 22.33 kV Al CONDUCTOR OR AERIAL CABLE	185	3	0.70	0.85
IV	22.33 kV เคเบิลอากาศ 22.33 kV AERIAL CABLE	185	3	0.95	0.95
V	สายแรงต่ำ L.V. CONDUCTOR	95	5	0.25	0.40
VI	สายสื่อสารโทรคมนาคม TELECOMMUNICATION CABLE	≤ 55 mm (TOTAL OUTSIDE DIA.)	1	0.25	0.40

ตัวอย่างการใช้งาน
TYPICAL APPLICATION

กองมาตรฐานระบบไฟฟ้า
ฝ่ายมาตรฐานและความปลอดภัย

ผู้เขียน ลมซ่าย
ผู้สำรวจ
วิศวกร
หัวหน้าแผนก
ผู้อำนวยการกอง
ผู้อำนวยการฝ่าย

รองผู้ว่าการวางแผนและพัฒนาระบบไฟฟ้า

การไฟฟ้าส่วนภูมิภาค

ผู้ว่าการ

115 kV วงจรเดี่ยว สายไฟฟ้าเดี่ยว
เสาคู่ สำหรับเข้าปลายสายลองข้าง
แบบ SS-DD-4

115 kV SINGLE CIRCUIT SINGLE CONDUCTOR
DOUBLE POLE, DEAD END STRUCTURE
TYPE SS-DD-4

ใช้แทนแบบ
ถูกแทนโดยแบบ
เขียนเสร็จวันที่ 16 พ.ค. 2550
แก้แบบวันที่
มิติเป็น เมตร
มาตราส่วน

แบบเลขที่ SA1-015/50011
แผ่นที่ 3 ของจำนวน 5 แผ่น

การประกอบเลขที่ ASSEMBLY NO. 5233

บัญชีวัสดุ
BILL OF MATERIAL

ลำดับที่ ITEM	รายละเอียด DESCRIPTION	จำนวน REQ'D	วัสดุเลขที่ MAT. NO.
1	เสา คอร. ยาว 22.00 ม. ชนิดมีกราวด์เพลทในเสา POLE, CONCRETE, 22.00 m LONG, WITH GROUND PLATE IN POLE	2	1000010015
2	เหล็กรูปรางน้ำ ขนาด 100x50x5 มม. ยาว 2,250 มม. มอก. 1227 STEEL CHANNEL, 100x50x5 mm, 2,250 mm LONG, TIS 1227	3	1010000100
3	เหล็กประกับคอนสายแบบท้าวแขน ขนาด 50x50x6 มม. ยาว 1,000 มม. BRACE, ALLEY ARM, 50x50x6 mm, 1,000 mm LONG	3	1010200009
4	เหล็กรูปรางน้ำ 200x80x7.5 มม. ยาว 1,000 มม. STEEL CHANNEL, 200x80x7.5 mm, 1,000 mm LONG	6	1010000400
5	สลักเกลียว M 16x130 มม. BOLT, MACHINE, M 16x130 mm	3	1010110200
6	สลักเกลียว M 16x300 มม. BOLT, MACHINE, M 16x300 mm	1	1010110204
7	สลักเกลียว M 16x350 มม. BOLT, MACHINE, M 16x350 mm	2	1010110205
8	สลักเกลียว M 20x350 มม. BOLT, MACHINE, M 20x350 mm	7	1010110300
9	สลักเกลียว M 20x400 มม. BOLT, MACHINE, M 20x400 mm	2	1010110301
10	สลักห่วงโอแวล M 16x150 มม. BOLT, OVAL EYE, M 16x150 mm	3	1010150000
11	สลักห่วงโอแวล M 20x350 มม. BOLT, OVAL EYE, M 20x350 mm	6	1010150100
12	แหวนสี่เหลี่ยมแบน ขนาด 52x52x4.5มม. รู ø 18 มม. มอก. 258 WASHER, SQUARE, FLAT, 52x52x4.5 mm, HOLE ø 18 mm, TIS 258	12	1010180100
13	แหวนสี่เหลี่ยมแบน ขนาด 62x62x6 มม. รู ø 22 มม. มอก. 258 WASHER, SQUARE, FLAT, 62x62x6 mm, HOLE ø 22 mm, TIS 258	30	1010180101
14	แหวนสปริง M 16 มอก. 259 WASHER, LOCK, M 16, TIS 259	3	1010180301
15	แหวนสปริง M 20 มอก. 259 WASHER, LOCK, M 20, TIS 259	6	1010180302

กองมาตรฐานระบบไฟฟ้า
ฝ่ายมาตรฐานและความปลอดภัย

ผู้เขียน ลมชาย .....
ผู้สำรวจ .....
วิศวกร .....
หัวหน้าแผนก .....
ผู้อำนวยการกอง .....
ผู้อำนวยการฝ่าย .....

รองผู้ว่าการวางแผนและวิศวกรระบบไฟฟ้า
.....

การไฟฟ้าส่วนภูมิภาค

ผู้ว่าการ .....

115 kV วงจรเดี่ยว สายไฟฟ้าเดี่ยว
เสาคู่ สำหรับเข้าปลายสายสองข้าง
แบบ SS-DD-4

115 kV SINGLE CIRCUIT SINGLE CONDUCTOR
DOUBLE POLE, DEAD END STRUCTURE
TYPE SS-DD-4

ใช้แทนแบบ .....
ถูกแทนโดยแบบ .....
เขียนเสร็จวันที่ 16 พ.ค. 2550
แก้แบบวันที่ .....
มิติเป็น .....
มาตราส่วน .....

แบบเลขที่ SA1-015/50011
แผ่นที่ 4 ของจำนวน 5 แผ่น

การประกอบเลขที่ ASSEMBLY NO.	5233

รายละเอียด DESCRIPTION			
D-3C	การประกอบลูกถ้วยแขวน SUSPENSION INSULATOR ASSEMBLY	3	
D-4C	การประกอบลูกถ้วยแขวน SUSPENSION INSULATOR ASSEMBLY	3	
D-11C	การประกอบลูกถ้วยแขวน SUSPENSION INSULATOR ASSEMBLY	3	
D-5S	การประกอบสายล่อฟ้า OVERHEAD GROUND WIRE ASSEMBLY	1	
D-10B	ฐานรากเสา POLE FOUNDATION	1	
D-25	การต่อลงดิน GROUNDING	1	

หมายเหตุ

1.* กรณีก่อสร้างในพื้นที่เขตทางหลวง ให้ใช้ค่าระยะห่างตามแนวดิ่งในวงเล็บ โดยดูรายละเอียดเพิ่มเติมในแบบเลขที่ SA1-015/43012 (การประกอบเลขที่ 5687)
2. หลักเกณฑ์การใช้ลูกถ้วยแรงสูงในระบบสายส่ง 115 kV ให้ดูแบบเลขที่ SA1-015/50001 (การประกอบเลขที่ 5163)
3. รูปแบบตัวอย่างการใช้งานดังกล่าวในแผ่นที่ 3 ให้ใช้เฉพาะในกรณีที่ไม่สามารถติดตั้งสายยึดโยงตามแบบเลขที่ SA1-015/48001 (การประกอบเลขที่ 5151) ได้ โดยระยะห่างระหว่างช่วงเสาของโครงสร้างสายส่ง 115 kV ที่อยู่ก่อนหน้าช่วง A และหลังช่วง B ให้ดูแบบเลขที่ SA1-015/48001 (การประกอบเลขที่ 5151) และให้เข้าปลายสายสองข้างของวงจรไฟฟ้าที่อยู่ใต้ระบบสายส่ง 115 kV ที่เสาคู่ที่ติดกับช่วงก่อสร้างแบบไม่รับแรงดึง สองโครงสร้าง

NOTES

1.* IN CASE OF CONSTRUCTION IN HIGHWAY AREA, USE THE VERTICAL CLEARANCE IN THE PARENTHESIS. FOR ADDITIONAL DETAIL, SEE DWG NO. SA1-015/43012 (ASSEMBLY NO. 5687) .
2. RULES FOR H.V. INSULATOR APPLICATION IN 115 kV TRANSMISSTION SYSTEM SEE. DWG.NO. SA1-015/50001 (ASSEMBLY NO. 5163) .
3. THE TYPICAL APPLICATION IN SHEET 3 SHALL BE USED IN CASE THE GUY CAN NOT BE INSTALLED ACCORDING TO DWG.NO. SA1-015/48001 (ASSEMBLY NO. 5151) . THE SPAN LENGTHS FOR 115 kV CONSTRUCTION STRUCTURE WHICH IS BEFORE SECTION A AND AFTER SECTION B SEE DWG. NO. SA1-015/48001 (ASSEMBLY NO. 5151) AND THE CIRCUITS UNDER 115 kV LINE SYSTEM SHALL BE DOUBLE DEADENDED AT TWO STRUCTURES BEFORE SLACK SPAN SECTION .

กองมาตรฐานระบบไฟฟ้า ฝ่ายมาตรฐานและความปลอดภัย	การไฟฟ้าส่วนภูมิภาค	ใช้แทนแบบ ..... ถูกแทนโดยแบบ .....
ผู้เขียน ลมช่าย ..... ผู้สำรวจ ..... วิศวกร ..... หัวหน้าแผนก ..... ผู้อำนวยการกอง ..... ผู้อำนวยการฝ่าย	ผู้ว่าการ ..... 115 kV วงจรเดี่ยว สายไฟฟ้าเดี่ยว เสาคู่ สำหรับเข้าปลายสายสองข้าง แบบ SS-DD-4	เขียนเสร็จวันที่ 16 พ.ค. 2550 แก้แบบวันที่ ..... มิติเป็น ..... มาตราส่วน .....
รองผู้ว่าการวางแผนและพัฒนาระบบไฟฟ้า	115 kV SINGLE CIRCUIT SINGLE CONDUCTOR DOUBLE POLE, DEAD END STRUCTURE TYPE SS-DD-4	แบบเลขที่ SA1-015/50011 แผ่นที่ 5 ของจำนวน 5 แผ่น