
การประกอบเสาที่ ASSEMBLY NO. 3208

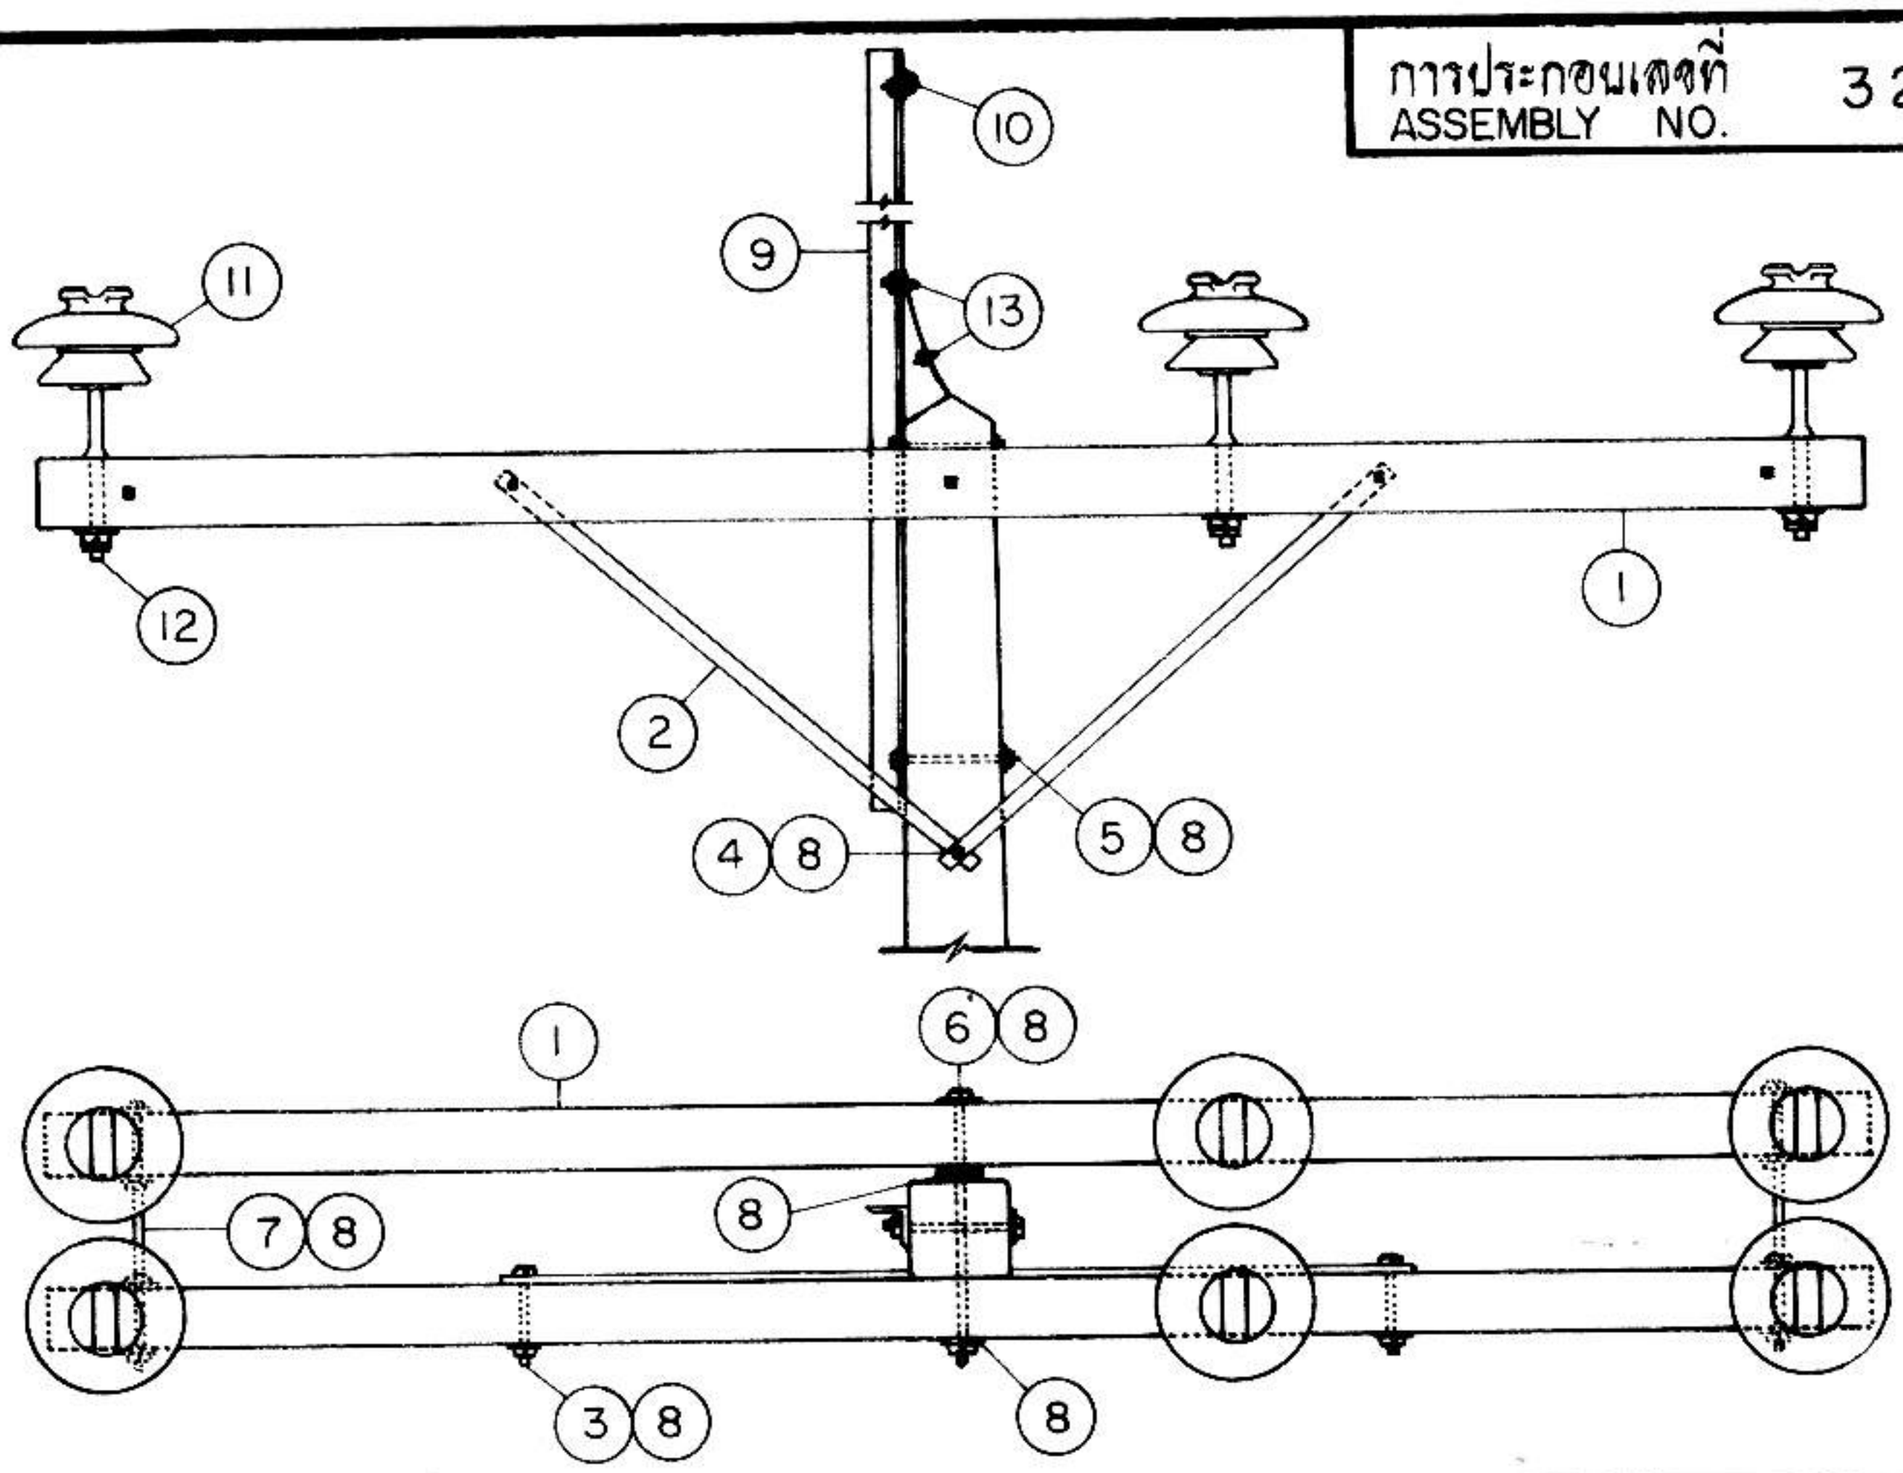

BILL OF MATERIAL

ITEM	DESCRIPTION	REQ'D	MAT. NO.
1	ไม้คอนสายขนาด 100 X120 X 3000 มม. CROSSARM (HT.) WOOD, 100 X 120 X 3000 mm	2	00100003 (0101)
2	เหล็กประกับไม้คอน 40 X 6 X 1000 มม. BRACE, FLAT, FOR CROSSARM 40 X 6 X 1000 mm	2	01200002 (0121)
3	สลักเกลียว M 16 X 130 มม. BOLT, MACHINE, M 16 X 130 mm	2	01110200 (0220)
4	สลักเกลียว M 16 X 200 มม. BOLT, MACHINE, M 16 X 200 mm	1	01110202 (0222)
5	สลักเกลียว M 16 X 250 มม. BOLT, MACHINE, M 16 X 250 mm	2	01110203 (0223)
6	สลักเกลียว M 16 X 450 มม. BOLT, MACHINE, M 16 X 450 mm	1	01110207 (0227)
7	สลักเกลียวตลอด M 16 X 450 มม. BOLT, DOUBLE ARMING, M 16 X 450 mm	2	01120001 (0244)
8	แหวนเหล็กแบนขนาด 52X52X4.5มม. ขนาดรู Ø 18 มม. มอก. 258 WASHER, SQUARE FLAT, 52X52X4.5 mm HOLE Ø 18 mm TIS 258	19	01180100 (0355)
9	เหล็กฉากรับสายล่อฟ้า OVERHEAD GROUND WIRE BAYONET	1	01010006 (0128)
10	กราวด์ไวร์แคลิ้มป์แบบ J 1152 GROUND WIRE CLAMP J 1152	1	01230205 (0296)
11	ลูกถ้วยก้านตรง 33 kV มอก. 279 แมม ค (แมม 56-3) INSULATOR, PIN TYPE, 33 kV TIS 279 TYPE C (CLASS 56-3)	6	03000002 (0409)
12	ก้านลูกถ้วยแรงสูง 33 kV PIN, INSULATOR	6	03100001 (0422)
13	ยูแคล้มป์ สลัก 1 ตัว M 8 (ไวร์ โร้ป คลิ๊ป) CLAMP, SINGLE U-BOLT M 8 (WIRE ROPE CLIP)	2	01230000 (0165)

กองวิศวกรรมเครื่องกลแผน	การไฟฟ้าส่วนภูมิภาค	ใช้แทนแบบ ถูกแทนโดยแบบ
ผู้เขียน สถาปนิก วิศวกรรู หัวหน้าแผนก ผู้อำนวยการกอง	ผู้จ่าการ	เขียนเสร็จวันที่ 16 ตค. 12 แก้แบบวันที่ 24 ก.ค. 24 มิติเป็น มม. มาตราส่วน 1:25
รองผู้จ่าการฝ่ายเทคนิค 2512	การประกอบไม้คอนคู่กับเสาคอนกรีต ระบบ 33 kV, 3 เฟส, มุม 5°-30° 33 kV, DOUBLE CROSSARM ASSEMBLY ON CONCRETE POLE, 3-PHASE, 5°-30°	แบบเลขที่ I50-015/120299 แผ่นที่ 1 ของจำนวน 1 แผ่น