


การประกอบเลขที่ ASSEMBLY NO. 3601

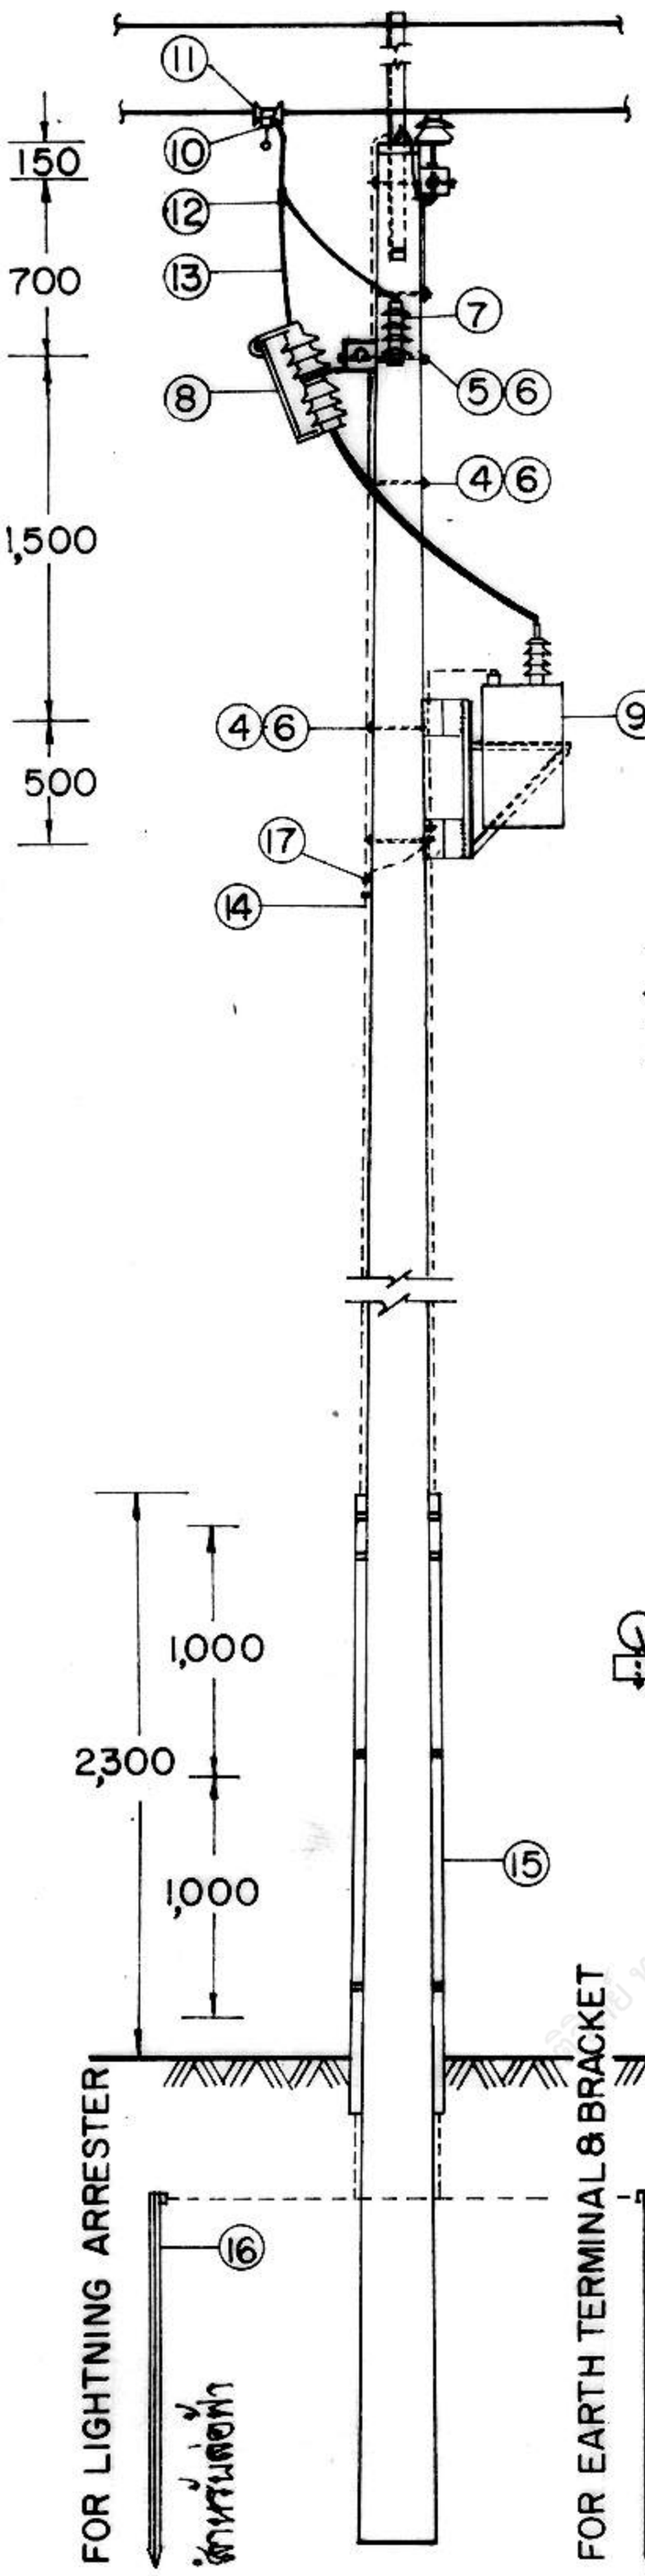


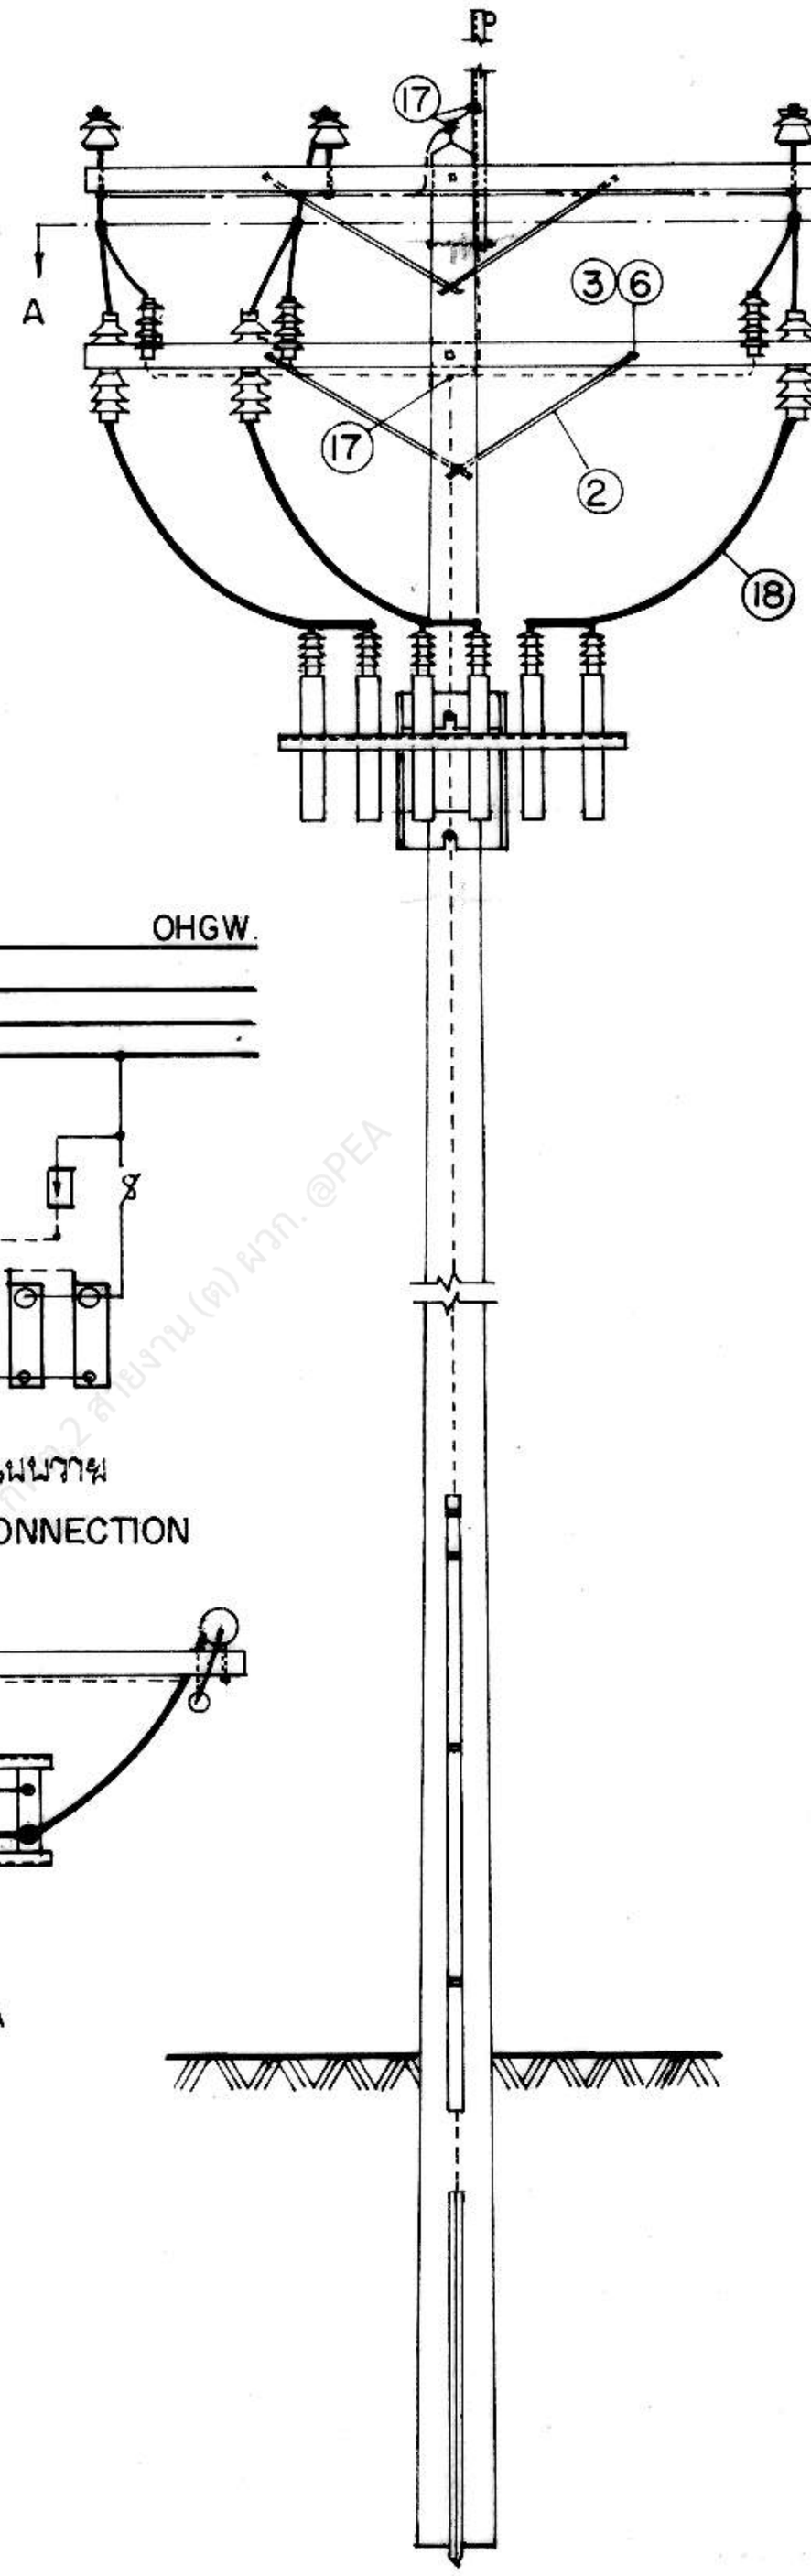

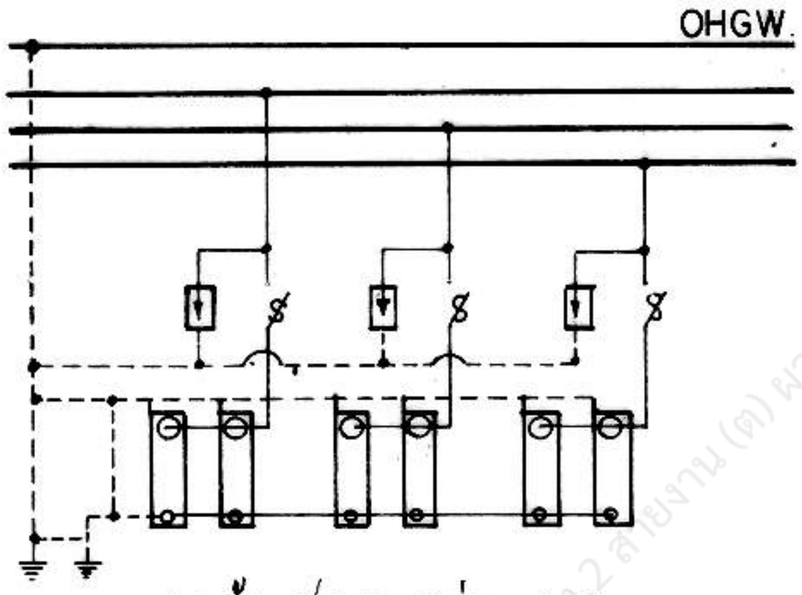

แผนผังแสดงการต่อแบบวาย

DIAGRAM OF WYE CONNECTION

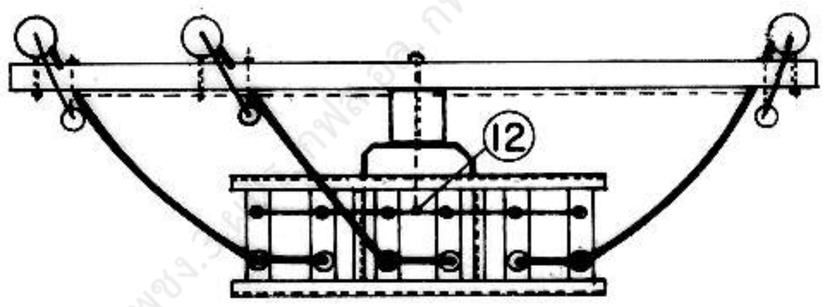



รูปตัด เอ–เอ

SECTION .A-A

กองวิศวกรรม	การไฟฟ้าส่วนภูมิภาค	ใช้แทนแบบ ถูกแทนโดยแบบ เขียนเสร็จวันที่ 18 ธค. 18 แก้แบบวันที่ 15 สค. 32 มิติเป็น มม. มาตราส่วน 1:50 แบบเลขที่ S02-015/18050 แผ่นที่ 1 ของจำนวน 3 แผ่น
ผู้เขียน ตรวจ วิศวกร หัวหน้าแผนก ผู้อำนวยการกอง	ผู้ว่าการ	
รองผู้ว่าการฝ่ายเทคนิค	การติดตั้งตะแฟซิเตอร์ 33 KV ก การต่อแบบวาย 1x6 ชุด CAPACITOR INSTALLATION 33 kV A WYE CONNECTION 1x6 SETS	

การประกอบเลขที่ ASSEMBLY NO. 3601

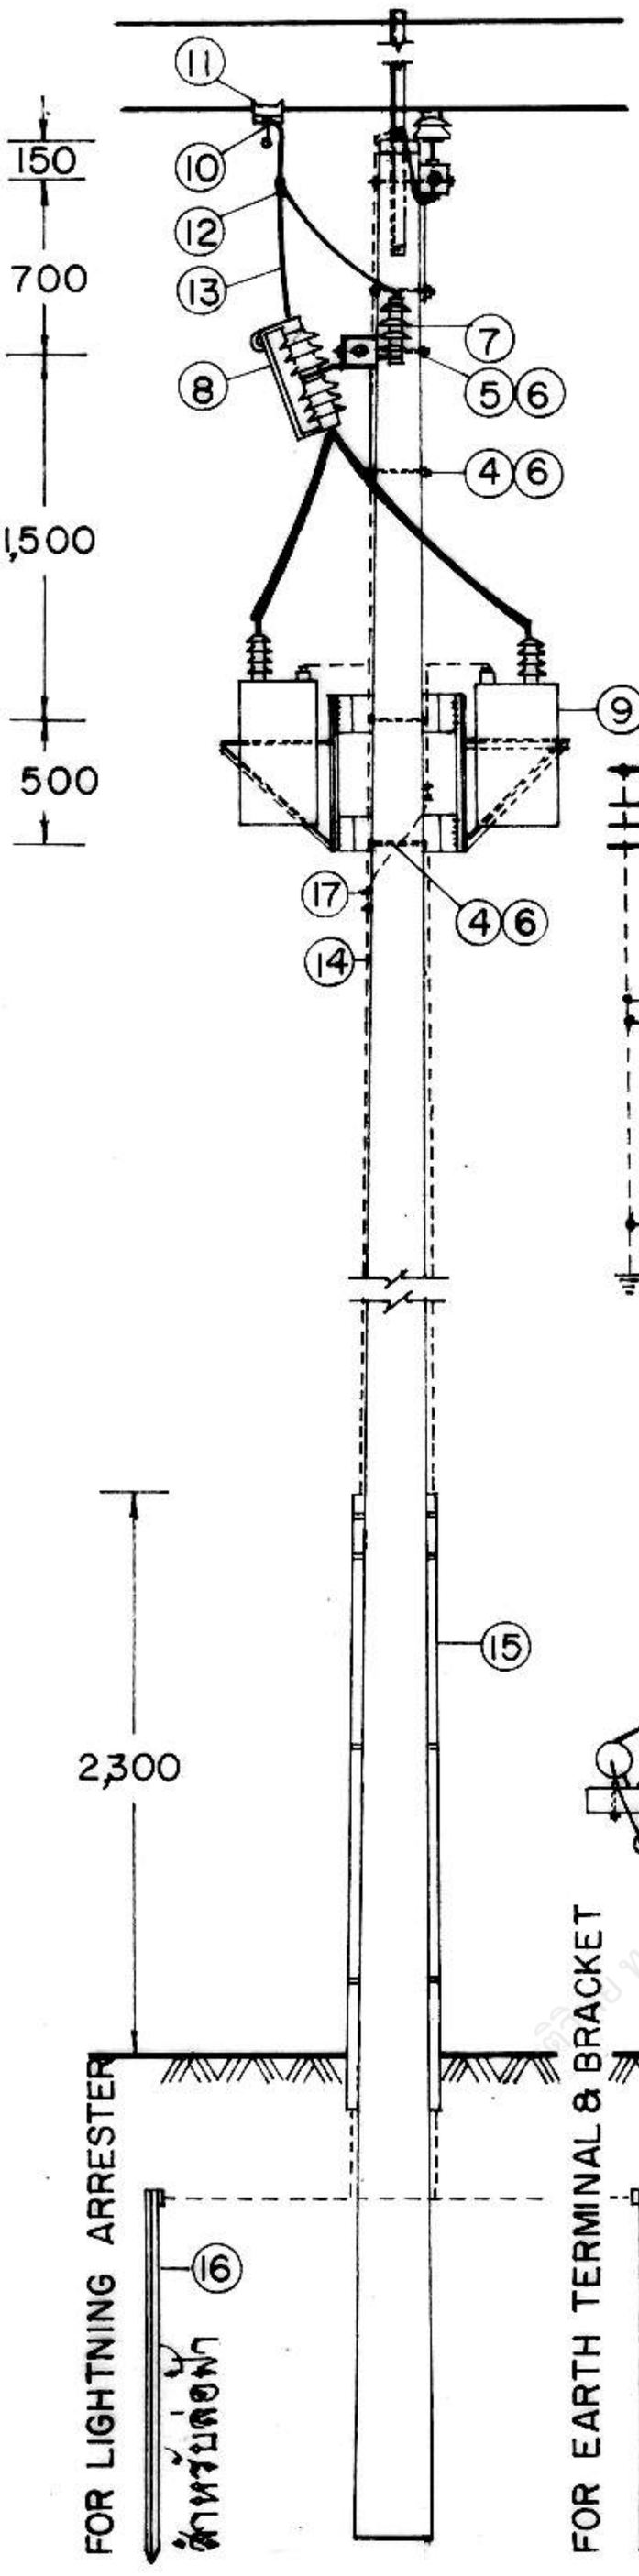

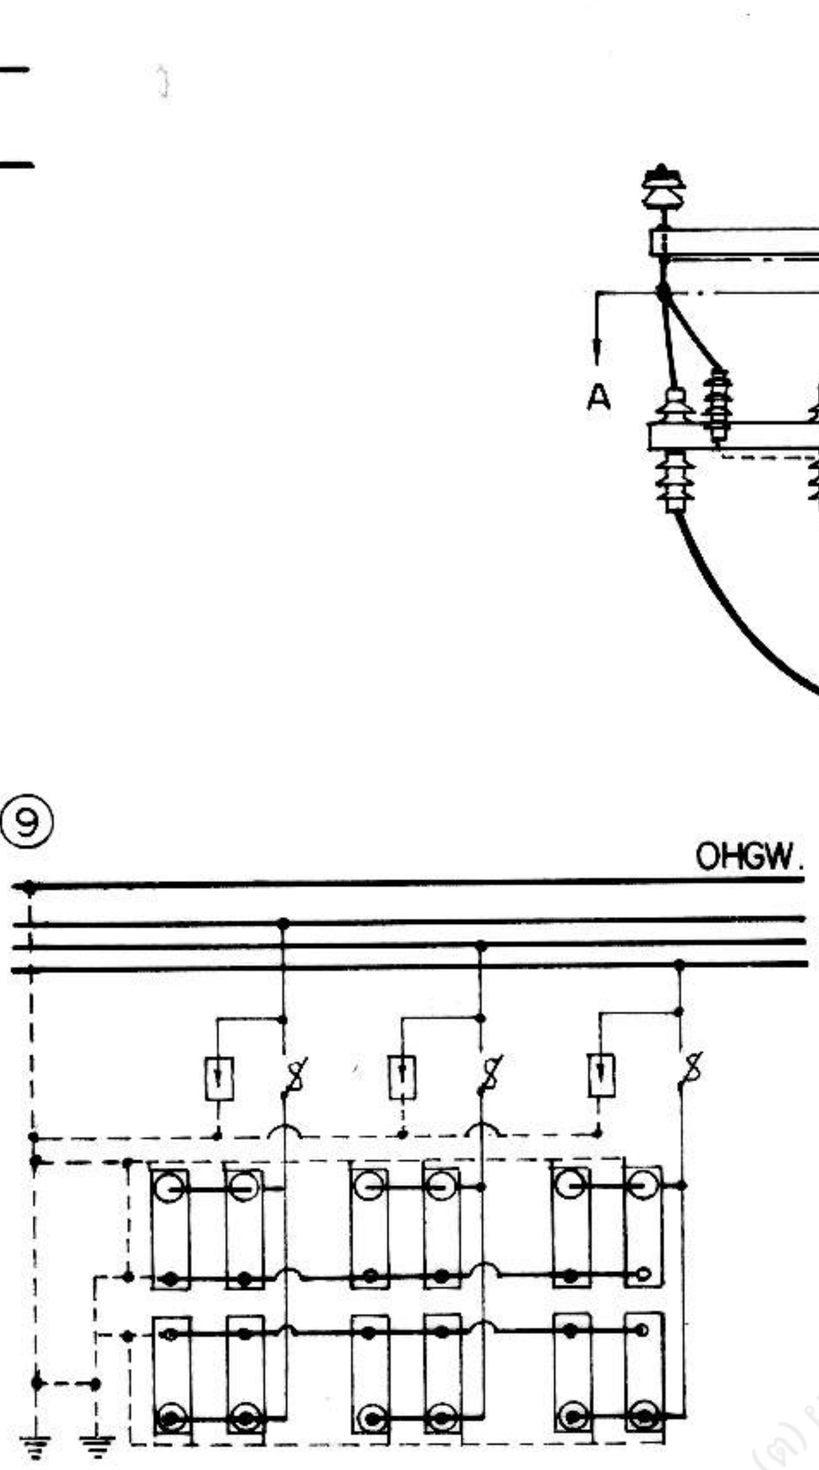


แผนผังแสดงการต่อแบบวาย

DIAGRAM OF WYE CONNECTION

รูปตัด เอ-เอ

SECTION A-A

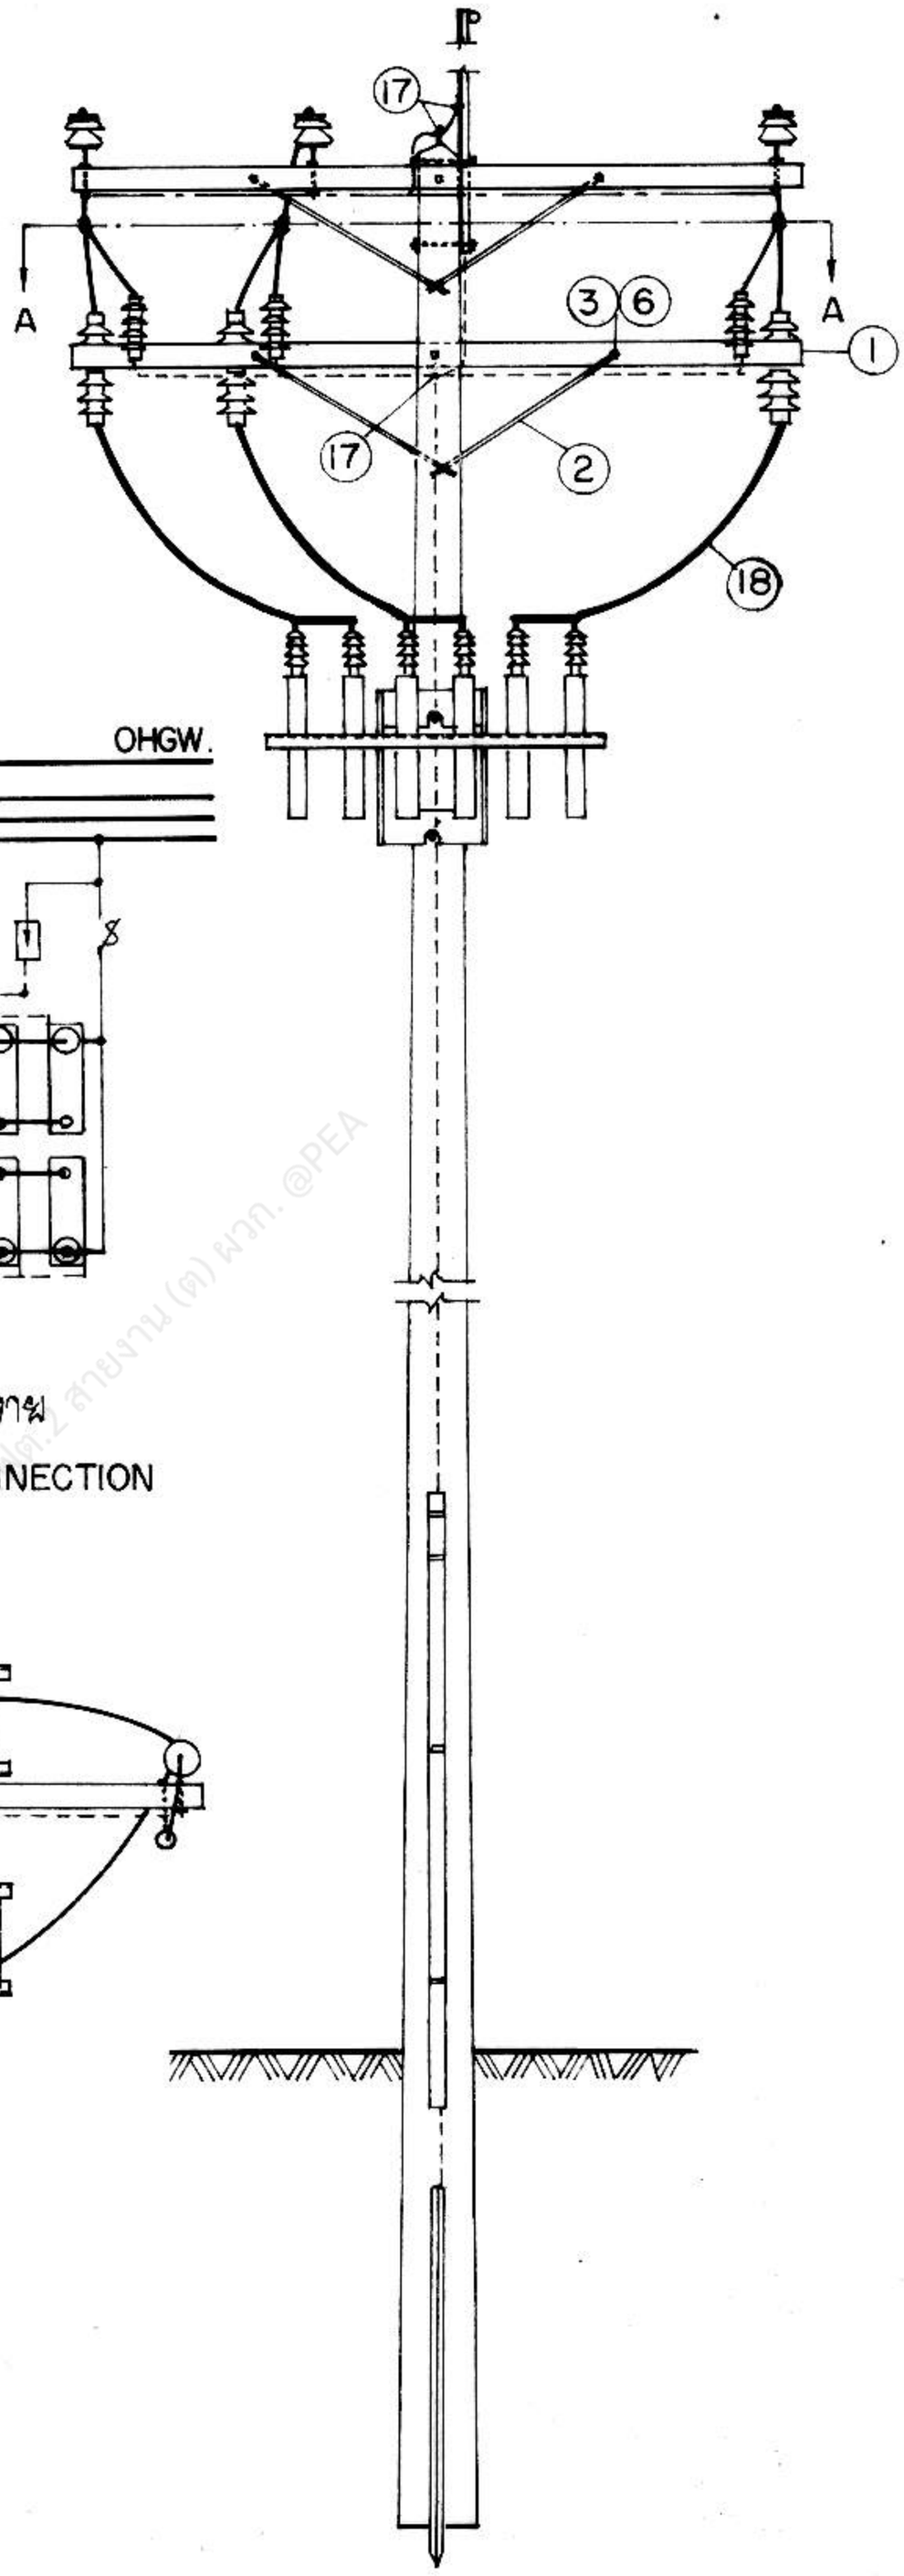

กองวิศวกรรม	การไฟฟ้าส่วนภูมิภาค	ใช้แทนแบบ .....
ผู้เขียน	ผู้ว่าการ	ถูกแทนโดยแบบ .....
ศิลปนิก		เขียนเสร็จวันที่ 18 ธ.ค. 18
วิศวกร วรพงษ์	การติดตั้งล่อฟ้าแรงสูง 33 kV	แก้แบบวันที่ 15 ส.ค. 32
หัวหน้าแผนก	ๆ การต่อแบบวาย 2 x 6 ชุด	มิติเป็น มม.
ผู้อำนวยการกอง	CAPACITOR INSTALLATION 33 kV	มาตราส่วน 1 : 50
รองผู้ว่าการฝ่ายเทคนิค	B WYE CONNECTION 2 x 6 SETS	แบบเลขที่ S02-015/18050
		แผ่นที่ 2 ของจำนวน 3 แผ่น

การประกอบเลขที่ ASSEMBLY NO. 3601

บัญชีวัสดุ
BILL OF MATERIAL

ลำดับที่ ITEM	รายละเอียด DESCRIPTION	จำนวน REQ'D 1 ชุด	2 ชุด	วัสดุเลขที่ MAT. NO
1	คอน คอร. สปัน ขนาด 120 X 120 X 3,000 มม. CROSSARM, SPUN, PRESTRESSED CONCRETE 120 X 120 X 3,000 mm	1	1	00110002
2	เหล็กประกับไม้คอน 40 X 6 X 1000 มม. BRACE, FLAT, FOR CROSSARM 40X6X1000 mm	2	2	01200002
3	สลักเกลียว M 16 X170 มม. BOLT, MACHINE, M 16 X170 mm	2	2	01110201
4	สลักเกลียว M 16 X250 มม. BOLT, MACHINE, M 16 X250 mm	3	3	01110203
5	สลักเกลียว M 16 X350 มม. BOLT, MACHINE, M 16 X350 mm	1	1	01110205
6	แหวนสี่เหลี่ยมแบน 52X52X4.5มม. รู Ø 18 มม. มอก. 258 WASHER, SQUARE, FLAT 52X52X4.5mm HOLE Ø 18 mm TIS 258	9	9	01180100
7	ล่อฟ้าแรงสูง 30 kV 5 กิโลแอมป์ LIGHTNING ARRESTER, 30 kV, 5 kA	3	3	04000100
8	ครอพเอาท์ ฟิวส์คัตเอาท์ หนึ่งอินซูเลเตอร์ 33 kV 100 แอมป์ CUT-OUT, FUSE, OPEN TYPE, SINGLE INSULATOR, DROP-OUT 33 kV, 100 A	3	3	04010100
9	คะแปซิเตอร์หนึ่งเฟสใช้นอกอาคาร 33 kV 100 กิโลวาร์พร้อมอุปกรณ์ประกอบรับ CAPACITOR, POWER, 1 PHASE, OUT-DOOR 33 kV 100 kVAR, COMP. WITH BRACKET	1X6	2X6	05050100 05110001
10	ฮอทไลน์แคล้มป์สำหรับสายเมนอะลูมิเนียม 25-120 ต.มม. CLAMP, HOT LINE, MAIN LINE Al. 25-120 mm^2	3	3	02330100 or 02330101
11	สเตอร์รัพแคล้มป์ หรือ เบลแคล้มป์ฮอทไลน์สำหรับสายเมนอะลูมิเนียม 25-185 mm^2 ต.มม. CLAMP, STIRRUP OR BAIL, HOTLINE, MAIN LINE Al 25-185 mm^2	3	3	02330000 or 02330001
12	พี.จี. คอนเนคเตอร์ สลักคู่ สำหรับสายอะลูมิเนียม 16-70 ต.มม. CONNECTOR, PARALLEL GROOVE, DOUBLE BOLTS, Al. 16-70 mm^2	4	8	02300101
13	สายอะลูมิเนียมเปลือย 35 ต.มม. มอก. 85 CONDUCTOR, 35 mm^2, TIS 85	5 ม. m	5 ม. m	02010001
14	ลวดเหล็กตีเกลียว 50/7 ต.มม. มอก. 404 STEEL, STRANDED WIRE 50/7 mm^2 TIS 404	24 ม. m	25 ม. m	01100004
15	ท่อ PVC แข็ง ขนาด Ø 20 X 2,500-4,000 มม. พร้อมอุปกรณ์ยึด CONDUIT, PVC RIGID, Ø 20 X 2,500-4,000 mm ; COMP. WITH FIXING ACCESS.	2	2	08040002 or 08040001
16	หลักดิน 60X60X5 มม. ยาว 2000 มม. GROUND ROD, 60X60X5 mm, 2000 mm LONG	2	2	01220002
17	ยูแคล้มป์ สลัก 1 ตัว M 8 (ไวร์ โร้ป คลิ๊ป) CLAMP, SINGLE U-BOLT M 8 (WIRE ROPE CLIP)	8	8	01230000
18	สายทองแดง หรืออะลูมิเนียมหุ้มฉนวน พีวีซี. 750 โวลต์ ขนาด 35-50 ต.มม. มอก.11 หรือ 293 CABLE, Cu OR AL, PVC INSULATED, 750 V, SIZE 35-50 mm^2 TIS 11 OR 293	7 ม. m	14 ม. m	— or 02070001 02070002

หมายเหตุ การติดตั้งคะแปซิเตอร์ แบบ 1X3 หรือ 2X3 ชุด ให้ยึดโยงตามแบบนี้

NOTE CAPACITOR INSTALLATION 1X3 OR 2X3 SETS SHALL BE INSTALLED ACCORDING TO THE ABOVE DRAWING

กองวิศวกรรม	การไฟฟ้าส่วนภูมิภาค	ใช้แทนแบบ
ผู้เขียน	ผู้ว่าการ 29 ธ.ค. 18	ถูกแทนโดยแบบ
สถาปนิก		เขียนเสร็จวันที่ 18 ธค. 18
วิศวกร	การติดตั้งคะแปซิเตอร์ 33 kV	แก้แบบวันที่ 15 ธค. 32
หัวหน้าแผนก	ค บัญชีวัสดุสำหรับติดตั้งทั่วไป	มิติเป็น
ผู้อำนวยการกอง		มาตราส่วน
รองผู้ว่าการฝ่ายเทคนิค	CAPACITOR INSTALLATION 33 kV C BILL OF MATERIAL	แบบเลขที่ S02-015/18050 แผ่นที่ 3 ของจำพวน 3 แผ่น