
การประกอบเลขที่ 5201
ASSEMBLY NO.

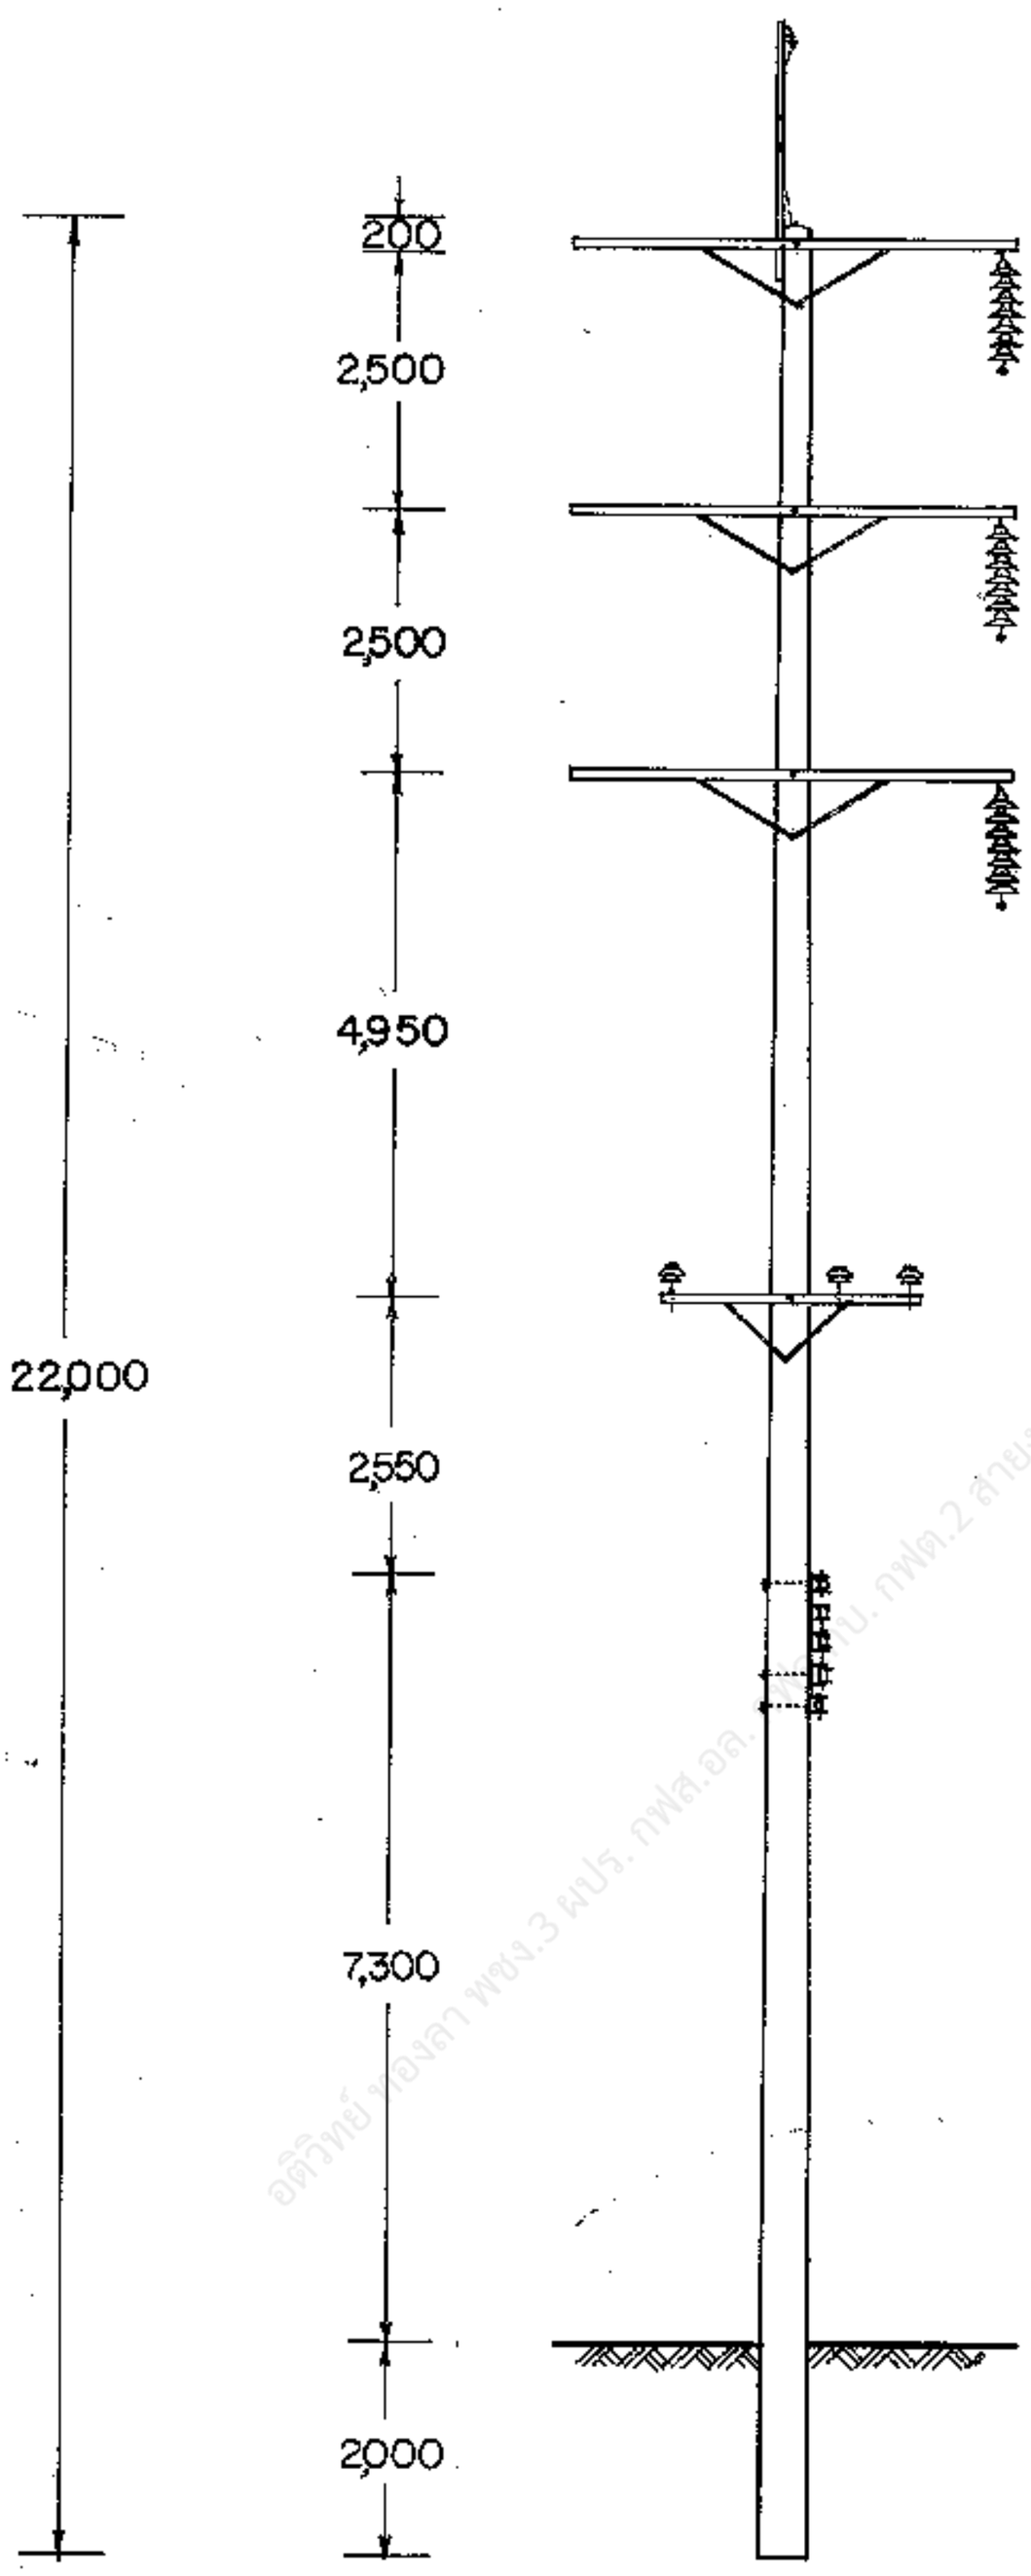


แบบ
TYPE SS - TG - 1

JAPANESE EXPERT TO PEA.

กองวิศวกรรม	การไฟฟ้าส่วนภูมิภาค	ใช้แทนแบบ.....
ผู้เขียน	ผู้ว่าการ	ถูกแทนโดยแบบ.....
ตำแหน่ง		เขียนเสร็จวันที่ 17 มี.ค. 19
วิศวกร	แผนโครงสร้างเสาสายระบบ 115 kV	แก้แบบวันที่ 24 มี.ค. 23
หัวหน้าแผนก	วงจรเดี่ยว	มิติเป็น ม.ม.
ผู้อำนวยการกอง	แบบเสาสำหรับทางตรง	มาตราส่วน 1:125
รองผู้ว่าการฝ่ายเทคนิค	115 kV LINE STRUCTURE CONSTRUCTION SINGLE CIRCUIT TANGENT STRUCTURE	แบบเลขที่ S02 - 015/19020 แผ่นที่ 1 ของจำนวน 3 แผ่น

ASSEMBLY NO. 5201

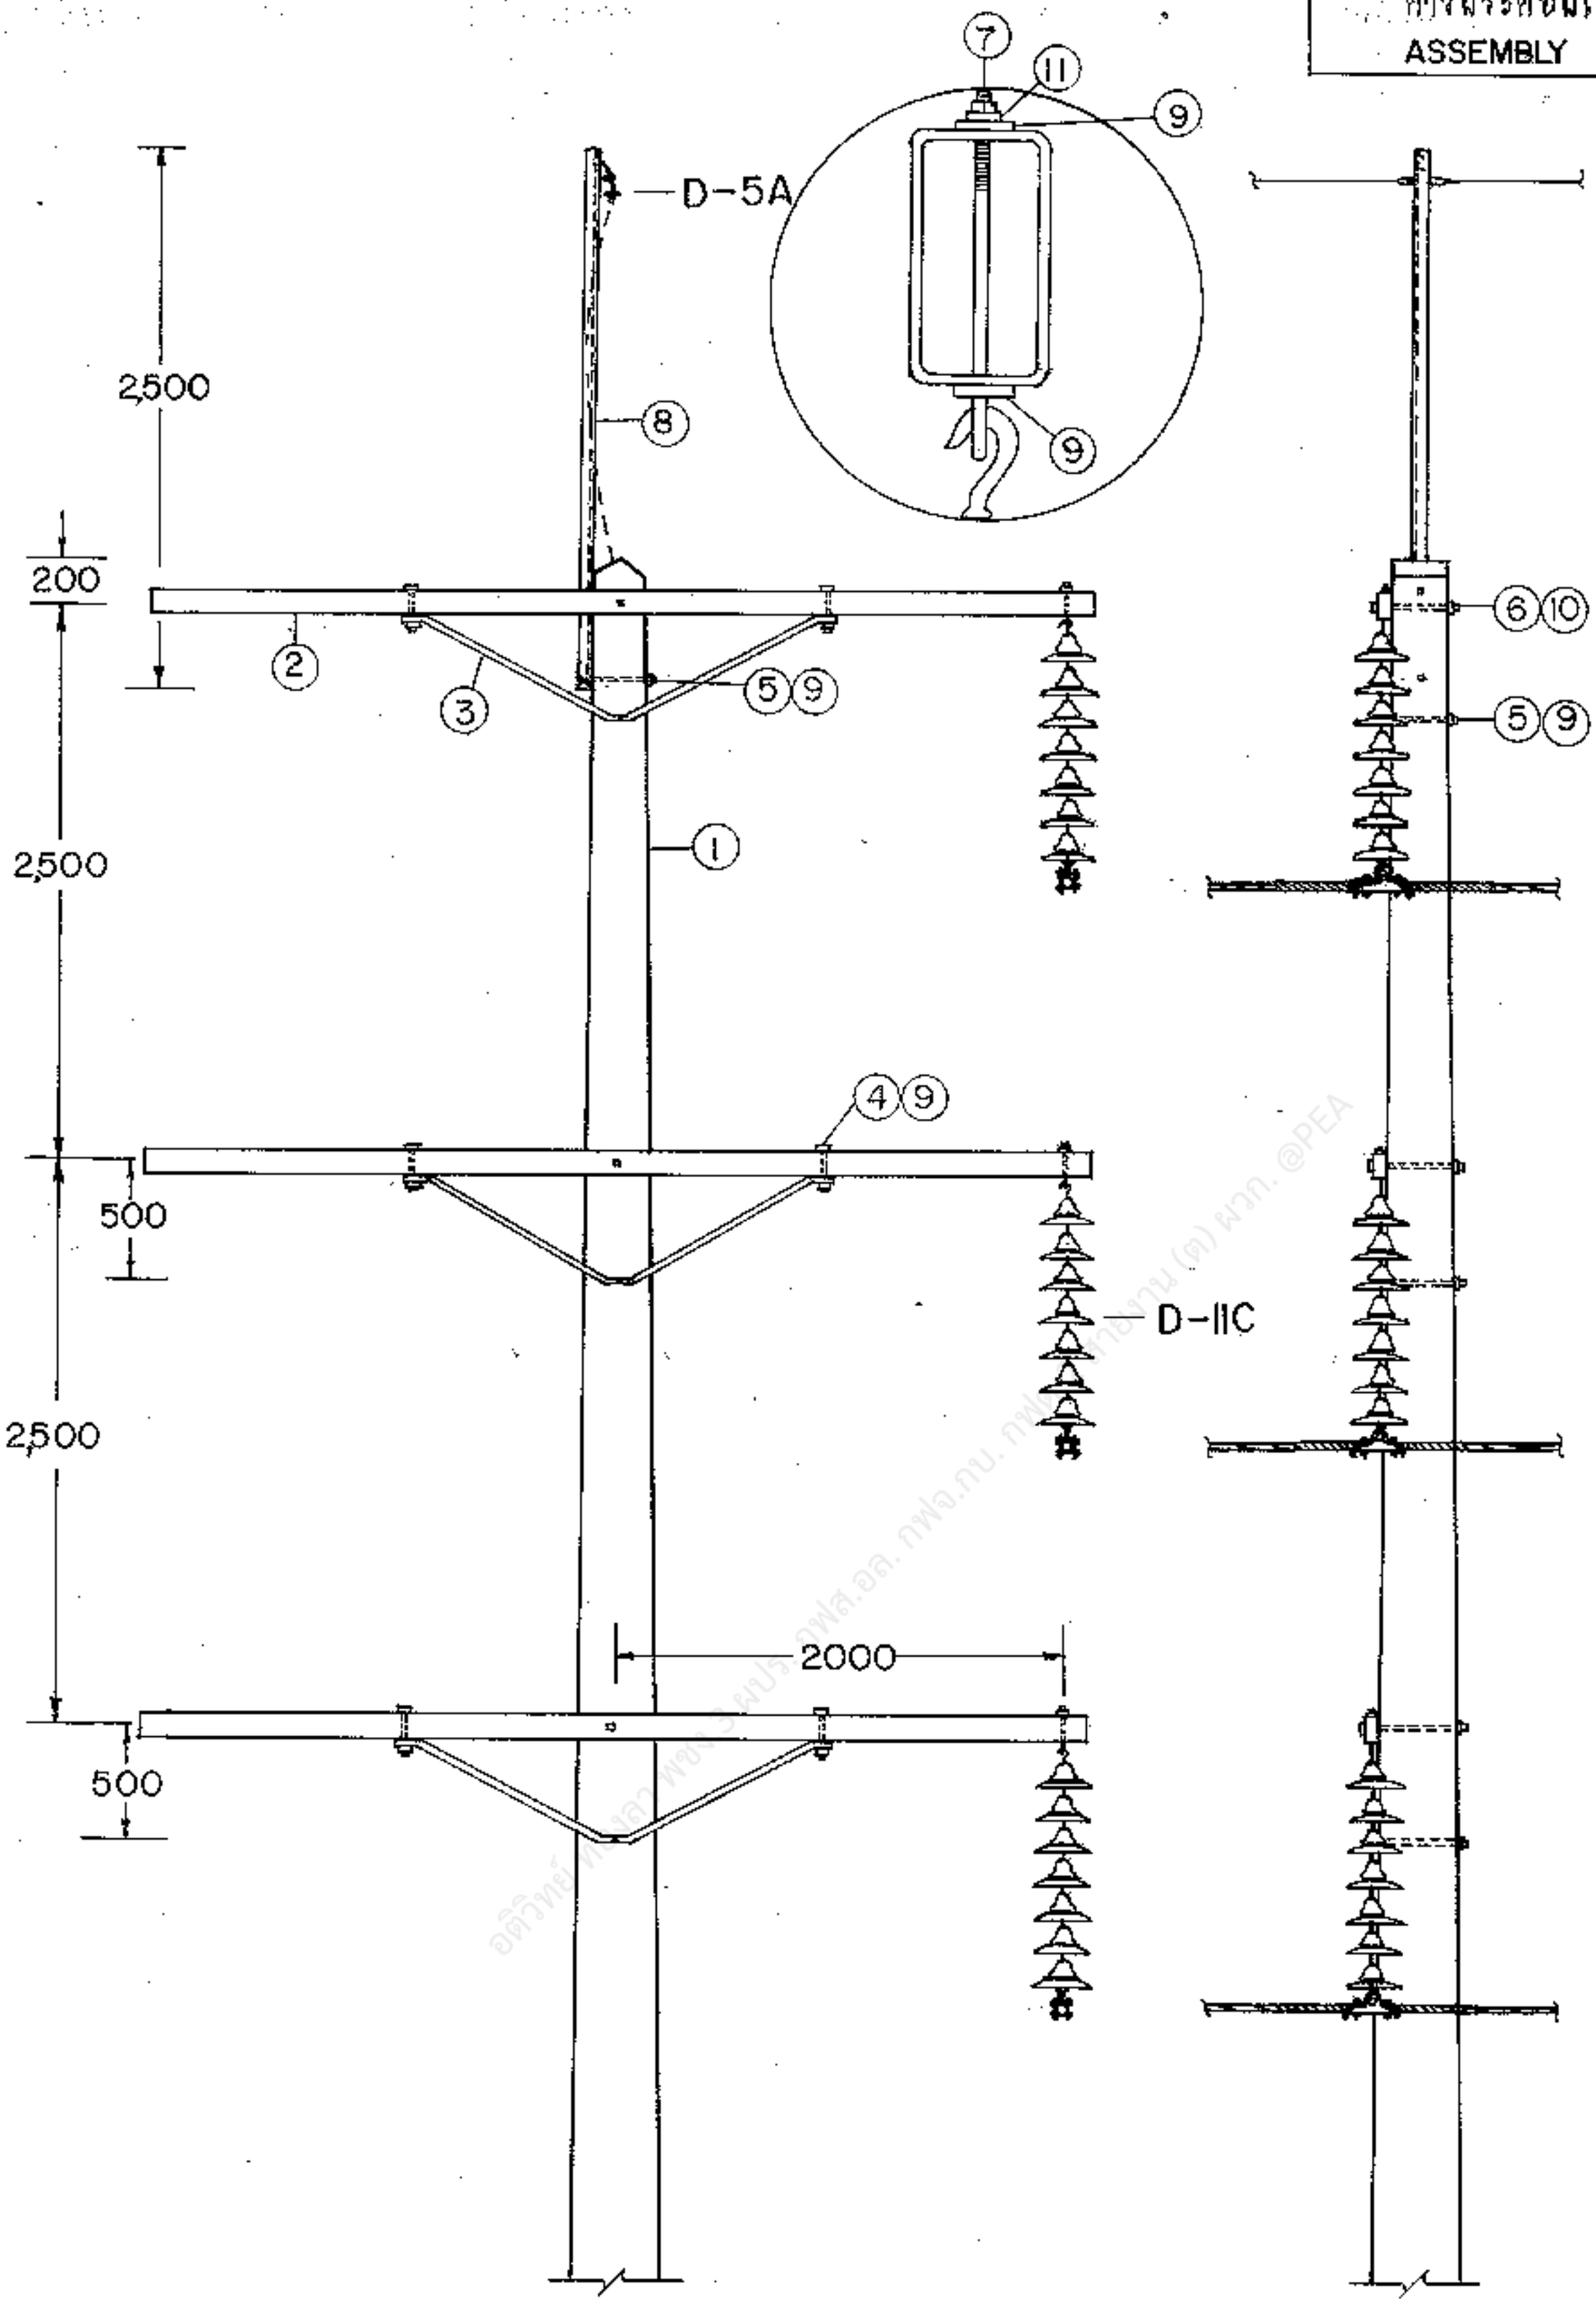

JAPANESE EXPERT TO PEA. J. Yamada

กองวิศวกรรม	การไฟฟ้าส่วนภูมิภาค	ใช้แทนแบบ .....
ผู้เขียน	ผู้ว่าการ	ถูกแทนโดยแบบ .....
สังกัด		เขียนเสร็จวันที่ 17 มีค. 19
วิศวกร	แนวโครงสร้างเสาสายส่งระบบ 115 KV	แก้แบบวันที่ 24 มีค. 23
หัวหน้าแผนก	จังหวัดเชียงใหม่	มิติเป็น ม.ม.
ผู้อำนวยการกอง	แบบเสาสำหรับทางตรง	มาตราส่วน 1:50
รองผู้ว่าการฝ่ายเทคนิค	115 kV LINE STRUCTURE CONSTRUCTION SINGLE CIRCUIT TANGENT STRUCTURE	แบบเลขที่ S02-015/19020 แผ่นที่ 2 ของจำนวน 3 แผ่น

การประกอบเลขที่ ASSEMBLY NO. 5201

บัญชีวัสดุ
BILL OF MATERIAL

ลำดับที่ ITEM	รายละเอียด DESCRIPTION	จำนวน REQ'D	วัสดุเลขที่ MAT. NO.
1	เสาคอนกรีต 22 ม. POLE, CONCRETE 22 m. LONG	1	00010011 (0041)
2	คอนสายแนนเหล็กขนาด 100 x 50 x3.2 มม. ยาว 4.20 ม. CROSSARM, STEEL 100 x 50 x3.2 mm. 4.20 m LONG	3	00120001 (0116)
3	เหล็กฉากรับคอนสายขนาด 50x 50x 6 มม.ช่วงกว้าง 1800 มม.ความลึก 450 มม. BRACE, ANGLE STEEL, 50x 50x 6 mm. 1800mm WIDE 450 mm DROP	3	00120007 (1119)
4	สลักเกลียว M 16 x 130 มม. BOLT, MACHINE, M 16 x 130 mm.	6	01110200 (0220) *
5	สลักเกลียว M 16 x 350 มม. BOLT, MACHINE M 16 x 350 mm.	5	01110206 (0225)
6	สลักเกลียว M 20x 400 มม. BOLT, MACHINE M 20x 400 mm.	3	01110301 (0233)
7	สลักห่วงโอเวล M 16 x 150 มม. BOLT, OVAL EYE M 16 x 150 mm.	3	01150000 (0257)
8	เหล็กฉากรับสายล่อฟ้าทางตรง ยาว 2.50 ม. OVERHEAD GROUND WIRE BAYONET 2.50 m. LONG	1	01010004 (0135)
9	แหวนสี่เหลี่ยมแบน 52 x 52x4.5มม. รู Ø 18 มม. มอก. 258 WASHER, SQUARE FLAT 52 x 52 x4.5 mm HOLE Ø 18 mm TIS. 258	17	01180100 (0355)
10	แหวนสี่เหลี่ยมแบน 62 X 62 X 6 มม. รู Ø 22 มม. มอก. 258 WASHER, SQUARE FLAT 62 X 62 X 6 mm HOLE Ø 22 mm TIS 258	6	01180101 (0356)
11	แหวนสปริง M 16 มอก. 259 WASHER, LOCK M 16 TIS 259	3	01180301 (0365)
	รายละเอียด DETAIL		
D-11C	การประกอบลูกถ้วยแขวน SUSPENSION INSULATOR ASSEMBLY	3	
D-5A	การต่อสายล่อฟ้า OVERHEAD GROUND WIRE CONNECTION	1	
D-10A	ฐานรากเสา POLE FOUNDATION	1	

JAPANESE EXPERT TO PEA. K. Yamada

กองวิศวกรรม	การไฟฟ้าส่วนภูมิภาค	ใช้แทนแบบ.....
ผู้เขียน.....	ผู้ว่าการ.....	ถูกแทนโดยแบบ.....
สถาปนิก.....	แบบโครงสร้างเสาสังระนาบ 115 kV	เขียนเสร็จวันที่ 17 มีค. 19
วิศวกร.....	วงจรเดี่ยว	แก้แบบวันที่ 24 มีค. 23
หัวหน้าแผนก.....	แบบเสาสำหรับทางตรง	มิติเป็น.....
ผู้อำนวยการกอง.....	115 kV LINE STRUCTURE CONSTRUCTION	มาตราส่วน.....
รองผู้ว่าการฝ่ายเทคนิค	SINGLE CIRCUIT	แบบเลขที่ S02-015/19020
.....	TANGENT STRUCTURE	แผ่นที่ 3 ของจำนวน 3 แผ่น