
การประกอบเลขที่ ASSEMBLY NO. 3908

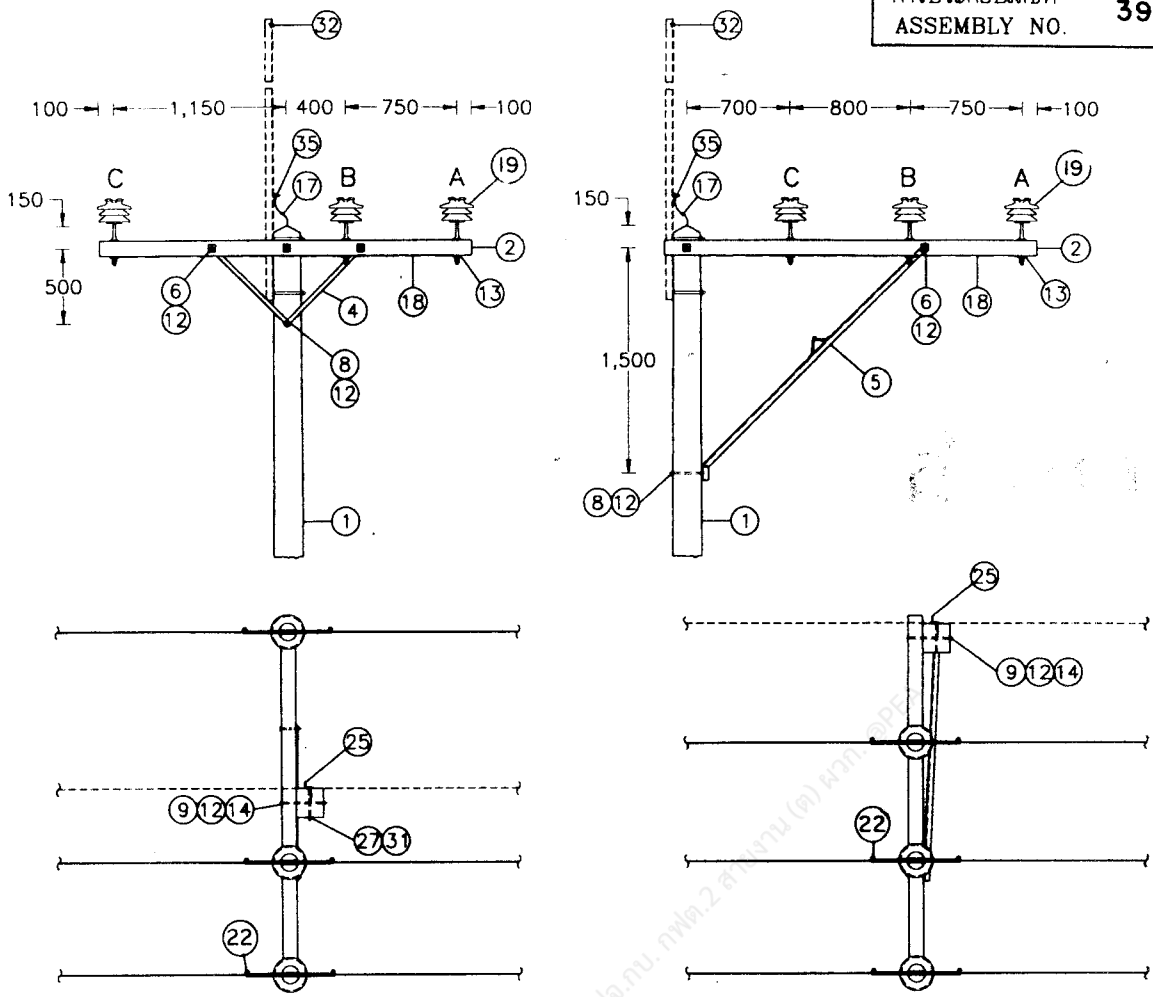


I สำหรับทางตรง FOR LINE ANGLE 0°-5°


II สำหรับทางโค้ง FOR LINE ANGLE 5°-30° (θ°)

กองวิศวกรรมไฟฟ้าและเครื่องกล ฝ่ายวิศวกรรม	การไฟฟ้าส่วนภูมิภาค	ใช้แทนแบบ ..... ถูกแทนโดยแบบ .....
ผู้เขียน B Suphakit ผู้สำรวจ ..... วิศวกร ..... หัวหน้าแผนก ..... ผู้อำนวยการกอง ..... ผู้อำนวยการฝ่าย	ผู้ว่าการ	เขียนเสร็จวันที่ 27 มี.ค. 40. แก้แบบวันที่ .....
	การประกอบคอนกับสาคอนกรีต 33 kV 1 วงจร (กรณีพาดสายหุ้มฉนวนแบบไม่เต็มพิกัด (PIC))	มิติเป็น มิลลิเมตร มาตราส่วน 1 : 50
รองผู้ว่าการ	33 kV CROSSARM ASSEMBLY ON CONCRETE POLE, 1 CIRCUIT (PARTIALLY INSULATED CONDUCTOR STRINGING)	แบบเลขที่ SA4-015/40007 แผ่นที่ 1 ของจำนวน 6 แผ่น

การประกอบเลขที่ ASSEMBLY NO. 3908

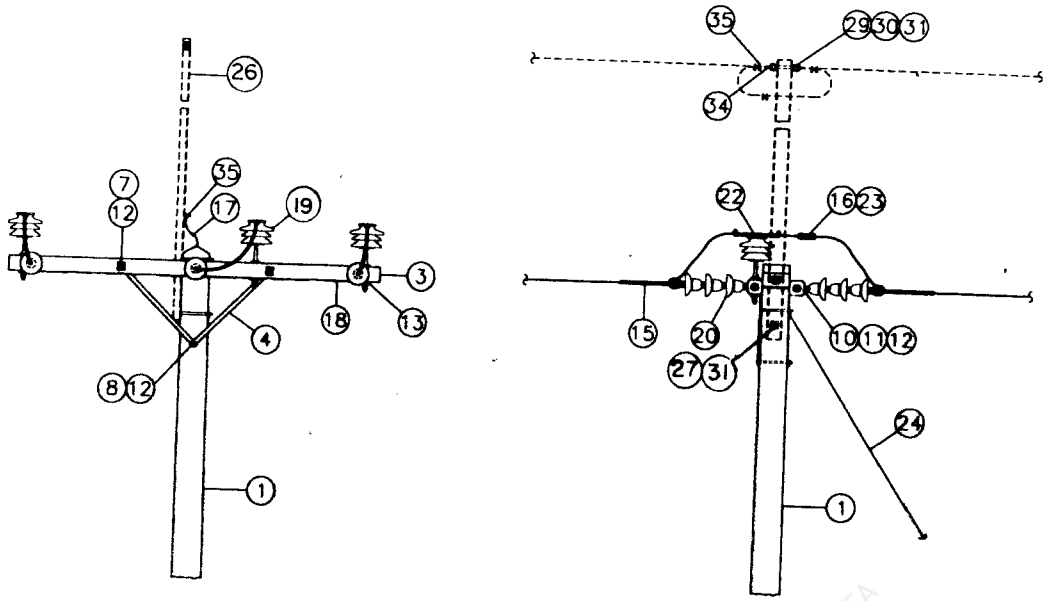

III สำหรับเข้าปลายสายสองข้าง
FOR DOUBLE DEADEND

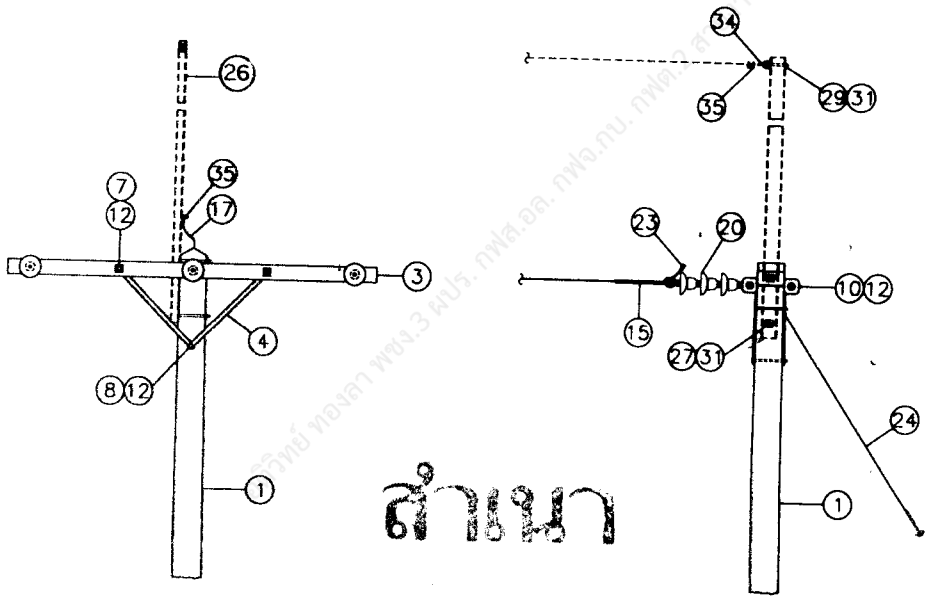


สำเนา

IV สำหรับเข้าปลายสาย
FOR DEADEND

กองวิศวกรรมไฟฟ้าและเครื่องกล ฝ่ายวิศวกรรม	การไฟฟ้าส่วนภูมิภาค	ใช้ทนแบบ ..... ถูกแทนโดยแบบ .....
ผู้เขียน B. Sipphakit ผู้สำรวจ ..... วิศวกร ..... หัวหน้าแผนก ..... ผู้อำนวยการกอง ..... ผู้อำนวยการฝ่าย	ผู้ว่าการ ..... 11 เม.ย 2540 การประกอบคอนกับเสาคอนกรีต 33 kV 1 วงจร (การโพดสายหุ้มฉนวนแบบไม่เต็มพิกัด (PIC))	เขียนเสร็จวันที่ 27 มี.ค.40 แก้แบบวันที่ ..... มิติเป็น มิลลิเมตร มาตราส่วน 1 : 50
รองผู้ว่าการ	33 kV CROSSARM ASSEMBLY ON CONCRETE POLE, 1 CIRCUIT (PARTIALLY INSULATED CONDUCTOR STRINGING)	แบบเลขที่ SA4-015/40007 แผ่นที่ 2 ของจำนวน 6 แผ่น

การประกอบเลขที่ ASSEMBLY NO. 3908

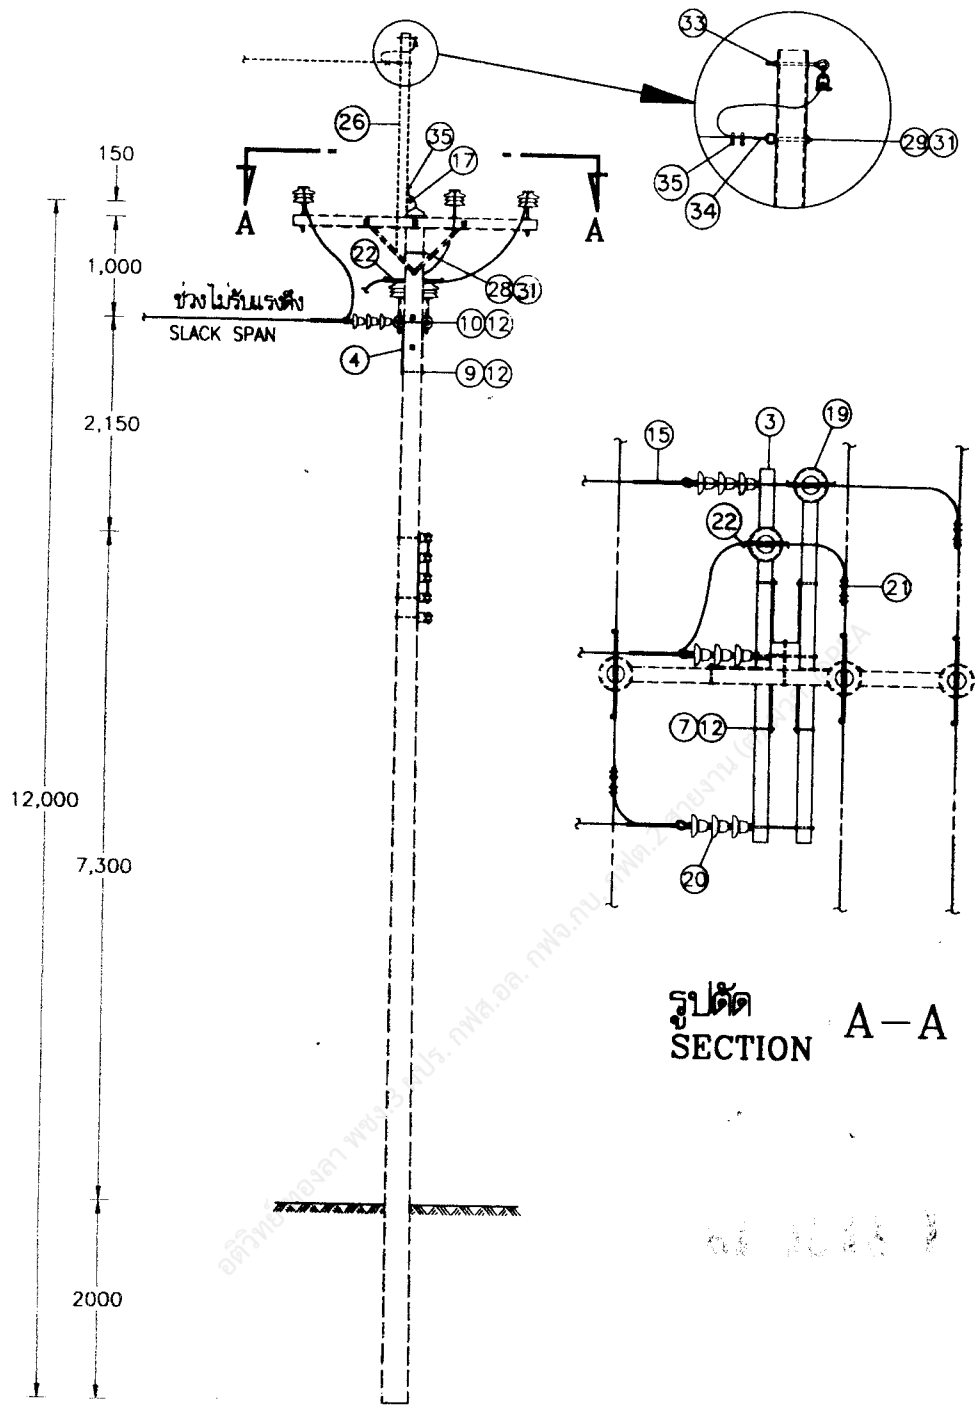


รูปตัด SECTION A–A

V สำหรับต่อแยกสาย FOR TAP LINE

กองวิศวกรรมไฟฟ้าและเครื่องกล ฝ่ายวิศวกรรม	การไฟฟ้าส่วนภูมิภาค	ใช้แทนแบบ ..... ถูกแทนโดยแบบ .....
ผู้เขียน ..... ผู้สำรวจ ..... วิศวกร ..... หัวหน้าแผนก ..... ผู้อำนวยการกอง ..... ผู้อำนวยการฝ่าย	ผู้ว่าการ	เขียนเสร็จวันที่ 27 มี.ค. 40 แก้แบบวันที่ ..... มิติเป็น มิลลิเมตร มาตราส่วน 1:50, 1:75
รองผู้ว่าการ	การประกอบตอนกันสาคอนกรีต 33 kV 1 วงจร (กรณีพาดสายหุ้มฉนวนแบบไม่เต็มที่ตัด (PIC))	
	33 kV CROSSARM ASSEMBLY ON CONCRETE POLE, 1 CIRCUIT (PARTIALLY INSULATED CONDUCTOR STRINGING)	แบบเลขที่ SA4-015/40007 แผ่นที่ 3 ของจำนวน 6 แผ่น

การประกอบเลขที่ ASSEMBLY NO. 3908

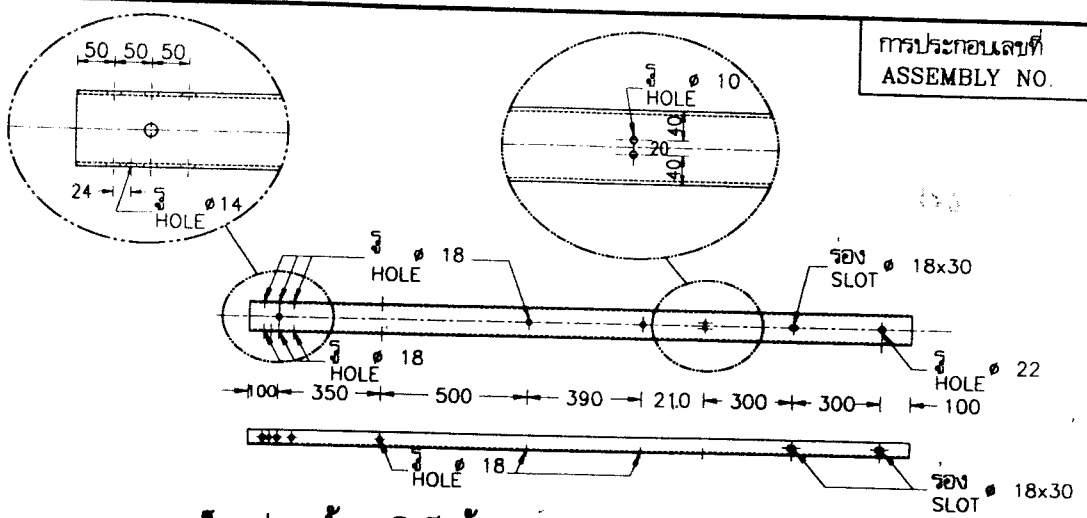

เหล็กรูปรางน้ำ ชนิดรีดร้อน ขนาด 100x50x5 มม. ยาว 2,250 มม. มอก. 1227 (วัสดุเลขที่ 01000100)

(26) STEEL, CHANNEL, 100X50X5 mm, 2,250 mm LONG TIS 1227 (MAT. NO. 01000100)

บัญชีวัสดุ
BILL OF MATERIAL

ลำดับที่ ITEM	รายละเอียด DESCRIPTION	จำนวน REQ'D I	I*	II	II*	III	IV	V	วัสดุเลขที่ MAT. NO.
1	เสาคอนกรีต 12 เมตร POLE, CONCRETE, 12 m LONG	1	1	1	1	1	1	–	00010004
2	คอน, คอนกรีตอัดแรง (คอร.) แบบสปันแรงสูง 100x100x2,500 มม. CROSSARM, PRESTRESSED CONCRETE, SPUN, H.T. 100x100x2,500 mm	1	1	1	1	–	–	–	00110001
3	คอน คอนกรีตอัดแรง (คอร.) แบบสปัน (สำหรับเข้าปลายสาย) 120x120x2,500 มม. CROSSARM, PRESTRESSED CONCRETE, SPUN (FOR DEAD-ENDING) 120x120x2,500 mm	–	–	–	–	2	2	2	00110004
4	เหล็กประกับไม้คอน ขนาด 30x6 มม. ยาว 760 มม. BRACE, FLAT, FOR CROSSARM 30x6x760 mm	2	–	2	–	2	4	4	01200001
5	เหล็กประกับไม้คอน แบบท้าวแขน ขนาด 40x40x5 มม. ยาว 2,120 มม. BRACE, ALLEY ARM 40x40x5 mm 2,120 LONG	–	1	–	1	–	–	–	01200004
6	สลักเกลียว M 16x130 มม. BOLT, MACHINE M 16x130 mm	2	1	2	1	–	–	–	01110200
7	สลักเกลียว M 16x170 มม. BOLT, MACHINE M 16x170 mm	–	–	–	–	2	4	4	01110201
8	สลักเกลียว M 16x250 มม. BOLT, MACHINE M 16x250 mm	1	1	1	1	1	1	–	01110203
9	สลักเกลียว M 16x300 มม. BOLT, MACHINE M 16x300 mm	1	1	1	1	–	–	1	01110204
10	สลักเกลียวห่วงกลม M 16x500 มม. BOLT, DOUBLE ARMING, ROUND EYE, M 16x500 mm	–	–	–	–	3	3	3	01130002
11	นัทรูปห่วง M 16 ดิน 582 NUT, EYE, M 16, DIN 582	–	–	–	–	3	–	–	01180001

กองวิศวกรรมไฟฟ้าและเครื่องกล
ฝ่ายวิศวกรรม

ผู้เขียน B Suppakit
ผู้สำรวจ .....
วิศวกร .....
หัวหน้าแผนก .....
ผู้อำนวยการกอง .....
ผู้อำนวยการฝ่าย .....

รองผู้ว่าการ ....

การไฟฟ้าส่วนภูมิภาค

ผู้ว่าการ .....

การประกอบคอนกับเสาคอนกรีต 33 kV 1 วงจร
(กรณีพาดสายหุ้มฉนวนแบบไม่เต็มพิกัด (PIC))

33 kV CROSSARM ASSEMBLY ON CONCRETE POLE, 1 CIRCUIT
(PARTIALLY INSULATED CONDUCTOR STRINGING)

ใช้แทนแบบ .....
ถูกแทนโดยแบบ .....
เขียนเสร็จวันที่ 27 มี.ค. 40
แก้แบบวันที่ .....
มิติเป็น มิลลิเมตร
มาตราส่วน 1:20

แบบเลขที่ SA4-015/40007
แผ่นที่ 4 ของจำนวน 6 แผ่น

การประกอบเลขที่ ASSEMBLY NO. **3908**

บัญชีวัสดุ
BILL OF MATERIAL

ลำดับที่ ITEM	รายละเอียด DESCRIPTION	จำนวน REQ'D I	I*	II	II*	III	IV	V	วัสดุเลขที่ MAT. NO.
12	แหวนสี่เหลี่ยมแบน 52x52x4.5 มม. รู ø18 มม. มอก. 258 WASHER, SQUARE, FLAT, 52x52x4.5 mm, HOLE. ø18 mm, TIS 258	5	4	5	4	13	14	14	01180100
13	แหวนสี่เหลี่ยมโค้ง 60x60x5 มม. เส้นผ่านศูนย์กลางรู 22 มม. WASHER, SQUARE, CURVED 60x60x5 mm HOLE DIA. 22 mm	3	3	3	3	3	–	–	01180201
14	แหวนรองแบบสปริง ขนาดระบุ 16มม. ประเภทใช้งานทั่วไป มอก. 259 WASHER, LOCK, SPRING, SIZE 16 mm, GENERAL PURPOSE, TIS 259	1	1	1	1	–	–	–	01180301
15	สเตรนแคล้มป์ หรือปรีฟอร์มเข้าปลายสาย พร้อมทิมเบิลเคลวิส ขนาดตามต้องการ CLAMP, STRAIN ; OR PREFORMED DEADEND WITH THIMBLE CLEVIS ; SIZE AS REQUIRED	–	–	–	–	6	3	3	03110000-4 02280000-4 03140011
16	หลอดต่อสายชนิดบีบไม่รับแรงดึง สายอะลูมิเนียม ขนาดตามต้องการ CONNECTOR, SPLICE, COMPRESSION TYPE, TENSIONLESS, AL ; SIZE AS REQUIRED	–	–	–	–	3	–	–	02410001-7
17	ยูแคล้มป์ สลัก 1 ตัว M 8 (ไวร์ โรป คลิ้พ) CLAMP, SINGLE U-BOLT, M. 8 (WIRE ROPE CLIP)	1	1	1	1	1	1	1	01230000
18	ลวดเหล็กกลม เส้นผ่าศูนย์กลาง 4.0 มม. เส้นเดียว มอก. 71 WIRE, STEEL SOLID DIA 4.0 mm TIS.71	4 ม.m	4 ม.m	4 ม.m	4 ม.m	4 ม.m	– ม.m	– ม.m	01100000
19	ลูกถ้วยก้านตรง มอก. 279 แบบ ค (แบบ 56-3) พร้อมก้าน INSULATOR, PIN TYPE, TIS 279, TYPE C (CLASS 56-3) ; COMPLETE WITH PIN	3	3	3	3	3	–	2	03000002 & 03100001
20	ลูกถ้วยแขวน มอก. 354 แบบ ง (แบบ 52-4) INSULATOR, SUSPENSION TYPE, TIS 354, TYPED (CLASS 52-4)	–	–	–	–	18	9	9	03020002
21	พี.จี. คอนเนคเตอร์ สำหรับสายอะลูมิเนียม ขนาดตามต้องการ CONNECTOR, PARALLEL GROOVE, Al ; SIZE AS REQUIRED	–	–	–	–	–	–	6	02300102-4
22	ลวดอะลูมิเนียมกลม 4.0 มม. ความยาวตามต้องการ TIE WIRE, Al 4.0 mm ; LENGTH AS REQUIRED	ม.m	ม.m	ม.m	ม.m	ม.m	ม.m	ม.m	02200002
23	เทปพันเคเบิลอากาศแรงสูง ขนาด 3/4" x 30' ELECTRICAL, SPLICING TAPE, FOR H.T. AERIAL CABLE, SIZE 3/4" x 30'	–	–	–	–	ม้วน Roll	ม้วน Roll	–	02180003
24	สายยึดโยงแบบ GY-32 GUY ASSEMBLY, GY-32	–	–	–	–	1	1	–	

บัญชีวัสดุสำหรับติดตั้งสายล่อฟ้า
BILL OF MATERIAL, FOR OHGW INSTALLATION

ลำดับที่ ITEM	รายละเอียด DESCRIPTION	จำนวน REQ'D I	I*	II	II*	III	IV	V	วัสดุเลขที่ MAT. NO.
25	เหล็กฉากรับสายล่อฟ้าทางตรง OVERHEAD, GROUND WIRE BAYONET	1	1	–	–	–	–	–	01010003

กองวิศวกรรมไฟฟ้าและเครื่องกล ฝ่ายวิศวกรรม	การไฟฟ้าส่วนภูมิภาค	ใช้แทนแบบ ..... ถูกแทนโดยแบบ .....
ผู้เขียน ..... ผู้สำรวจ ..... วิศวกร ..... หัวหน้าแผนก ..... ผู้อำนวยการกอง ..... ผู้อำนวยการฝ่าย	ผู้ว่าการ ..... พ.ศ. 2548	เขียนเสร็จวันที่ 27 มี.ค. 40 แก้แบบวันที่ ..... มิติเป็น ..... มาตราส่วน .....
รองผู้ว่าการ	การประกอบคอนกับเสาคอนกรีต 33 kV 1 วงจร (กรณีพาดสายหุ้มฉนวนแบบไม่เต็มพิกัด (PIC)) 33 kV CROSSARM ASSEMBLY ON CONCRETE POLE, 1 CIRCUIT (PARTIALLY INSULATED CONDUCTOR STRINGING)	แบบเลขที่ SA4-015/40007 แผ่นที่ 5 ของจำนวน 6 แผ่น

การประกอบเลขที่ ASSEMBLY NO. 3908

บัญชีวัสดุสำหรับติดตั้งสายล่อฟ้า
BILL OF MATERIAL, FOR OHGW INSTALLATION

ลำดับที่ ITEM	รายละเอียด DESCRIPTION	จำนวน REQ'D							วัสดุเลขที่ MAT. NO.
		I	I*	II	II*	III	IV	V	
26	เหล็กรูปรางน้ำ ขนาด 100x50x5 มม. ยาว 2,250 มม. มอก.1227 เจาะรูตามแบบแผ่นที่ 4 STEEL, CHANNEL 100x50x5 mm, 2,250 mm LONG, TIS 1227 ; PUNCH HOLE AS DWG.ON SHEET NO. 4	–	–	1	1	1	1	1	01000100
27	สลักเกลียว M 16x250 มม. BOLT, MACHINE M 16x250 mm	2	2	–	–	2	2	–	01110203
28	สลักเกลียว M 16x350 มม. BOLT, MACHINE M 16x350 mm	–	–	2	2	–	–	2	01110205
29	สลักห่วงกลม M 16x200 มม. BOLT, ROUND EYE M 16x200 mm	–	–	–	–	1	1	1	01140001
30	นัทรูปห่วง M 16 ดิน 582 NUT, EYE M 16 DIN 582	–	–	–	–	1	–	–	01180001
31	แหวนสี่เหลี่ยมแบน 52x52x4.5 มม. รู ø18 มม. มอก. 258 WASHER, SQUARE, FLAT, 52x52x4.5 mm, HOLE. ø18 mm, TIS 258	2	2	2	2	4	3	3	01180100
32	กราวด์วายร์แคล้มป์ แบบ เจ 1152 GROUND WIRE CLAMP J 1152	1	1	1	1	–	–	–	01230205
33	กราวด์วายร์แคล้มป์ สำหรับคอนสาย GROUND WIRE SUPPORT AND CLAMP, FOR WOOD BAYONET	–	–	–	–	–	–	1	01230200
34	กายทิมเบิล สำหรับสายยึดโยง 50–95 ตร.มม. THIMBLE, GUY, FOR STEEL WIRE 50–95 mm²	–	–	–	–	2	1	1	01210304
35	ยูแคล้มป์ สลัก 1 ตัว เอ็ม 8 (ไวร์ โร๊ป คลิ้พ) CLAMP, SINGLE U–BOLT, M. 8 (WIRE ROPE CLIP)	1	1	1	1	7	3	5	01230000

ลำดับที่ ITEM	แบบอ้างอิง REFERENCE DRAWING	แบบเลขที่ DWG NO.	การประกอบเลขที่ ASSENBLY NO.
1	โครงสร้างเสาระบบจำหน่าย 22 kV และ 33 kV สำหรับพาดสายหุ้ม PIC 22 kV AND 33 kV POLE STRUCTURE, FOR PIC STRINGING	IB1–015/33083	8244
2	หลักของการก่อสร้างระบบจำหน่าย 33 kV (เฉพาะแบบเหนือดิน) PRINCIPLES OF 33 kV DISTRIBUTION CONSTRUCTION (OVERHEAD LINE ONLY)	SA4–015/37017	9505

* ใช้ในกรณีประกอบคอนแบบท้ามแขน

* IN CASE ALLEYARM ASSEMBLY

สำเนา

กองวิศวกรรมไฟฟ้าและเครื่องกล ฝ่ายวิศวกรรม	การไฟฟ้าส่วนภูมิภาค	ใช้แทนแบบ ..... ถูกแทนโดยแบบ ..... เขียนแล้วเสร็จวันที่ 27 มี.ค. 40
ผู้เขียน ..... ผู้สำรวจ ..... วิศวกร ..... หัวหน้าแผนก ..... ผู้อำนวยการกอง ..... ผู้อำนวยการฝ่าย	ผู้ว่าการ ..... การประกอบคอนกับเสาคอนกรีต 33 kV 1 วงจร (กรณีพาดสายหุ้มฉนวนแบบไม่เต็มพิกัด (PIC))	แก้แบบวันที่ ..... มิติเป็น ..... มาตราส่วน .....
รองผู้ว่าการ	33 kV CROSSARM ASSEMBLY ON CONCRETE POLE, 1 CIRCUIT (PARTIALLY INSULATED CONDUCTOR STRINGING)	แบบเลขที่ SA4–015/40007 แผ่นที่ 6 ของจำนวน 6 แผ่น