การประกอบเลขที่
ASSEMBLY NO. 3202

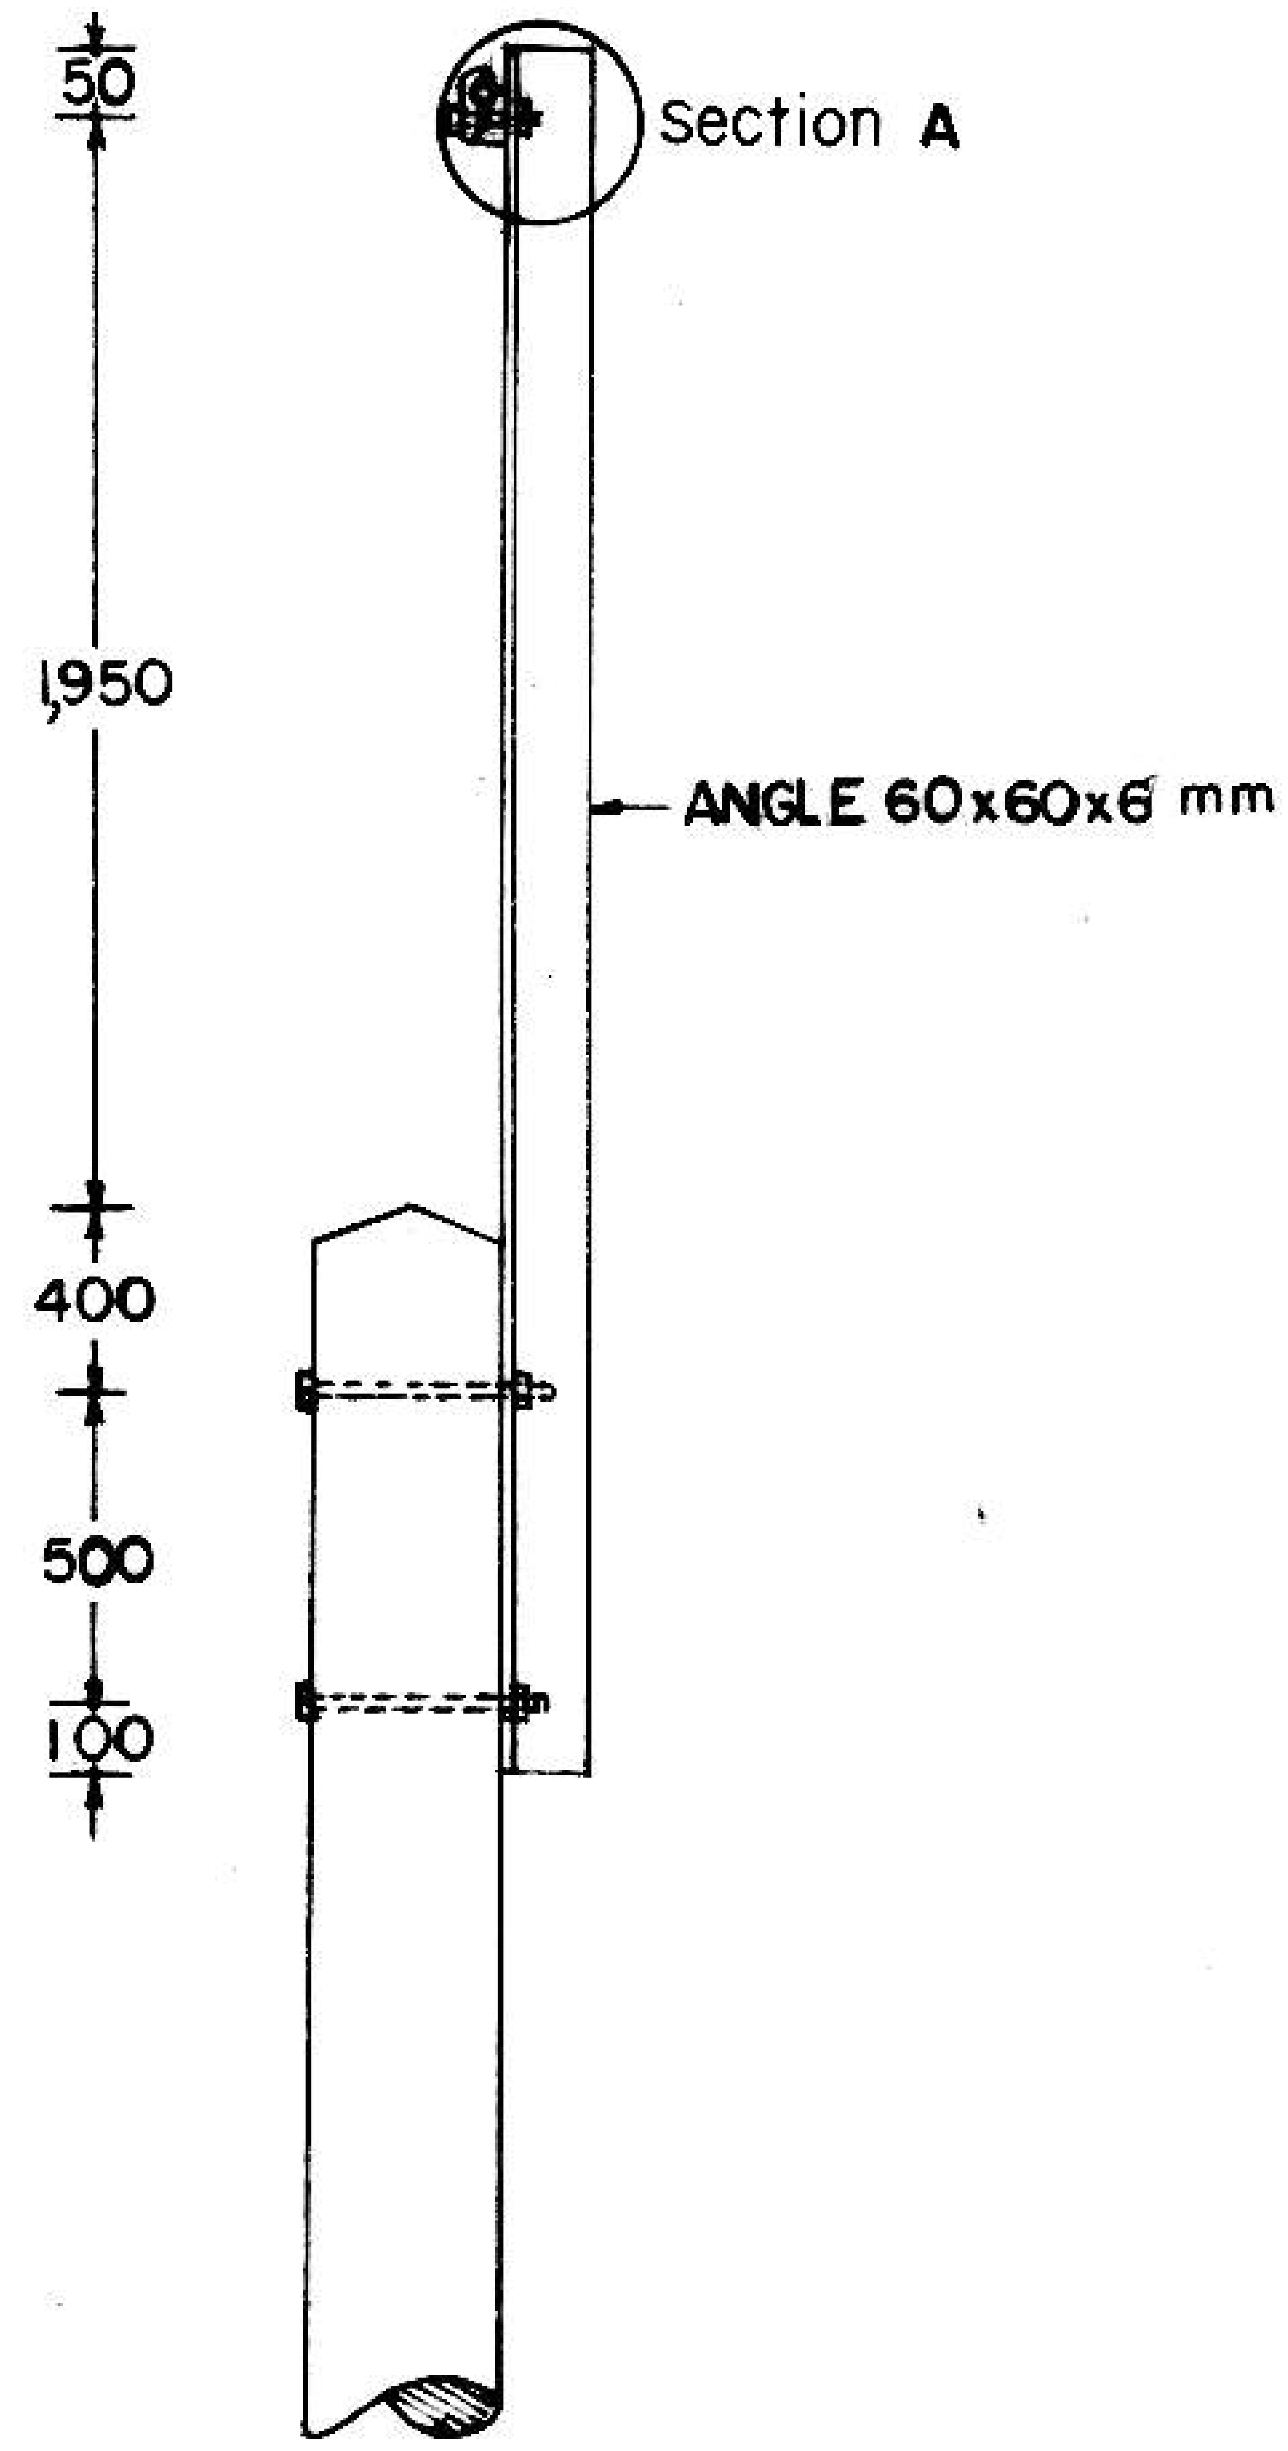

เหล็กฉากรับสายล่อฟ้าทางตรง
STRAIGHT BAYONET
SCALE 1:40

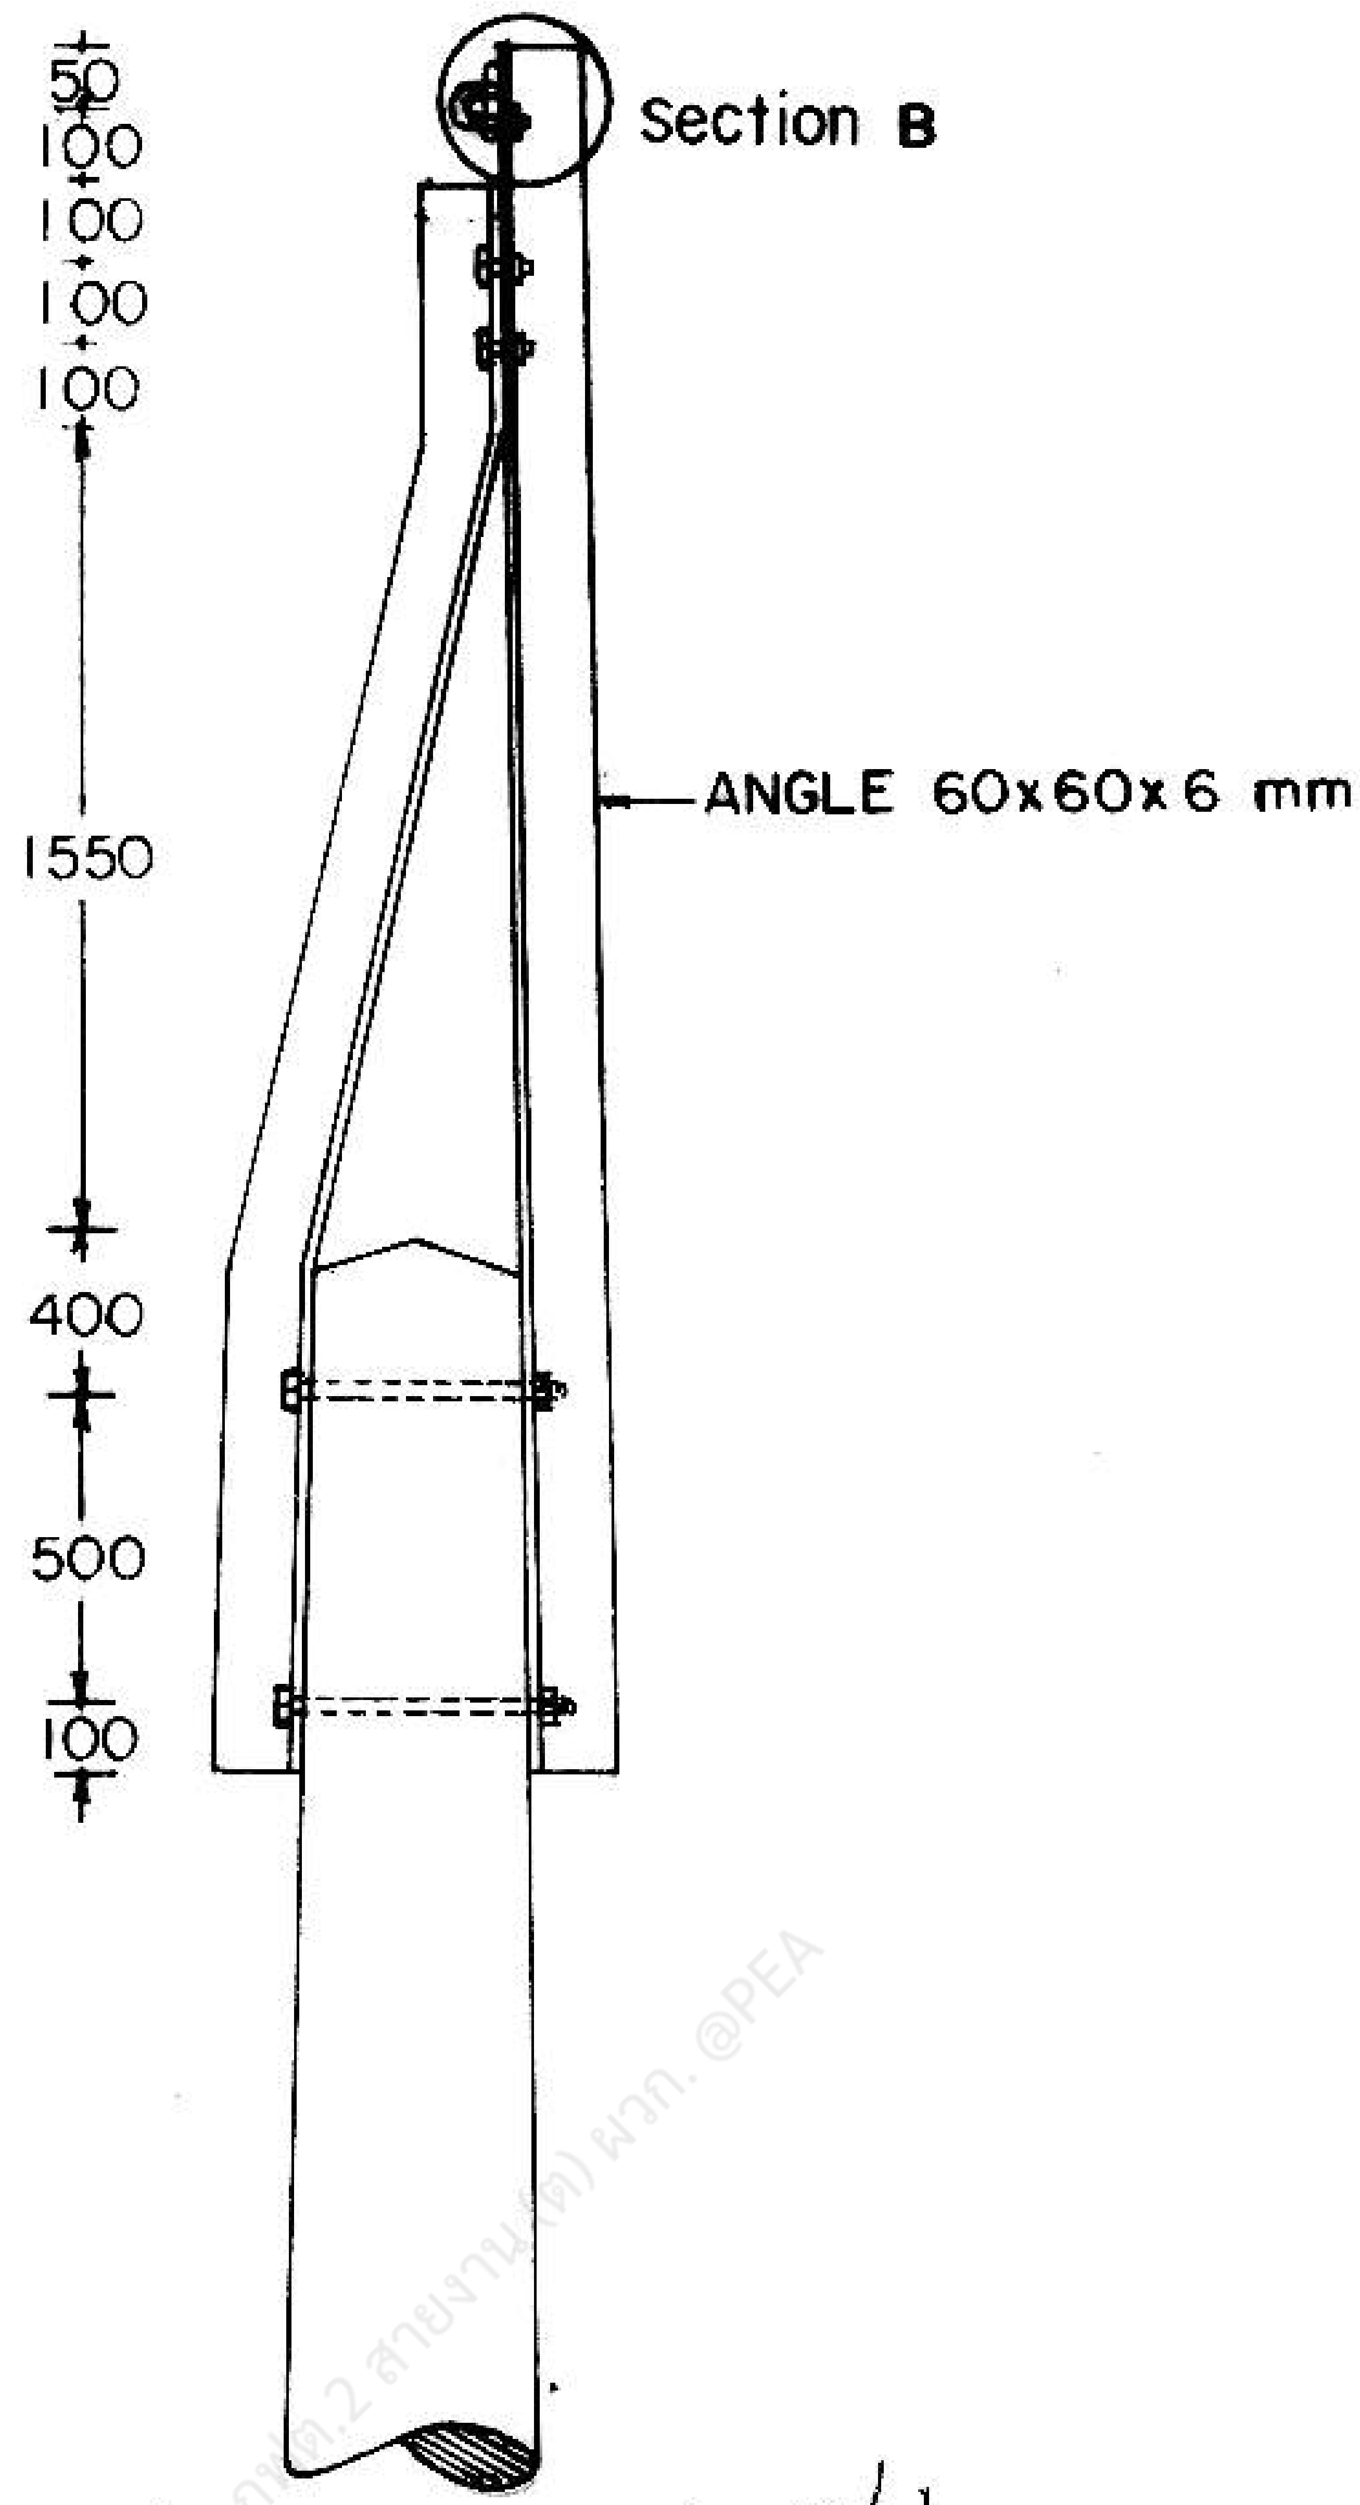

เหล็กฉากรับสายล่อฟ้าทางโค้ง
CORNER BAYONET
SCALE 1:40

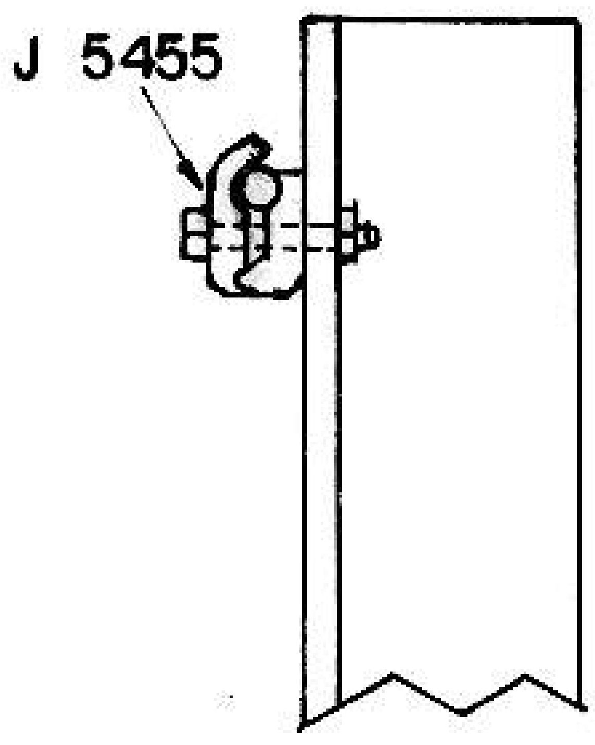

SECTION A
SCALE 1:5

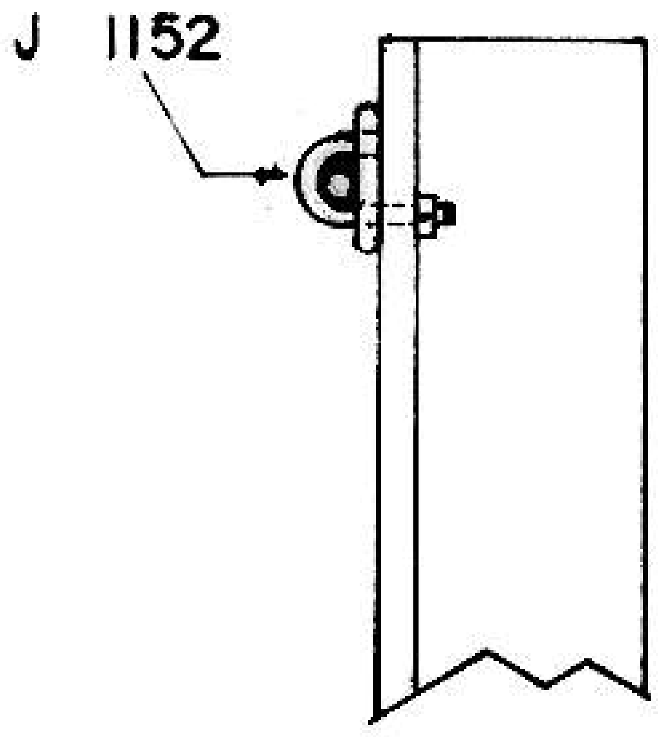

SECTION B
SCALE 1:5

กราวด์ไวร์แคล้มป์เหมือนแบบ J 5455 และ J 1152
GROUND WIRE CLAMP SIMILAR TO JOSLYN CAT NO. J 5455 AND J 1152

อดิวิทย์ ทองลา พชง.3 ผปร. กฟส.อล. กฟฉ.1 กฟต.2 สายงาน(ต) ผวก. @PEA

กองวิศวกรรมและวางแผน
ผู้เขียน
สถาปนิก
วิศวกร
หัวหน้าแผนก
ผู้อำนวยการกอง
รองผู้ว่าการฝ่ายเทคนิค

การไฟฟ้าส่วนภูมิภาค
ผู้ว่าการ

การประกอบเหล็กฉากรับสายล่อฟ้า
ระบบ 33 kV

OVERHEAD GROUND WIRE BAYONET ASSEMBLY
33 KV SYSTEM

ใช้แทนแบบ
ถูกแทนโดยแบบ
เขียนเสร็จวันที่ 20/9/12
แก้แบบครั้งที่
มิติเป็น มม.
มาตราส่วน 1:5, 1:40
แบบเลขที่ I50-015/120277
แผ่นที่ 1 ของจำนวน 2 แผ่น

การประกอบเลขที่
ASSEMBLY NO. 3202

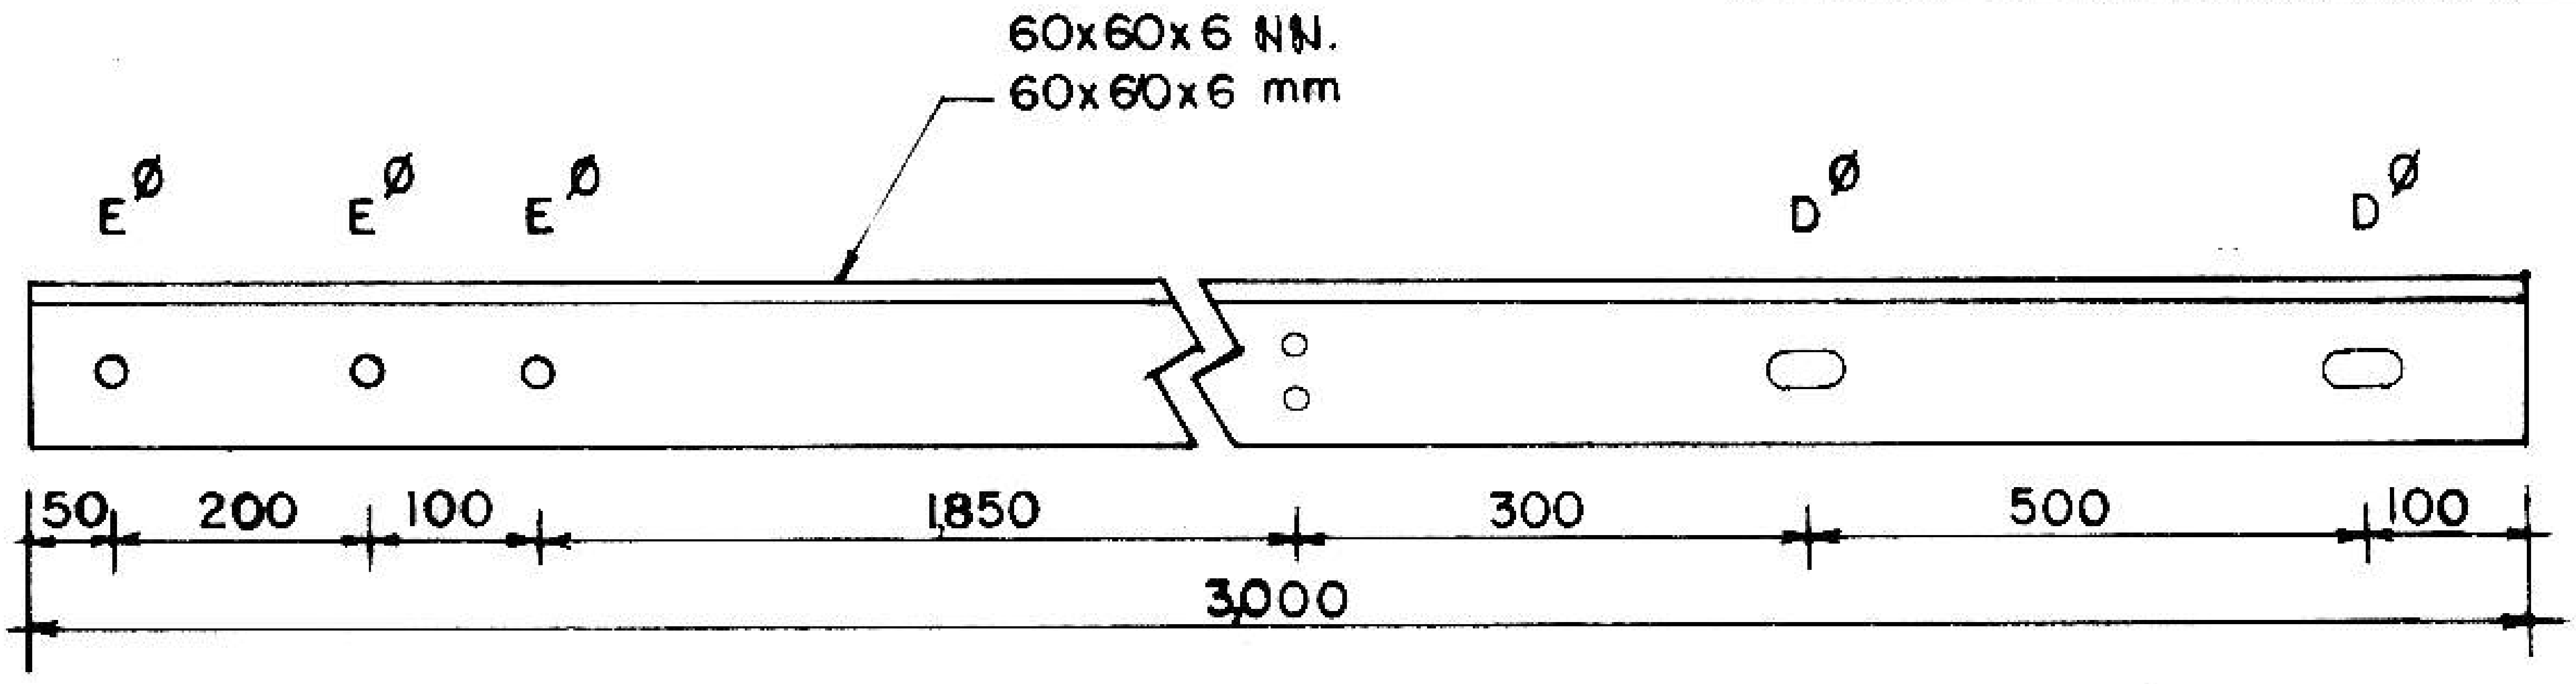

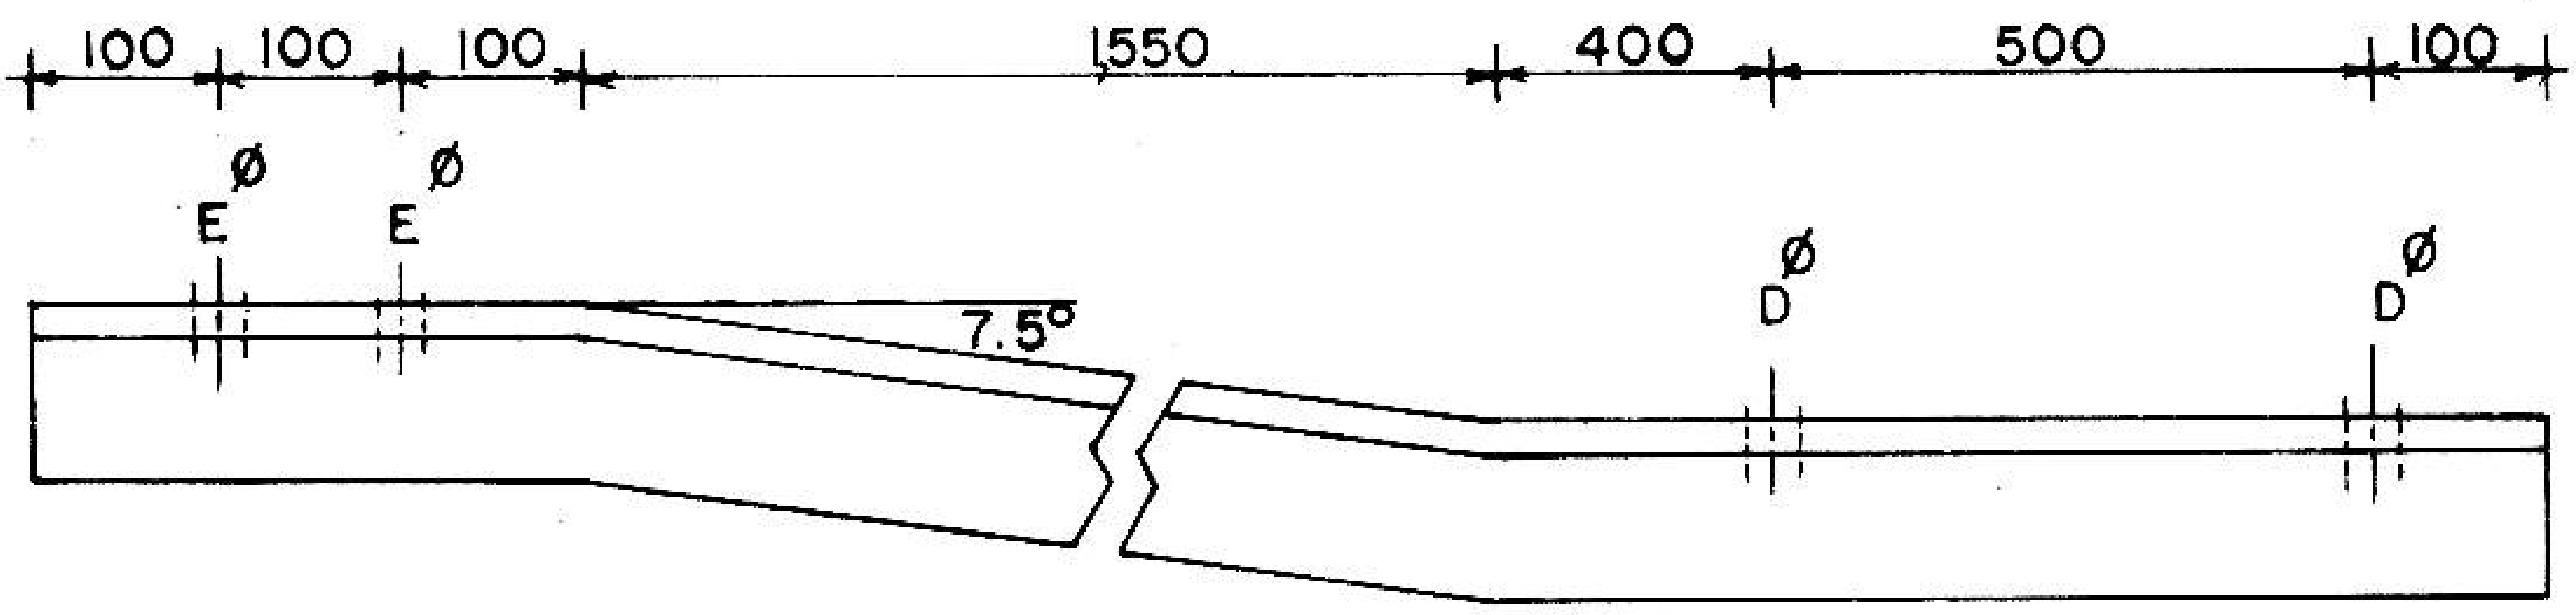

$E^{\varnothing}$ = เจาะรู 14 มม.
$D^{\varnothing}$ = เจาะรู 18X30 มม.
$E^{\varnothing}$ = 14 mm hole
$D^{\varnothing}$ = 18X30 mm hole

อดิวิทย์ ทองลา พชง.3 ผปร. กฟส.อล. กฟจ.กบ. กฟต.2 สายงาน (ต) ผวก. @PEA

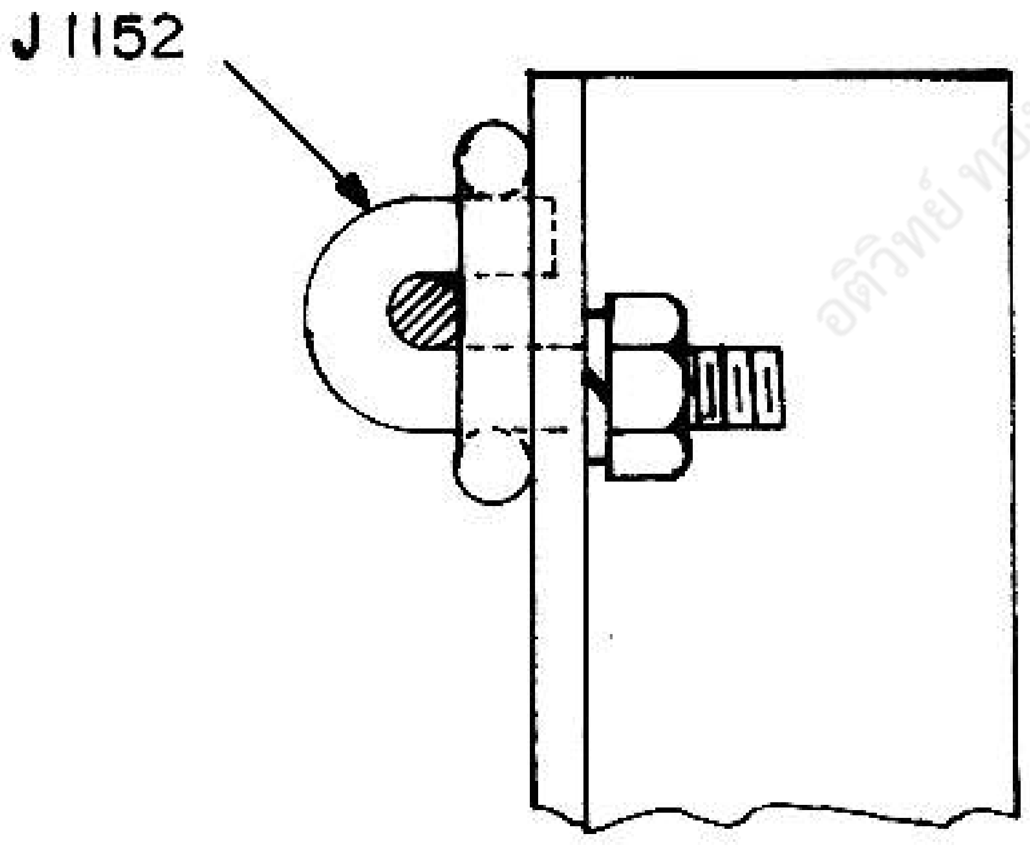

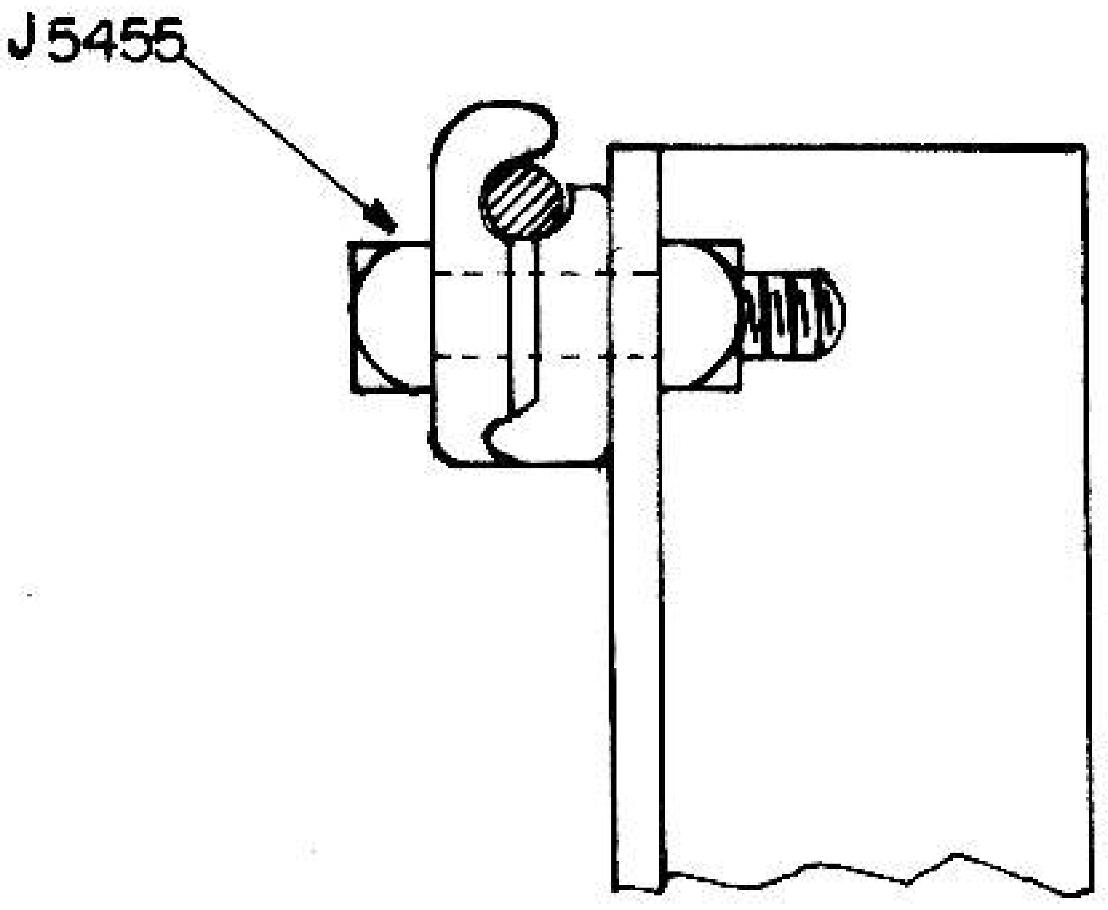

หมายเหตุ การาวด์ไวร์แคล้มป์ แบบ J 5455 ปัจจุบัน กฟภ. เลิกการจัดซื้อแล้ว ของส่วนที่เหลือคงคลังให้เบิกจ่าย สำหรับการก่อสร้างระบบจำหน่ายทางตรง มุม 0-5° จนกว่าจะหมด

กองวิศวกรรมและวางแผน	การไฟฟ้าส่วนภูมิภาค	ใช้แทนแบบ
ผู้เขียน พระเจ ๑๒ สถาปนิก วิศวกร หัวหน้าแผนก ผู้อำนวยการกอง	ผู้ว่าการ เหล็กฉากรับสายล่อฟ้า	ถูกแทนโดยแบบ เขียนเสร็จวันที่ 20/9/12 แก้แบบวันที่ มิติเป็น มม. มาตราส่วน 1:10
รองผู้ว่าการฝ่ายเทคนิค	OVERHEAD GROUND WIRE BAYONET	แบบเลขที่ 150-015/12027 แผ่นที่ 2 ของจำนวน 2 แผ่น