การประกอบเลขที่
ASSEMBLY NO. 0215

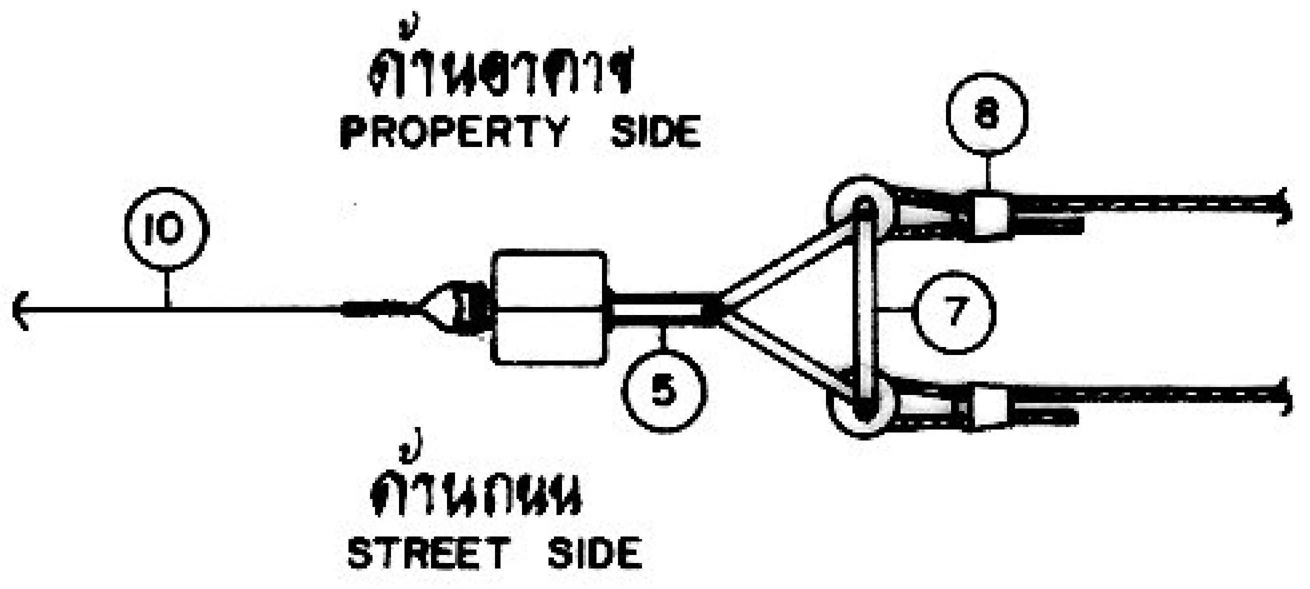
ด้านอาคาร
PROPERTY SIDE
10
8
7
5
ด้านถนน
STREET SIDE

N – สายเป็นกลาง
NEUTRAL LINE

A,B,C – สายเฟส
PHASE LINE

L – สายต่อไฟถนน
STREET LIGHTING LINE

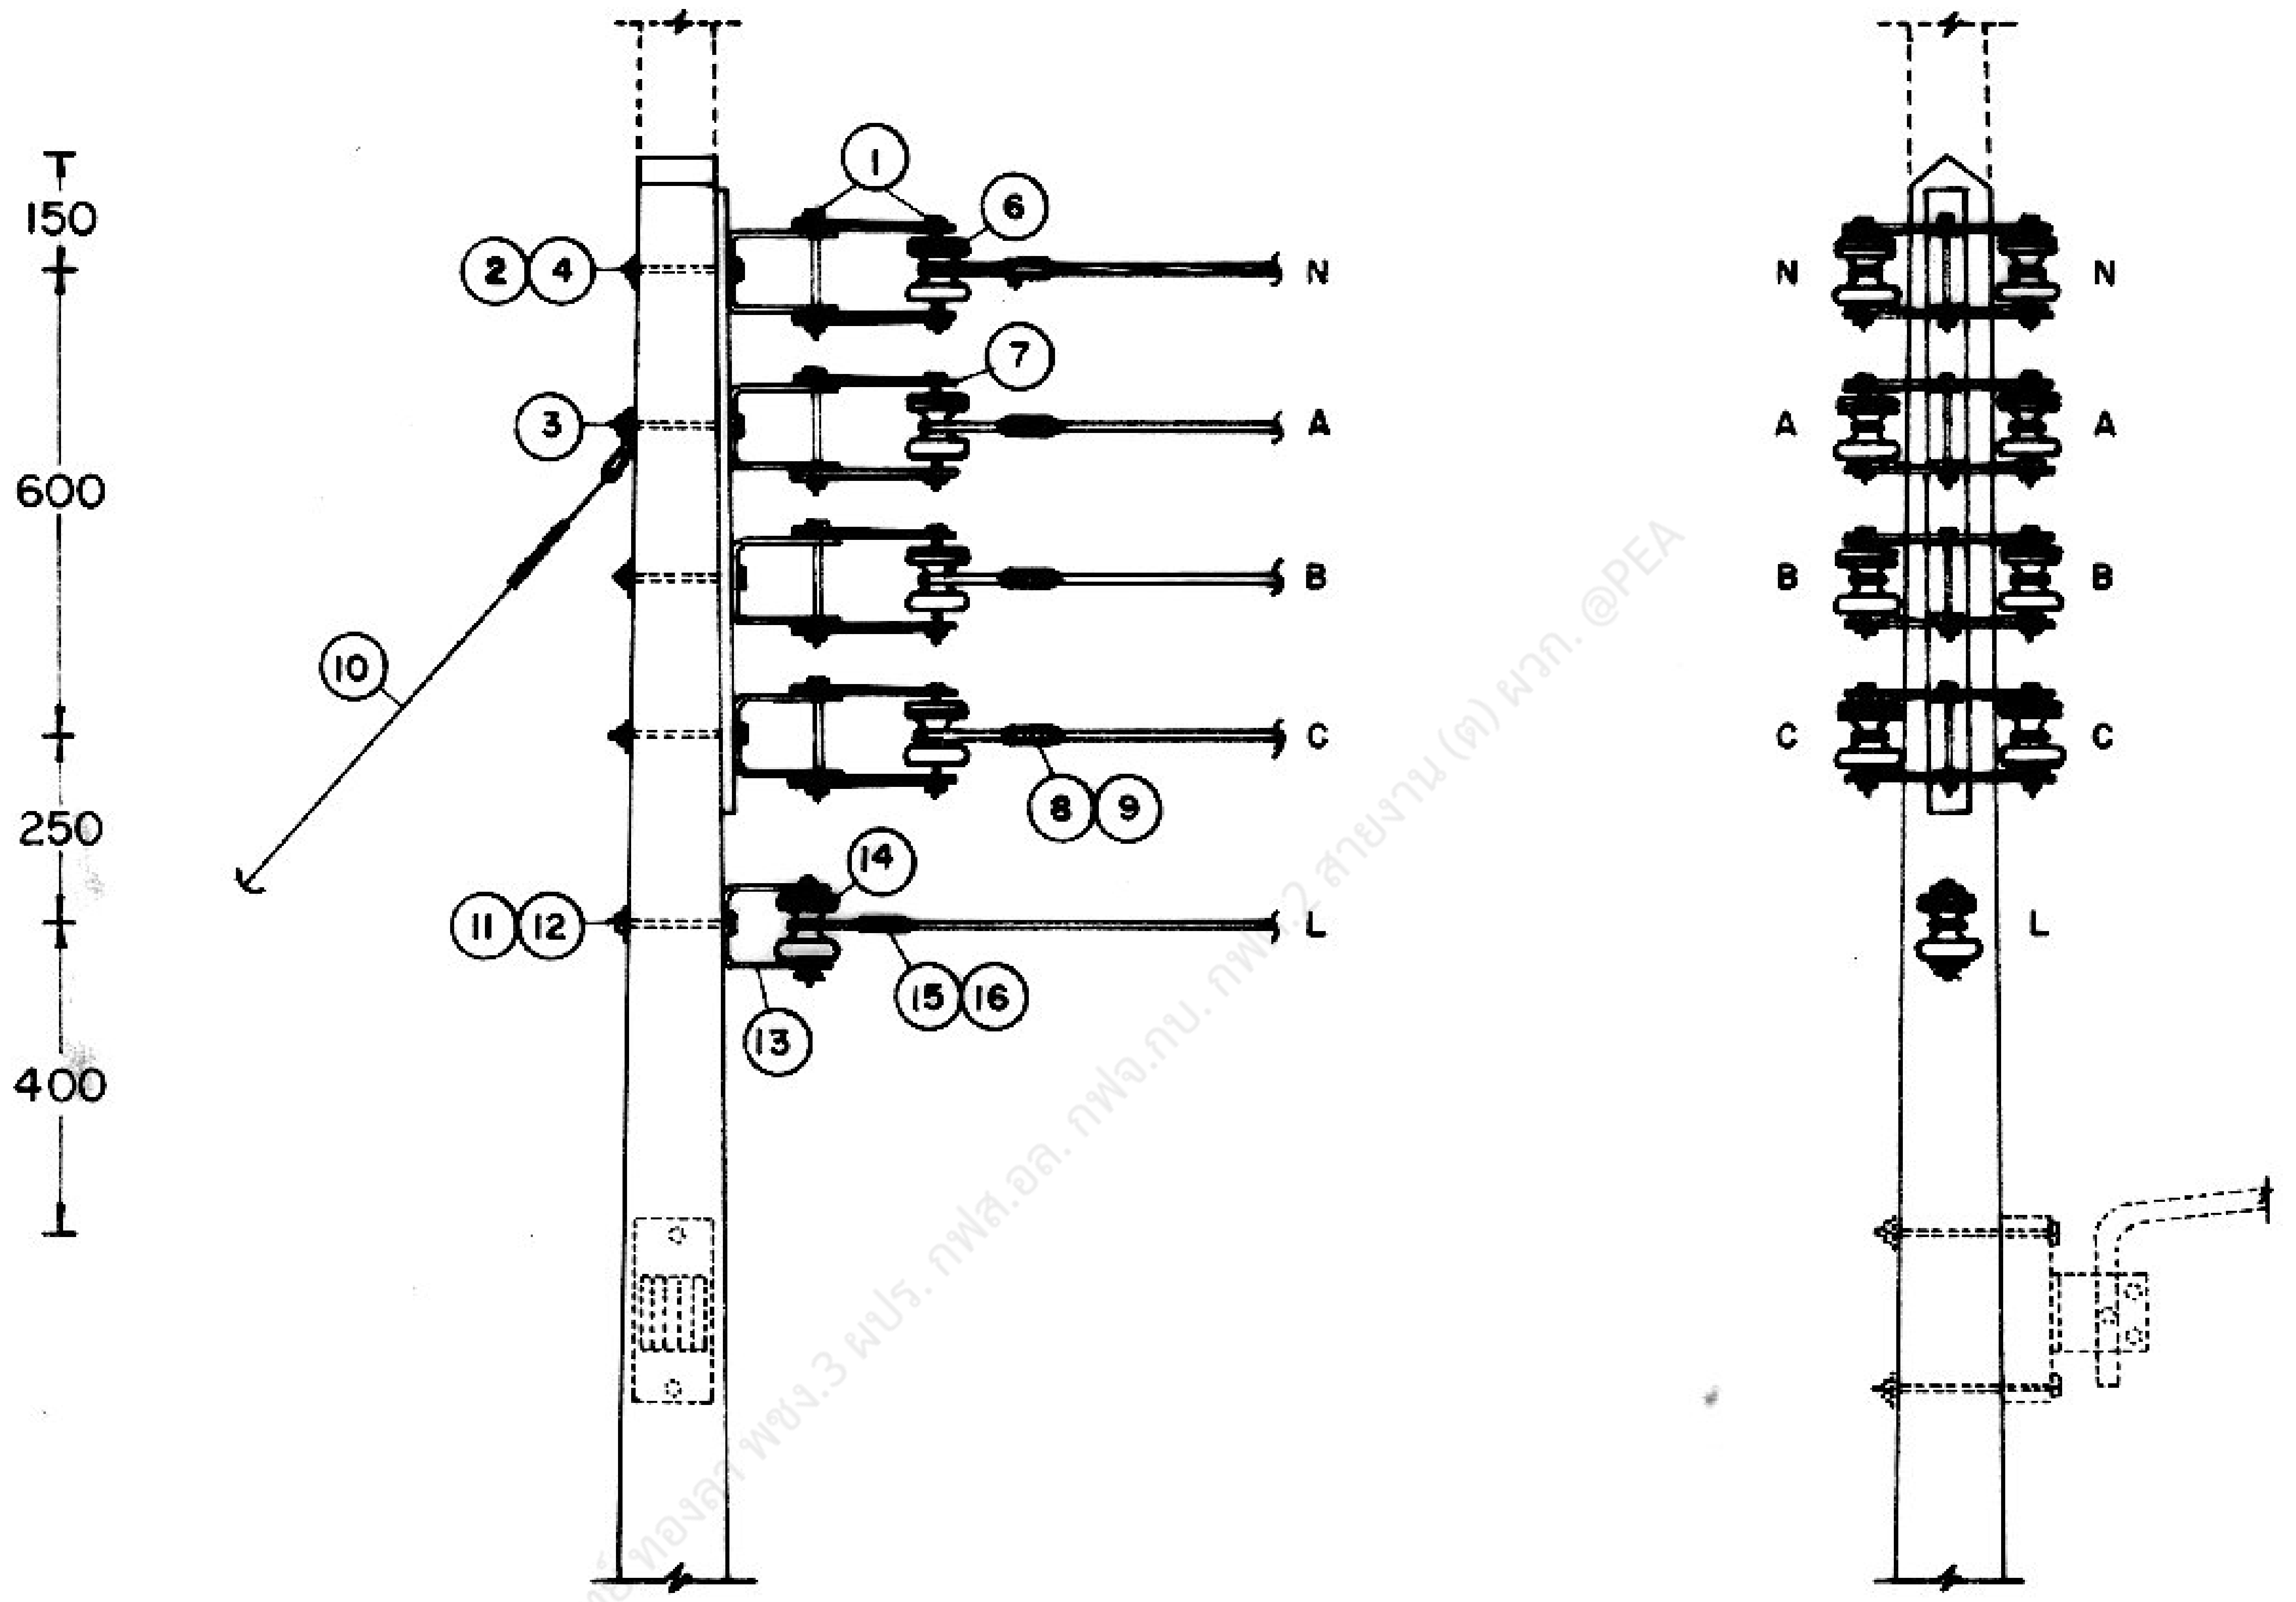
150
600
250
400
1
6
2
4
7
3
10
8
9
14
11
12
15
16
13
N
A
B
C
L

แบบ 3 เฟส 4 สาย 2 วงจร
3-PHASE 4-WIRE 2-CIRCUITS

หมายเหตุ การประกอบคอนเนคเตอร์เข้าปลายสาย ดูแบบเลขที่ SAI-015/22015

NOTE DEADEND CONNECTOR ASSEMBLY SEE DWG. NO. SAI-015/22015

กองวิศวกรรมไฟฟ้าและเครื่องกล ฝ่ายวิศวกรรม	การไฟฟ้าส่วนภูมิภาค	ใช้แทนแบบ.......... ถูกแทนโดยแบบ..........
ผู้เขียน.......... ผู้สำรวจ.......... วิศวกร.......... หัวหน้าแผนก.......... หัวหน้ากอง.......... ผู้อำนวยการฝ่าย..........	ผู้ว่าการ.......... การติดตั้งแร็คแรงต่ำบนเสาคอนกรีต 9 ม. 2 วงจร สำหรับเข้าปลายสายเสาต้นสุดท้าย	เขียนเสร็จวันที่ 12 เม.ย. 22 แก้แบบวันที่.......... มิติเป็น มม. มาตราส่วน 1 : 20
รองผู้ว่าการฝ่ายเทคนิค..........	SECONDARY RACK INSTALLATION ON 9 m CONCRETE POLE 2-CIRCUITS FOR DEADEND STRUCTURE	แบบเลขที่ SAI-015/22025 แผ่นที่ 1 ของจำนวน 3 แผ่น

7 ก.ย. 2522

อดิวิทย์ ทองลา พชง.3 ผปร. กฟส.อล. กฟจ.กบ. กฟข.2 สายงาน (ต) ผวก. @PEA

การประกอบเลขที่
ASSEMBLY NO. 0215

บัญชีวัสดุ
BILL OF MATERIAL

ลำดับที่ ITEM	รายละเอียด DESCRIPTION	จำนวน REQ'D	วัสดุเลขที่ MAT. NO.
1	สลักเกลียว M 16 X 170 มม. BOLT, MACHINE, M 16 X 170 mm	12	01110201
2	สลักเกลียว M 16 X 170 มม. BOLT, MACHINE, M 16 X 170 mm	3	01110201
2a	สลักเกลียว M 16 X 250 มม. สำหรับเสาคอนกรีต 12 ม. BOLT, MACHINE, M 16 X 250 mm FOR 12 m CONCRETE POLE	3	01110203
3	สลักเกลียว M 16 X 200 มม. BOLT, MACHINE, M 16 X 200 mm	1	01110202
3a	สลักเกลียว M 16 X 250 มม. สำหรับเสาคอนกรีต 12 ม. BOLT, MACHINE, M 16 X 250 mm FOR 12 m CONCRETE POLE	1	01110203
4	แหวนสี่เหลี่ยมแบน 52 X 52 X 4.5 มม. รู Ø 18 มม. มอก. 258 WASHER, SQUARE, FLAT, 52 X 52 X 4.5 mm HOLE Ø 18 mm TIS 258	3	01180100
5	แร็ค 4 X 200 มม. แบบหลังยื่น RACK, SECONDARY, MEDIUM PRESSED STEEL 4 X 200 mm EXTENDED BACK	1	03130002
6	ลูกถ้วยแรงต่ำ มอก. 227 แบบ ข (แบบ 53-2) INSULATOR, SPOOL TYPE, L.T. TIS 227 TYPE B (CLASS 53-2)	8	03030000
7	เหล็กแผ่น 6 X 30 X 250 มม. แบบเลขที่ SAI-015/22030 (การประกอบเลขที่ 0105) PLATE, STEEL 6 X 30 X 250 mm DWG. NO. SAI-015/22030 (ASSEMBLY NO. 0105)	24	01030001
8	คอนเนคเตอร์เข้าปลายสายอะลูมิเนียม ขนาดตามต้องการ CONNECTOR, DEADEND , AI SIZE AS REQUIRED	8	02310000-2
9	PVC เทป กว้าง 19 มม. (ใช้ความยาว 2 ม. ต่อ จุด) มอก. 386 PVC TAPE, 19 mm WIDE (2 m LONG PER POINT) TIS 386		02180001 or 02180002
10	การประกอบสายยึดโยง GY-01 GUY ASSEMBLY GY - 01	1	–
10a	การประกอบสายยึดโยง GY-02 สำหรับเสาคอนกรีต 12 ม. GUY ASSEMBLY GY - 02 FOR 12 m CONCRETE POLE	1	–
	สำหรับการติดตั้งสายดับไฟถนน FOR STREET LIGHTING INSTALLATION		
11	สลักเกลียว M 16 X 170 มม. BOLT, MACHINE, M 16 X 170 mm	1	01110201
11a	สลักเกลียว M 16 X 250 มม. สำหรับเสาคอนกรีต 12 ม. BOLT, MACHINE, M 16 X 250 mm FOR 12 m CONCRETE POLE	1	01110203
12	แหวนสี่เหลี่ยมแบน 52 X 52 X 4.5 มม. รู Ø 18 มม. มอก. 258 WASHER, SQUARE, FLAT, 52 X 52 X 4.5 mm HOLE Ø 18 mm TIS. 258	1	01180100
13	ที่จับลูกถ้วยสำหรับลูกถ้วย มอก. 227 (แบบ 53-2) CLEVIS, FLAT STEEL, FOR INSULATOR TIS. 227 (CLASS 53-2)	1	03130100
14	ลูกถ้วยแรงต่ำ มอก. 227 แบบ ข (แบบ 53-2) INSULATOR, SPOOL TYPE, L.T. TIS 227 TYPE B (CLASS 53-2)	1	03030000
15	คอนเนคเตอร์เข้าปลายสายอะลูมิเนียม 25-35 ต.มม. CONNECTOR, DEADEND , AI 25-35 mm^2	1	02310000
16	PVC เทป กว้าง 19 มม. (ใช้ความยาว 2 ม. ต่อ จุด) มอก. 386 PVC TAPE, 19 mm WIDE (2 m LONG PER POINT) TIS 386		02180001 or 02180002

กองวิศวกรรมไฟฟ้าและเครื่องกล ฝ่ายวิศวกรรม	การไฟฟ้าส่วนภูมิภาค	ใช้แทนแบบ.......... ถูกแทนโดยแบบ..........
ผู้เขียน.......... ผู้สำรวจ.......... วิศวกร.......... หัวหน้าแผนก.......... หัวหน้ากอง.......... ผู้อำนวยการฝ่าย..........	ผู้ว่าการ.......... การติดตั้งแร็คแรงต่ำกับเสาคอนกรีต 9 ม. 2 วงจร สำหรับเข้าปลายสายเสาต้นสุดท้าย	เขียนเสร็จวันที่ 12 เม.ย. 22 แก้แบบวันที่.......... ผิดเป็น.......... มาตราส่วน..........
รองผู้ว่าการฝ่ายเทคนิค	SECONDARY RACK INSTALLATION ON 9 m CONCRETE POLE 2-CIRCUITS FOR DEADEND STRUCTURE	แบบเลขที่ SAI-015/22025 แผ่นที่ 2 ของจำนวน 3 แผ่น

- 7 ก.ย. 252

การประกอบเลขที่
ASSEMBLY NO. 0215

คำแนะนำ การจึงสายระบบจำหน่ายแรงต่ำ จะต้องมีระยะหย่อนยานตามตารางข้างล่างนี้

SUGGESTION MINIMUM SAG OF L.T. DISTRIBUTION LINE AS SHOWN IN THE FOLLOWING TABLE.

ขนาดสายไฟฟ้า ต.มม. SIZE OF CONDUCTOR mm^2	ระยะหย่อนยานต่ำสุด ม. MINIMUM SAG m	
	ระยะระหว่างเสา SPAN 40 ม. m	ระยะระหว่างเสา SPAN 50 ม. m
50 , 70	0.35	0.50
95	0.40	0.60

อติวิทย์ ทองลา พชง.3 ผปร. กฟส.อล. กฟจ.กบ. กฟต.2 สายงาน (ต) ผวก. @PEA

กองวิศวกรรมไฟฟ้าและเครื่องกล
ฝ่ายวิศวกรรม

ผู้เขียน
ผู้สำรวจ
วิศวกร กิตติพงษ์
หัวหน้าแผนก
หัวหน้ากอง
ผู้อำนวยการฝ่าย
รองผู้ว่าการฝ่ายเทคนิค

- 1 ก.ย. 22

การไฟฟ้าส่วนภูมิภาค

ผู้ว่าการ

การติดตั้งแร็คแรงต่ำกับเสาคอนกรีต 9 ม.
2 วงจร
สำหรับเข้าปลายสายเสาต้นสุดท้าย

SECONDARY RACK INSTALLATION ON 9 m CONCRETE POLE
2-CIRCUITS
FOR DEADEND STRUCTURE

ใช้แทนแบบ
ถูกแทนโดยแบบ
เขียนเสร็จวันที่ 12 เม.ย. 22
แก้แบบวันที่
มิติเป็น
มาตราส่วน
แบบเลขที่ SAI-015/22025
แผ่นที่ 3 ของจำนวน 3 แผ่น