

การประกอบเลขที่ ASSEMBLY NO. 5288

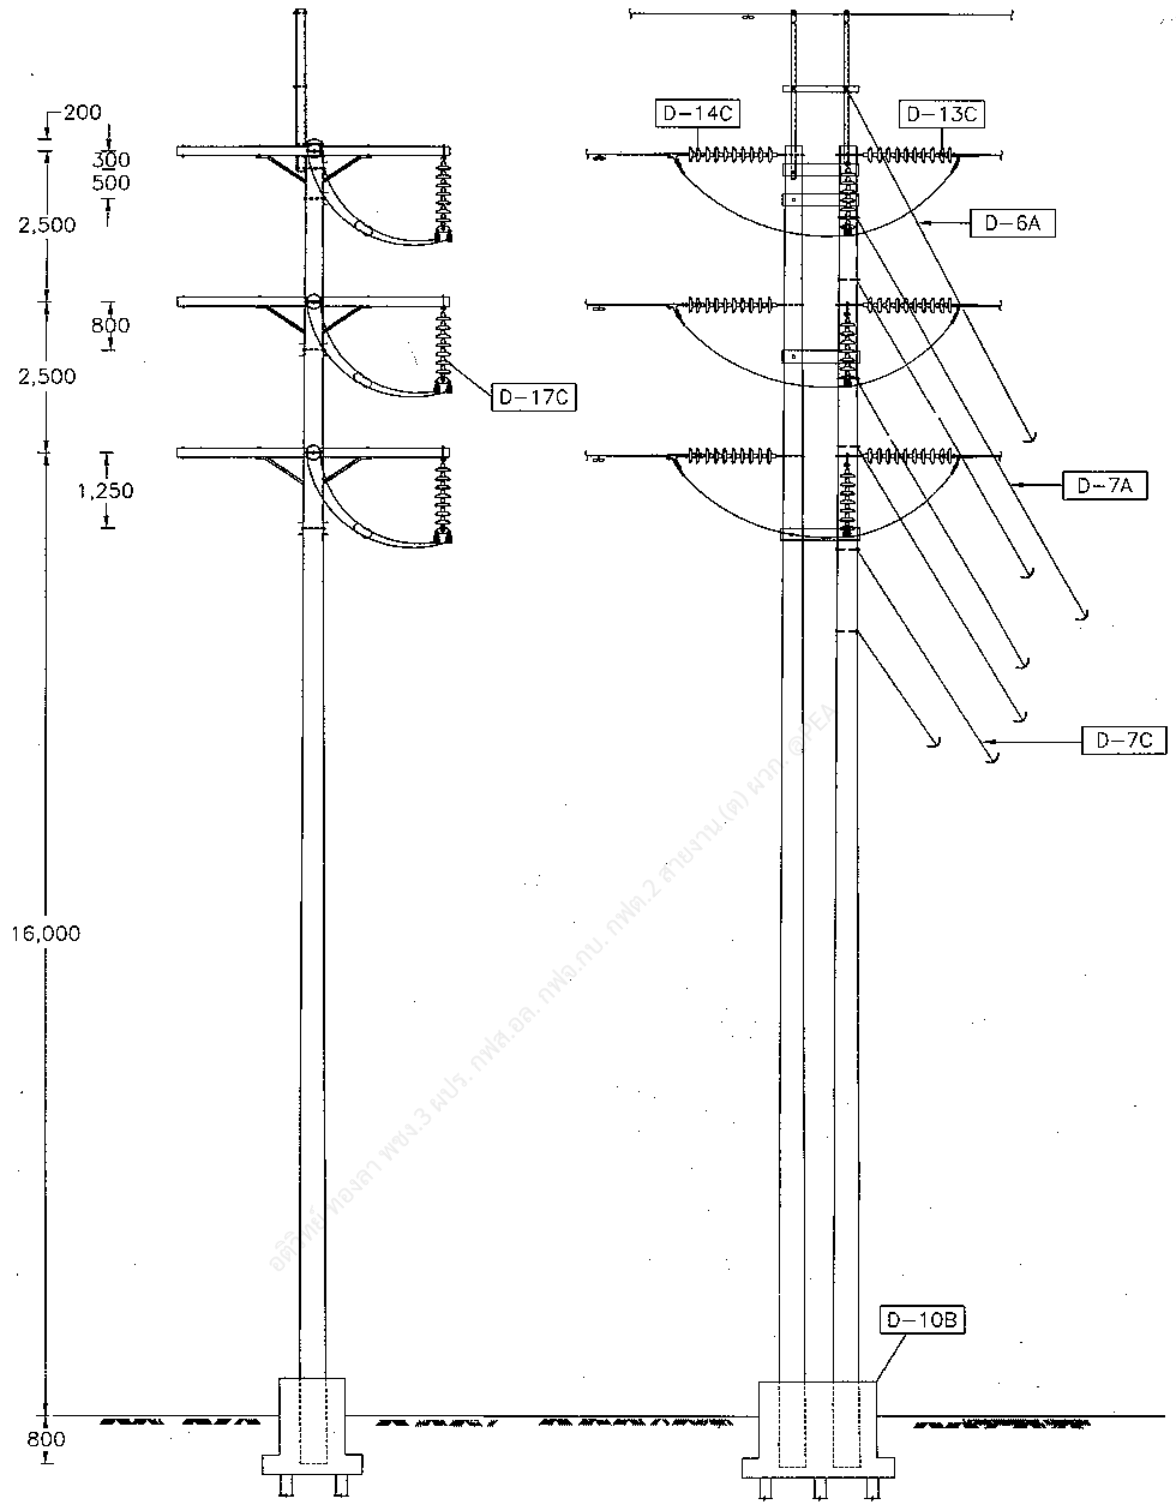


กองวิศวกรรมไฟฟ้าและเครื่องกล ฝ่ายวิศวกรรม	การไฟฟ้าส่วนภูมิภาค	ใช้แทนแบบ ..... ถูกแทนโดยแบบ .....
ผู้เขียน สมนึก สาครฯ ผู้สำรวจ ..... วิศวกร ..... หัวหน้าแผนก ..... ผู้อำนวยการกอง ..... ผู้อำนวยการฝ่าย	ผู้ว่าการ ..... (นาย)	เขียนเสร็จวันที่ 25 พ.ค. 43 แก้แบบวันที่ ..... มิติเป็น มิลลิเมตร มาตราส่วน 1 : 125
รองผู้ว่าการเทคนิคและบริการ ..... (นาย)	115 kV วงจรเดี่ยว สายไฟฟ้าคู่ โครงสร้างเสาช่วงระยะไม่เกิน 200 เมตร แบบ SD-LS-2 115 kV SINGLE CIRCUIT DOUBLE CONDUCTOR SPAN ≤ 200 m STRUCTURE TYPE SD-LS-2	แบบเลขที่ SA1-015/43003 แผ่นที่ 1 ของจำนวน 6 แผ่น

การประกอบเลขที่
ASSEMBLY NO. 5288

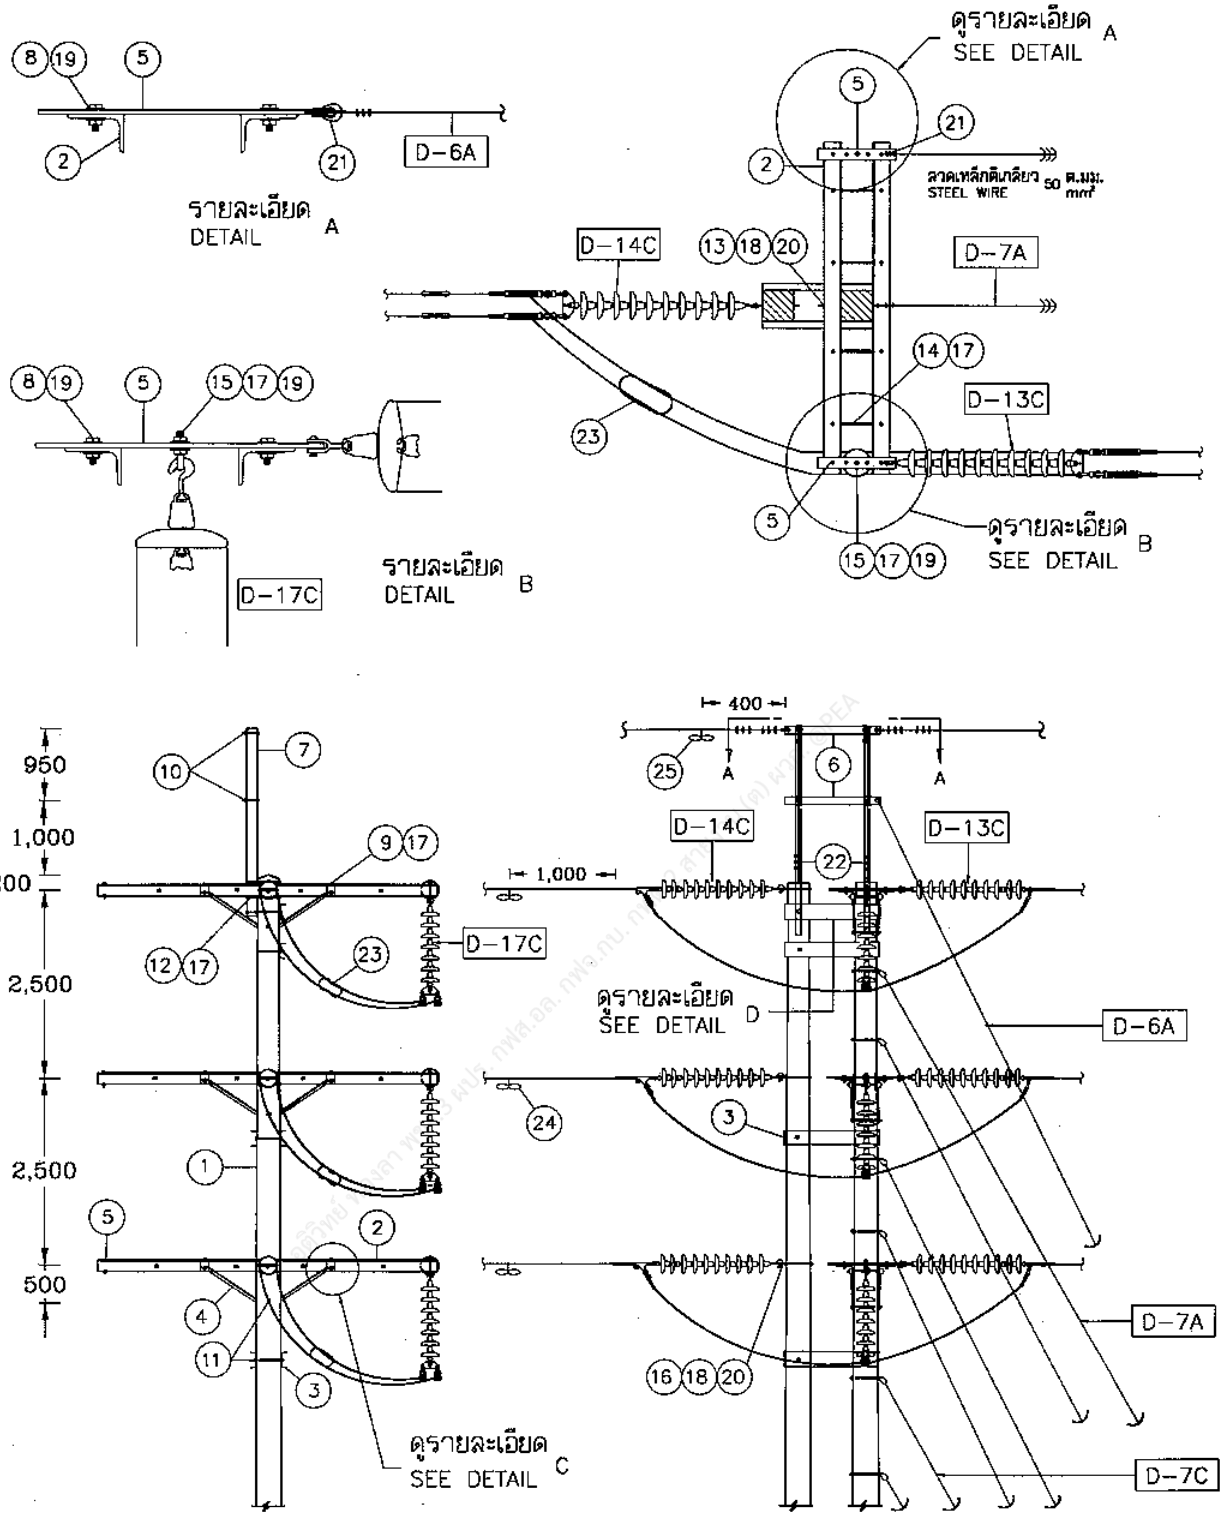


กองวิศวกรรมไฟฟ้าและเครื่องกล ฝ่ายวิศวกรรม	การไฟฟ้าส่วนภูมิภาค	ใช้แทนแบบ ..... ถูกแทนโดยแบบ .....
ผู้เขียน ..... ผู้สำรวจ ..... วิศวกร ..... หัวหน้าแผนก ..... ผู้อำนวยการกอง ..... ผู้อำนวยการฝ่าย	ผู้ว่าการ	เขียนเสร็จวันที่ 25 พ.ค. 43 แก้แบบวันที่ ..... มิติเป็น ..... มิลลิเมตร มาตราส่วน 1:100
รองผู้ว่าการเทคนิคและบริการ	115 kV วงจรเดี่ยว สายไฟฟ้าคู่ โครงสร้างเสาช่วงระยะไม่เกิน 200 เมตร แบบ SD-LS-2 115 kV SINGLE CIRCUIT DOUBLE CONDUCTOR SPAN ≤ 200 m STRUCTURE TYPE SD-LS-2	แบบเลขที่ SA1-015/43003 แผ่นที่ 2 ของจำนวน 6 แผ่น


การประกอบเลขที่ ASSEMBLY NO. 5288

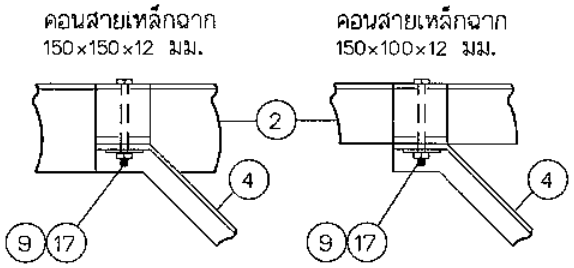

รายละเอียด DETAIL C

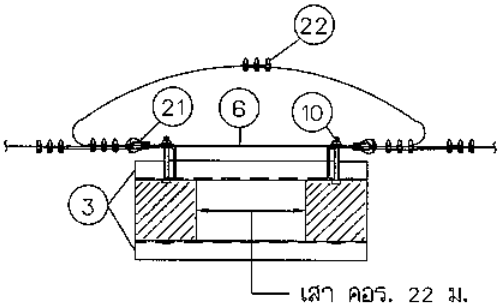


รูปตัด SECTION A–A

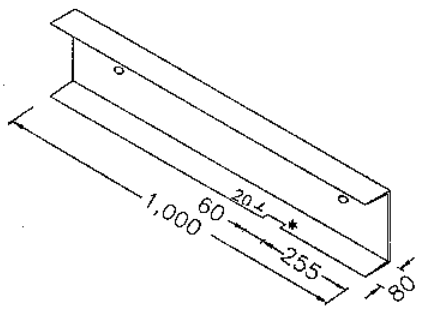


* ดัดแปลงเพิ่มเติมจากวัสดุเลขที่ 01000400

รายละเอียด DETAIL D

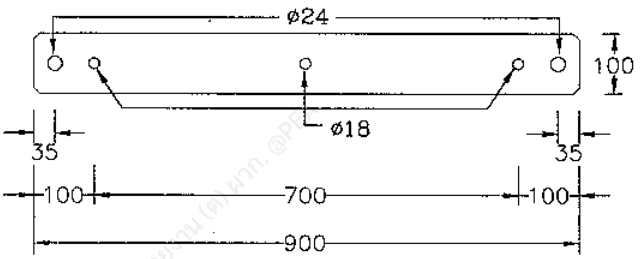


วัสดุลำดับที่ MAT.NO. (6)

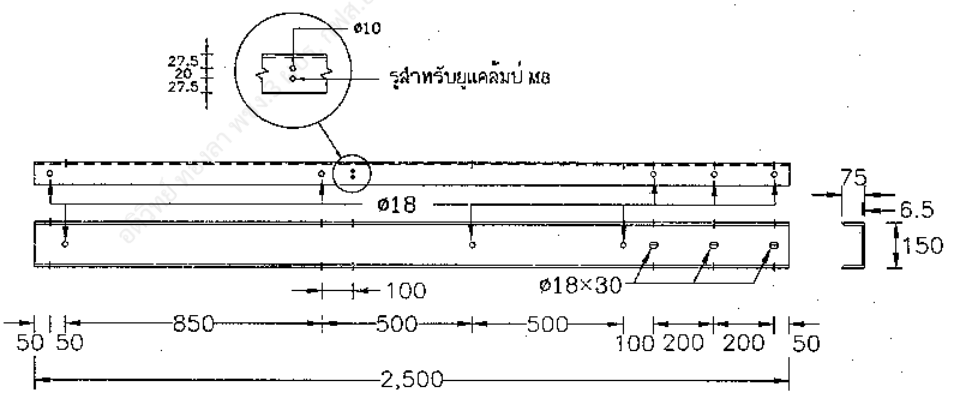

วัสดุลำดับที่ MAT.NO. (7)

กองวิศวกรรมไฟฟ้าและเครื่องกล ฝ่ายวิศวกรรม	การไฟฟ้าส่วนภูมิภาค	ใช้แทนแบบ ..... ถูกแทนโดยแบบ .....
ผู้เขียน สมนึก สาคร ผู้สำรวจ ..... วิศวกร ..... หัวหน้าแผนก ..... ผู้อำนวยการกอง ..... ผู้อำนวยการฝ่าย	ผู้ว่าการ ..... (ถกม)	เขียนเสร็จวันที่ 25 พ.ค.43 แก้แบบวันที่ ..... มิติเป็น มิลลิเมตร มาตราส่วน 1 : 25
รองผู้ว่าการเทคนิคและบริการ ..... (ถกม)	115 kV วงจรเดี่ยว สายไฟฟ้าคู่ โครงสร้างเสาช่วงระยะไม่เกิน 200 เมตร แบบ SD–LS–2 115 kV SINGLE CIRCUIT DOUBLE CONDUCTOR SPAN ≤ 200 m STRUCTURE TYPE SD–LS–2	แบบเลขที่ SA1–015/43003 แผ่นที่ 3 ของจำนวน 6 แผ่น

การประกอบเลขที่
ASSEMBLY NO. 5288

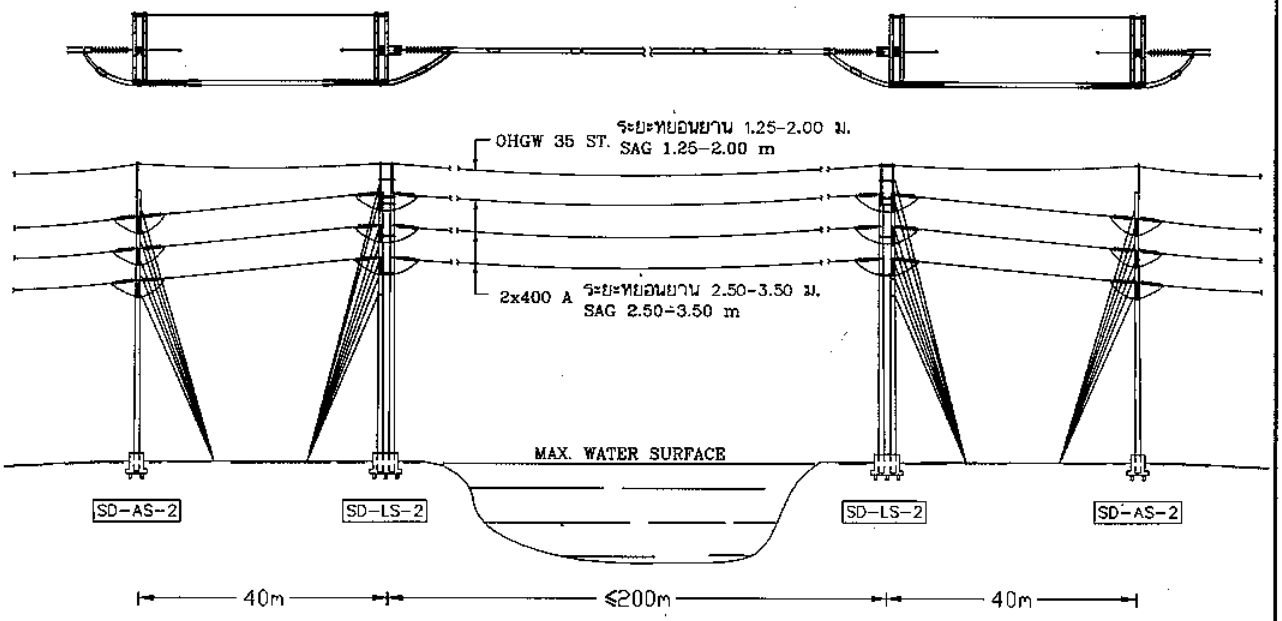

ลักษณะการใช้งาน
APPLICATION

ข้อกำหนดการใช้งาน

1. กรณีแม่น้ำนั้นมีสะพานข้ามแม่น้ำขนานไปกับแนวสายส่ง , ระยะห่างต่ำสุดตามแนวระดับระหว่างสายไฟฟ้ากับขอบสะพานไม่น้อยกว่า 4.5 ม. และระยะต่ำสุดในแนวดิ่งของสายไฟฟ้าเส้นล่างสุดที่ระยะหย่อนยานสายสูงสุด ต้องอยู่สูงกว่าส่วนสูงสุดของท้องคานสะพานไม่น้อยกว่า 3.9 ม.
2. กรณีแม่น้ำนั้นไม่มีสะพานข้ามแม่น้ำ และเรือที่สัญจรผ่านมีความสูงไม่เกิน 8 ม.
3. หากพิจารณาตรวจสอบสถานที่แล้วไม่เป็นไปตามข้อกำหนด 1 และ 2 ดังกล่าวข้างต้น ต้องพิจารณาออกแบบเฉพาะใหม่เป็นแห่งๆไป

RECOMMENDATION

1. IN CASE OF THERE IS A BRIDGE PARALLEL WITH 115 kV LINE , THE MINIMUM HORIZONTAL CLEARANCE BETWEEN CONDUCTOR AND THE EDGE OF BRIDGE IS 4.5 m AND THE VERTICAL CLEARANCE OF THE LOWEST CONDUCTOR AT MAXIMUM SAG SHALL BE HIGHER THAN THE HIGHEST POINT ON BOTTOM OF THE BRIDGE BEAM NOT LESS THAN 3.9 m .
2. IN CASE OF NO BRIDGES , THE HEIGHT OF BOATS PASSING NOT MORE THAN 8 m .
3. OTHER CASES , NEW DESIGN IS NEEDED .

กองวิศวกรรมไฟฟ้าและเครื่องกล ฝ่ายวิศวกรรม	การไฟฟ้าส่วนภูมิภาค	ใช้แทนแบบ ..... ถูกแทนโดยแบบ .....
ผู้เขียน .....สมนึก...สาคร.. ผู้สำรวจ ..... วิศวกร..... หัวหน้าแผนก..... ผู้อำนวยการกอง..... ผู้อำนวยการฝ่าย.....	ผู้ว่าการ..... (นายช)	เขียนเสร็จวันที่ 25 พ.ค. 43 แก้แบบวันที่ ..... มิติเป็น ..... มาตราส่วน .....
	115 kV วงจรเดี่ยว สายไฟฟ้าคู่ โครงสร้างเสาช่วงระยะไม่เกิน 200 เมตร แบบ SD-LS-2	
รองผู้ว่าการเทคนิคและบริการ ..... (นายช)	115 kV SINGLE CIRCUIT DOUBLE CONDUCTOR SPAN ≤ 200 m STRUCTURE TYPE SD-LS-2	แบบเลขที่ SA1-015/43003 แผ่นที่ 4 ของจำนวน 6 แผ่น

การประกอบเลขที่ ASSEMBLY NO. 5288

บัญชีวัสดุเสาต้น P1–P2
BILL OF MATERIAL OF P1–P2 POLE

ลำดับที่ ITEM	รายละเอียด DESCRIPTION	จำนวน REQ'D	วัสดุเลขที่ MAT. NO.
1	เสาคอนกรีต 22 ม. POLE, CONCRETE, 22 m LONG	2	00010011
2	คอนสายแบบเหล็กฉาก ขนาด 150x100x12 มม. ยาว 4.50 ม. หรือ ขนาด 150x150x12 มม. ยาว 4.50 ม. CROSSARM,STEEL ANGLE,150x100x12 mm.,4.50 m LONG or STEEL ANGLE, 150x150x12 mm.,4.50 m LONG	6	00120002
3	เหล็กรูปรางน้ำ ขนาด 200x80x7.5 มม. ยาว 1,000 มม. STEEL CHANNEL, 200x80x7.5 mm 1,000 mm LONG	6	01000400
4	เหล็กฉากรับคอนสาย ขนาด 50x50x6 มม. ช่วงกว้าง 1,800 มม. ดรอพ 450 มม. BRACE, ANGLE STEEL 50x50x6 mm, 1,800 mm WIDE ,450 mm DROP	6	01200007
5	แผ่นเหล็กยึนสองปลาย ขนาด 12x100x760 มม. PLATE,STEEL,DOUBLE ARMING,12x100x760 mm	6	01030102
6	แผ่นเหล็ก ขนาด 6x100 มม. ยาว 900 มม. PLATE,STEEL, 6x100 mm, 900 mm LONG	2	–
7	เหล็กรูปรางน้ำรับสายล่อฟ้า ขนาด 150x75x6.5 มม. ยาว 2,500 มม. OVERHEAD GROUND WIRE STEEL CHANNEL, 150x75x6.5 mm 2,500 mm LONG	2	–
8	สลักเกลียว M16x75 มม. พร้อมแหวนกลม 2 อัน BOLT, MACHINE, M16x75 mm COMPLETE WITH 2 ROUND WASHERS	12	01110400
9	สลักเกลียว M16x170 มม. BOLT, MACHINE M16x170 mm	12	01110201
10	สลักเกลียว M16x200 มม. BOLT, MACHINE M16x200 mm	4	01110202
11	สลักเกลียว M16x350 มม. BOLT, MACHINE M16x350 mm	9	01110205
12	สลักเกลียว M16x450 มม. BOLT, MACHINE M16x450 mm	6	01110207
13	สลักเกลียว M20x350 มม. BOLT, MACHINE M20x350 mm	3	01110300
14	สลักเกลียวตลอด M16x400 มม. BOLT, DOUBLE ARMING, M16x400 mm	12	01120000
15	สลักห่วงโอเวล M16x150 มม. [เพิ่มนัทอีกหนึ่งอัน] BOLT, OVAL EYE M16x150 mm [ADD ONE SQUARE NUT]	3	01150000
16	สลักห่วงโอเวล M20x350 มม. BOLT, OVAL EYE M20x350 mm	3	01150100
17	แหวนสี่เหลี่ยมแบน 52x52x4.5 มม. รู ø18 มม. มอก.258 WASHER, SQUARE, FLAT, 52x52x4.5 mm, HOLE ø18 mm, TIS 258	70	01180100
18	แหวนสี่เหลี่ยมแบน 62x62x6 มม. รูø22 มม. มอก.258 WASHER, SQUARE, FLAT, 62x62x6 mm, HOLE ø22 mm, TIS 258	12	01180101
19	แหวนสปริง M16 ประเภทใช้งานทั่วไป มอก. 259 WASHER, LOCK, M16 GENERAL PURPOSE, TIS 259	15	01180301
20	แหวนสปริง M 20 มอก. 259 WASHER, LOCK, SPRING, SIZE 20 mm, GENERAL PURPOSE, TIS 259	6	01180302

กองวิศวกรรมไฟฟ้าและเครื่องกล ฝ่ายวิศวกรรม	การไฟฟ้าส่วนภูมิภาค	ใช้แทนแบบ ..... ถูกแทนโดยแบบ .....
ผู้เขียน ...สมนึก สาครฯ... ผู้สำรวจ ..... วิศวกร ..... หัวหน้าแผนก ..... ผู้อำนวยการกอง ..... ผู้อำนวยการฝ่าย	ผู้ว่าการ ..... (แทน)	เขียนเสร็จวันที่ 25 พ.ค. 43 แก้แบบวันที่ ..... มิติเป็น ..... มาตราส่วน .....
รองผู้ว่าการเทคนิคและบริการ ..... (แทน)	115 kV วงจรเดี่ยว สายไฟฟ้าคู่ โครงสร้างเสาช่วงระยะไม่เกิน 200 เมตร แบบ SD–LS–2 115 kV SINGLE CIRCUIT DOUBLE CONDUCTOR SPAN ≤ 200 m STRUCTURE TYPE SD–LS–2	แบบเลขที่ SA1–015/43003 แผ่นที่ 5 ของจำนวน 6 แผ่น

การประกอบเลขที่
ASSEMBLY NO. 5288

บัญชีวัสดุเสาต้น P1-P2
BILL OF MATERIAL OF P1-P2 POLE

ลำดับที่ ITEM	รายละเอียด DESCRIPTION	จำนวน REQ'D	วัสดุเลขที่ MAT. NO.
21	ทิมเบิลเคลวิส สำหรับปรีฟอร์มเข้าปลายสาย CLEVIS, THIMBLE, FOR PREFORMED DEADEND	6	03140011
22	ยูแคล้มป์ สลัก 1 ตัว เอ็ม 8 (ไวร์ โร้ป คลิ้พ) CLAMP, SINGLE U-BOLT, M. 8 (WIRE ROPE CLIP)	23	01230000
23	ปรีฟอร์มแยกสาย สำหรับสายอลูมิเนียม 400 ต.มม. SPACER,HELICAL ROD,PREFORMED,FOR AL 400 sq.mm.	6	02240000
24	ไวเบรชั่น แดมเปอร์ แบบดัมเบล สำหรับสายอลูมิเนียมเปลือย ขนาด 400 ต.มม. VIBRATION DAMPER TYPE DUMBBELL FOR BARE ALUMINIUM CONDUCTOR 400 mm^2	6	-
25	ไวเบรชั่น แดมเปอร์ แบบดัมเบล สำหรับสายลวดเหล็กตีเกลียว ขนาด 35 ต.มม. VIBRATION DAMPER TYPE DUMBBELL FOR STEEL STRAND WIRE 35 mm^2	1	-

ลำดับที่ ITEM	รายละเอียด DESCRIPTION	จำนวน REQ'D	
D-13C	การประกอบลูกถ้วยแขวน SUSPENSION INSULATOR ASSEMBLY	3	
D-14C	การประกอบลูกถ้วยแขวน SUSPENSION INSULATOR ASSEMBLY	3	
D-17C	การประกอบลูกถ้วยแขวน SUSPENSION INSULATOR ASSEMBLY	3	
D-6A	การประกอบยึดโยงลวดเหล็กตีเกลียว 50 ต.มม. STEEL STRANDED WIRE 50 mm^2, GUY ASSEMBLY	4	
D-7A	การประกอบยึดโยงลวดเหล็กตีเกลียว 95 ต.มม. STEEL STRANDED WIRE 95 mm^2, GUY ASSEMBLY	4	
D-7C	การประกอบยึดโยงลวดเหล็กตีเกลียว 95 ต.มม. STEEL STRANDED WIRE 95 mm, GUY ASSEMBLY	2	
D-9E	สมอบกคอนกรีต (อาจมีการเปลี่ยนแปลงเป็นแบบอื่น โดยขึ้นอยู่กับสภาพของดิน) CONCRETE ANCHOR (MAY BE CHANGED TO THE OTHER TYPE WHICH DEPEND ON SOIL CONDITION)	1	
D-10B	ฐานรากเสา (อาจมีการเปลี่ยนแปลงเป็นแบบอื่น โดยขึ้นอยู่กับสภาพของดิน) POLE FOUNDATION (MAY BE CHANGED TO THE OTHER TYPE WHICH DEPEND ON SOIL CONDITION)	1	

กองวิศวกรรมไฟฟ้าและเครื่องกล
ฝ่ายวิศวกรรม

ผู้เขียน สมนึก สาคร
ผู้สำรวจ .....
วิศวกร .....
หัวหน้าแผนก .....
ผู้อำนวยการกอง .....
ผู้อำนวยการฝ่าย .....

รองผู้ว่าการเทคนิคและบริการ
.....

การไฟฟ้าส่วนภูมิภาค

ผู้ว่าการ.....

115 kV วงจรเดี่ยว สายไฟฟ้าคู่
โครงสร้างเสาช่วงระยะไม่เกิน 200 เมตร
แบบ SD-LS-2

115 kV SINGLE CIRCUIT DOUBLE CONDUCTOR
SPAN ≤ 200 m STRUCTURE
TYPE SD-LS-2

ใช้แทนแบบ .....
ถูกแทนโดยแบบ .....
เขียนเสร็จวันที่ 25 พ.ค. 43
แก้แบบวันที่ .....
มิติเป็น .....
มาตราส่วน .....

แบบเลขที่ SA1-015/43003
แผ่นที่ 6 ของจำนวน 6 แผ่น