
การประกอบเลขที่	2706
ASSEMBLY NO.	3706

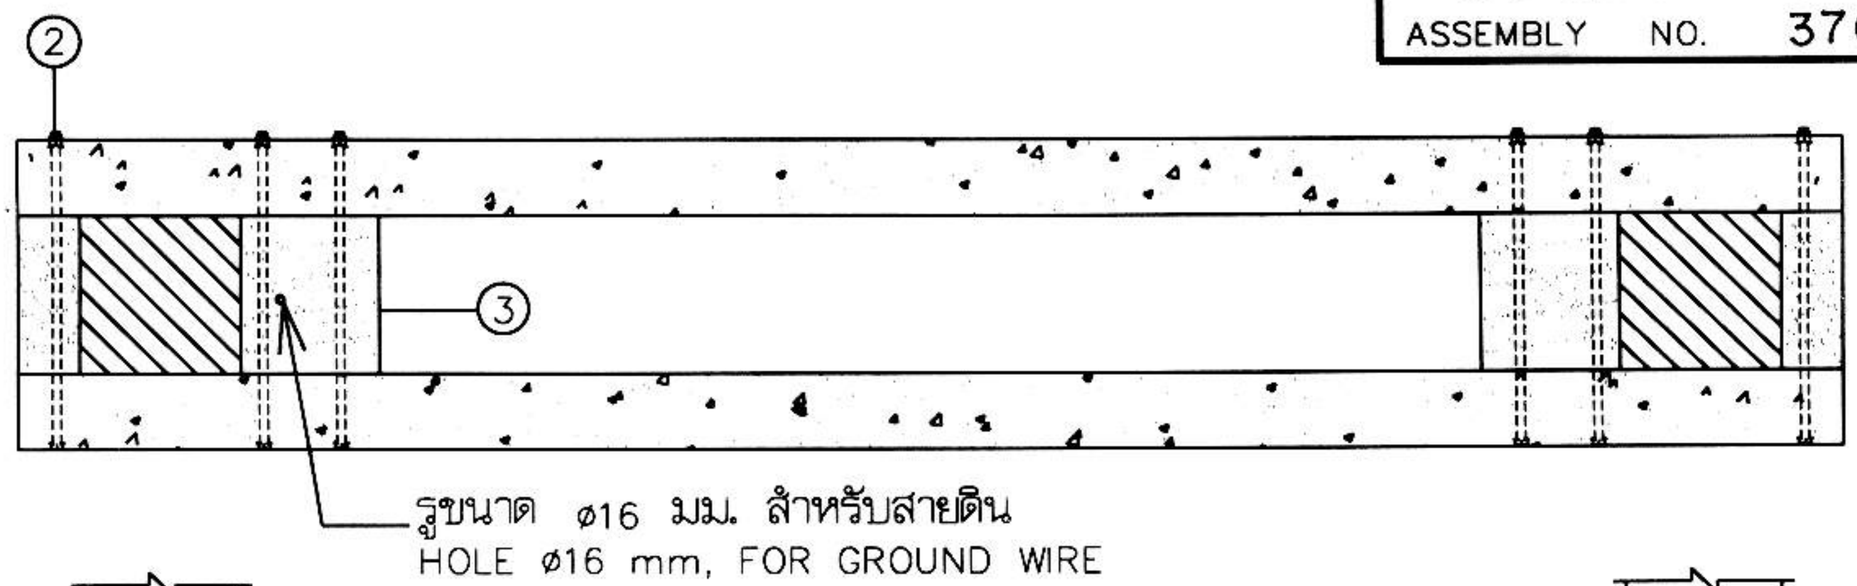

บัญชีวัสดุ
BILL OF MATERIAL

ลำดับที่ ITEM	รายละเอียด DESCRIPTION	จำนวน REQ'D	วัสดุเลขที่ MAT. NO.
1	คาน คอร. ขนาด 150 X 250 X 3,550 มม. สำหรับนั่งร้านหม้อแปลง PRESTRESSED CONCRETE BEAM,150 X 250 X 3,550 mm;FOR TRANSFORMER PLATFORM	2	
2	สลักเกลียวหัวหกเหลี่ยม M16 X 550 มม. (สำหรับเสา คอร. ขนาด 12 ม.) หรือ M16 X 600 มม. (สำหรับเสา คอร. ขนาด 12.20 ม. และ 14 ม.) หรือ M16 X 650 มม. (สำหรับเสา คอร. ขนาด 12.20 ม., 14 ม. และ 14.30 ม.) BOLT,MACHINE,HEXAGON, M16 X 550 mm (FOR 12 m CONCRETE POLE) OR M16 X 600 mm (FOR 12.20 m AND 14 m CONCRETE POLE) OR M16 X 650 mm (FOR 12.20 m, 14 m AND 14.30 m CONCRETE POLE)	12	01110401 01110402 or or
3	ปูนทราย 1:3 (ปูนซีเมนต์ผสมทรายหยาบ) MORTAR 1:3	50 กก. kg	

กองที่ดินและอาคาร ฝ่ายโยธาและสถาปัตย์	การไฟฟ้าส่วนภูมิภาค	ใช้แทนแบบ S02-015/19159 ถูกแทนโดยแบบ ..... เขียนเสร็จวันที่ 26. ก.ค. 2539 แก้แบบวันที่ ..... มิติเป็น ...มิลลิเมตร..... มาตราส่วน 1 : 25
ผู้เขียน ..... ผู้สำรวจ ..... วิศวกร ..... หัวหน้าแผนก ..... ผู้อำนวยการกอง ..... ผู้อำนวยการฝ่าย ..... รองผู้ว่าการ ..... - 5 ก.ค. 2539	ผู้ว่าการ ..... 5 ก.ค. 2539 การติดตั้ง คาน คอร. นั่งร้านหม้อแปลง สำหรับหม้อแปลง 3-เฟส ระบบ 22 kV และ 33 kV PRESTRESSED CONCRETE PLATFORM INSTALLATION FOR 3-PHASE TRANSFORMER 22 kV AND 33 kV SYSTEM	แบบเลขที่ IB2-015/39015 แผ่นที่ 1 ของจำนวน 2 แผ่น

การประกอบเลขที่	2706
ASSEMBLY NO.	3706

ข้อกำหนดในการใช้งาน

1. ขนาดหม้อแปลงที่ติดตั้งบนคาน คอร. นั่งร้านหม้อแปลง : 50–500 kVA (น้ำหนักต้องไม่เกิน 3,000 กก.)

2. สำหรับคาน คอร. นั่งร้านหม้อแปลงของเดิม ขนาด 150 X 250 X 3,450 มม. (วัสดุเลขที่ 00210001) สามารถประกอบใช้งานกับเสา คอร. ขนาด 12 ม. 12.20 ม. และ 14 ม. ได้

RECOMMENDATIONS

1. THE CAPACITY OF TRANSFORMER THAT INSTALLED ON PRESTRESSED CONCRETE PLATFORM : 50–500 kVA(WEIGHT SHALL NOT EXCEED 3,000 kg).

2. THE 150 X 250 X 3,450 mm PRESTRESSED CONCRETE BEAM (MAT. NO. 00210001) CAN BE ASSEMBLIED ON 12 m, 12.20 m AND 14 m POLE .

หมายเหตุ

1. บัญชีวัสดุใช้สำหรับการประกอบ คาน คอร. นั่งร้านหม้อแปลง เท่านั้น

2. การทำฐานรากเสา ดูแบบเลขที่ IB1–015/240032 (การประกอบเลขที่ 8503)

NOTES

1. BILL OF MATERIAL, USED ONLY FOR PRESTRESSED CONCRETE BEAM ASSEMBLY .

2. POLE FOUNDATION,SEE DWG. NO. IB1–015/240032 (ASSEMBLY NO. 8503) .

อติวิทย์ ทองสา พชง.3 ผปร. กฟส.อล. กฟต.สายงาน (ต) ผวก. @PEA

กองที่ดินและอาคาร ฝ่ายโยธาและสถาปัตย์	การไฟฟ้าส่วนภูมิภาค	ใช้แทนแบบ S02-015/19159
ผู้เขียน	ผู้ว่าการ ..... 17 ก.ย. 2539	ถูกแทนโดยแบบ .....
ผู้สำรวจ	การติดตั้ง คาน คอร. นั่งร้านหม้อแปลง สำหรับหม้อแปลง 3-เฟส ระบบ 22 kV และ 33 kV	เขียนเสร็จวันที่ 26. ก.ค. 2539
วิศวกร		แก้แบบวันที่ .....
หัวหน้าแผนก		มิติเป็น .....
ผู้อำนวยการกอง		มาตราส่วน .....
ผู้อำนวยการฝ่าย		
รองผู้ว่าการ ..... 6 ก.ย. 2539	PRESTRESSED CONCRETE PLATFORM INSTALLATION FOR 3–PHASE TRANSFORMER 22 kV AND 33 kV SYSTEM	แบบเลขที่ IB2-015/39015 แผ่นที่ 2 ของจำนวน 2 แผ่น