การประกอบเลขที่ 0213
ASSEMBLY NO.

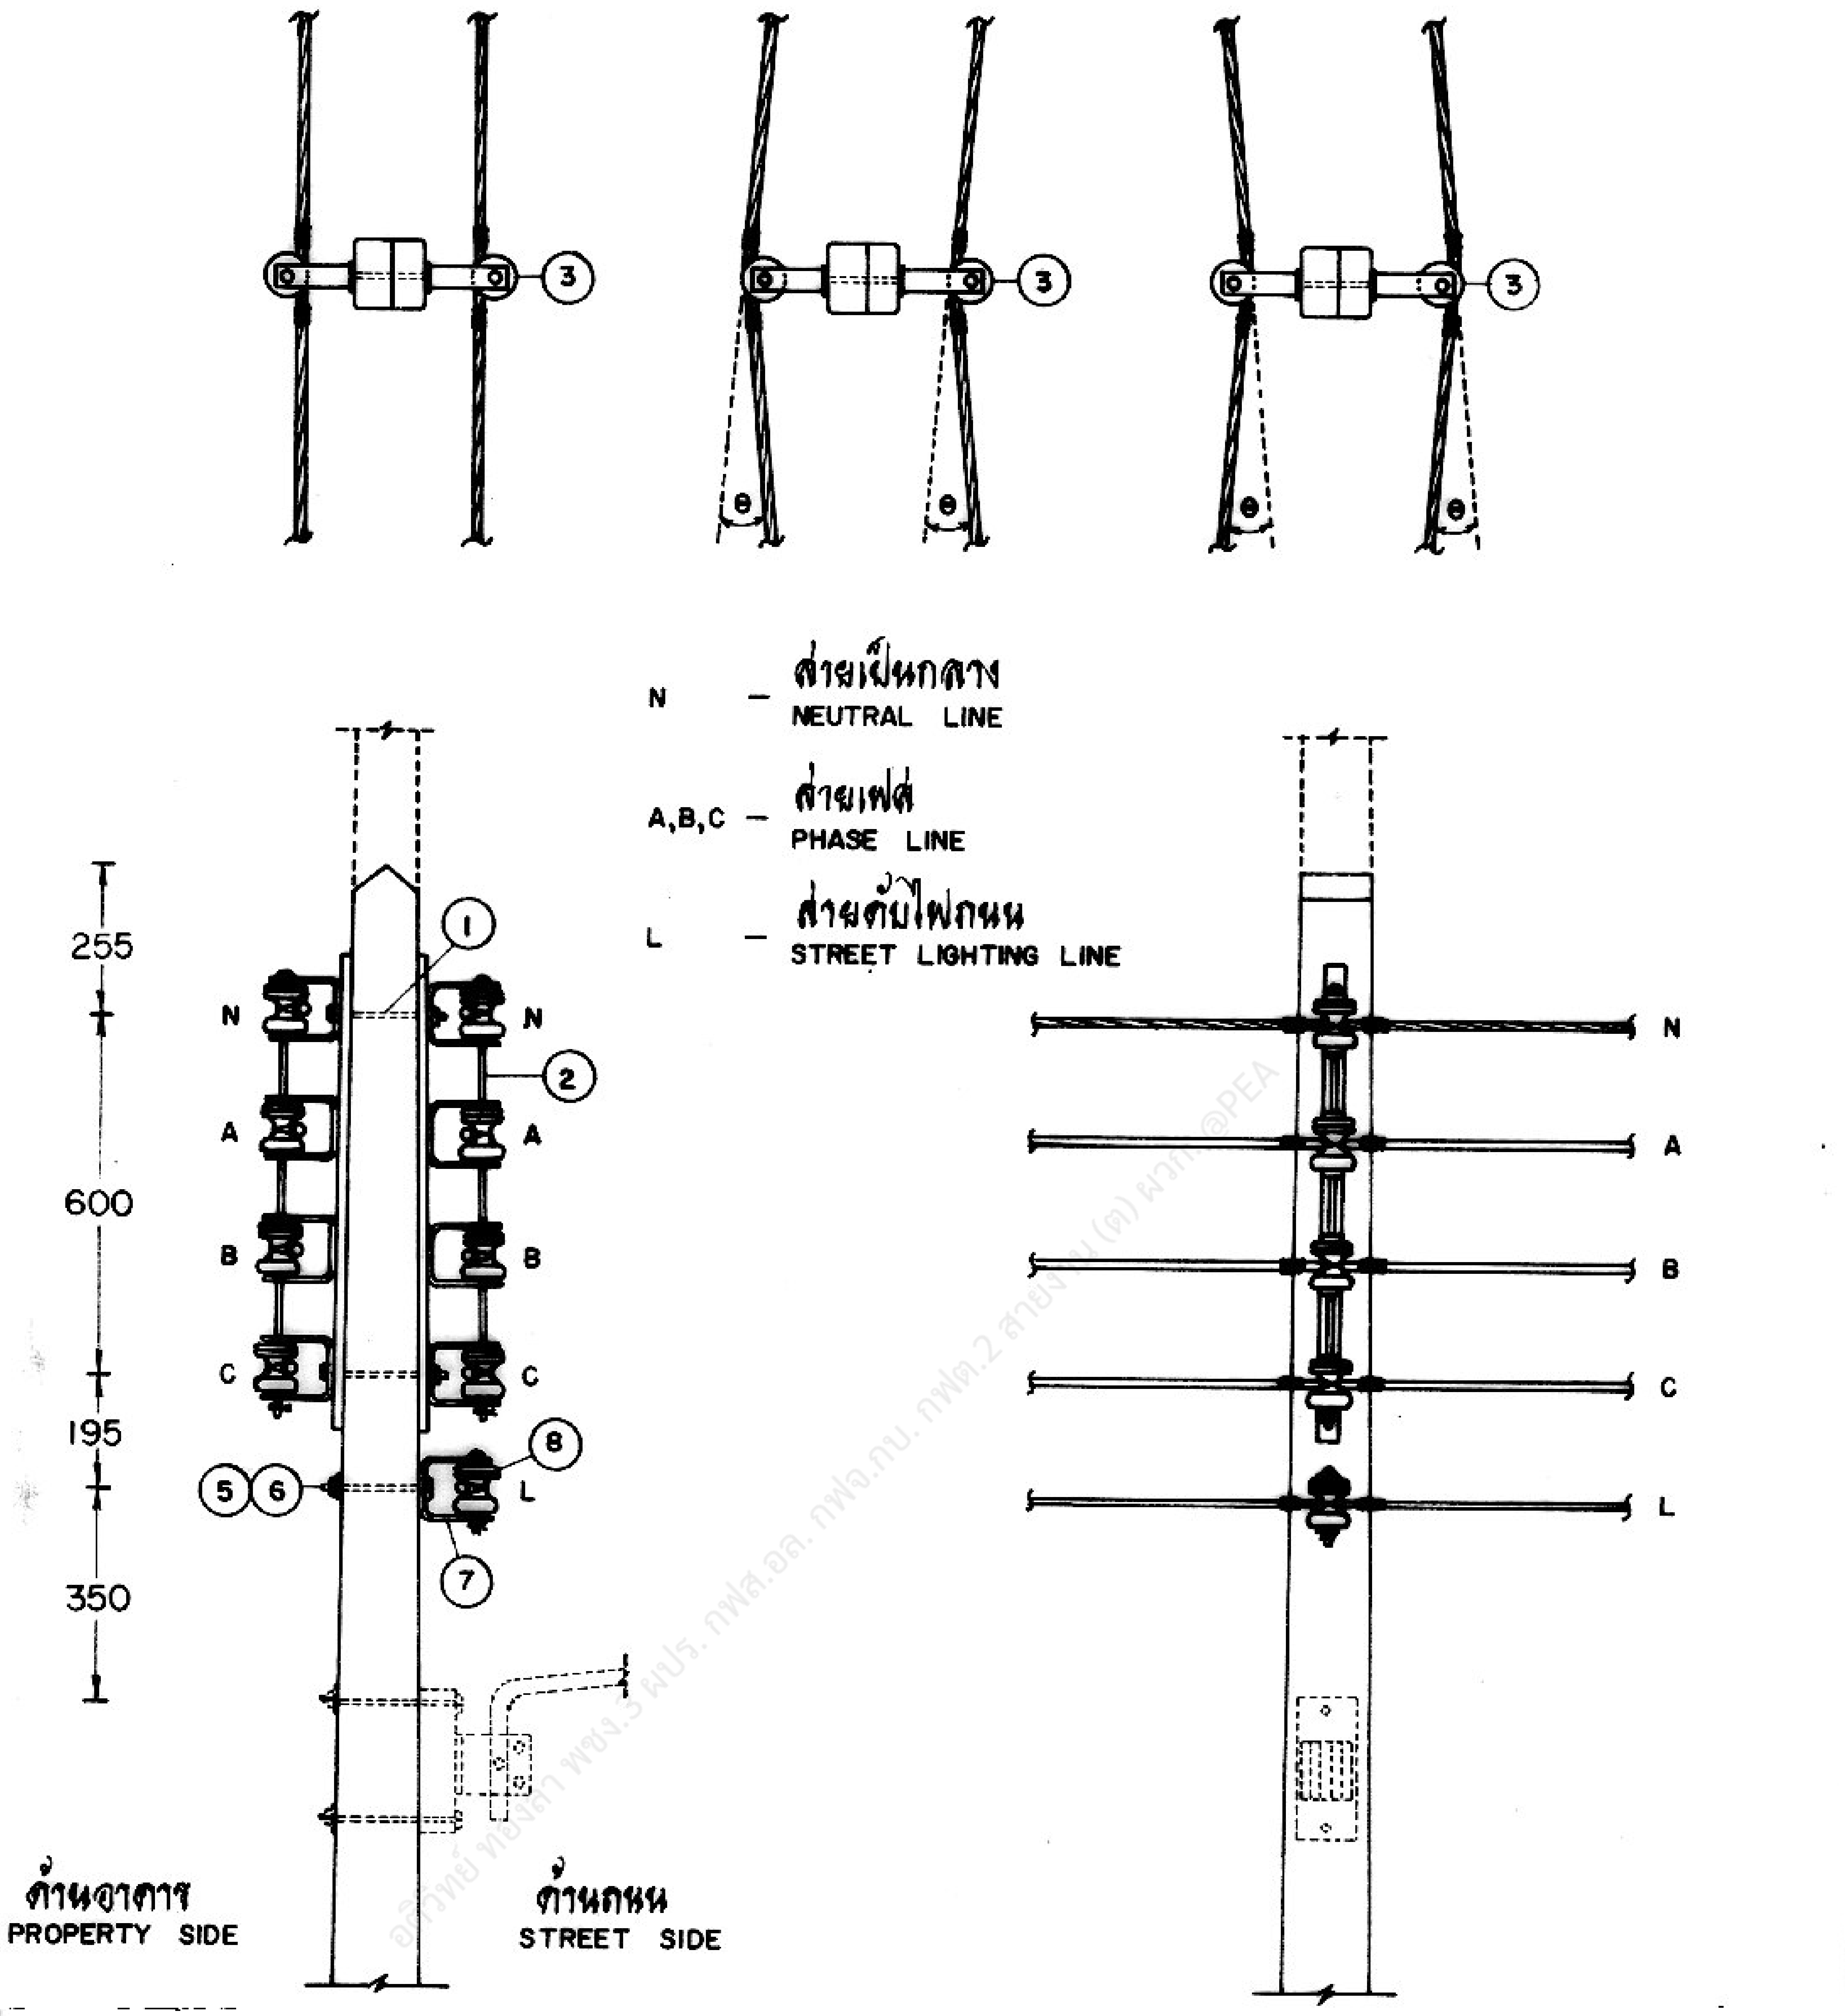

อภิวัฒน์ พ่อค้า พชง.3 ผปร. กฟส.อล. กฟจ.กบ. กฟต.2 สายงาน(ต) ผวก. @PEA

แบบ 3 เฟส 4 สาย 2 วงจร
3-PHASE 4-WIRE 2-CIRCUIT

22

023

แผ่น

กองวิศวกรรมไฟฟ้าและเครื่องกล
ฝ่ายวิศวกรรม

ผู้เขียน สุเมธ
ผู้สำรวจ
วิศวกร กิตติพงษ์
หัวหน้าแผนก ธีรธัช
หัวหน้ากอง
ผู้อำนวยการฝ่าย
รองผู้ว่าการฝ่ายเทคนิค

การไฟฟ้าส่วนภูมิภาค

ผู้ว่าการ

การติดตั้งแร็คแรงต่ำกับเสาคอนกรีต 9 ม.
2 วงจร
ก สำหรับทางตรง 0°-5° (θ)

SECONDARY RACK INSTALLATION ON 9 m CONCRETE POLE
2-CIRCUITS
A FOR TANGENT STRUCTURE 0°-5° (θ)

ใช้แทนแบบ
ถูกแทนโดยแบบ
เขียนเสร็จวันที่ 12 เม.ย.
แก้แบบวันที่
ผิดเป็น ผม.
มาตราส่วน 1 : 20
แบบเลขที่ SA1-015/220
แผ่นที่ 1 ของจำนวน 3

1 ก.ย. 2522

การประกอบเลขที่ ASSEMBLY NO. 0213

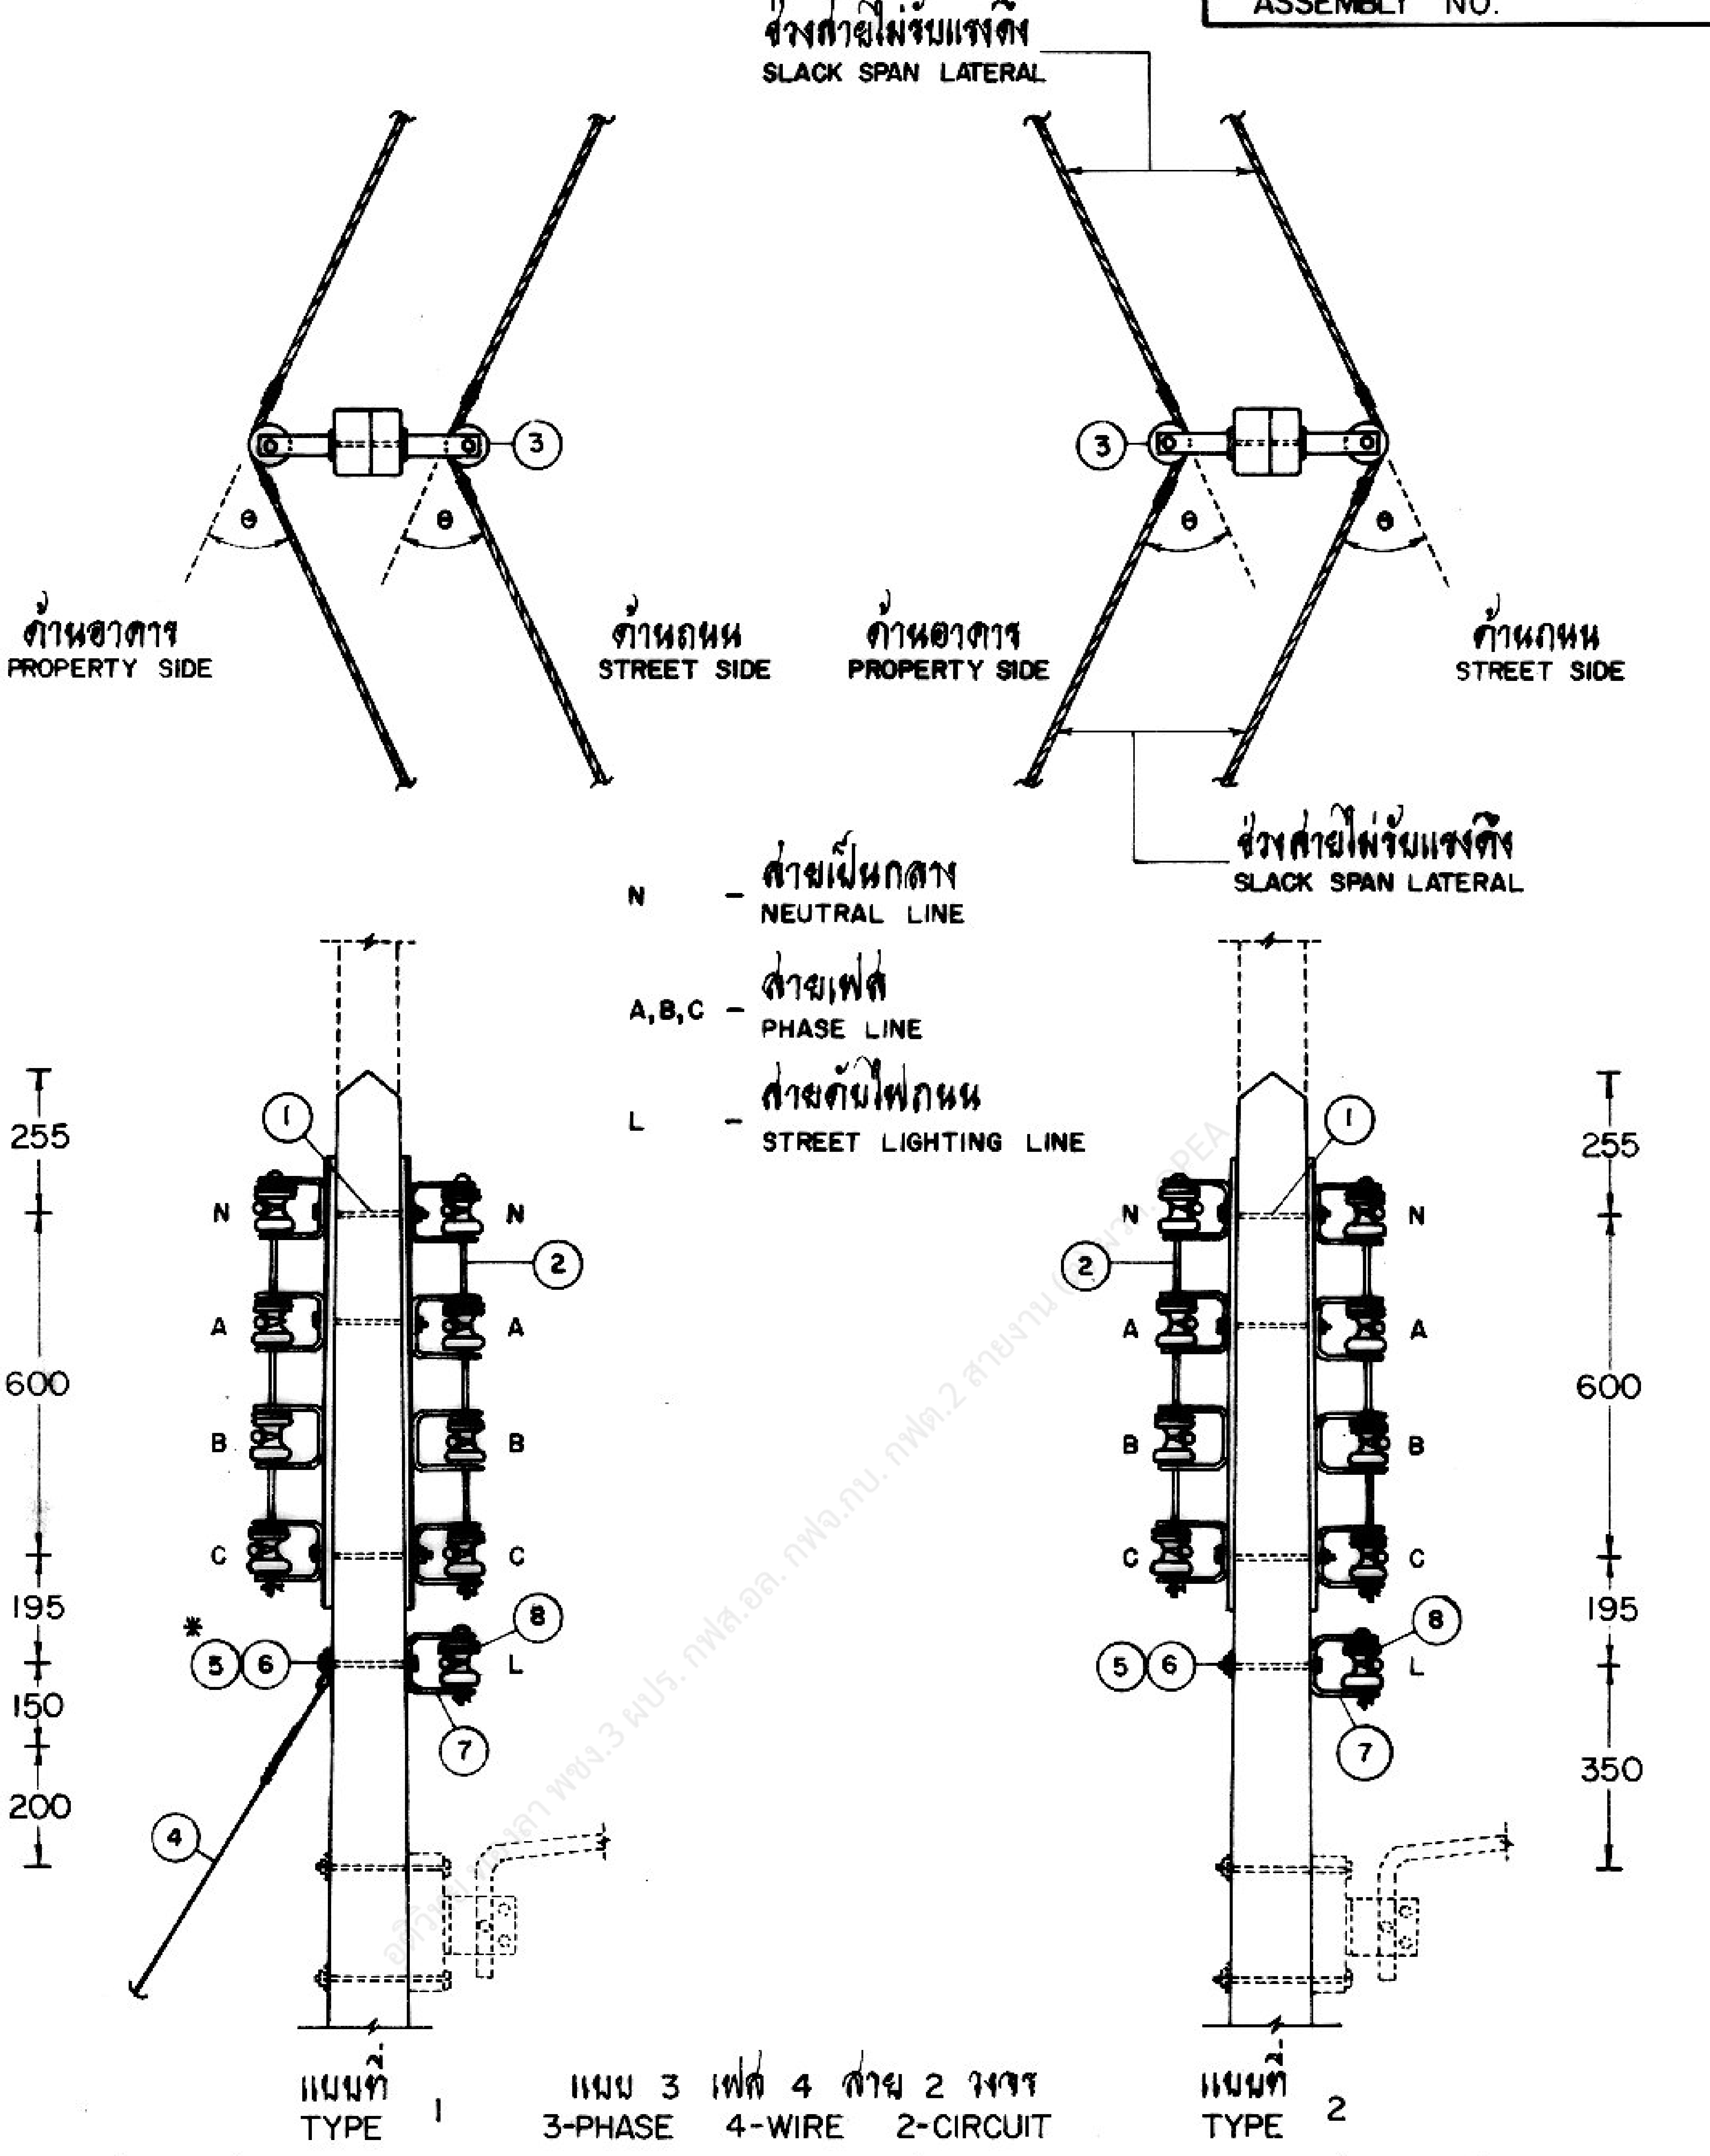

ในกรณีที่ไม่ติดตั้งสายดับไฟถนน การจัดทำสายยึดโยง ต้องเพิ่มสลักเกลียว รายการที่ 5 หนึ่งชุด และแหวนสี่เหลี่ยมแบนในรายการที่ 6 หนึ่งตัว

* IF THE STREET LIGHTING LINE IS NOT INSTALLED, ONE MACHINE BOLT ITEM 5 AND ONE SQUARE WASHER ITEM 6 SHALL BE ADDED FOR GUY ASSEMBLY.

กองวิศวกรรมไฟฟ้าและเครื่องกล
ฝ่ายวิศวกรรม

ผู้เขียน
ผู้สำรวจ
วิศวกร สิทธิพงษ์
หัวหน้าแผนก
หัวหน้ากอง
ผู้อำนวยการฝ่าย
รองผู้ว่าการฝ่ายเทคนิค

การไฟฟ้าส่วนภูมิภาค

ผู้ว่าการ

การติดตั้งแร็คแรงต่ำบนเสาคอนกรีต 9 ม.
2 วงจร
ข สำหรับทางโค้ง 5°-60° (θ)

SECONDARY RACK INSTALLATION ON 9 m CONCRETE POLE
2-CIRCUITS
B FOR ANGLE STRUCTURE 5°-60° (θ)

ใช้แทนแบบ
ถูกแทนโดยแบบ
เขียนเสร็จวันที่ 12 เม.ย. 22
แก้แบบวันที่
มิติเป็น มม.
มาตราส่วน 1 : 20
แบบเลขที่ SAI-015/22023
แผ่นที่ 2 ของจำนวน 3 แผ่น

7 ก.ย. 2522

การประกอบเลขที่ ASSEMBLY NO. 0213

บัญชีวัสดุ
BILL OF MATERIAL

ลำดับที่ ITEM	รายละเอียด DESCRIPTION	จำนวน REQ'D ก/A	ข/B 1	ข/B 2	วัสดุเลขที่ MAT. NO.
1	สลักเกลียว M 16 X 200 มม. BOLT, MACHINE, M 16 X 200 mm	2	3	3	01110202
1 a	สลักเกลียว M 16 X 300 มม. สำหรับเสาคอนกรีต 12 ม. BOLT, MACHINE, M 16 X 300 mm FOR 12 m CONCRETE POLE	2	3	3	01110204
2	แร็ค 4 X 200 มม. แบบหลังยื่น RACK, SECONDARY, MEDIUM PRESSED STEEL 4 X 200 mm EXTENDED BACK	2	2	2	03130002
3	ลูกรอกแรงต่ำ มอก. 227 แบบ ข (แบบ 53-2) INSULATOR, SPOOL TYPE, L.T. TIS 227 TYPE B (CLASS 53-2)	8	8	8	03030000
4	การประกอบสายยึดโยง GY-01 GUY ASSEMBLY GY-01	-	1	-	—
4 a	การประกอบสายยึดโยง GY-02 สำหรับเสาคอนกรีต 12 ม. GUY ASSEMBLY GY-02 FOR 12 m CONCRETE POLE	-	1	-	—
	สำหรับการติดตั้งสายคุมไฟถนน FOR STREET LIGHTING INSTALLATION				
5*	สลักเกลียว M 16 X 170 มม. BOLT, MACHINE, M 16 X 170 mm	1	1	1	01110201
5 a*	สลักเกลียว M 16 X 250 มม. สำหรับเสาคอนกรีต 12 ม. BOLT, MACHINE, M 16 X 250 mm FOR 12 m CONCRETE POLE	1	1	1	01110203
6*	แหวนสี่เหลี่ยมแบน 52 X 52 X 4.5 มม. รู Ø 18 มม. มอก. 258 WASHER, SQUARE, FLAT, 52 X 52 X 4.5 mm HOLE Ø 18 mm TIS 258	1	1	1	01180100
7	ที่จับลูกรอกสำหรับลูกรอก มอก.227 (แบบ 53-2) CLEVIS, FLAT STEEL, FOR INSULATOR TIS 227 (CLASS 53-2)	1	1	1	03030100
8	ลูกรอกแรงต่ำ มอก. 227 แบบ ข (แบบ 53-2) INSULATOR, SPOOL TYPE, L.T. TIS 227 TYPE B (CLASS 53-2)	1	1	1	03030000

คำแนะนำในการขึงสายระบบจำหน่ายทางโค้ง 5°-60° แบบที่ 2

1 ระยะช่วงสายไม่รับแรงดึง ไม่เกิน 20 ม.

2 ระยะหย่อนยานต่ำสุดของสาย 50,70 และ 95 ต.มม. เท่ากับ 0.80, 0.90 และ 1.00 ม. ตามลำดับ

SUGGESTION FOR ANGLE STRUCTURE 5°-60°, TYPE 2

1 MAXIMUM SLACK SPAN LATERAL 20 m.

2. MINIMUM SAG OF 50, 70 AND 95 mm^2 CONDUCTOR SHALL BE 0.80, 0.90 AND 1.00 m RESPECTIVELY.

กองวิศวกรรมไฟฟ้าและเครื่องกล ฝ่ายวิศวกรรม	การไฟฟ้าส่วนภูมิภาค	ใช้แทนแบบ ถูกแทนโดยแบบ เขียนเสร็จวันที่ 12 เม.ย. 22
ผู้เขียน ผู้ตรวจ วิศวกร หัวหน้าแผนก หัวหน้ากอง ผู้อำนวยการฝ่าย	ผู้ว่าการ การติดตั้งแร็คแรงต่ำกับเสาคอนกรีต 9 ม. 2 วงจร	แก้แบบวันที่ มิติเป็น มาตราส่วน
รองผู้ว่าการฝ่ายเทคนิค	SECONDARY RACK INSTALLATION ON 9 m CONCRETE POLE 2-CIRCUITS	แบบเลขที่ SAI-015/22023 แผ่นที่ 3 ของจำนวน 3 แผ่น