


การประกอบเลขที่ ASSEMBLY NO. 3802

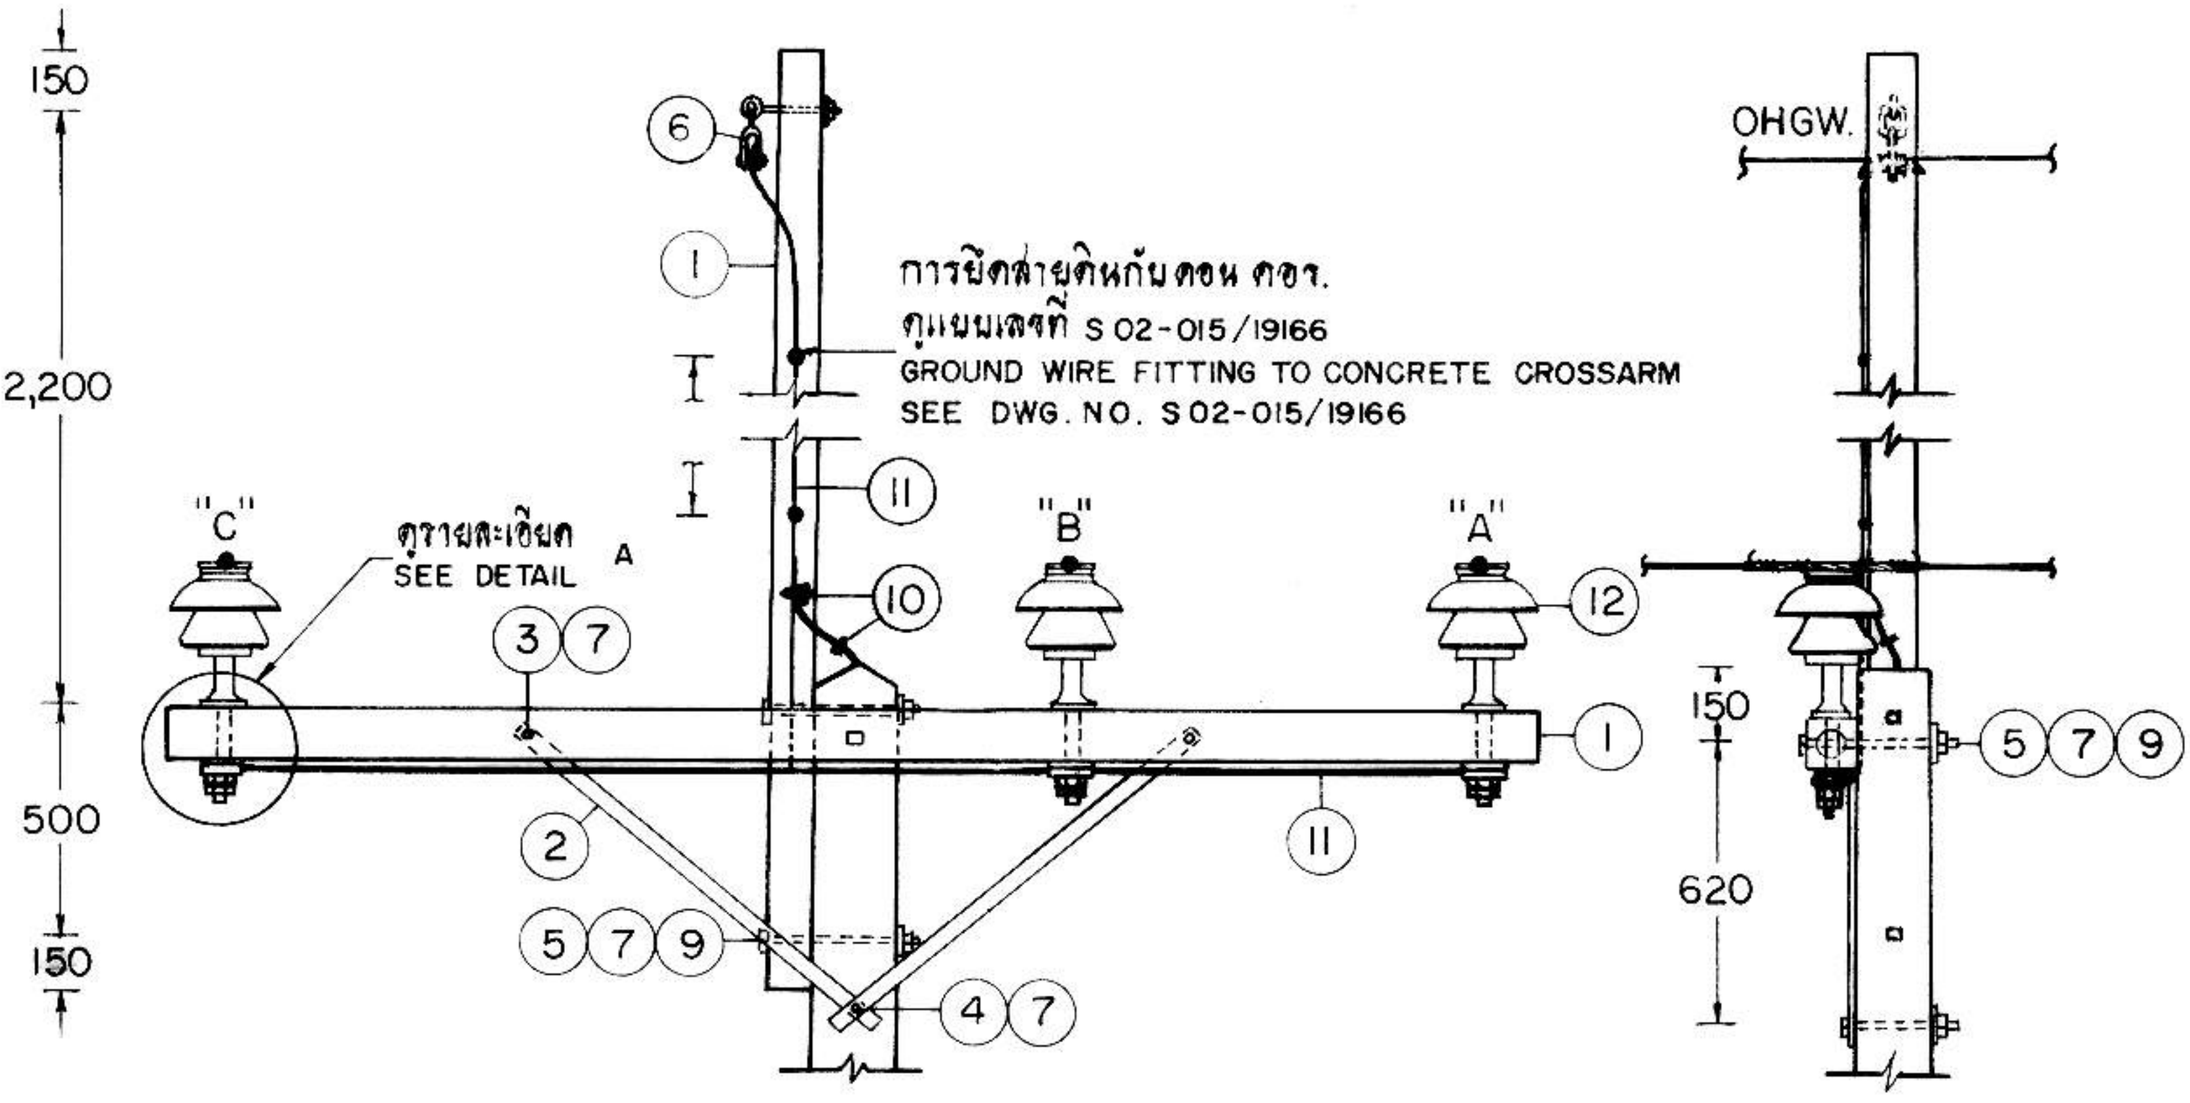

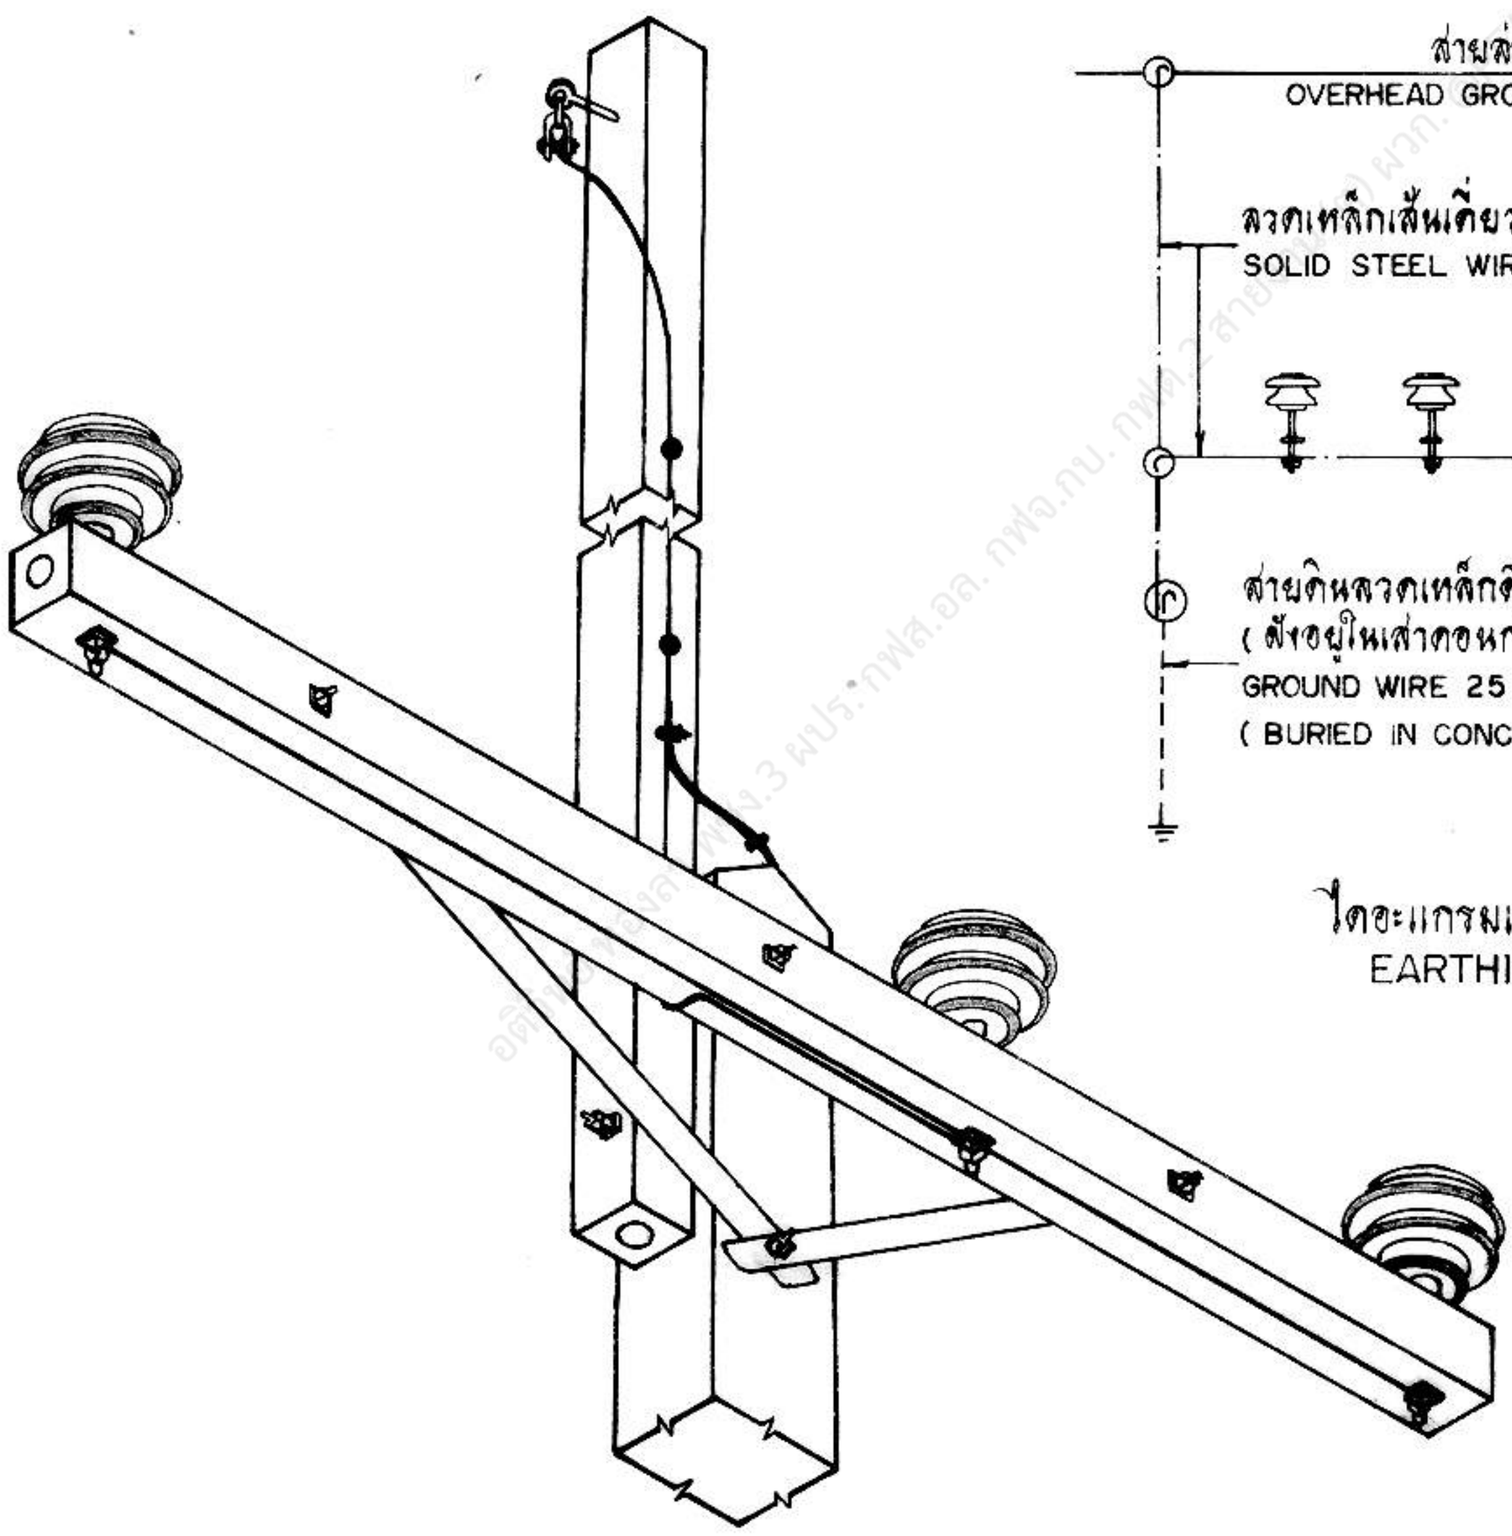


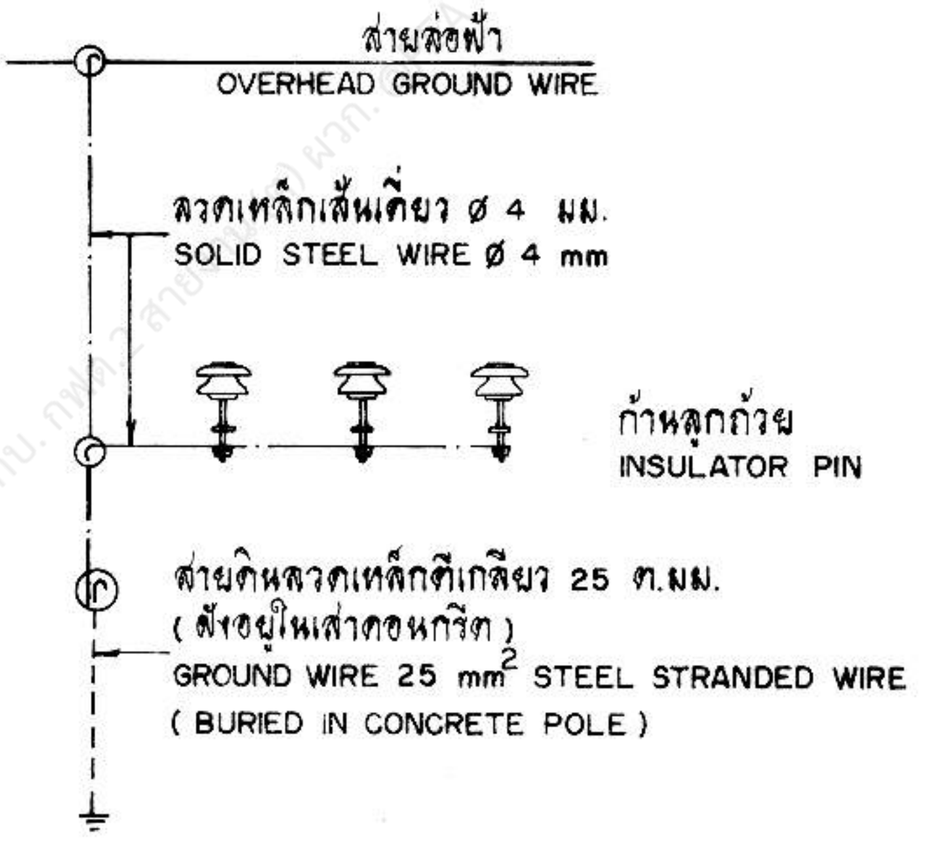


ไดอะแกรมแสดงการต่อลงดิน
EARTHING DIAGRAM

กองวิศวกรรม	การไฟฟ้าส่วนภูมิภาค	ใช้แทนแบบ
ผู้เขียน ผู้สำรวจ วิศวกร หัวหน้าแผนก หัวหน้ากอง	ผู้ว่าการ การประกอบคอน คอร. สปัน กันเสาคอนกรีต ระดับ 33 kV ทางตรงมุม 0°-5°	ถูกแทนโดยแบบ เขียนเสร็จวันที่ 18 มี.ค. 20 แก้แบบวันที่ 24 เม.ย. 21 มิติเป็น มม. มาตราส่วน 1:25, 1:30 แบบเลขที่ S02-015/20045
รองผู้ว่าการฝ่ายเทคนิค	SPUN PRESTRESSED CONCRETE CROSSARM ASSEMBLY 33 kV SYSTEM TANGENT STRUCTURE 0°-5°	แผ่นที่ 1 ของจำนวน 2 แผ่น

การประกอบเลขที่ ASSEMBLY NO. **3802**

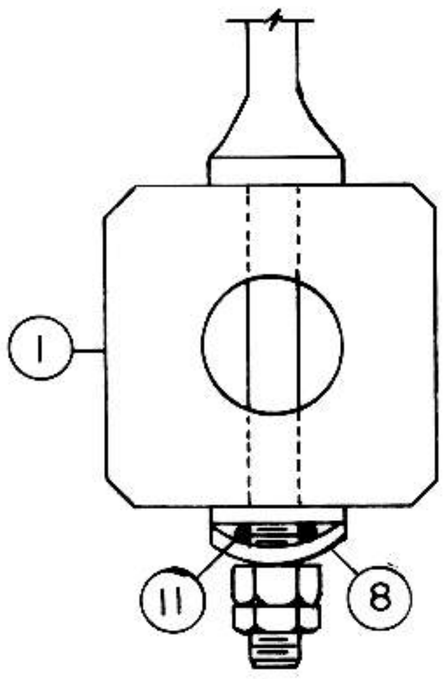

รายละเอียด A
DETAIL

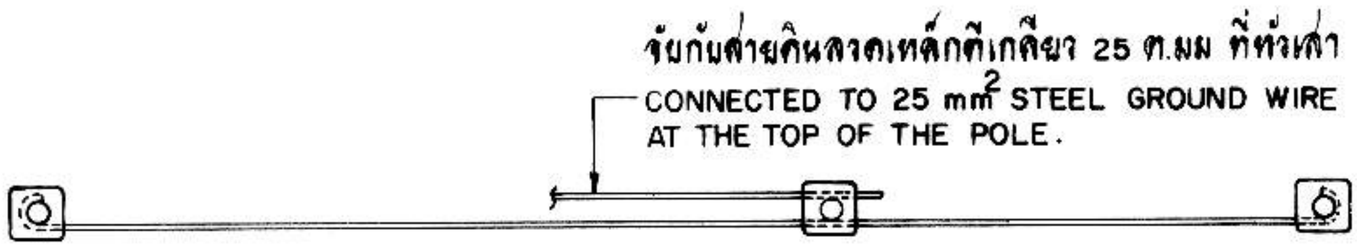

การโค้งดัดสายดินลวดเหล็กเส้นเดียว Ø 4 มม.
ต่อระหว่างก้านลูกถ้วย ประกอบที่คอน คอร. สปัน
THE ARRANGEMENT OF Ø 4 mm GALVANIZED
STEEL WIRE BOND BETWEEN INSULATOR PINS

บัญชีวัสดุ
BILL OF MATERIAL

ลำดับที่ ITEM	รายละเอียด DESCRIPTION	จำนวน REQ'D ก /A	จำนวน REQ'D ข /B	วัสดุเลขที่ MAT. NO.
1	คอน คอร.สปัน ขนาด 120 X 120 X 3,000 มม. CROSSARM, SPUN, PRESTRESSED CONCRETE 120 X 120 X 3,000 mm	2	2	00110002
2	เหล็กประกับไม้คอน ขนาด 40 X 6 X 1,000 มม. BRACE, FLAT, FOR CROSSARM 40 X 6 X 1,000 mm	2	2	01200002
3	สลักเกลียว M 16 X 170 มม. BOLT, MACHINE, M 16 X 170 mm	2	2	01110201
4	สลักเกลียว M 16 X 200 มม. BOLT, MACHINE, M 16 X 200 mm	1	1	01110202
5	สลักเกลียว M 16 X 350 มม. BOLT, MACHINE, M 16 X 350 mm	3	3	01110205
6	กราวด์วายร์แคล้มป์ สำหรับไม้คอนสาย GROUND WIRE SUPPORT AND CLAMP, FOR WOOD BAYONET	1	1	01230200
7	แหวนสี่เหลี่ยมแผน ขนาด 52 X 52 X 4.5 มม. รู Ø 18 มม. มอก. 258 WASHER, SQUARE, FLAT 52 X 52 X 4.5 mm HOLE Ø 18 mm TIS 258	9	9	01180100
8	แหวนสี่เหลี่ยมโค้ง ขนาด 60 X 60 X 5 มม. รู Ø 22 มม. WASHER, SQUARE, CURVED 60 X 60 X 5 mm HOLE Ø 22 mm	1	3	01180201
9	แหวนสปริง M 16 มอก. 259 WASHER, LOCK, M 16 TIS 259	3	3	01180301
10	ยูแคล้มป์ สลัก 1 ตัว M 8 (ไวร์ โรป คลิ๊ฟ) CLAMP, SINGLE U-BOLT M 8 (WIRE ROPE CLIP)	2	2	01230000
11	ลวดเหล็กกลม เส้นผ่าศูนย์กลาง 4 มม. เส้นเดียว (มอก. 71) น้ำหนักประมาณ 0.1 กก./ม. WIRE, STEEL, SOLID, DIAMETER 4 mm (TIS 71) WEIGHT 0.1 kg/m	3.5 ม. m	6.5 ม. m	01100000
12	ลูกถ้วยก้านตรง 33 kV มอก. 279 แบบ ค (แบบ 56-3) พร้อมก้าน INSULATOR, PIN TYPE, 33 kV, TIS 279 TYPE C (CLASS 56-3) COMP. WITH PIN	1	3	03000002 03100001

หมายเหตุ
1. ก ระบบ 1 เฟส 19 kV ข ระบบ 3 เฟส 33 kV
2. การก่อสร้างระบบ 1 เฟส 19 kV ให้ติดตั้งลูกถ้วยที่ตำแหน่งเฟส B

NOTES
1. A FOR 1 PHASE 19 kV SYSTEM, B FOR 3-PHASE 33 kV SYSTEM.
2. FOR 1-PHASE 19 kV SYSTEM FIX INSULATOR AT PHASE "B" POSITION.

กองวิศวกรรม	การไฟฟ้าส่วนภูมิภาค	ใช้แทนแบบ .....
ผู้เขียน	ผู้ว่าการ	ถูกแทนโดยแบบ .....
ผู้สำรวจ		เขียนเสร็จวันที่ 18 มี.ค. 20
วิศวกร	การประกอบคอน คอร. สปัน กันเสาคอนกรีต	แก้แบบวันที่ 24 เม.ย. 21
หัวหน้าแผนก	ระบบ 33 kV	มิติเป็น .....
หัวหน้ากอง	ทางตรงมุม 0°-5°	มาตราส่วน .....
รองผู้ว่าการฝ่ายเทคนิค	SPUN PRESTRESSED CONCRETE CROSSARM ASSEMBLY 33 kV SYSTEM TANGENT STRUCTURE 0°-5°	แบบเลขที่ S 02-015/20045
		แผ่นที่ 2 ของจำนวน 2 แผ่น