
D—10D TYPE 1

การประกอบเลขที่ ASSEMBLY NO. **5684**

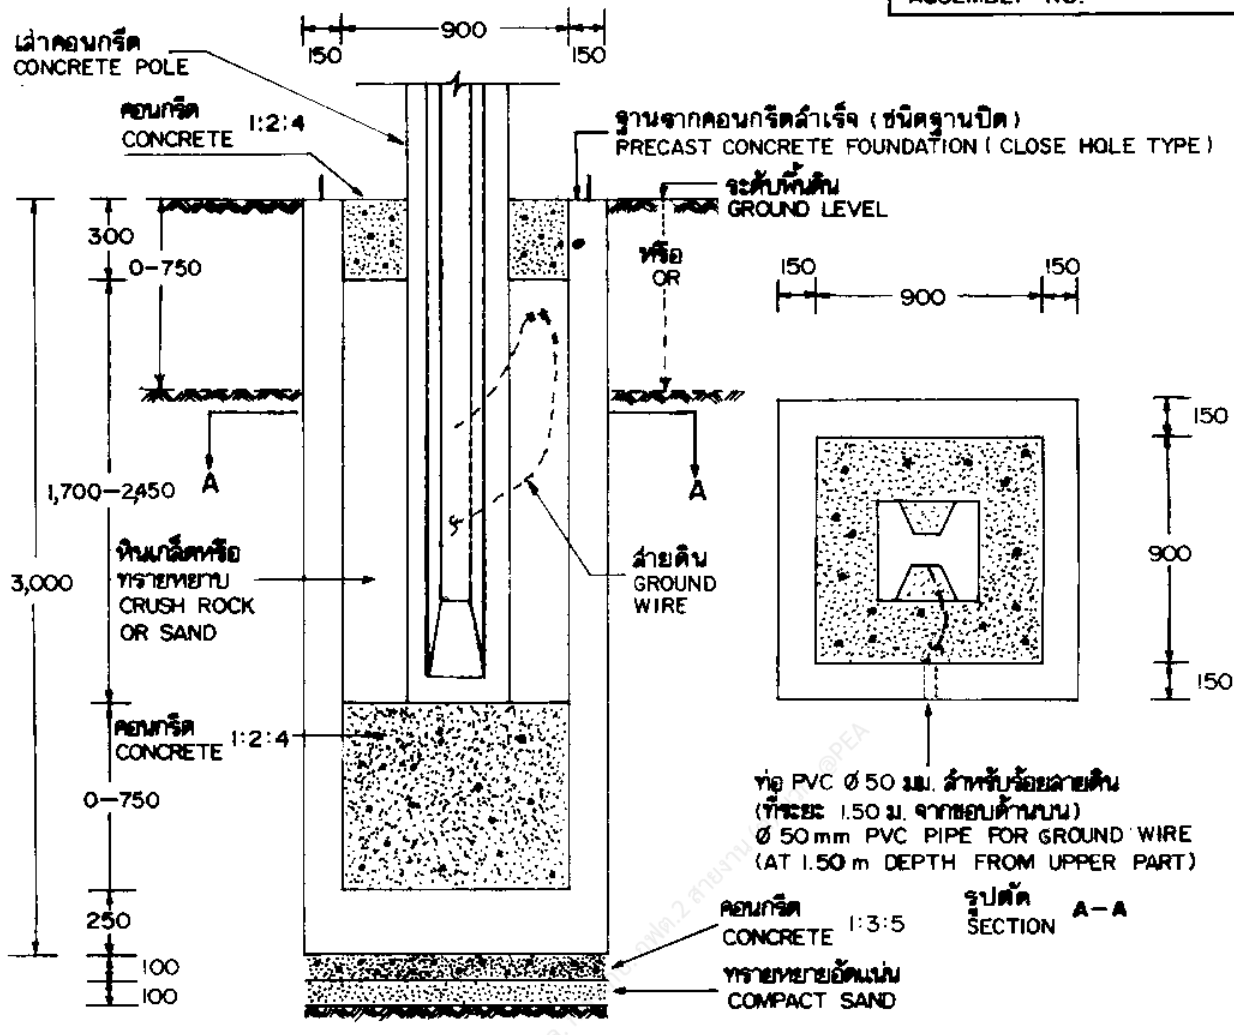

หมายเหตุ

1. ฐานรากนี้ใช้สำหรับในกรณีดินสามารถรับน้ำหนักปลอดภัย ได้ตั้งแต่ 10 ตัน/ตารางเมตร ขึ้นไป
2. ดูรายละเอียดเพิ่มเติมจากแบบเลขที่ IBI-018/36001

NOTES


1. THIS FOUNDATION USES ONLY IN CASE OF ALLOWABLE SOIL BEARING CAPACITY OF 10 TON/m^2 OR MORE.
2. SEE ADDITIONAL DETIALS IN DRAWING NO. IBI-018/36001

กองวิศวกรรมไฟฟ้าและเครื่องกล ฝ่ายวิศวกรรม	**การไฟฟ้าส่วนภูมิภาค**	ใช้แทนแบบ ถูกแทนโดยแบบ
ผู้เขียน ผู้สำรวจ วิศวกร หัวหน้าแผนก ผู้อำนวยการกอง ผู้อำนวยการฝ่าย	ผู้ว่าการ 18 ต.ค. 2536	เขียนแบบวันที่ 18 ต.ค. 2536 แก้แบบวันที่ มิติเป็น มิลลิเมตร มาตราส่วน 1:30
รองผู้ว่าการฝ่ายเทคนิค	รายละเอียด 10 D ฐานรากเสา (แบบที่ 1) DETAIL 10 D POLE FOUNDATION (TYPE 1)	แบบเลขที่ SAI-015/36014 แผ่นที่ 1 ของจำนวน 3 แผ่น

18 ต.ค. 2536

D— 10D TYPE 2

การประกอบเลขที่ ASSENBLY NO. 5684

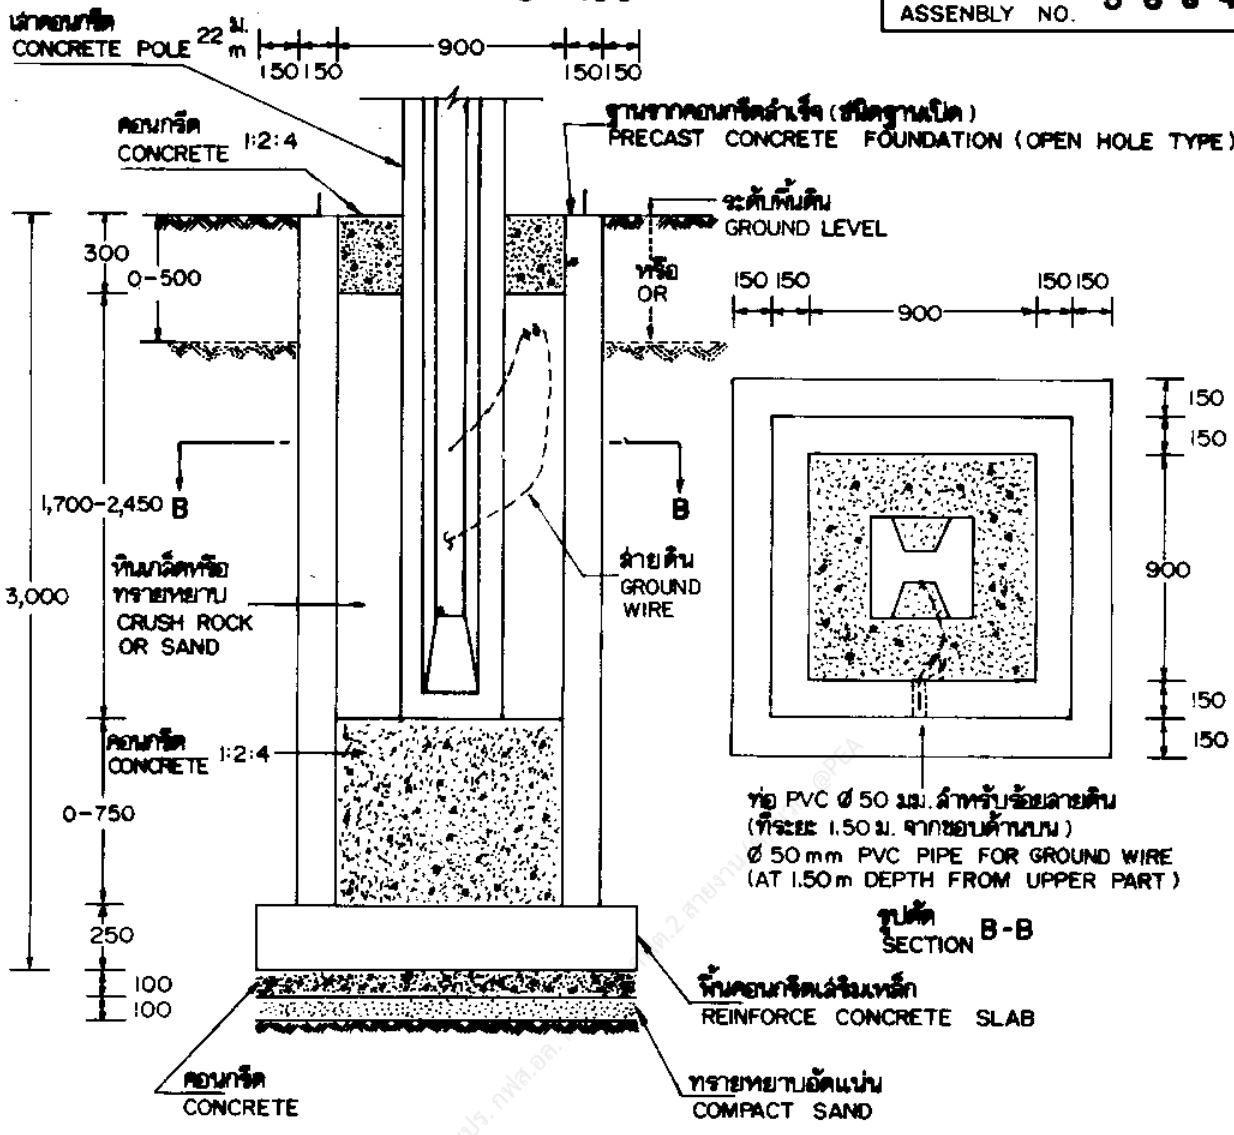

หมายเหตุ

1. ฐานรากนี้ใช้สำหรับในกรณีดินสามารถรับน้ำหนักปลอดภัยได้ตั้งแต่ 10 ตัน/ตารางเมตร ขึ้นไป
2. ดูรายละเอียดเพิ่มเติม จากแบบเลขที่ IBI-018/36003

NOTES


1. THIS FOUNDATION USES ONLY IN CASE OF ALLOWABLE SOIL BEARING CAPACITY OF 10 TON/m^2 OR MORE .
2. SEE ADDITIONAL DETAILS IN DRAWING NO. IBI-018/36003 .

กองวิศวกรรมไฟฟ้าและเครื่องกล ฝ่ายวิศวกรรม	การไฟฟ้าส่วนภูมิภาค	ใช้แทนแบบ _____ ถูกแทนโดยแบบ _____
ผู้เขียน _____ ผู้สำรวจ _____ วิศวกร _____ หัวหน้าแผนก _____ ผู้อำนวยการกอง _____ ผู้อำนวยการฝ่าย _____	ผู้ว่าการ _____	เขียนเสร็จวันที่ 18 ต.ค. 2536 แก้แบบวันที่ _____ มิติเป็น มิลลิเมตร มาตราส่วน 1:30
รองผู้ว่าการฝ่ายเทคนิค _____	รายละเอียด 10 D ฐานรากเสา (แบบที่ 2) DETAIL 10 D POLE FOUNDATION (TYPE 2)	แบบเลขที่ SAI-015/36014 แผ่นที่ 2 ของจำนวน 3 แผ่น

2536

D—10D TYPE 3

การประกอบเลขที่ ASSEMBLY NO. 5684

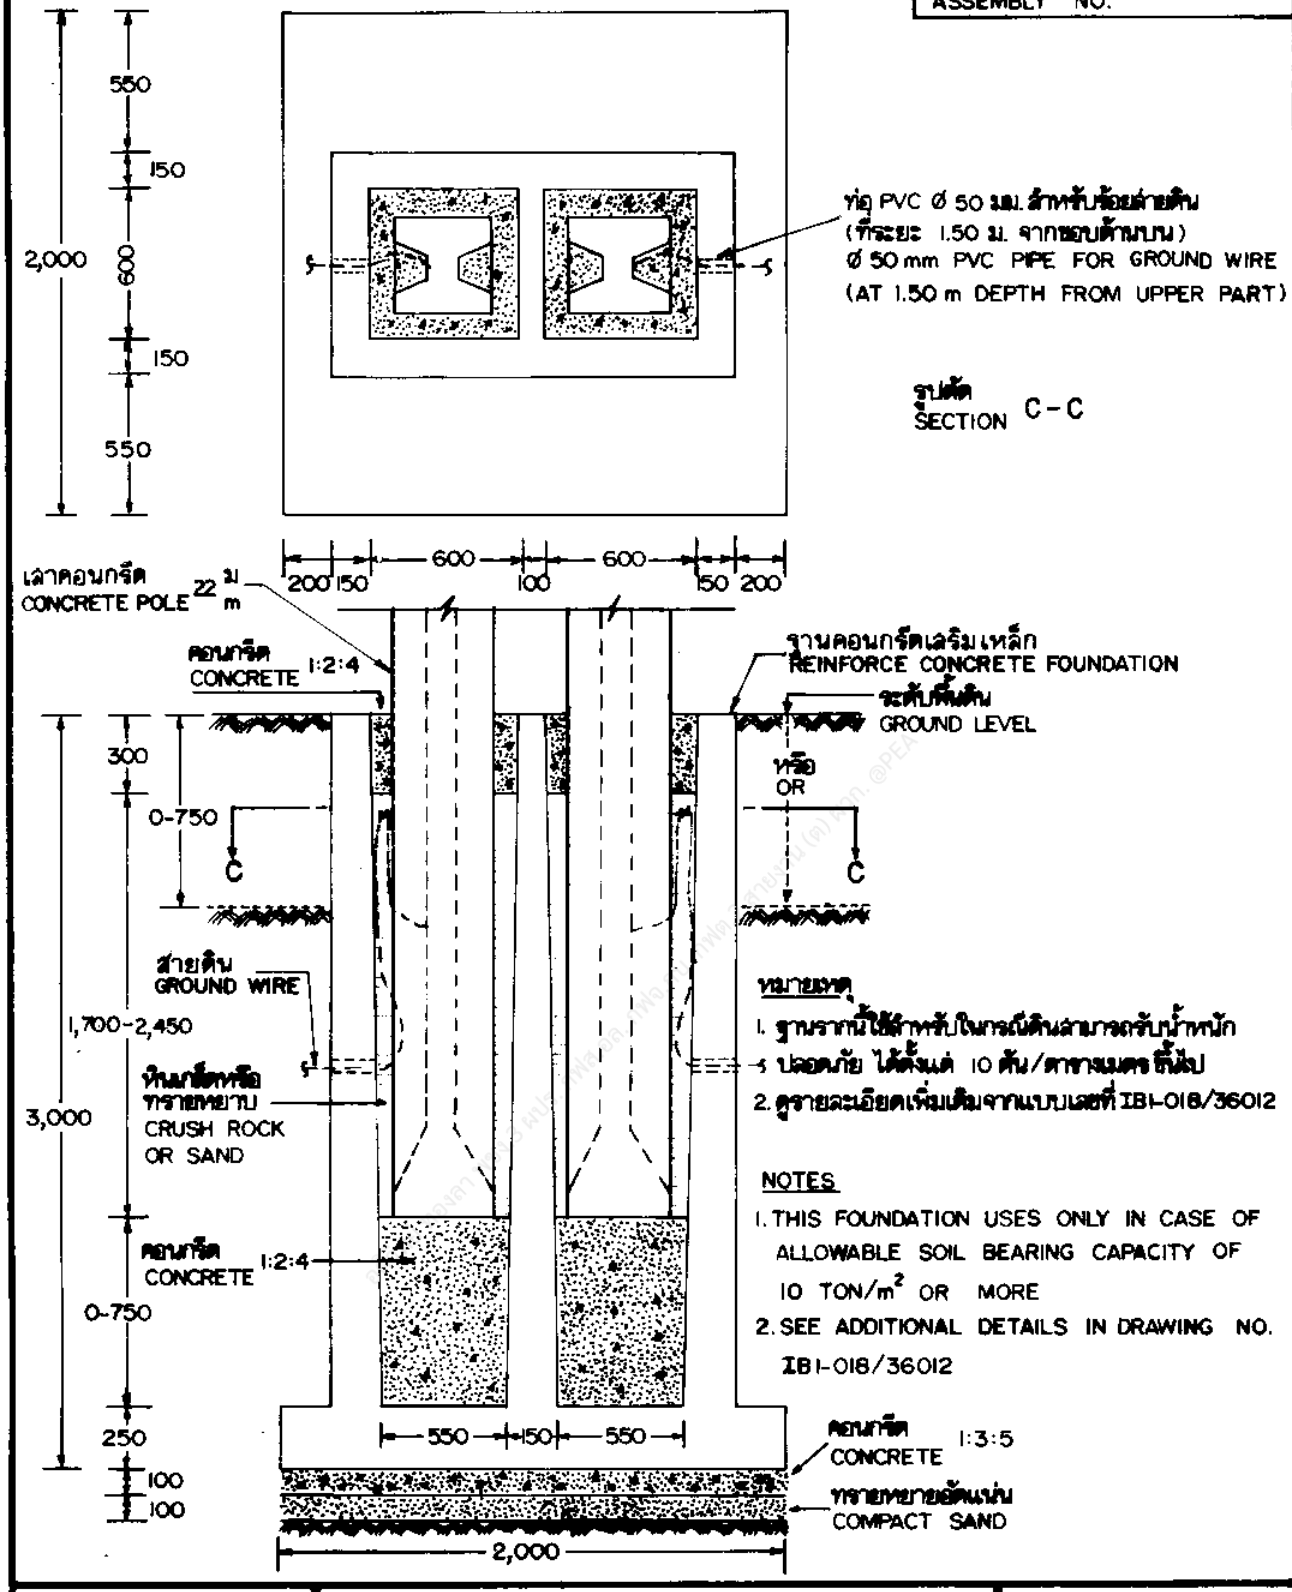

หมายเหตุ

1. ฐานรากนี้ใช้สำหรับในกรณีดินสามารถรับน้ำหนักปลอดภัย ได้ตั้งแต่ 10 ตัน/ตารางเมตร ขึ้นไป
2. ดูรายละเอียดเพิ่มเติมจากแบบเลขที่ IBI-018/36012

NOTES

1. THIS FOUNDATION USES ONLY IN CASE OF ALLOWABLE SOIL BEARING CAPACITY OF 10 TON/m^2 OR MORE
2. SEE ADDITIONAL DETAILS IN DRAWING NO. IBI-018/36012

กองวิศวกรรมไฟฟ้าและเครื่องกล ฝ่ายวิศวกรรม	การไฟฟ้าส่วนภูมิภาค	ใช้ยกแบบ ลูกแบบโดยแบบ เขียนเสร็จวันที่ 18 ส.ค. 2536 แก้แบบวันที่ มิติเป็น มิลลิเมตร มาตราส่วน 1:30
ผู้เขียน ผู้สำรวจ วิศวกร หัวหน้าแผนก ผู้อำนวยการฝ่าย ผู้ช่วยผู้อำนวยการฝ่าย	ผู้ว่าการ 18 ส.ค. 2536	
ของผู้ว่าการฝ่ายเทคนิค	รายละเอียด 10D ฐานรากเสา (แบบที่ 3)	
	DETAIL 10D POLE FOUNDATION (TYPE 3)	แบบเลขที่ SAI-015/36014 แผ่นที่ 3 ของจำนวน 3 แผ่น

18 ส.ค. 2536