


การประกอบเลขที่ 3418
ASSEMBLY NO.

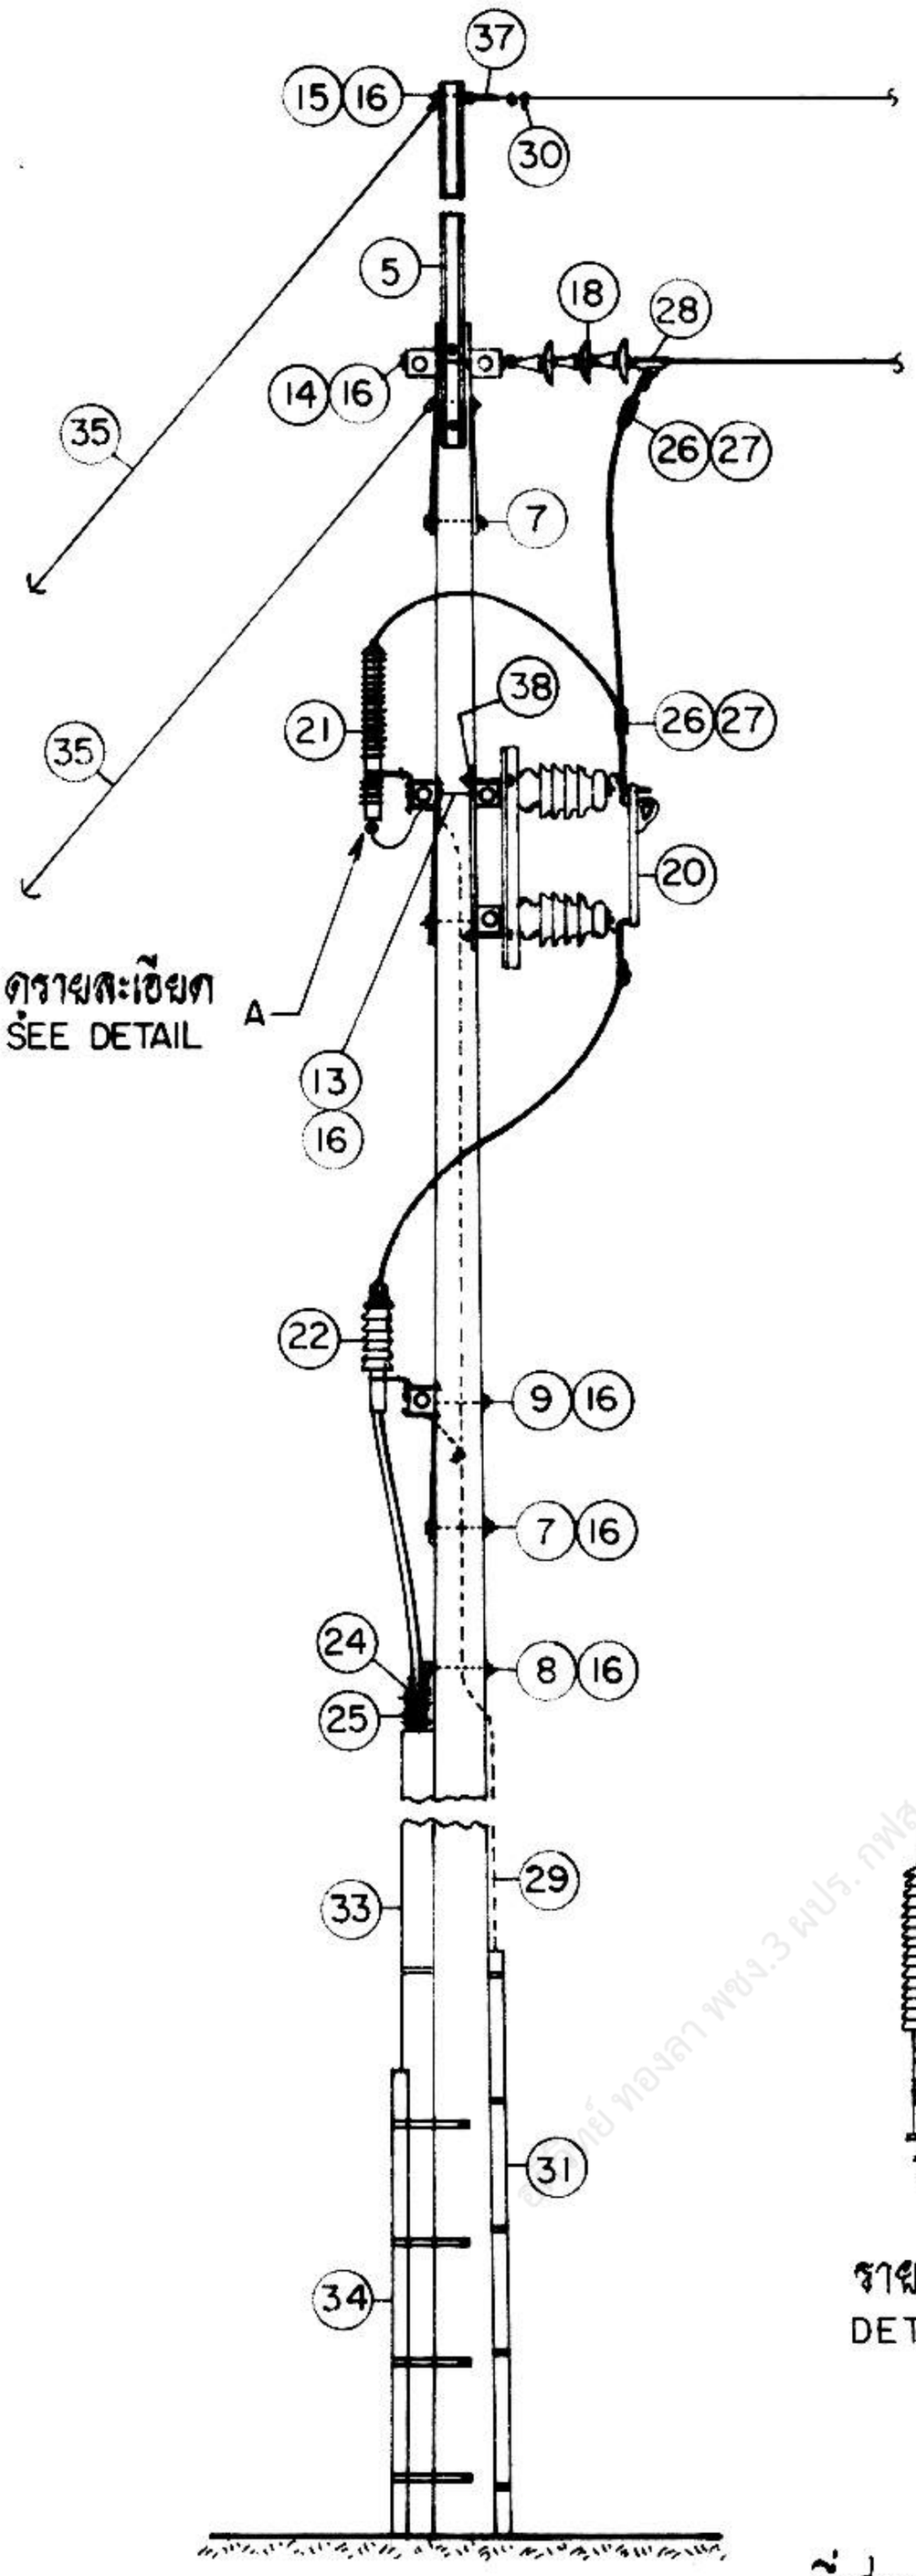

I

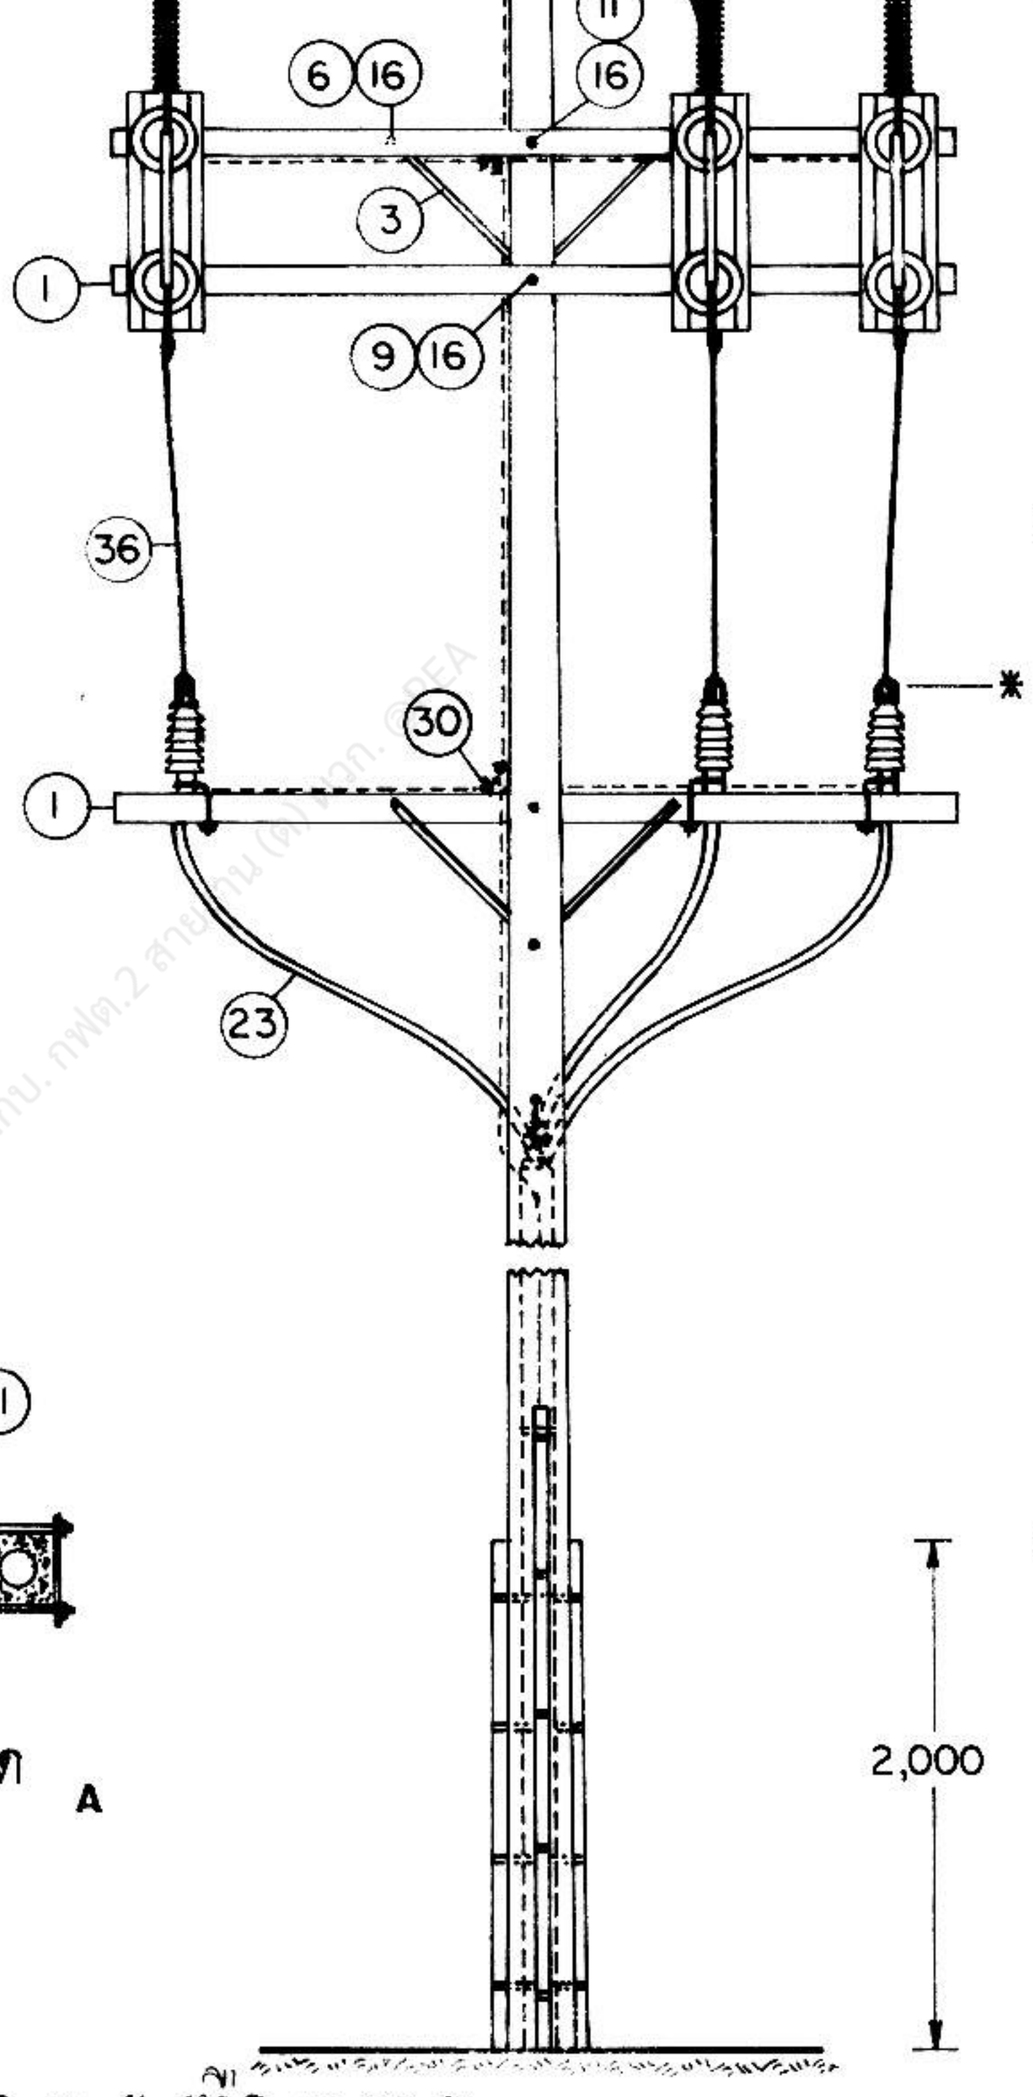

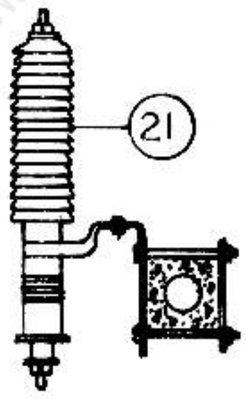


รายละเอียด A
DETAIL


ที่เสาคอนกรีต 12 ม. หรือ 12.20 ม.
AT 12 m OR 12.20 m CONCRETE POLE


กองวิศวกรรมไฟฟ้าและเครื่องกล ฝ่ายวิศวกรรม	การไฟฟ้าส่วนภูมิภาค	ใช้แทนแบบ ถูกแทนโดยแบบ เขียนแล้วเมื่อวันที่ 6 พ.ย. 35 แก้แบบวันที่ 19 ก.ย. 39 มิติเป็น มิลลิเมตร มาตราส่วน 1:50
ผู้เขียน ผู้สำรวจ วิศวกร หัวหน้าแผนก ผู้อำนวยการกอง ผู้อำนวยการฝ่าย	ผู้ว่าการ การติดตั้งหัวเคเบิลที่เสาต้นสุดท้าย ระบบ 33 kV	
รองผู้ว่าการฝ่ายเทคนิค	CABLE RISER INSTALLATION, AT DEADEND POLE 33 kV SYSTEM	แบบเลขที่ SA4-015/35013 แผ่นที่ 1 ของจำนวน 6 แผ่น

1 พ.ย 2535


การประกอบเลขที่ 3418
ASSEMBLY NO. 3418

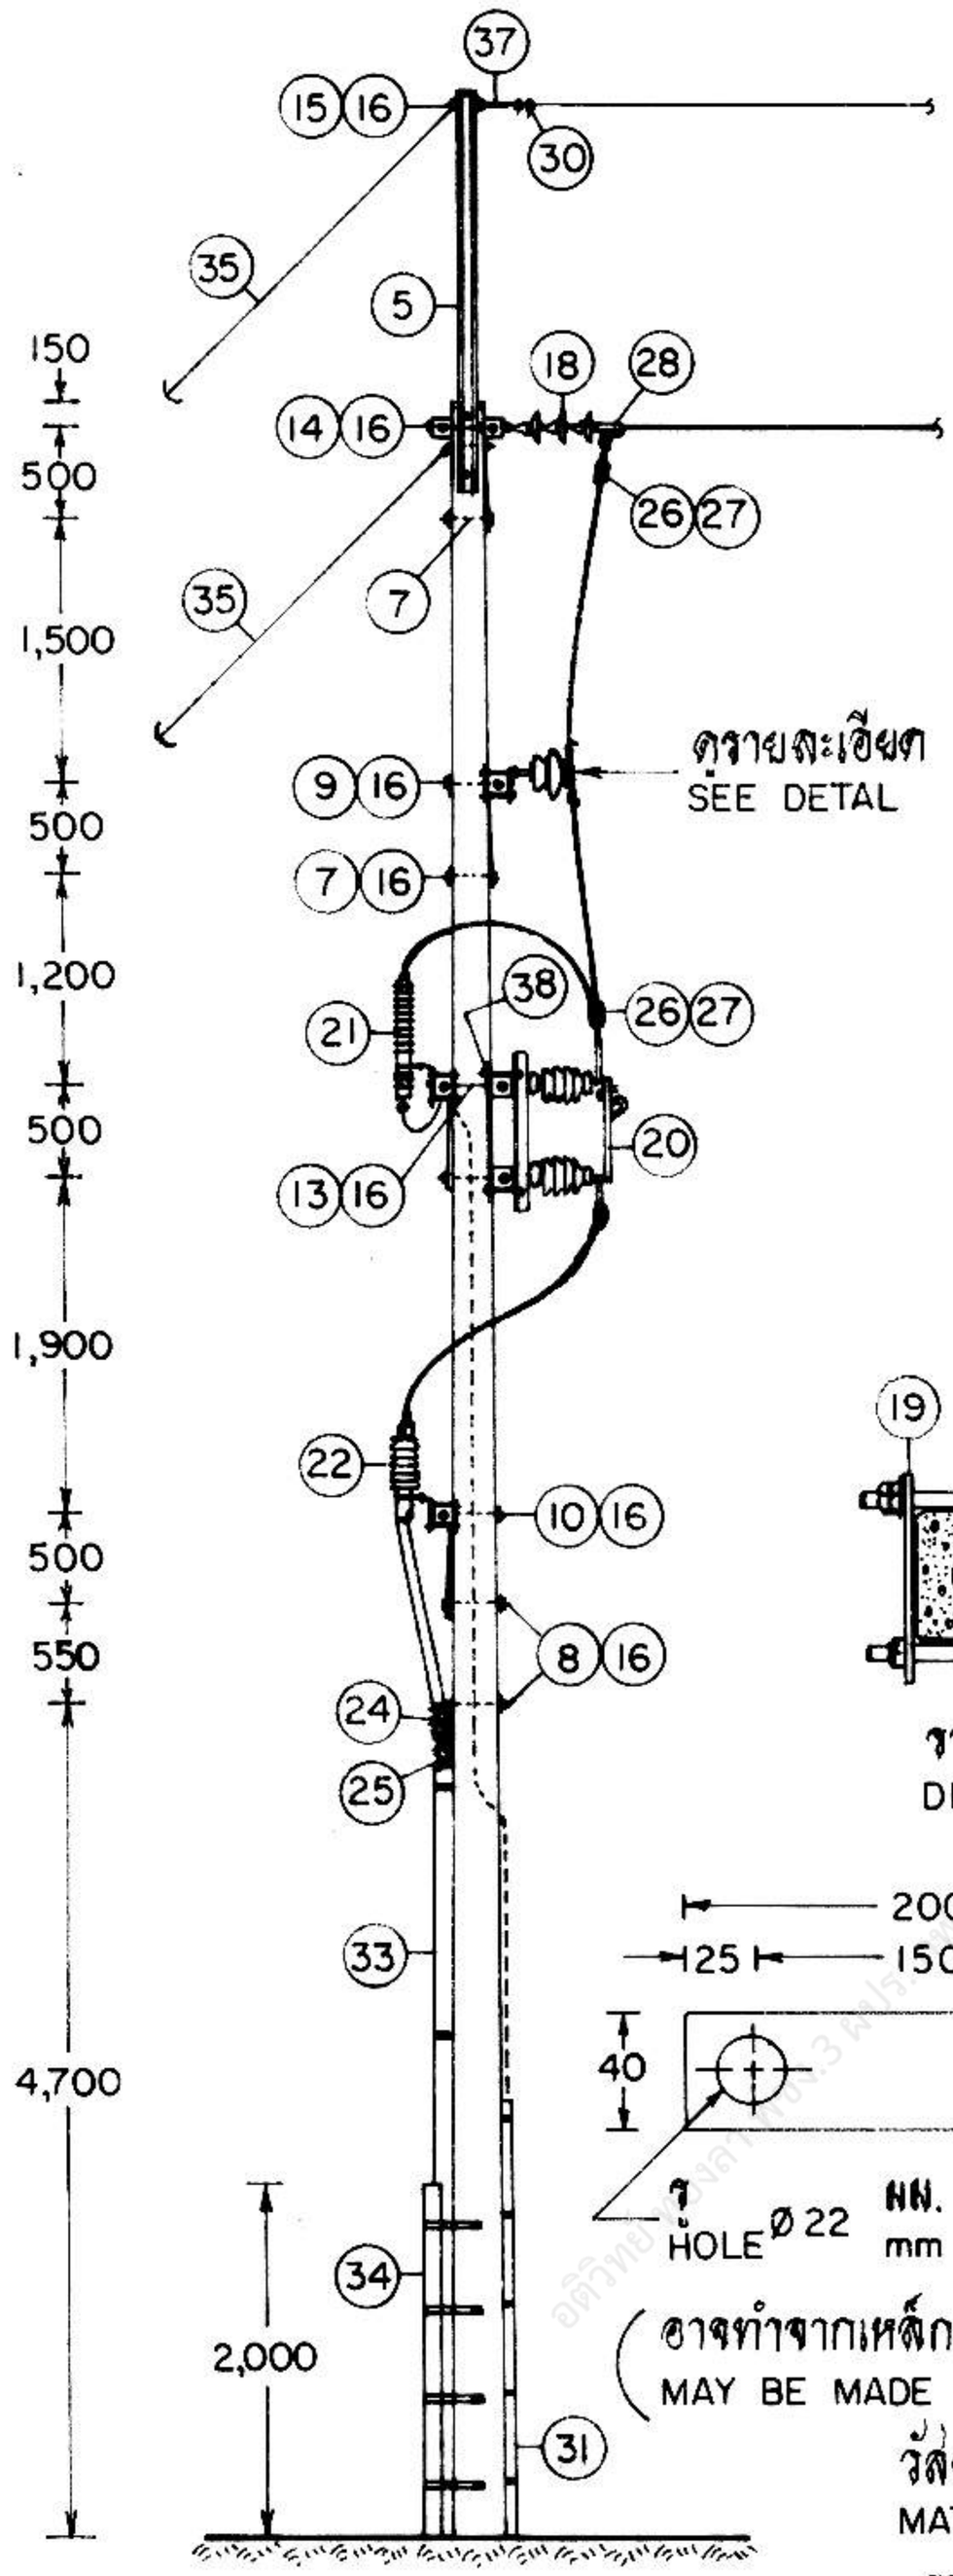

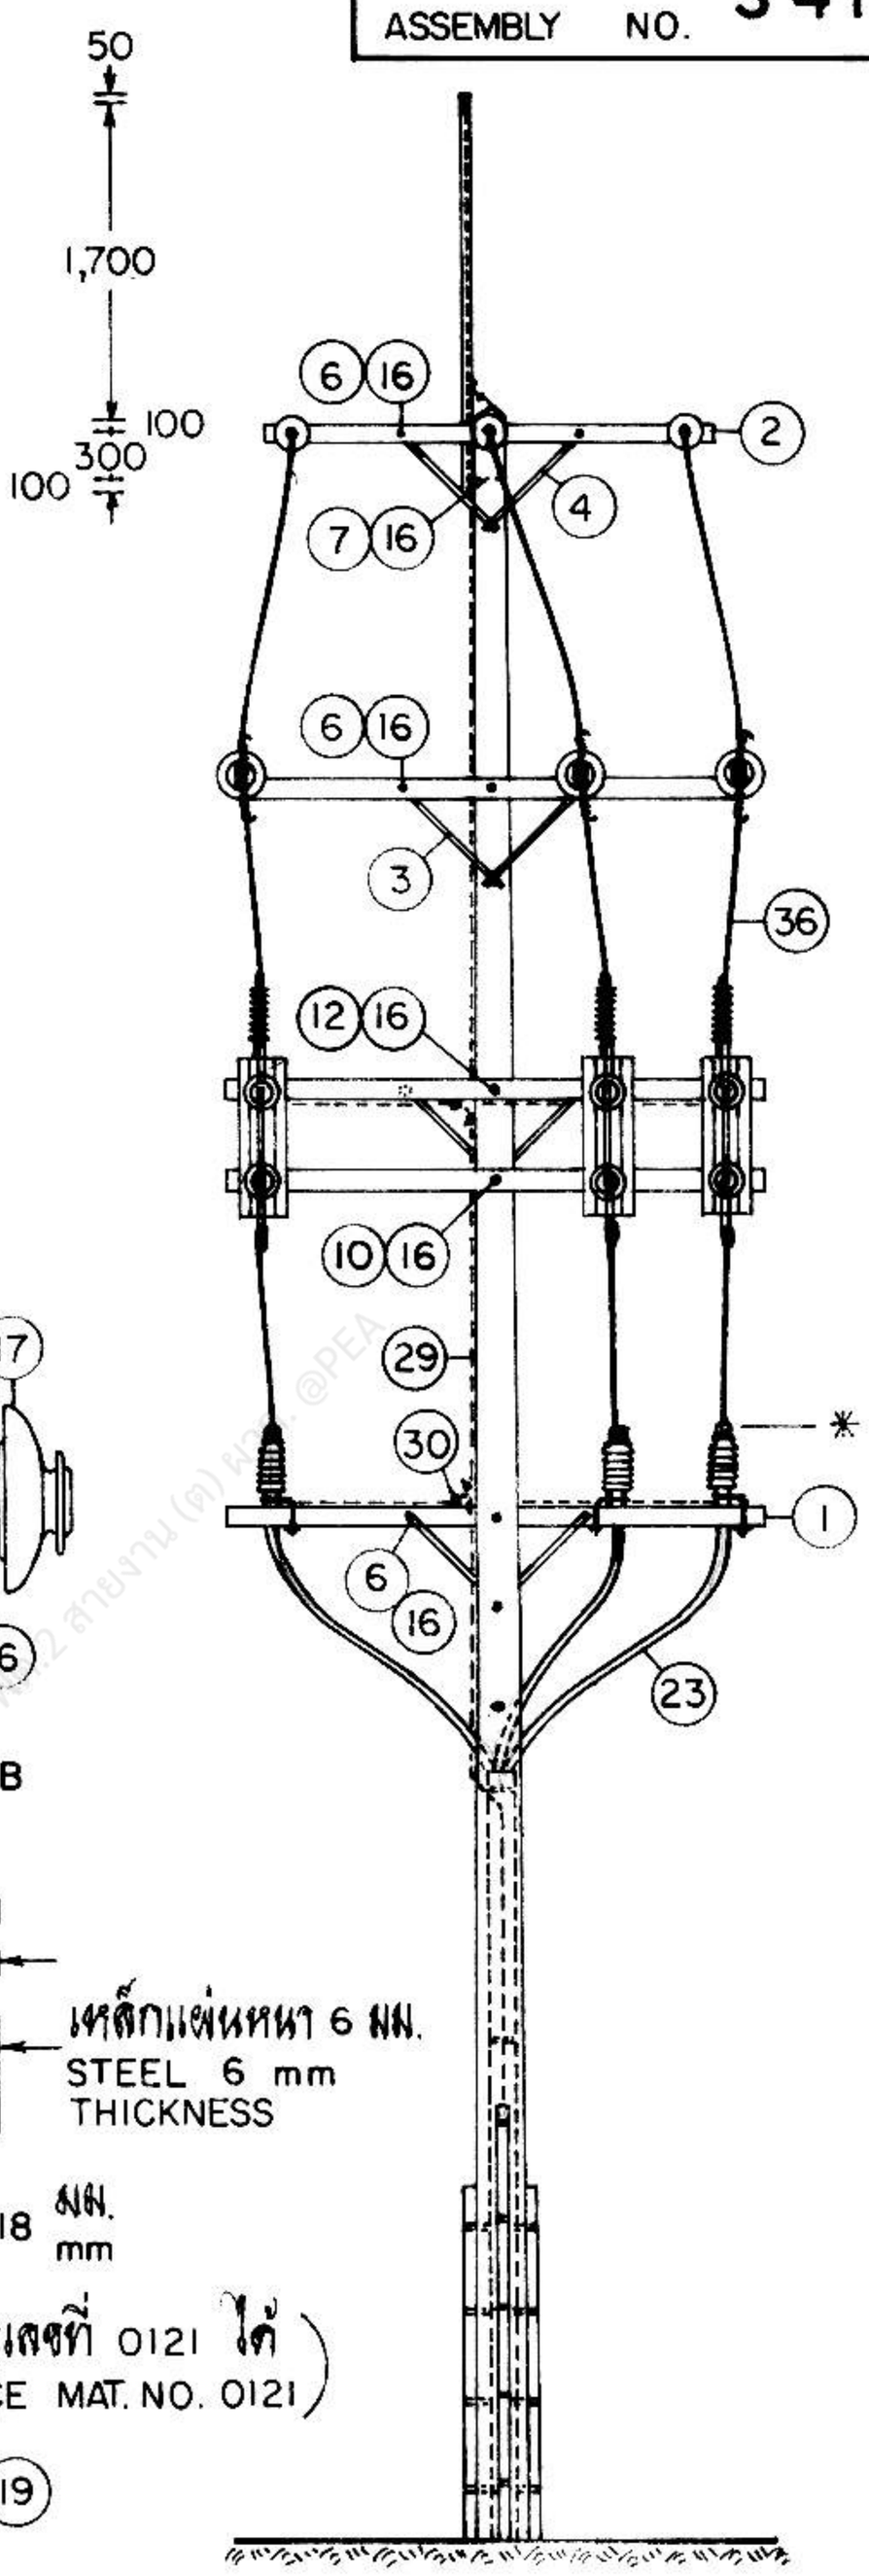

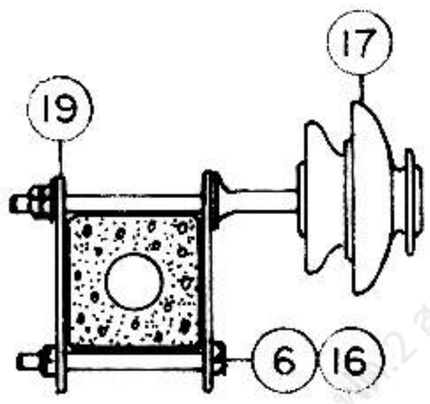

รายละเอียด B
DETAIL

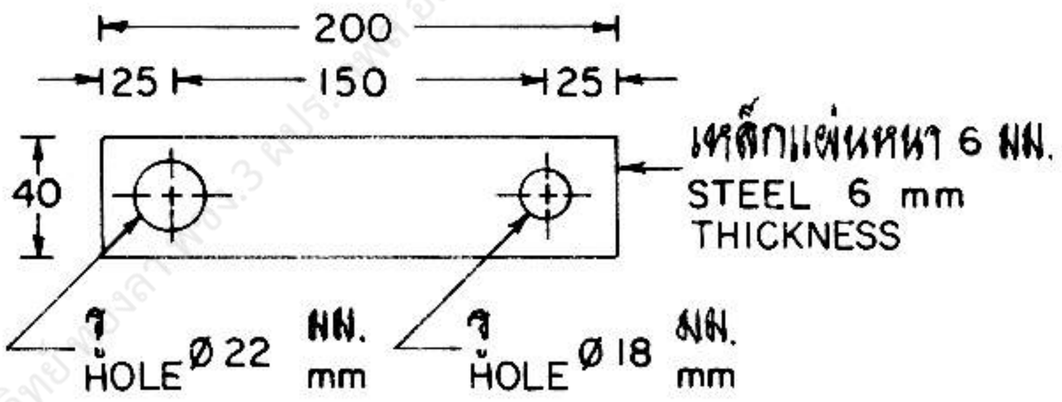

(อาจทำจากเหล็กประกับ วัสดุเลขที่ 0121 ได้
MAY BE MADE FROM BRACE MAT. NO. 0121)

วัสดุลำดับที่ (19)
MAT. ITEM

รายละเอียด C
DETAIL

II ที่เสาคอนกรีต 14 ม. หรือ 14.30 ม.
AT 14 m OR 14.30 m CONCRETE POLE

กองวิศวกรรมไฟฟ้าและเครื่องกล ฝ่ายวิศวกรรม	**การไฟฟ้าส่วนภูมิภาค**	ใช้แทนแบบ ถูกแทนโดยแบบ
ผู้เสนอ ... ผู้สำรวจ ... วิศวกร ... หัวหน้าแผนก ... ผู้อำนวยการกอง ... ผู้อำนวยการฝ่าย ...	ผู้ว่าการ สุเทพ อัมมาร (แทน)	เสนอเสร็จวันที่ 6 พ.ย. 35 แก้แบบวันที่ 19 ก.ย. 39 มิติเป็น มิลลิเมตร มาตราส่วน 1 : 75
รองผู้ว่าการฝ่ายเทคนิค ...	การติดตั้งหัวเคเบิลที่เสาต้นสุดท้าย ระบบ 33 kV CABLE RISER INSTALLATION, AT DEADEND POLE 33 kV SYSTEM	แบบเลขที่ SA4-015/35013 แผ่นที่ 2 ของจำนวน 6 แผ่น

1 พ.ย. 2535

การประกอบเลขที่ ASSEMBLY NO. 3418

บัญชีวัสดุ
BILL OF MATERIAL

ลำดับที่ ITEM	รายละเอียด DESCRIPTION	จำนวน REQ'D I	จำนวน REQ'D II	วัสดุเลขที่ MAT. NO.
1	คอน คอร. สปัน ขนาด 120 X 120 X 3,000 มม. CROSSARM, SPUN, PRESTRESSED CONCRETE, 120 X 120 X 3,000 mm	4	5	00110002
2	คอน คอร. สปัน (สำหรับเข้าปลายสาย) 120 X 120 X 2,500 มม. CROSSARM, SPUN, PRESTRESSED CONCRETE (FOR DEADENDING), 120 X 120 X 2,500 mm	2	2	00110004
3	เหล็กประกับคอน 30 X 6 X 760 มม. BRACE, FLAT, FOR CROSSARM, 30 X 6 X 760 mm	4	4	01200001
4	เหล็กประกับคอน 40 X 6 X 1,000 มม. BRACE, FLAT, FOR CROSSARM, 40 X 6 X 1,000 mm	4	6	01200002
5	เหล็กรูปรางน้ำรับสายล่อฟ้า ขนาด 100 X 50 X 5 มม. ยาว 2,250 มม. OVERHEAD GROUND WIRE BAYONET, CHANNEL STEEL, 100 X 50 X 5 mm, 2,250 mm LONG	1	1	01000100
6	สลักเกลียว M 16 X 170 มม. BOLT, MACHINE, M 16 X 170 mm	8	13	01110201
7	สลักเกลียว M 16 X 250 มม. BOLT, MACHINE, M 16 X 250 mm	4	4	01110203
8	สลักเกลียว M 16 X 300 มม. BOLT, MACHINE, M 16 X 300 mm	1	2	01110204
9	สลักเกลียว M 16 X 350 มม. BOLT, MACHINE, M 16 X 350 mm	2	1	01110205
10	สลักเกลียว M 16 X 400 มม. BOLT, MACHINE, M 16 X 400 mm	–	2	01110206
11	สลักเกลียว M 16 X 450 มม. BOLT, MACHINE, M 16 X 450 mm	1	–	01110207
12	สลักเกลียว M 16 X 500 มม. BOLT, MACHINE, M 16 X 500 mm	–	1	01110208
13	สลักเกลียวตลอด M 16 X 500 มม. BOLT, DOUBLE ARMING, M 16 X 500 mm	2	2	01120002
14	สลักเกลียวห่วงกลม M 16 X 450 มม. BOLT, DOUBLE ARMING, ROUND EYE, M 16 X 450 mm	3	3	01130001
15	สลักเกลียวห่วงกลม M 16 X 200 มม. BOLT, ROUND EYE, M 16 X 200 mm	1	1	01140001
16	แหวนสี่เหลี่ยมแผน 52 X 52 X 4.5 มม. รู Ø 18 มม. มอก. 258 WASHER, SQUARE, FLAT, 52 X 52 X 4.5 mm, HOLE Ø 18 mm, TIS 258	37	45	01180100
17	ลูกถ้วยก้านตรง 33 kV มอก. 279 แบบ ค (แบบ 56-3) พร้อมก้าน INSULATOR, PIN TYPE, 33 kV, TIS 279, TYPE C (CLASS 56-3), COMP. WITH PIN	–	3	03000002 03100001
18	ลูกถ้วยแขวน มอก. 354 แบบ ง (แบบ 52-4) INSULATOR, SUSPENSION TYPE, TIS 354, TYPE D (CLASS 52-4)	9	9	03020002
19	แผ่นเหล็ก 40 X 6 มม. ยาว 200 มม. เจาะรูตามรายละเอียด C STEEL PLATE, 40 X 6 mm, 200 mm LONG, PUNCH HOLE AS DETAIL C	–	6	——

กองวิศวกรรมไฟฟ้าและเครื่องกล
ฝ่ายวิศวกรรม

ผู้เสนอ ...
ผู้สำรวจ ...
วิศวกร ...
หัวหน้าแผนก ...
ผู้อำนวยการกอง ...
ผู้อำนวยการฝ่าย ...

ของผู้ว่าการฝ่ายเทคนิค ...

การไฟฟ้าส่วนภูมิภาค

ผู้ว่าการ ...

การติดตั้งหัวเคเบิลที่เสาต้นสุดท้าย
ระบบ 33 kV

CABLE RISER INSTALLATION, AT DEADEND POLE
33 kV SYSTEM

ใช้แทนแบบ ...
ถูกแทนโดยแบบ ...
เขียนแล้วเสร็จวันที่ 6 พ.ย. 35
แก้แบบวันที่ 19 ก.ย. 39
มิติเป็น ...
มาตราส่วน ...

แบบเลขที่ SA4-015/35013
แผ่นที่ 3 ของจำนวน 6 แผ่น

พ.ศ. 2535

การประกอบเลขที่ ASSEMBLY NO. **3418**

บัญชีวัสดุ
BILL OF MATERIAL

ลำดับที่ ITEM	รายละเอียด DESCRIPTION	จำนวน REQ'D I	จำนวน REQ'D II	วัสดุเลขที่ MAT. NO.
20	สวิตช์ตัดตอนแรงสูง 33 kV, 600 แอมป์ ชนิดติดตั้งในสถานีเปลี่ยนแรงดัน SWITCH, DISCONNECTING, SINGLE POLE, 33 kV, 600 A, STATION CLASS	3	3	04050101
21	ล่อฟ้า 30 kV, 10 kA LIGHTNING ARRESTER, 30 kV, 10 kA	3	3	04000101
22	หัวเคเบิล สำหรับเคเบิลใต้ดินทองแดง 33 kV ขนาดตามต้องการ CABLE RISER, FOR 33 kV Cu UNDERGROUND CABLE; SIZE AS REQUIRED	3	3	02150101 5457
23	เคเบิลใต้ดินทองแดง 33 kV ขนาด และความยาวตามต้องการ CABLE, UNDERGROUND, Cu, 33 kV ; SIZE AND LENGTH AS REQUIRED	N. m	N. m	
24	ห่วงรัดสาย สำหรับเคเบิลใต้ดินทองแดง 33 kV ขนาดตามต้องการ CABLE GRIP, FOR 33 kV Cu UNDERGROUND CABLE ; SIZE AS REQUIRED	1	1	
25	AIRSEAL COMPOUND จำนวนตามต้องการ AIRSEAL COMPOUND, QUANTITY AS REQUIRED			
26	พี.จี. คอนเนคเตอร์ ขนาดตามต้องการ CONNECTOR, PARALLEL GROOVE ; SIZE AS REQUIRED	9	9	02300102 02300103
27	PVC เทป กว้าง 19 มม. (ใช้ความยาว 2 ม. ต่อ 1 จุด) PVC TAPE, 19 mm WIDE (2 m LONG PER POINT)	ม้วน roll	ม้วน roll	02180002
28	ส่เตรนแคล้มป์ ขนาดตามต้องการ CLAMP, STRAIN ; SIZE AS REQUIRED	3	3	03110000 03110004
29	ลวดเหล็กตีเกลียว 50/7 ต.มม. มอก. 404 WIRE, STEEL STRANDED, 50/7 mm^2, TIS 404	27 N. m	30 N. m	01100004
30	ยูแคล้มป์ ชนิด 1 ตัว M 8 CLAMP, SINGLE U-BOLT, M 8	12	12	01230000
31	ท่อ PVC แข็ง ขนาด Ø 20 X 2,500 - 4,000 มม. พร้อมอุปกรณ์ยึด CONDUIT, PVC RIGID, Ø 20 X 2,500 - 4,000 mm ; COMP. WITH FIXING ACCESS.	1	1	08040002 or 08040001
32	หลักดิน 60 X 60 X 5 มม. ยาว 2 ม. ROD, GROUND, 60 X 60 X 5 mm, 2 m LONG	1	1	01220002
33	ท่อเหล็กกล้าเคลือบสังกะสี ประเภทที่ 3 มอก. 770 หรือท่อ HDPE PN6.3 มอก. 982 พร้อมอุปกรณ์ยึดและข้อต่อ (ถ้าต้องการ) ขนาดและความยาวตามต้องการ CONDUIT, GALVANIZED STEEL, TYPE 3 TIS 770 OR HDPE PN6.3, TIS 982 COM. WITH FIXING ACCESS AND COUPLING (IF REQ'D) SIZE AND LENGTH AS REQ'D			08050003 or 08050004
34	โครงเหล็กกั้นท่อร้อยสาย CONDUIT STEEL GUARD	1	1	
35	สายยึดโยงแบบ GY - 33 GUY ASSEMBLY, GY - 33	1	1	
36	สายอะลูมิเนียมหุ้มฉนวนแบบไม่เต็มพิกัด 33 kV หรือ เคเบิลอากาศอะลูมิเนียม 33 kV ขนาดตามต้องการ CABLE, Al, PARTIALLY INSULATED, 33 kV ; OR CABLE, AERIAL, Al, 33 kV ; SIZE AS REQUIRED	15 ม. m	21 ม. m	0644 - 02060103 02050100 - 02050104

กองวิศวกรรมไฟฟ้าและเครื่องกล ฝ่ายวิศวกรรม	**การไฟฟ้าส่วนภูมิภาค**	ใช้แทนแบบ ..... ถูกแทนโดยแบบ ..... เขียนเสร็จวันที่ 6 พ.ย. 35 แก้แบบวันที่ 19 ก.ย. 39 30 เม.ย. 42 มิติเป็น ..... มาตราส่วน .....
ผู้เขียน ..... ผู้ตรวจ ..... วิศวกร ..... หัวหน้าแผนก ..... ผู้อำนวยการกอง ..... ผู้อำนวยการฝ่าย	ผู้ว่าการ ..... การติดตั้งหัวเคเบิลที่เสาต้นสุดท้าย ระบบ 33 kV	
ของผู้ว่าการฝ่ายเทคนิค	CABLE RISER INSTALLATION, AT DEADEND POLE 33 kV SYSTEM	แบบเลขที่ SA4-015/35013 แผ่นที่ 4 ของจำนวน 6 แผ่น

พ.ย. 2535

การประกอบเลขที่ ASSEMBLY NO. 3418

บัญชีวัสดุ
BILL OF MATERIAL

ลำดับที่ ITEM	รายละเอียด DESCRIPTION	จำนวน REQ'D I	จำนวน REQ'D II	วัสดุเลขที่ MAT. NO.
37	กายทิมเบิล สำหรับสายยึดโยง 50-95 ต.มม. THIMBLE, GUY, FOR STEEL WIRE 50-95 mm^2	1	1	01210304
38	อุปกรณ์ติดตั้งสวิตช์ตัดตอนแรงสูง MOUNTING ACCESSORIES, FOR DISCONNECTING SWITCH	3 ชุด sets	3 ชุด sets	—

แบบอ้างอิง REFERENCE DRAWING		แบบเลขที่ DWG. NO.	การประกอบเลขที่ ASSEMBLY NO.
1	การประกอบสายดิน วิธียึดลวดเหล็ก GROUND LEAD ASSEMBLY, STEEL WIRE FITTING	SO2-015/19166 SA1-015/31012	9703 9703A
2	การประกอบที่ยึดท่อ PVC สำหรับสายดิน PVC PIPE FITTING ASSEMBLY, FOR GROUND WIRE	SO2-015/19128 SA1-015/31013	9704 9704A
3	การติดตั้งโครงเหล็กกั้น (สำหรับท่อร้อยสายขึ้นเสา ระบบ 22 kV, 33 kV เสาคอนกรีต 12 ม. และ 14 ม.) STEEL GUARD CONSTRUCTION (FOR 22 kV, 33 kV RISER POLE, 12 m AND 14 m CONCRETE POLE)	SA1-015/31028	7906
4	หลักเกณฑ์การใช้ลูกถ้วยแรงสูง ในบริเวณใกล้ฝั่งทะเล RECOMMENDATION FOR H.V. INSULATOR INSTALLATION, NEAR THE SEA COAST	SA1-015/24019	9502

หมายเหตุ

* เพื่อป้องกันปัญหาเนื่องจากนก (ถ้าต้องการ) ให้ใช้ PVC เทป (วัสดุเลขที่ 5906) พัน

NOTE

* TO PROTECT THE PROBLEM DUE TO BIRDS (IF REQUIRED), IT SHALL BE WRAPPED WITH PVC TAPE (MAT. NO. 5906) .

กองวิศวกรรมไฟฟ้าและเครื่องกล
ฝ่ายวิศวกรรม

ผู้เขียน ...
ผู้สำรวจ
วิศวกร ...
หัวหน้าแผนก ...
ผู้อำนวยการกอง ...
ผู้อำนวยการฝ่าย ...

รองผู้ว่าการฝ่ายเทคนิค ...

การไฟฟ้าส่วนภูมิภาค

ผู้ว่าการ ...

การติดตั้งหัวเคเบิลที่เสาต้นสุดท้าย
ระบบ 33 kV

CABLE RISER INSTALLATION, AT DEADEND POLE
33 kV SYSTEM

ใช้แทนแบบ .....
ถูกแทนโดยแบบ .....
เขียนเสร็จวันที่ 6 พ.ย. 35
แก้แบบวันที่ 19 ก.ย. 39
มิลิเป็น .....
มาตราส่วน .....

แบบเลขที่ SA4-015/35013
แผ่นที่ 5 ของจำนวน 6 แผ่น

พ.ศ. 2535

การประกอบเลขที่ ASSEMBLY NO.	3418

บัญชีวัสดุสำหรับเสาคอนกรีต 12.20 ม. และ 14.30 ม. (เฉพาะสลักเกลียว)
BILL OF MATERIAL,FOR 12.20 AND 14.30 m CONCRETE POLE (BOLT ONLY)

ลำดับที่ ITEM	รายละเอียด DESCRIPTION	จำนวน REQ'D I	จำนวน REQ'D II	วัสดุเลขที่ MAT. NO.
6	สลักเกลียว M 16 x 170 มม. BOLT, MACHINE, M 16 x 170 mm	8	13	01110201
7	สลักเกลียว M 16 x 250 มม. BOLT, MACHINE, M 16 x 250 mm	3	–	01110203
7a	สลักเกลียว M 16 x 300 มม. BOLT, MACHINE, M 16 x 300 mm	1	4	01110204
8	สลักเกลียว M 16 x 350 มม. BOLT, MACHINE, M 16 x 350 mm	1	1	01110205
8a	สลักเกลียว M 16 x 400 มม. BOLT, MACHINE, M 16 x 400 mm	–	1	01110206
9	สลักเกลียว M 16 x 400 มม. BOLT, MACHINE, M 16 x 400 mm	2	–	01110206
9a	สลักเกลียว M 16 x 450 มม. BOLT, MACHINE, M 16 x 450 mm	–	1	01110207
10	สลักเกลียว M 16 x 450 มม. BOLT, MACHINE, M 16 x 450 mm	–	2	01110207
11	สลักเกลียว M 16 x 500 มม. BOLT, MACHINE, M 16 x 500 mm	1	–	01110208
12	สลักเกลียว M 16 x 600 มม. BOLT, MACHINE, M 16 x 600 mm	–	1	01110209
13	สลักเกลียวตลอด M 16 x 500 มม. BOLT, DOUBLE ARMING, M 16 x 500 mm	2	–	01120002
13a	สลักเกลียวตลอด M 16 x 600 มม. BOLT, DOUBLE ARMING, M 16 x 600 mm	–	2	01120004
14	สลักเกลียวห่วงกลม M 16 x 500 มม. BOLT, DOUBLE ARMING, ROUND EYE, M 16 x 500 mm	3	–	01130002
14a	สลักเกลียวห่วงกลม M 16 x 550 มม. BOLT, DOUBLE ARMING, ROUND EYE, M 16 x 550 mm	–	3	01130004
15	สลักห่วงกลม M 16x200 มม. BOLT, ROUND EYE M.16x200 mm	1	1	01140001

ข้อแนะนำ

1. การเข้าปลายสาย PIC ให้ดำเนินการตามแบบเลขที่ SAI-015/32038 (การประกอบเลขที่ 9568)
2. เพื่อป้องกันปัญหาเรื่องไฟไหม้ และหนูกัดท่อร้อยสาย (บริเวณต้น RISER POLE ที่มีหญ้าขึ้นหนาแน่น) ให้ใช้ท่อร้อยสายขึ้นเป็นท่อเหล็กกล้าเคลือบสังกะสี (RSC) และใช้หินเบอร์ 2 เทบริเวณรอบโคนเสารัศมีประมาณ 3 เมตร

SUGGESTION

1. PIC DEADENDING SHALL BE PROVIDED AS PER IN DWG. NO. SAI-015/32038 (ASSEMBLY NO. 9568)
2. TO PROTECT THE PROBLEM DUE TO FIRE AND MICE (THERE ARE THICK GROWTH OF GRASSES AROUND RISER POLE) USE GALVANIZED STEEL CONDUIT (RSC) FOR RISER AND COVER WITH ROCK (NO.2) OF 3 m IN RADIUS FROM RISER POLE .

กองวิศวกรรมไฟฟ้าและเครื่องกล ฝ่ายวิศวกรรม	การไฟฟ้าส่วนภูมิภาค	ใช้แทนแบบ ..... ถูกแทนโดยแบบ .....
ผู้เขียน ศุภกิจ บุญเรือง ผู้สำรวจ ..... วิศวกร ..... หัวหน้าแผนก ..... ผู้อำนวยการกอง ..... ผู้อำนวยการฝ่าย	ผู้ว่าการ ..... 18 ก.ค. 2539	เขียนเสร็จวันที่ 2 ก.ย. 39 แก้แบบวันที่ 30 เม.ย. 42 มิติเป็น ..... มาตราส่วน .....
รองผู้ว่าการ	การติดตั้งหัวเคเบิลที่เสาต้นสุดท้าย ระบบ 33 kV CABLE RISER INSTALLATION, AT DEADEND POLE 33 kV SYSTEM	แบบเลขที่ SA4-015/35013 แผ่นที่ 6 ของจำนวน 6 แผ่น