การประกอบเลขที่ ASSEMBLY NO. **0531**

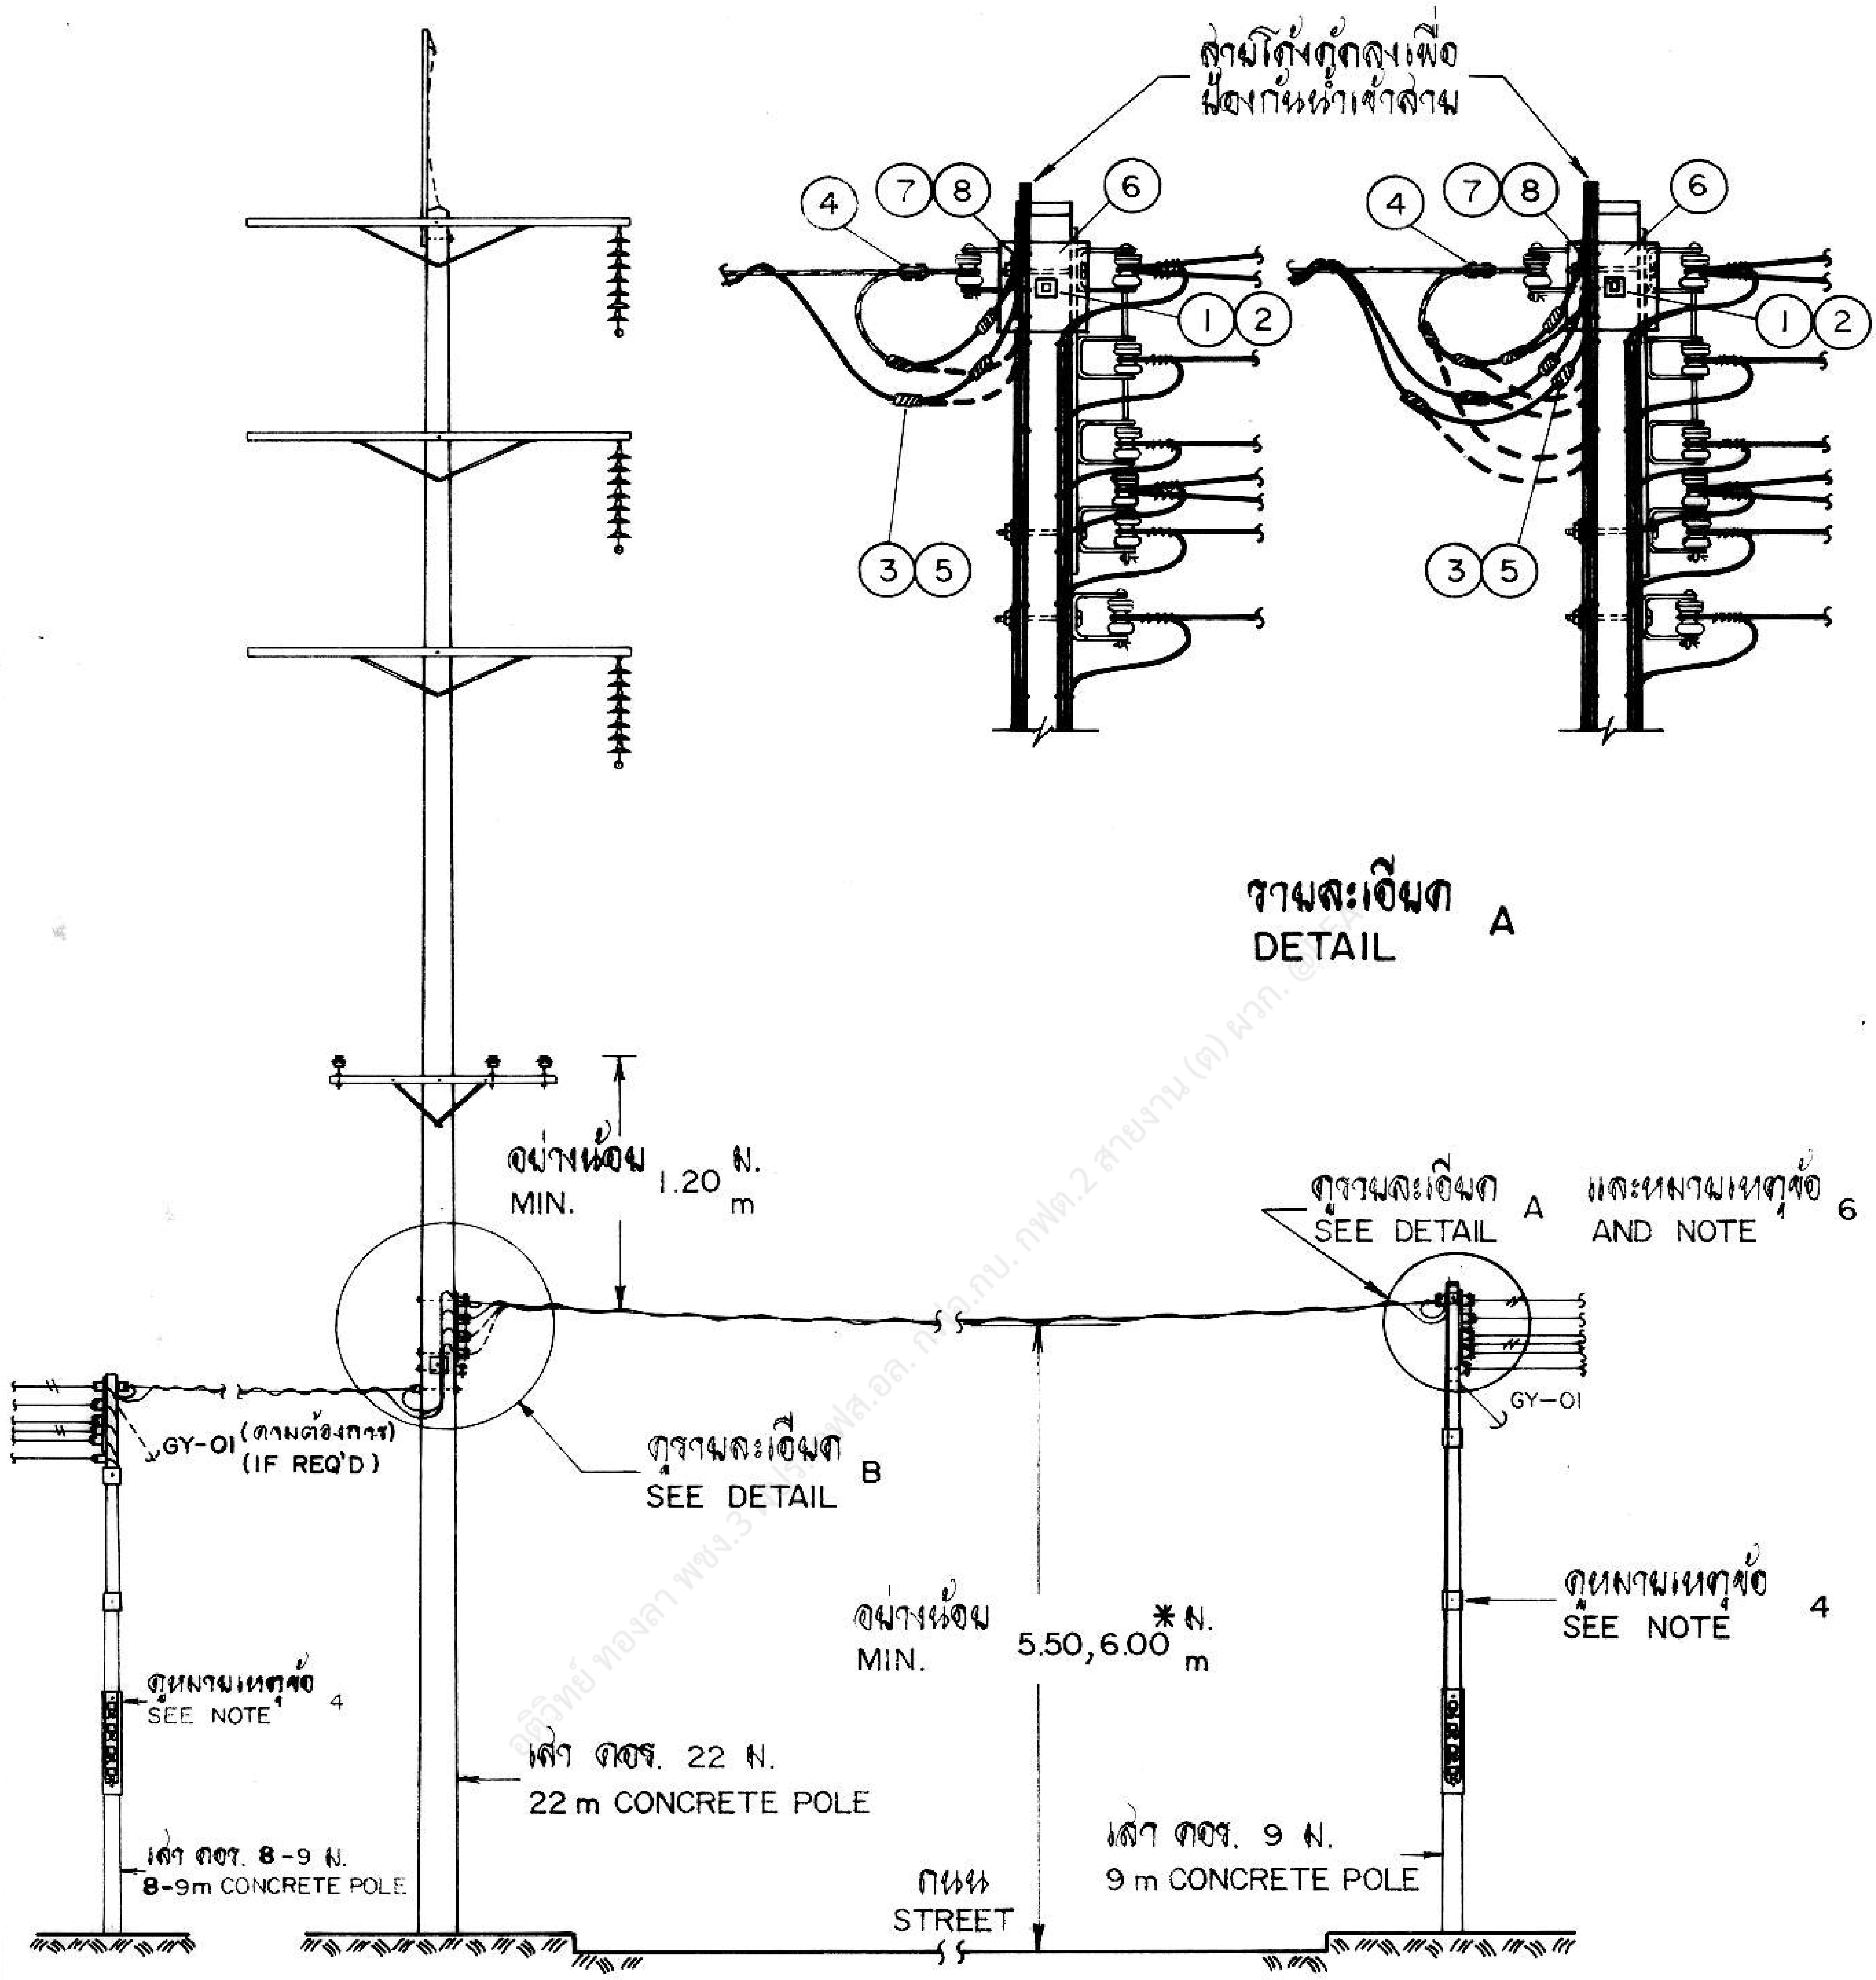
สายโค้งกู้ลงเพื่อป้องกันน้ำเข้าสาย
4
7
8
6
1
2
3
5
รายละเอียด DETAIL A
อย่างน้อย MIN. 1.20 ม. m
ดูรายละเอียด A SEE DETAIL A
และหมายเหตุข้อ 6 AND NOTE 6
GY-01 (ตามต้องการ) (IF REQ'D)
GY-01
ดูรายละเอียด B SEE DETAIL B
อย่างน้อย MIN. 5.50, 6.00* ม. m
ดูหมายเหตุข้อ 4 SEE NOTE 4
ดูหมายเหตุข้อ 4 SEE NOTE 4
เสา คอร. 22 ม. 22 m CONCRETE POLE
เสา คอร. 8-9 ม. 8-9m CONCRETE POLE
เสา คอร. 9 ม. 9 m CONCRETE POLE
ถนน STREET
≤ 50 ม. m

* สำหรับกรณีพาดสายข้ามทางหลวง
FOR STRINGING CROSS OVER THE HIGHWAY

กองวิศวกรรมไฟฟ้าและเครื่องกล ฝ่ายวิศวกรรม	การไฟฟ้าส่วนภูมิภาค	ใช้แทนแบบ ถูกแทนโดยแบบ
ผู้เขียน ผู้ตรวจ วิศวกร	ผู้ว่าการ 5 ส.ค. 26	เขียนเสร็จวันที่ 13 พ.ค. 26 แก้แบบครั้งที่ 21 มี.ค. 27

การประกอบเลขที่
ASSEMBLY NO. 0531

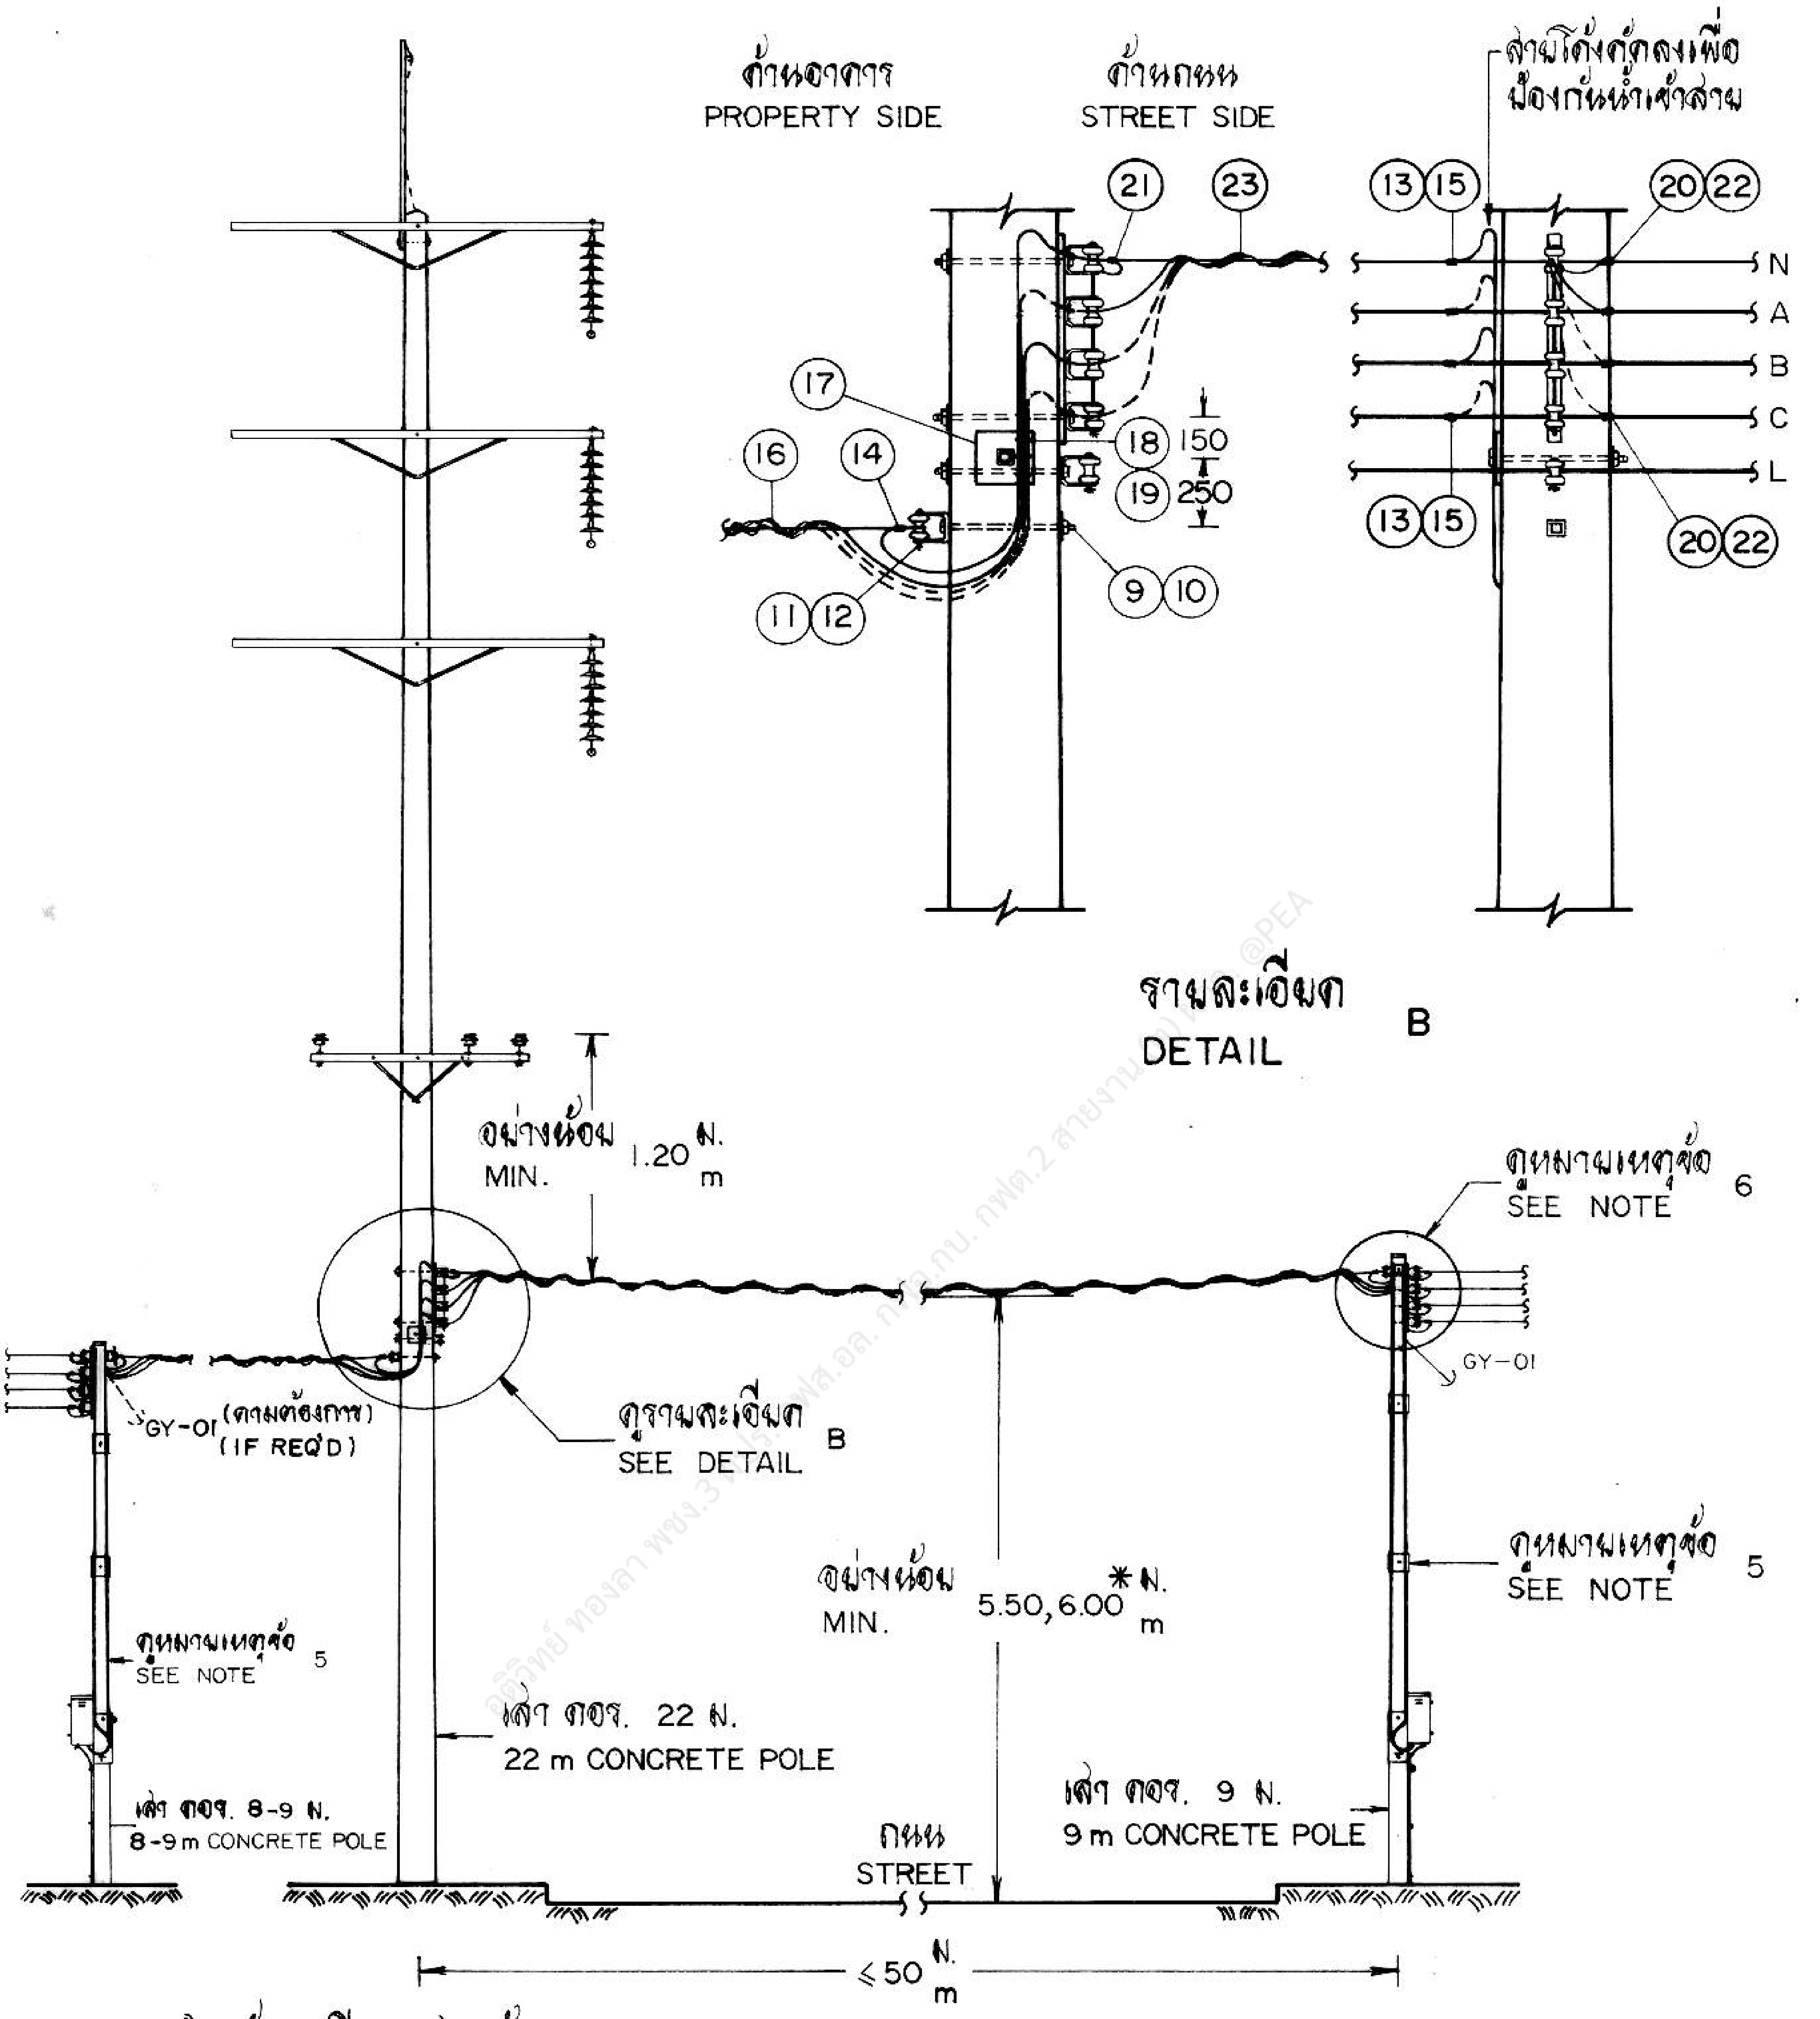

* สำหรับกรณีพาดสายข้ามทางหลวง
FOR STRINGING CROSS OVER THE HIGHWAY

อธิวิทย์ ทองลา พชง.3 [illegible] กฟส.อล. [illegible] กบ. กฟต.2 สายงาน [illegible] @PEA

กองวิศวกรรมไฟฟ้าและเครื่องกล
ฝ่ายวิศวกรรม

ผู้เขียน
ผู้สำรวจ
วิศวกร
หัวหน้าแผนก
ผู้อำนวยการกอง
ผู้อำนวยการฝ่าย

รองผู้ว่าการฝ่ายเทคนิค

การไฟฟ้าส่วนภูมิภาค

ผู้ว่าการ 5 ส.ค. 26

การติดตั้งมิเตอร์แรงต่ำที่เสาบริการ
บริเวณแนวสายส่ง 115 kV
II มิเตอร์ 3 เฟส

L.T. METER INSTALLATION ON SERVICE POLE
IN 115 kV SUBTRANSMISSION STRUCTURE AREA
II 3-PHASE METER

ใช้แทนแบบ
ถูกแทนโดยแบบ
เขียนเสร็จวันที่ 13 พ.ค. 26
แก้แบบวันที่ 21 มี.ค. 27
มิติเป็น มิลลิเมตร
มาตราส่วน 1 : 40, 1 : 125

แบบเลขที่ SAI-015/26012
แผ่นที่ 2 ของจำนวน 8 แผ่น

การประกอบเลขที่ 0531
ASSEMBLY NO. 0531

บัญชีวัสดุ สำหรับรายละเอียด A
BILL OF MATERIAL FOR DETAIL A

ลำดับที่ ITEM	รายละเอียด DESCRIPTION	จำนวน REQ'D	วัสดุเลขที่ MAT. NO.
1	สลักเกลียว M 16 X 200 มม. BOLT, MACHINE M 16 X 200 mm	1	01110202
2	แหวนสี่เหลี่ยมแบน 52 X 52 X 4.5 มม. รู Ø 18 มม. มอก. 258 WASHER, SQUARE, FLAT 52 X 52 X 4.5 mm HOLE Ø 18 mm TIS 258	2	01180100
3	พีจี. คอนเนคเตอร์ สลักคู่ หรือ คอนเนคเตอร์ ชนิดบีบ สำหรับสายอะลูมิเนียม ขนาดตามต้องการ CONNECTOR, PARALLEL GROOVE, DOUBLE BOLT, OR COMPRESSION TYPE, Al SIZE AS REQ'D	1–4	02300101-2 or 02210000-2
4	คอนเนคเตอร์ เข้าปลายสายอะลูมิเนียม ขนาดตามต้องการ CONNECTOR, DEADEND Al SIZE AS REQUIRED	1	02310000-1
5	PVC เทป กว้าง 19 มม (ใช้ความยาว 2 ม. ต่อ 1 จุด) มอก. 386 PVC TAPE, 19 mm WIDE (2 m LONG PER POINT) TIS 386		02180001 or 02180002
6	แผ่นรองรับมิเตอร์ ขนาด 20 X 20 ซม. METER PLATE, SIZE 20 X 20 cm	1	–
7	ตะปูหัวกลมแบน ยาว 15–20 มม. Ø 1 มม. มอก. 113 NAIL, ROUND MILD STEEL WIRE 15–20 mm LONG Ø 1 mm TIS 113	6	–
8	เข็มขัดรัดสาย (ทำด้วยลวดอะลูมิเนียมแบน 1 X 10 มม.) CABLE STRAP (MADE OF ARMOUR TAPE 1 X 10 mm)		02200000

บัญชีวัสดุ สำหรับรายละเอียด B
BILL OF MATERIAL FOR DETAIL B

สำหรับต่อแยกไปยังเสาบริการที่อยู่ด้านอาคาร
FOR TAP LINE TO PROPERTY SIDE SERVICE POLE

ลำดับที่ ITEM	รายละเอียด DESCRIPTION	จำนวน REQ'D I	 II	วัสดุเลขที่ MAT. NO.
9	สลักเกลียว M 16 X 450 มม. BOLT, MACHINE M 16 X 450 mm	2	2	01110207
10	แหวนสี่เหลี่ยมแบน 52 X 52 X 4.5 มม. รู Ø 18 มม. มอก. 258 WASHER, SQUARE, FLAT 52 X 52 X 4.5 mm HOLE Ø 18 mm TIS 258	3	3	01180100
11	ลูกรอกแรงต่ำ แบบ ข (แบบ 53–2) มอก. 227 INSULATOR, SPOOL TYPE L.T. TYPE B (CLASS 53–2) TIS 227	1	1	03030000
12	ที่จับลูกรอก สำหรับลูกรอก แบบ ข (แบบ 53–2) มอก. 227 CLEVIS, FLAT STEEL, FOR INSULATOR, TYPE B (CLASS 53–2) TIS 227	1	1	03130100
13	พีจี. คอนเนคเตอร์ สลักคู่ หรือ คอนเนคเตอร์ ชนิดบีบ สำหรับสายอะลูมิเนียม ขนาดตามต้องการ CONNECTOR, PARALLEL GROOVE, DOUBLE BOLT, OR COMPRESSION TYPE, Al SIZE AS REQ'D	2–4	4	02300101-2 or 02210000-2
14	คอนเนคเตอร์ เข้าปลายสายอะลูมิเนียม ขนาดตามต้องการ CONNECTOR, DEADEND Al SIZE AS REQUIRED	1	1	02310000-1
15	PVC เทป กว้าง 19 มม. (ใช้ความยาว 2 ม. ต่อ 1 จุด) มอก. 386 PVC TAPE, 19 mm WIDE (2 m LONG PER POINT)' TIS 386			02180001 or 02180002
16	สายพันรวมหลายสาย ขนาดและจำนวนสายตามตารางที่ 1 ความยาวตามต้องการ MULTIPLEX CABLE, SIZE AND NO. OF CABLE, ACCORDING TO TABLE 1, LENGTH AS REQ'D		–	–
16a	สายพันรวมสี่สาย ขนาดและความยาวตามต้องการ QUADRUPLEX CABLE, SIZE AND LENGTH AS REQUIRED	–		–
17	แผ่นรองรับมิเตอร์ ขนาด 20 X 20 ซม. METER PLATE, SIZE 20 X 20 cm	1	1	–
18	ตะปูหัวกลมแบน ยาว 15–20 มม. Ø 1 มม. มอก. 113 NAIL, ROUND MILD STEEL WIRE 15–20 mm LONG, Ø 1 mm TIS 113	6	6	–
19	เข็มขัดรัดสาย (ทำด้วยลวดอะลูมิเนียมแบน 1 X 10 มม.) CABLE STRAP (MADE OF ARMOUR TAPE 1 X 10 mm)			02200000

กองวิศวกรรมไฟฟ้าและเครื่องกล
ฝ่ายวิศวกรรม

ผู้เขียน
ผู้สำรวจ
วิศวกร
หัวหน้าแผนก
ผู้อำนวยการกอง
ผู้อำนวยการฝ่าย

รองผู้ว่าการฝ่ายเทคนิค

การไฟฟ้าส่วนภูมิภาค

ผู้ว่าการ ๕ ธ.ค. ๒๖

การติดตั้งมิเตอร์แรงต่ำที่เสาบริการ
บริเวณแนวสายส่ง 115 kV

L.T. METER INSTALLATION ON SERVICE POLE
IN 115 kV SUBTRANSMISSION STRUCTURE AREA

ใช้แทนแบบ
ถูกแทนโดยแบบ
เขียนเสร็จวันที่ 13 พ.ค. 26
แก้แบบวันที่ 21 มี.ค. 27
ผิดเป็น
มาตราส่วน

แบบเลขที่ SAI–015/26012
แผ่นที่ 3 ของจำนวน 8 แผ่น

4 ส.ค. 2526

การประกอบเลขที่ 0531
ASSEMBLY NO.

บัญชีวัสดุ สำหรับรายละเอียด B
BILL OF MATERIAL FOR DETAIL B

สำหรับต่อแยกสายข้ามถนนไปยังเสาบริการ
FOR TAP LINE CROSS OVER THE STREET TO SERVICE POLE

ลำดับที่ ITEM	รายละเอียด DESCRIPTION	จำนวน REQ' D I	 II	วัสดุเลขที่ MAT. NO.
20	พีจี. คอนเนคเตอร์ สลักคู่ หรือคอนเนคเตอร์ ชนิดบีบ สำหรับสายอะลูมิเนียม ขนาดตามต้องการ CONNECTOR, PARALLEL GROOVE, DOUBLE BOLT, OR COMPRESSION TYPE, Al SIZE AS REQ' D.	2-4	4	02300101-2 or 02210000-2
21	คอนเนคเตอร์ เข้าปลายสายอะลูมิเนียม ขนาดตามต้องการ CONNECTOR, DEADEND, Al SIZE AS REQUIRED	1	1	02310000-1
22	PVC เทป กว้าง 19 มม. (ใช้ความยาว 2 ม. ต่อ 1 จุด) มอก. 386 PVC TAPE, 19 mm WIDE (2 m LONG PER POINT) TIS 386			02180001 02180002
23	สายพันร่วมหลายสาย ขนาดและจำนวนสายตามตารางที่ 1 ความยาวตามต้องการ MULTIPLEX CABLE, SIZE AND NO. OF CABLES, ACCORDING TO TABLE 1, LENGTH AS REQUIRED		–	–
23a	สายพันร่วมสี่สาย ขนาดและความยาวตามต้องการ QUADRUPLEX CABLE, SIZE AND LENGTH AS REQUIRED	–		–

การจัดทำเข็มขัดรัดสายด้วยสายอะลูมิเนียมแบน 1X10 มม.

- สำหรับสายพันร่วมสองสาย หรือสายพันร่วมสามสาย ใช้ลวดอะลูมิเนียมแบน 1X10 มม. ยาว 15 ซม. ต่อหนึ่งจุด
- สำหรับสายพันร่วมสี่สาย ใช้ลวดอะลูมิเนียมแบน 1X10 มม. ยาว 18 ซม. ต่อหนึ่งจุด

ข้อแนะนำในการใช้งาน

1. ในกรณีที่เสาระบบจำหน่ายแรงสูงมีอุปกรณ์สำคัญติดตั้งอยู่ก่อนแล้ว เช่น รีโคลสเซอร์ หม้อแปลง หรือชุดสวิตช์ สามารถใช้แบบนี้ในการติดตั้งมิเตอร์แรงต่ำได้ แต่ให้เปลี่ยนสลักเกลียววัสดุลำดับที่ ⑨ เป็น สลักเกลียว M 16X250 มม. (วัสดุเลขที่ 01110203)
2. การต่อสายเฟสเข้ามิเตอร์แรงต่ำ 1 เฟส 2 สาย ให้ต่อได้อย่างมาก 2 จุด ต่อสายเมน (สายพันร่วมหลายสาย) 1 เส้น และให้จัดแบ่งโหลดให้สมดุลย์กันหรือใกล้เคียงกัน

SUGGESTION

1. THIS CONSTRUCTION DRAWING CAN BE APPLIED FOR INSTALLING THE L.T. METER IN AREA THAT IS EXISTING MAIN EQUIPMENT SUCH AS RECLOSER, TRANSFORMER OR SWITCHES ON THE DISTRIBUTION POLE, BY CHANGING THE MACHINE BOLT ITEM ⑨ TO M 16X250 mm (MAT. NO. 01110203)
2. THE MAXIMUM CONNECTION OF THE INCOMING PHASE CABLE OF 1-PHASE, 2-WIRE, L.T. METER TO THE MAIN LINE SHALL BE NOT EXCEEDED 2 POINTS ON MAIN LINE (MULTIPLEX CABLE) AND THE LOAD OF MAIN LINE SHALL BE BALANCED OR EQUALLY SHARED.

กองวิศวกรรมไฟฟ้าและเครื่องกล ฝ่ายวิศวกรรม	การไฟฟ้าส่วนภูมิภาค	ใช้แทนแบบ ถูกแทนโดยแบบ
ผู้เขียน ผู้สำรวจ วิศวกร หัวหน้าแผนก ผู้อำนวยการกอง ผู้อำนวยการฝ่าย	ผู้ว่าการ ๕ ส.ค. ๒๖	เขียนเสร็จวันที่ 13 พ.ค. 26 แก้แบบวันที่ 21 มี.ค. 27
	การติดตั้งมิเตอร์แรงต่ำที่เสาบริการ บริเวณแนวสายส่ง 115 kV	มิติเป็น มาตราส่วน
รองผู้ว่าการฝ่ายเทคนิค	L.T. METER INSTALLATION ON SERVICE POLE IN 115 kV SUBTRANSMISSION STRUCTURE AREA	แบบเลขที่ SAI-015/26012 แผ่นที่ 4 ของจำนวน 8 แผ่น

4 ส.ค. 2526

การประกอบเลขที่ ASSEMBLY NO.	0531

หมายเหตุ

1. บัญชีวัสดุ : I สำหรับการติดตั้งมิเตอร์แรงต่ำ 1 เฟส 2 สาย

   II สำหรับการติดตั้งมิเตอร์แรงต่ำ 3 เฟส 4 สาย
2. ขนาดของสายไฟฟ้าที่ต่อเข้าและออกจากมิเตอร์แรงต่ำ 1 เฟส 2 สาย ดูตารางที่ 1 ในแบบเลขที่ SAI-015/24024 (การประกอบเลขที่ 0517) แผ่นที่ 5
3. ขนาดของสายไฟฟ้าที่ต่อเข้าและออกจากมิเตอร์แรงต่ำ 3 เฟส 4 สาย ดูแบบเลขที่ I40-015/120246 (การประกอบเลขที่ 0503)
4. การติดตั้งมิเตอร์แรงต่ำ 1 เฟส 2 สาย บนเสาคอนกรีต 8-9 ม. และแป้นไม้สำหรับยึดสายเข้าและออกจากมิเตอร์ให้ติดตั้งและใช้วัสดุสำหรับติดตั้ง ตามแบบเลขที่ SAI-015/23070, SAI-015/23071, SAI-015/23072 และ SAI-015/26013 (การประกอบเลขที่ 0309, 0524, 0525 และ 0532)
5. การติดตั้งมิเตอร์แรงต่ำ 3 เฟส 4 สาย บนเสาคอนกรีต 8-9 ม. และแป้นไม้สำหรับยึดสายเข้าและออกจากมิเตอร์ ให้ติดตั้งและใช้วัสดุสำหรับติดตั้ง ตามแบบเลขที่ SAI-015/21039 และ SAI-015/23056 (การประกอบเลขที่ 0518 และ 0522)
6. การประกอบอุปกรณ์ที่หัวเสา สำหรับการติดตั้งมิเตอร์ 1 เฟส 2 สาย บนเสาคอนกรีต 8-9 ม. และการติดตั้งมิเตอร์แรงต่ำ 3 เฟส 4 สาย บนเสาคอนกรีต 9 ม. อนุโลมให้ติดตั้งและใช้วัสดุสำหรับติดตั้งตามแบบการติดตั้งมิเตอร์ 3 เฟส 4 สาย บนเสาคอนกรีต 8 ม. แบบเลขที่ SAI-015/23056 (การประกอบเลขที่ 0522) แผ่นที่ 2
7. สายพันร่วมหลายสายให้ประกอบขึ้นเอง ตามแบบเลขที่ SAI-015/20016
8. ขนาดของสายศูนย์ต่ำสุด ของสายพันร่วมหลายสายที่พาดข้ามถนน :

   อะลูมิเนียมเปลือย อะลูมิเนียมอัลลอย 35 ต.มม.

   อะลูมิเนียมแกนเหล็ก 35/6 ต.มม. (25/4 ต.มม. สำหรับสายพันร่วมสองสาย)
9. ระยะต่ำสุดในแนวดิ่งของสายไฟฟ้าแรงต่ำ 400/230 โวลต์

   เหนือทางสาธารณะ และไม่เป็นทางผ่านของรถบรรทุก 4.60 ม.

   เหนือทางที่ใช้สำหรับคนเดินเท้าเท่านั้น 3.70 ม.
10. กระแสใช้งานของสายพันร่วมหลายสายเท่ากับ 75% ของค่ากระแสใช้งานที่กำหนดในแบบเลขที่ SAI-015/22047

กองวิศวกรรมไฟฟ้าและเครื่องกล ฝ่ายวิศวกรรม	การไฟฟ้าส่วนภูมิภาค	ใช้แทนแบบ ถูกแทนโดยแบบ เขียนเสร็จวันที่ 13 พ.ค. 26 แก้แบบวันที่ 21 มี.ค. 27 มิติเป็น มาตราส่วน
ผู้เขียน ผู้สำรวจ วิศวกร หัวหน้าแผนก ผู้อำนวยการกอง ผู้อำนวยการฝ่าย	ผู้ว่าการ ๕ ส.ค. ๒๖ การติดตั้งมิเตอร์แรงต่ำที่เสาบริการ บริเวณแนวสายส่ง 115 kV	
รองผู้ว่าการฝ่ายเทคนิค	L.T. METER INSTALLATION ON SERVICE POLE IN 115 kV SUBTRANSMISSION STRUCTURE AREA	แบบเลขที่ SAI-015/26012 แผ่นที่ 5 ของจำนวน 8 แผ่น

4 ส.ค. 2526

การประกอบเลขที่ ASSEMBLY NO. 0531

NOTES

1. BILL OF MATERIAL : I FOR 1-PHASE, 2-WIRE, L.T. METER INSTALLATION.
   II FOR 3-PHASE, 4-WIRE, L.T. METER INSTALLATION.
2. THE SIZE OF INCOMING AND OUTGOING CABLE FOR 1-PHASE, 2-WIRE, L.T. METER SEE TABLE I IN DRAWING NO. SAI-015/24024 (ASSEMBLY NO. 0517) SHEET NO. 5
3. THE SIZE OF INCOMING AND OUTGOING CABLE FOR 3-PHASE, 4-WIRE, L.T. METER SEE DRAWING NO. I40-015/120246 (ASSEMBLY NO. 0503)
4. 1-PHASE, 2-WIRE, L.T. METER INSTALLATION ON 8—9 m CONCRETE POLE, CONSTRUCT AS DRAWING NO. SAI-015/23070, SAI-015/23071, SAI-015/23072 AND SAI-015/26013 (ASSEMBLY NO. 0309, 0524, 0525 AND 0532)
5. 3-PHASE, 4-WIRE, L.T. METER INSTALLATION ON 8—9 m CONCRETE POLE, CONSTRUCT AS DRAWING NO. SAI-015/21039 AND SAI-015/23056 (ASSEMBLY NO. 0518 AND 0522).
6. THE POLE TOP ASSEMBLY FOR 1-PHASE, 2-WIRE, L.T. METER INSTALLATION ON 8—9 m CONCRETE POLE AND 3-PHASE, 4-WIRE, L.T. METER INSTALLATION ON 9 m. CONCRETE POLE, PERMIT TO CONSTRUCT AS 3-PHASE, 4-WIRE, L.T. METER INSTALLATION ON 8 m CONCRETE POLE IN DRAWING NO. SAI-015/23056 (ASSEMBLY NO. 0522) SHEET NO. 2
7. MULTIPLEX CABLE SHALL BE ASSEMBLIED ACCORDING TO DRAWING NO. SAI-015/20016
8. THE MINIMUM SIZE OF NEUTRAL OF MULTIPLEX CABLE THAT STRINGING CROSS OVER THE STREET :
   BARE ALUMINIUM, Al-ALLOY 35 mm^2
   ACSR 35/6 mm^2 (25/4 mm^2 FOR DUPLEX CABLE)
9. THE MINIMUM GROUND CLEARANCE OF 400/230 V L.T. LINE :
   OVER RESIDENTIAL DRIVEWAYS NOT SUBJECT TO TRUCK TRAFFIC 4.60 METERS
   OVER WAYS ACCESSIBLE TO PEDESTRIANS ONLY 3.70 METERS
10. THE MULTIPLEX CABLE CURRENT RATING SHALL BE EQUALLED TO 75% OF THE CURRENT RATING SPECIFIED IN DRAWING NO. SAI-015/22047

กองวิศวกรรมไฟฟ้าและเครื่องกล ฝ่ายวิศวกรรม	การไฟฟ้าส่วนภูมิภาค	ใช้แทนแบบ ถูกแทนโดยแบบ
ผู้เขียน ผู้สำรวจ วิศวกร หัวหน้าแผนก ผู้อำนวยการกอง ผู้อำนวยการฝ่าย	ผู้ว่าการ ๕ ส.ค. ๒๖	เขียนเสร็จวันที่ 13 พ.ค. 26 แก้แบบวันที่ 21 มี.ค. 27
	การติดตั้งมิเตอร์แรงต่ำที่เสาบริการ บริเวณแนวสายส่ง 115 kV	ผิดเป็น มาตราส่วน
~~รองผู้ว่าการฝ่ายเทคนิค~~	L.T. METER INSTALLATION ON SERVICE POLE IN 115 kV SUBTRANSMISSION STRUCTURE AREA	แบบเลขที่ SAI-015/26012 แผ่นที่ 6 ของจำนวน 8 แผ่น

- 4 ส.ค. 2526

การประกอบเลขที่
ASSEMBLY NO. **0531**

ขนาดของสายพันร่วมหลายสายที่ใช้เป็นสายเมนสำหรับกิโลวัตต์ชั่วโมงมิเตอร์ 1 เฟส 2 สาย 220 โวลต์ จะต้องมีขนาดไม่เล็กกว่าที่กำหนดในตารางข้างล่างนี้:

TABLE SIZE OF MULTIPLEX CABLE AS MAIN LINE FOR 1-PHASE, 2-WIRE 220 V KILOWATTHOUR METER SHALL BE NOT LESS THAN THAT SPECIFIED IN TABLE BELOW:

พิกัดกระแสและจำนวนของมิเตอร์ RATING AND NO. OF METER				ขนาดของสายไฟฟ้า ต.มม. SIZE OF CONDUCTOR mm^2	ชนิดของสายพันร่วมหลายสาย TYPE OF MULTIPLEX CABLE
3(9), 5(15)	แอมป์ AMP	1–4	เครื่อง SETS	25	สายพันร่วมสองสาย DUPLEX CABLE
10(30), 20(40)	แอมป์ AMP	1	เครื่อง SET		
30(60)	แอมป์ AMP	1	เครื่อง SET	35	
3(9), 5(15) & 10(30)	แอมป์ AMP แอมป์ AMP	1–3 1	เครื่อง SETS เครื่อง SET		
10(30)	แอมป์ AMP	2	เครื่อง SETS		
3(9), 5(15) & 20(40)	แอมป์ AMP แอมป์ AMP	1–3 1	เครื่อง SETS เครื่อง SET	50	
20(40)	แอมป์ AMP	2	เครื่อง SETS		
50(100)	แอมป์ AMP	1	เครื่อง SET	50, 70	
3(9), 5(15) & 30(60)	แอมป์ AMP แอมป์ AMP	1–3 1	เครื่อง SETS เครื่อง SET	70	

กองวิศวกรรมไฟฟ้าและเครื่องกล ฝ่ายวิศวกรรม	การไฟฟ้าส่วนภูมิภาค	ใช้แทนแบบ ถูกแทนโดยแบบ เขียนเสร็จวันที่ 13 พ.ค. 26 แก้แบบวันที่ 21 มีค. 27 ผิดเป็น มาตราส่วน
ผู้เขียน ผู้สำรวจ วิศวกร หัวหน้าแผนก ผู้อำนวยการกอง ผู้อำนวยการฝ่าย	ผู้ว่าการ ๕ ธ.ค. ๒๖ การติดตั้งมิเตอร์แรงต่ำที่เสาบริการ บริเวณแนวสายส่ง 115 kV	
รองผู้ว่าการฝ่ายเทคนิค	L.T. METER INSTALLATION ON SERVICE POLE IN 115 kV SUBTRANSMISSION STRUCTURE AREA	แบบเลขที่ SAI-015/26012 แผ่นที่ 7 ของจำนวน 8 แผ่

4 ส.ค. 2526

การประกอบเลขที่
ASSEMBLY NO. 0531

ตารางที่ TABLE 1 (ต่อ CONT.)

พิกัดกระแสและจำนวนของมิเตอร์ RATING AND NO. OF METER	ขนาดของสายไฟฟ้า ต.มม. SIZE OF CONDUCTOR mm^2	ชนิดของสายพันร่วมหลายสาย TYPE OF MULTIPLEX CABLE
3(9), 5(15) แอมป์ AMP 1–3 เครื่อง SETS & 50(100) แอมป์ AMP 1 เครื่อง SET	95	สายพันร่วมสองสาย DUPLEX CABLE
10(30) แอมป์ AMP 3–4 เครื่อง SETS	35	สายพันร่วมสามสาย TRIPLEX CABLE
20(40) แอมป์ AMP 3–4 เครื่อง SETS	50	

อดิวิทย์ ทองลา พชง.3 ผปร. กฟส.อล. กฟจ.กบ. กฟต.2 สายงาน (ต) ผวก. @PEA

กองวิศวกรรมไฟฟ้าและเครื่องกล
ฝ่ายวิศวกรรม

การไฟฟ้าส่วนภูมิภาค

ผู้เขียน
ผู้ตรวจ
วิศวกร
หัวหน้าแผนก
ผู้อำนวยการกอง
ผู้อำนวยการฝ่าย

รองผู้ว่าการฝ่ายเทคนิค

ผู้ว่าการ ๕ ส.ค. ๒๖

การติดตั้งมิเตอร์แรงต่ำที่เสาบริการ
บริเวณแนวสายส่ง 115 kV

L.T. METER INSTALLATION ON SERVICE POLE
IN 115 kV SUBTRANSMISSION STRUCTURE AREA

ใช้แทนแบบ
ถูกแทนโดยแบบ
เขียนเสร็จวันที่ 13 พ.ค. 26
แก้แบบวันที่ 21 มี.ค. 27
มิติเป็น
มาตราส่วน
แบบเลขที่ SAI–015/26012
แผ่นที่ 8 ของจำนวน 8 แผ่น

4 ส.ค. 2526