การประกอบเลขที่ ASSEMBLY NO. 0105

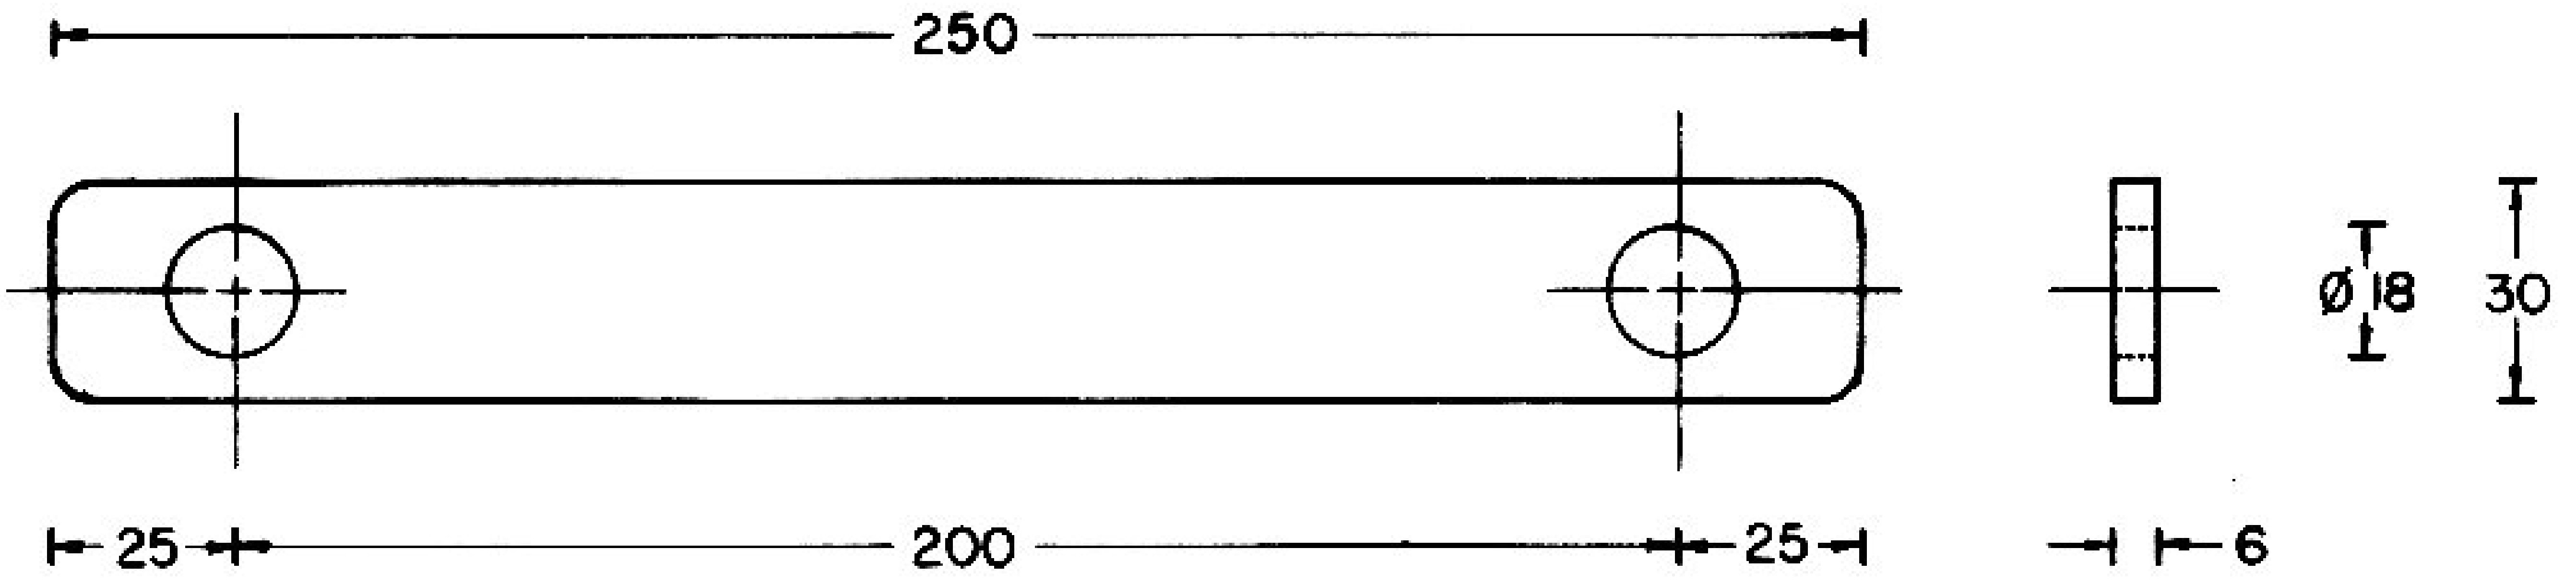

สำหรับเข้าปลายสายแรงต่ำ 2 สาย
FOR 2 L.T. DISTRIBUTION LINE DEADENDING (วัสดุเลขที่ MAT. NO. 0139)

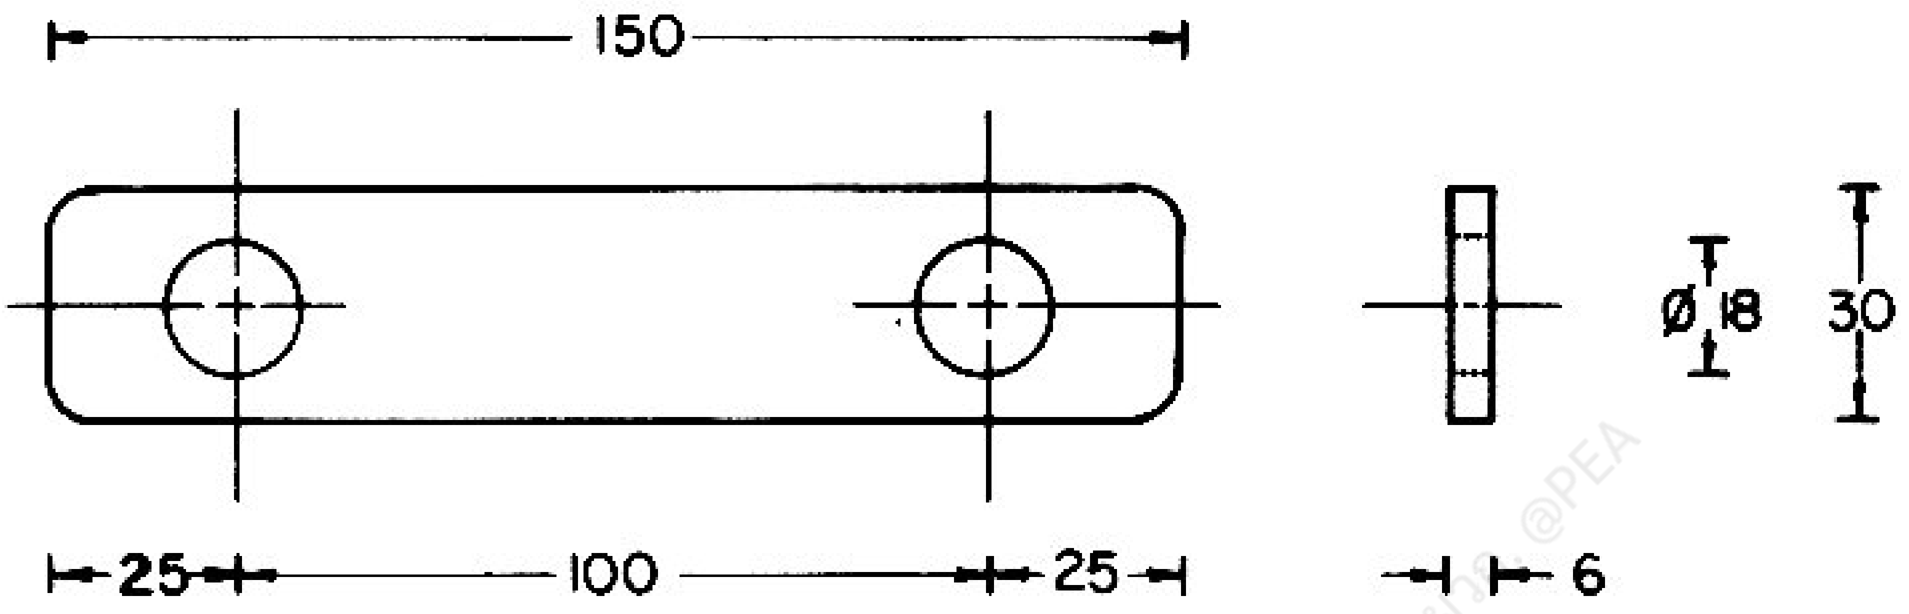

สำหรับต่อแยกสาย
FOR TAP LINE (วัสดุเลขที่ MAT. NO. 0138)

หมายเหตุ

1 ชุบสังกะสีตามมาตรฐาน กฟภ.

2 อาจทำด้วยเหล็กประกับไม้คอน ขนาด 30 X 6 X 760 มม. (วัสดุเลขที่ 0120) แล้วทาด้วยสีกันสนิม และสีเทา

NOTES

1. HOT DIP GALVANIZED ACCORDING TO P.E.A. STANDARD.

2. IT MAY BE MADE BY 30 X 6 X 760 mm BRACE (MAT. NO. 0120) AND THEN PAINTED WITH A PRIMER COAT AND GRAY WEATHER-RESISTANCE COATS.

กองวิศวกรรมไฟฟ้าและเครื่องกล
ฝ่ายวิศวกรรม
ผู้เขียน
ผู้ตรวจ
วิศวกร สิทธิพงษ์
หัวหน้าแผนก
หัวหน้ากอง
ผู้อำนวยการฝ่าย
รองผู้ว่าการฝ่ายเทคนิค

การไฟฟ้าส่วนภูมิภาค
ผู้ว่าการ
- 1 ก.ย. 25[illegible]

เหล็กแผ่น
สำหรับเข้าปลายสายแรงต่ำ 2 สาย และต่อแยกสาย

STEEL PLATE
FOR 2 L.T. DISTRIBUTION LINE DEADENDING AND TAP LINE

ใช้แทนแบบ
ถูกแทนโดยแบบ
เขียนเสร็จวันที่ 31 พ.ค. 22
แก้แบบวันที่
มิติเป็น มม.
มาตราส่วน 1 : 25
แบบเลขที่ SAI-015/22030
แผ่นที่ 1 จากจำนวน 1 แผ่น

1 ก.ย. 2523