การประกอบเลขที่
ASSEMBLY NO. 5269

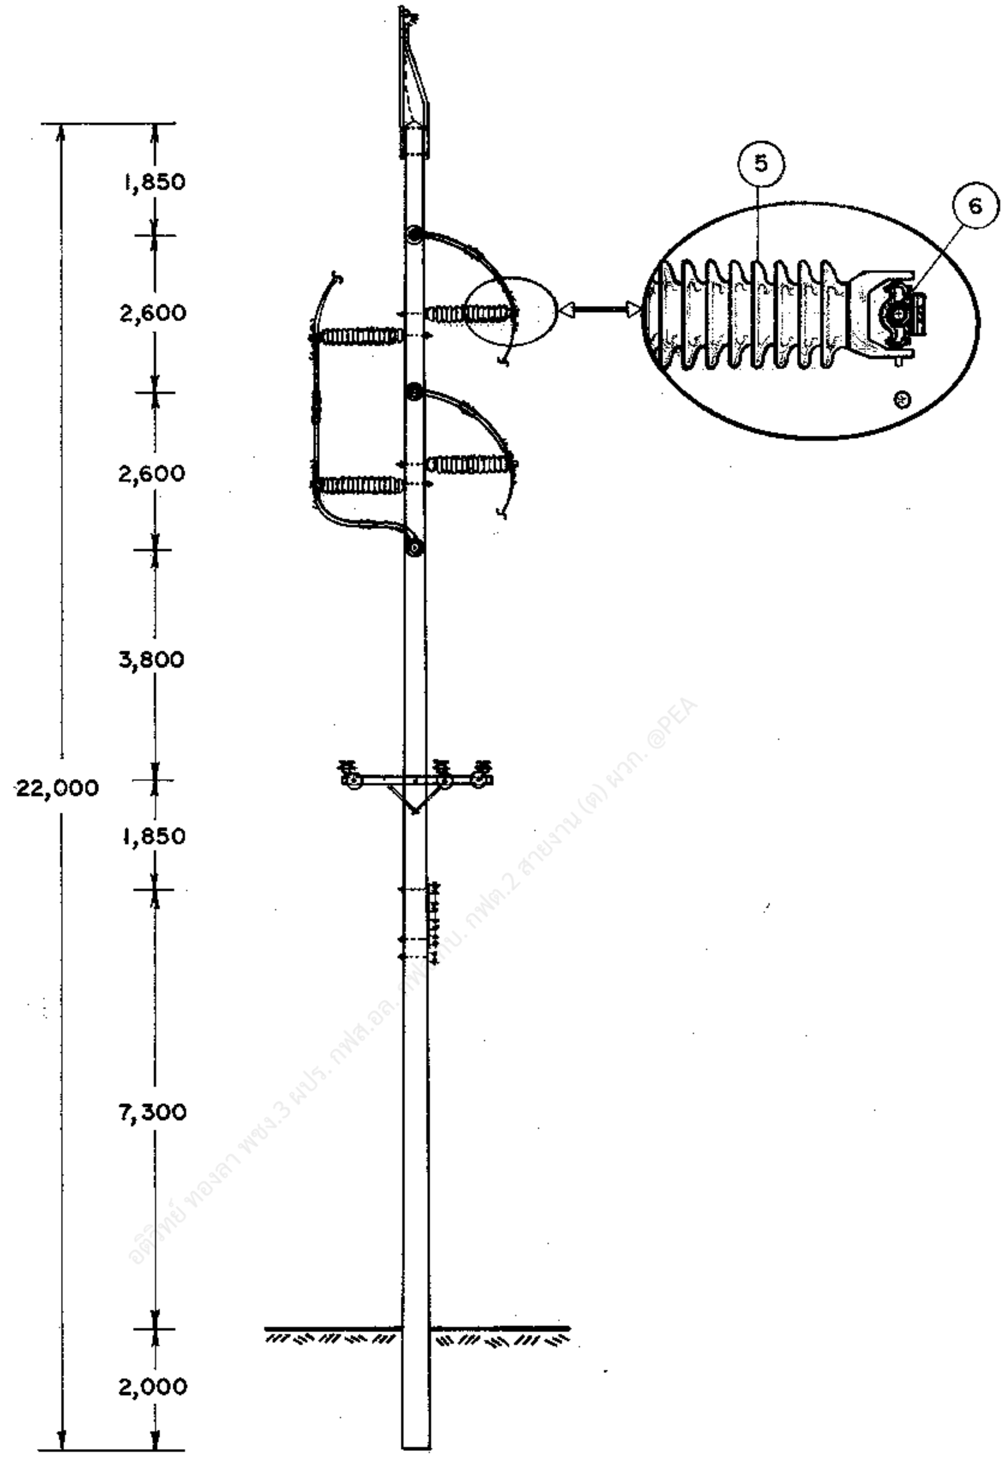

อดิศักดิ์ ทองลา พชง.3 ผปร. กฟส.อล. กฟฉ.2 สายงาน (ด) ผวก. @PEA

กองวิศวกรรมไฟฟ้าและเครื่องกล
ฝ่ายวิศวกรรม

ผู้เขียน อัมพร.
ผู้ตรวจ
วิศวกร ว.ค.
หัวหน้าแผนก ว.ค.
ผู้อำนวยการกอง
ผู้อำนวยการฝ่าย

รองผู้ว่าการฝ่ายเทคนิค

การไฟฟ้าส่วนภูมิภาค

ผู้ว่าการ 10 มี.ค. 35

115 kV วงจรเดี่ยว สายไฟฟ้าคู่
เสาสำหรับสลับเฟสสาย
SD–TR–1

115 kV SINGLE CIRCUIT DOUBLE CONDUCTOR
TRANSPOSE STRUCTURE
TYPE SD–TR–1

ใช้แทนแบบ
ถูกแทนโดยแบบ
เขียนเสร็จวันที่ 24 ก.พ. 35
แก้แบบวันที่
มิติเป็น มิลลิเมตร
มาตราส่วน 1 : 125

แบบเลขที่ SAL–015/35006
แผ่นที่ 1 ของจำนวน 3 แผ่น

10 มี.ค. 2535

การประกอบเลขที่ **5269**
ASSEMBLY NO.

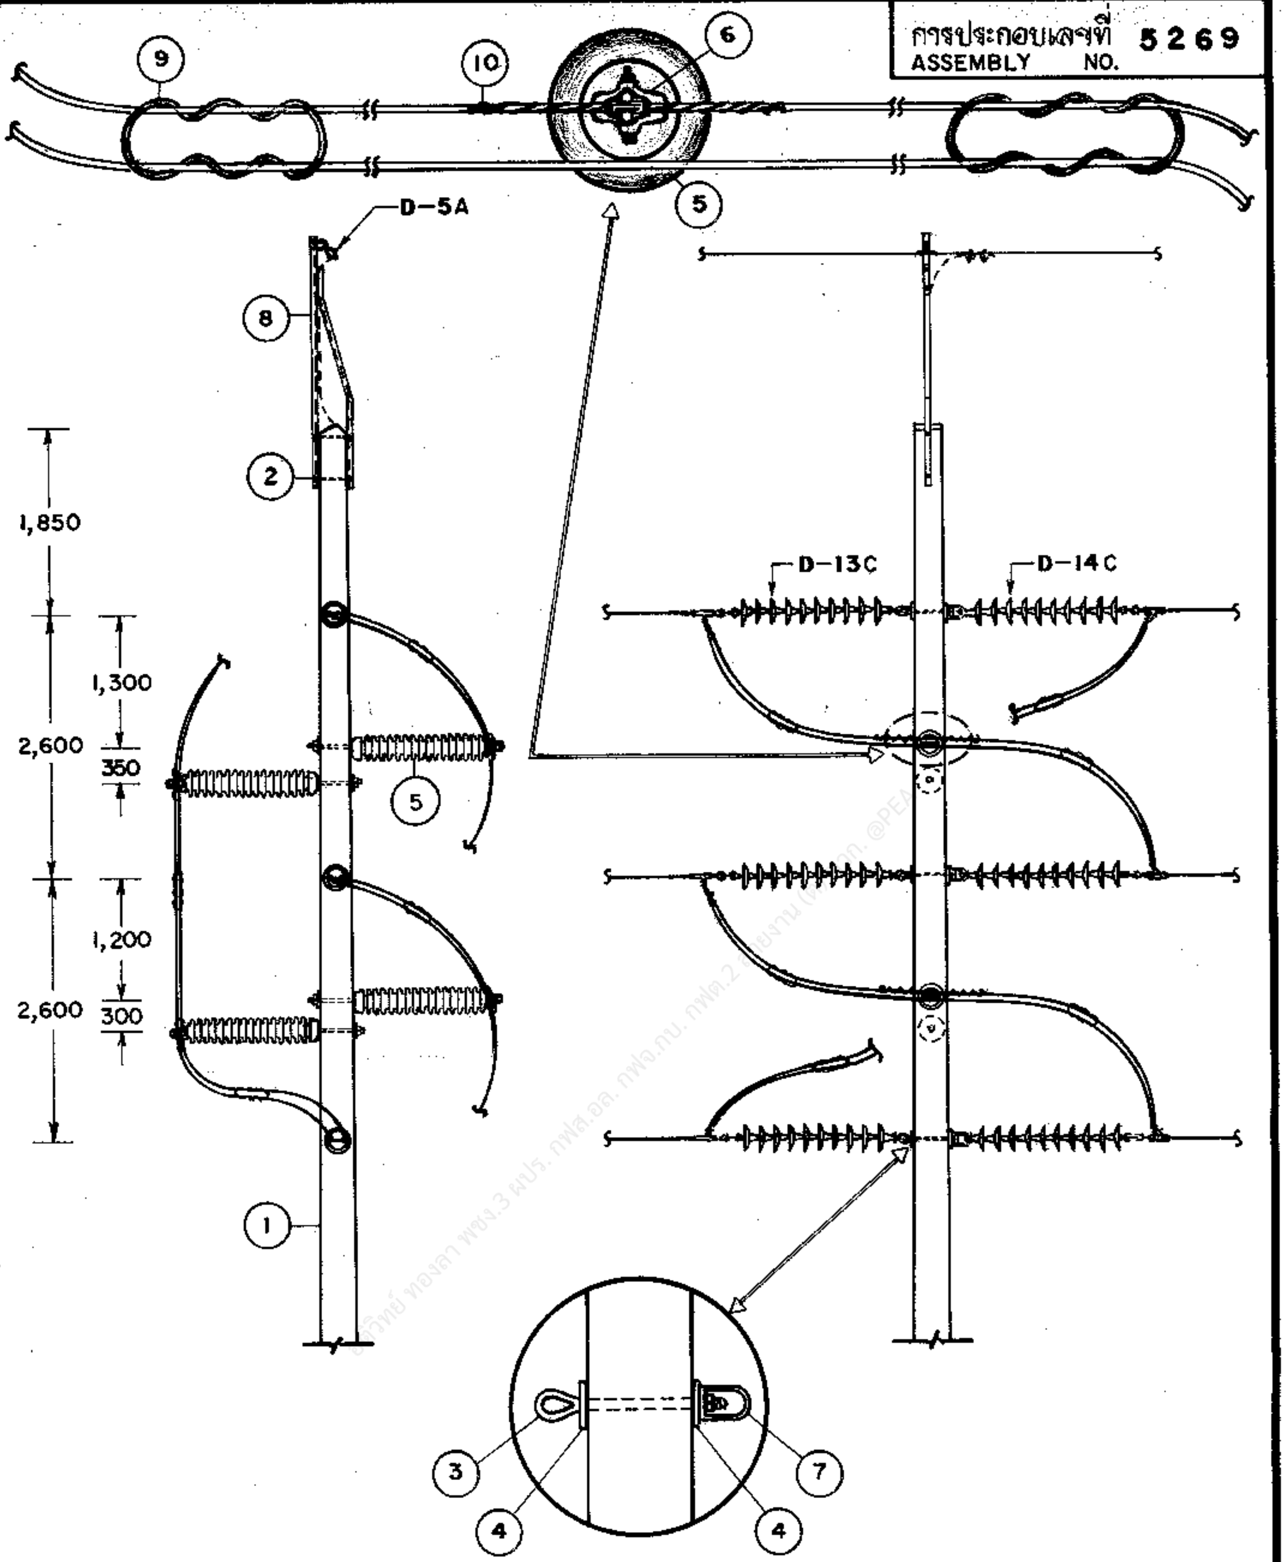
9
10
6
5
D-5A
8
2
1,850
1,300
2,600
350
5
1,200
2,600
300
1
D-13C
D-14C
3
4
4
7

สุวิทย์ ทองสา พชง.3 ฝปร. กฟส.อล. กฟอ.กน. กฟภ.2 ...งาน @PEA

กองวิศวกรรมไฟฟ้าและเครื่องกล ฝ่ายวิศวกรรม	**การไฟฟ้าส่วนภูมิภาค**	ใช้แทนแบบ ถูกแทนโดยแบบ
ผู้เขียน ผู้สำรวจ วิศวกร หัวหน้าแผนก ผู้อำนวยการกอง ผู้อำนวยการฝ่าย	ผู้ว่าการ 10 มี.ค. 35	เขียนเสร็จวันที่ 24 ก.พ.35 แก้แบบวันที่ มิติเป็น มิลลิเมตร
	115 kV วงจรเดี่ยว สายไฟฟ้าคู่ เสาสำหรับสลับเฟสสาย แบบ SD-TR-1	มาตราส่วน 1 : 75
รองผู้ว่าการฝ่ายเทคนิค	115 kV SINGLE CIRCUIT DOUBLE CONDUCTOR TRANSPOSE STRUCTURE TYPE SD-TR-1	แบบเลขที่ SAI-015/35006 แผ่นที่ 2 ของจำนวน 3 แผ่น

10 มี.ค. 2535

การประกอบเลขที่ ASSEMBLY NO. **5269**

บัญชีวัสดุ
BILL OF MATERIAL

ลำดับที่ ITEM	รายละเอียด DESCRIPTION	จำนวน REQ'D	วัสดุเลขที่ MAT. NO.
1	เสาคอนกรีต 22 ม. POLE, CONCRETE 22 m LONG	1	00010011 (0041)
2	สลักเกลียว M 16X350 มม. BOLT, MACHINE, M 16X350 mm	3	01110205 (0225)
3	สลักห่วงโอแวล M 20X350 มม. BOLT, OVAL EYE, M 20X350 mm	3	01150100 (0260)
4	แหวนสี่เหลี่ยมแบน 62X62X6 มม. รู Ø 22 มม. มอก. 258 WASHER, SQUARE, FLAT, 62X62X6 mm HOLE Ø 22 mm TIS 258	12	01180101 (0356)
5	ลูกถ้วย แบบโพสท์ ติดตั้งในแนวนอน ระบบ 115 kV พร้อมอุปกรณ์ประกอบ ยึดกับเสา (สลักเกลียว M 20X400 มม.) INSULATOR, POST TYPE, HORIZONTAL MOUNTING, 115 kV COMP. WITH ACCESSORIES FOR POLE MOUNTING (BOLT, M 20X400 mm)	4	—
6	แคล้มป์จับสาย ใช้ประกอบลูกถ้วย แบบโพสท์ 115 kV CLAMP, TOP TYPE, FOR POST TYPE INSULATOR 115 kV	4	—
7	อายเล็ท สำหรับสลักเกลียว M 20 EYELET FOR BOLT, M 20	3	01180002 (0346)
8	เหล็กฉากรับสายล่อฟ้า ทางโค้ง OVERHEAD GROUND WIRE CORNER BAYONET	1	01010005 (0136)
9	ปรีฟอร์มแยกสาย SPACER, HELICAL ROD, PREFORMED	7	02240000 (0918)
10	ปรีฟอร์มไลน์การ์ด ขนาดตามต้องการ LINE GUARD, PREFORMED SIZE AS REQUIRED	4	—

	รายละเอียด DESCRIPTION		
D-13C	การประกอบลูกถ้วยแขวน SUSPENSION INSULATOR ASSEMBLY	3	
D-14C	การประกอบลูกถ้วยแขวน SUSPENSION INSULATOR ASSEMBLY	3	
D-5A	การต่อสายล่อฟ้า OVERHEAD GROUND WIRE CONNECTION	1	
D-10A	ฐานรากเสา POLE FOUNDATION	1	

กองวิศวกรรมไฟฟ้าและเครื่องก
ฝ่ายวิศวกรรม

ผู้เขียน ____
ผู้สำรวจ ____
วิศวกร ____
หัวหน้าแผนก ____
ผู้อำนวยการกอง ____
ผู้อำนวยการฝ่าย ____
รองผู้ว่าการฝ่ายเทคนิค

การไฟฟ้าส่วนภูมิภาค

ผู้ว่าการ ____ 10 มี.ค. 35

115 kV วงจรเดี่ยว สายไฟฟ้าคู่
เสาสำหรับสลับเฟสสาย
แบบ SD-TR-1

115 kV SINGLE CIRCUIT DOUBLE CONDUCTOR
TRANSPOSE STRUCTURE
TYPE SD-TR-1

ใช้แทนแบบ ____
ถูกแทนโดยแบบ ____
เขียนเสร็จวันที่ 24 ก.พ. 35
แก้แบบวันที่ ____
มิติเป็น ____
มาตราส่วน ____
แบบเลขที่ SAI-015/35006
แผ่นที่ 3 ของจำนวน 3 แผ่น

10 มี.ค. 2535