
การประกอบเลขที่ ASSEMBLY NO. 5204

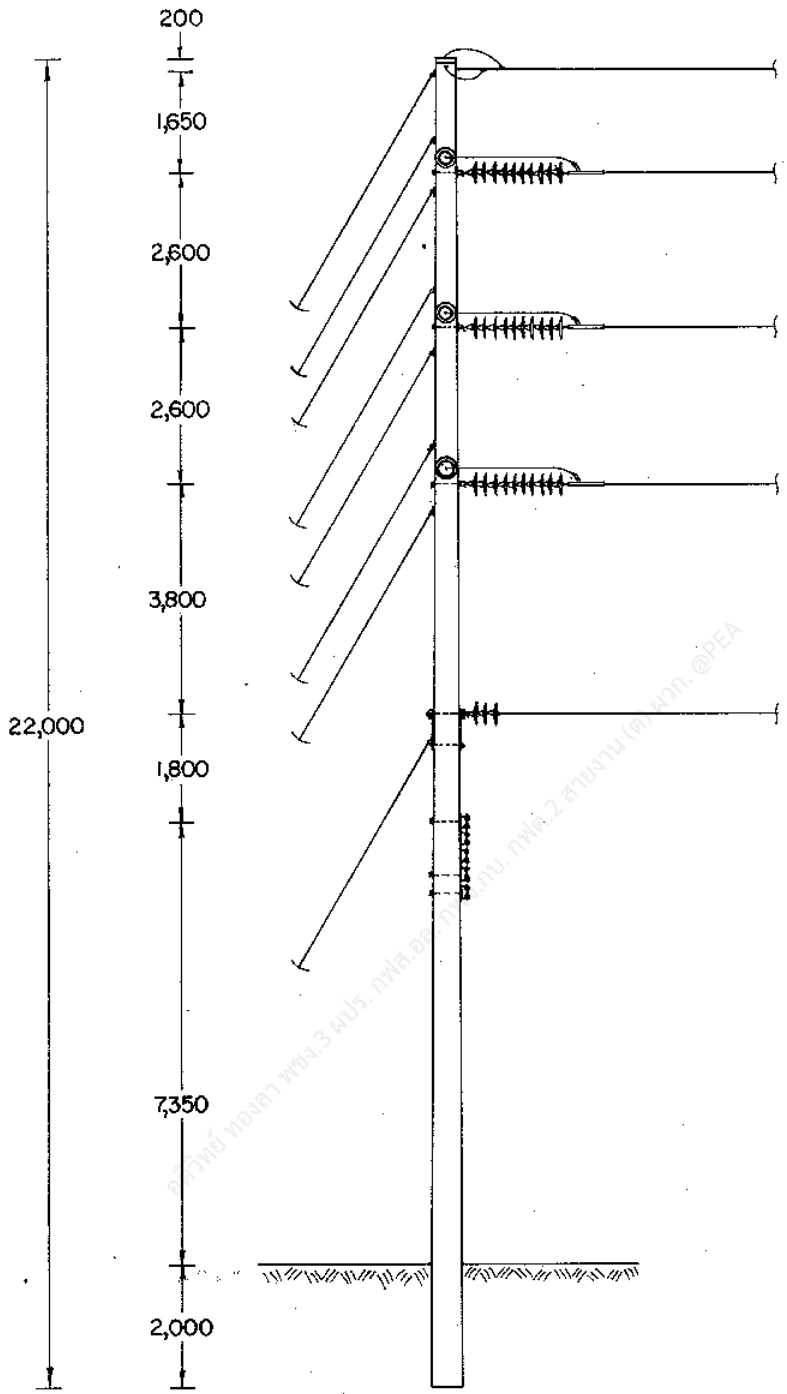

กองวิศวกรรมไฟฟ้าและเครื่องกล
ฝ่ายวิศวกรรม

ผู้เขียน
ตรวจ
วิศวกร
หัวหน้าแผนก
หัวหน้ากอง
ผู้อำนวยการฝ่าย

รองผู้ว่าการฝ่ายเทคนิค

การไฟฟ้าส่วนภูมิภาค

ผู้ว่าการ

115 kV วงจรเดี่ยว - สายไฟฟ้าเดี่ยว
เสาเดี่ยวสำหรับทางโค้ง 90°
แบบ SS-LA-1


115 kV SINGLE CIRCUIT SINGLE CONDUCTOR
SINGLE POLE, 90° ANGLE STRUCTURE
TYPE SS—LA—1

ใช้แทนแบบ
ถูกแทนโดยแบบ
เขียนแล้วเสร็จวันที่ 2 N.O. 23
แก้แผ่นนี้ที่
มิติเป็น มม.
มาตราส่วน 1 : 125

แบบเลขที่ SAI-015/23001
แผ่นที่ 1 ของจำนวน 3 แผ่น

19 ต.ค. 2523

การประกอบเลขที่ ASSEMBLY NO. 5204

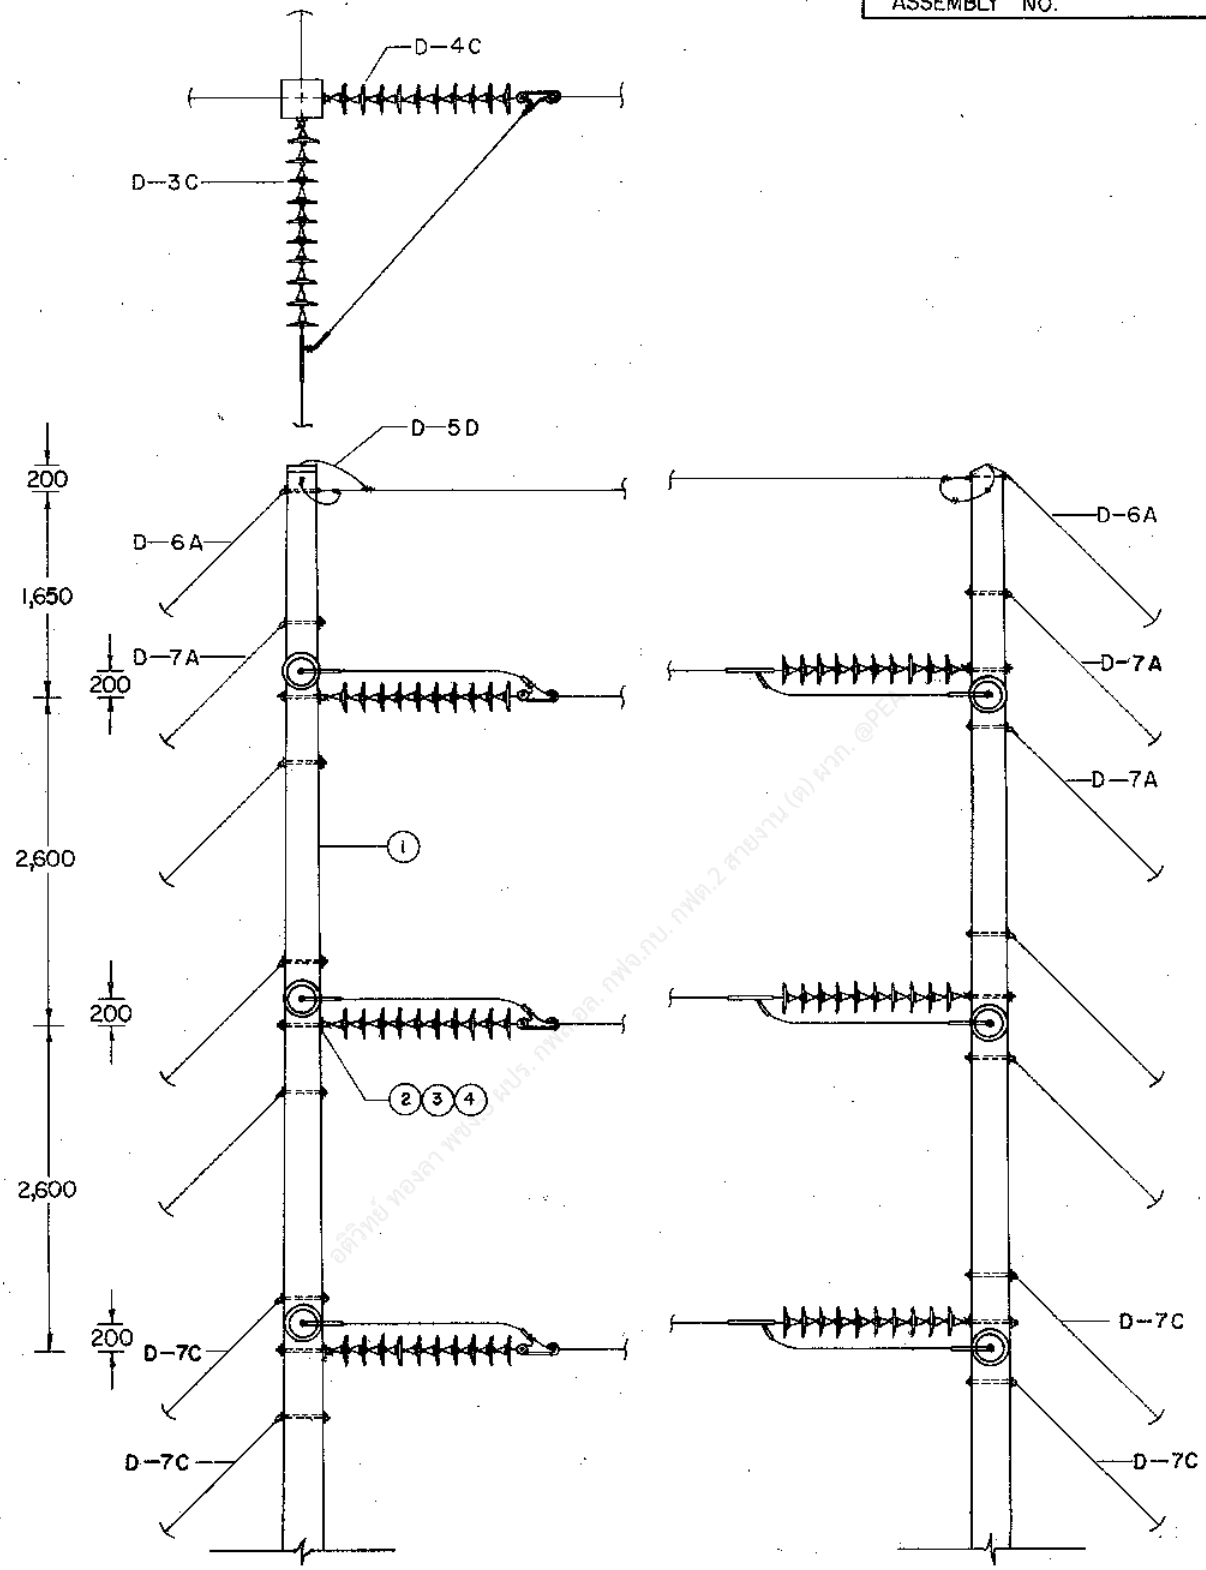

กองวิศวกรรมไฟฟ้าและเครื่องกล ฝ่ายวิศวกรรม	การไฟฟ้าส่วนภูมิภาค	ใช้แทนแบบ ถูกแทนโดยแบบ
ผู้เรียน ผู้สำรวจ วิศวกร หัวหน้าแผนก หัวหน้ากอง ผู้อำนวยการฝ่าย	ผู้ว่าการ 115 kV วงจรเดี่ยว สายไฟฟ้าเดี่ยว เสาเดี่ยวสำหรับทางโค้ง 9.0° แบบ SS-LA-1	เรียนเสร็จวันที่ 2 พ.ค. 23 แก้แบบวันที่ 15 ต.ค. 40 มิติเป็น มม. มาตราส่วน 1 : 60
รองผู้ว่าการฝ่ายเทคนิค	115 kV SINGLE CIRCUIT SINGLE CONDUCTOR SINGLE POLE, 90° ANGLE STRUCTURE TYPE SS-LA-1	แบบเลขที่ SAI-015/23001 แผ่นที่ 2 รวมจำนวน 3 แผ่น

19 กันยายน 2523

การประกอบเลขที่
ASSEMBLY NO. 5204

บัญชีวัสดุ
BILL OF MATERIAL

ลำดับที่ ITEM	รายละเอียด DESCRIPTION	จำนวน REQ'D	รหัสวัสดุเลขที่ MAT. NO.
1	เสาคอนกรีต 22 ม. POLE, CONCRETE 22 m. LONG	1	00010011 (0041)
2	สลักห่วงโอแวล M 20 X 350 มม. BOLT, OVAL EYE M 20 X 350 mm	6	01150100 (0260)
3	แหวนสี่เหลี่ยมแบน 62 X 62 X 6 มม. รู Ø 22 มม. มอก. 258 WASHER, SQUARE, FLAT 62 X 62 X 6 mm HOLE Ø 22 mm TIS. 258	12	01180101 (0356)
4	แหวนสปริก M 20 มอก. 259 WASHER, LOCK, M 20, TIS 259	6	01180302 (0366)

รายละเอียด
DETAIL

D-3C	การประกอบลูกถ้วยแขวน SUSPENSION INSULATOR ASSEMBLY	3	
D-4C	การประกอบลูกถ้วยแขวน SUSPENSION INSULATOR ASSEMBLY	3	
D-5D	การต่อสายล่อฟ้า OVERHEAD GROUND WIRE CONNECTION	1	
D-6A	การประกอบสายยึดโยงลวดเหล็กตีเกลียว 50 ต.มม. STEEL STRANDED WIRE 50 mm² GUY ASSEMBLY	2	
D-6C	การประกอบสายยึดโยงลวดเหล็กตีเกลียว 50 ต.มม. STEEL STRANDED WIRE 50 mm² GUY ASSEMBLY	—	
D-7A	การประกอบสายยึดโยงลวดเหล็กตีเกลียว 95 ต.มม. STEEL STRANDED WIRE 95 mm² GUY ASSEMBLY	8	
D-7C	การประกอบสายยึดโยงลวดเหล็กตีเกลียว 95 ต.มม. STEEL STRANDED WIRE 95 mm² GUY ASSEMBLY	4	
D-9A	สมอบกคอนกรีต CONCRETE ANCHOR	2	
D-10A	ฐานรากเสา POLE FOUNDATION	1	

กองวิศวกรรมไฟฟ้าและเครื่องกล
ฝ่ายวิศวกรรม

ผู้เขียน
ผู้ตรวจ
วิศวกร
หัวหน้าแผนก
หัวหน้ากอง
ผู้อำนวยการฝ่าย
รองผู้ว่าการฝ่ายเทคนิค

การไฟฟ้าส่วนภูมิภาค

ผู้ว่าการ

115 kV วงจรเดี่ยว สายไฟฟ้าเดี่ยว
เสาเดี่ยวสำหรับทางโค้ง 90°
แบบ SS-LA-1

115 kV SINGLE CIRCUIT SINGLE CONDUCTOR
SINGLE POLE, 90° ANGLE STRUCTURE
TYPE SS—LA—1

ใช้แทนแบบ
ถูกแทนโดยแบบ
เขียนเสร็จวันที่ 2 พ.ค. 23
แก้แบบวันที่ 15 ก.ย. 40
มิติเป็น
มาตราส่วน

แบบเลขที่ SAI-015/23001
แผ่นที่ 3 ของจำนวน 3 แผ่น

19 มี.ค. 2523