
การประกอบเลขที่ 3414
ASSEMBLY NO.

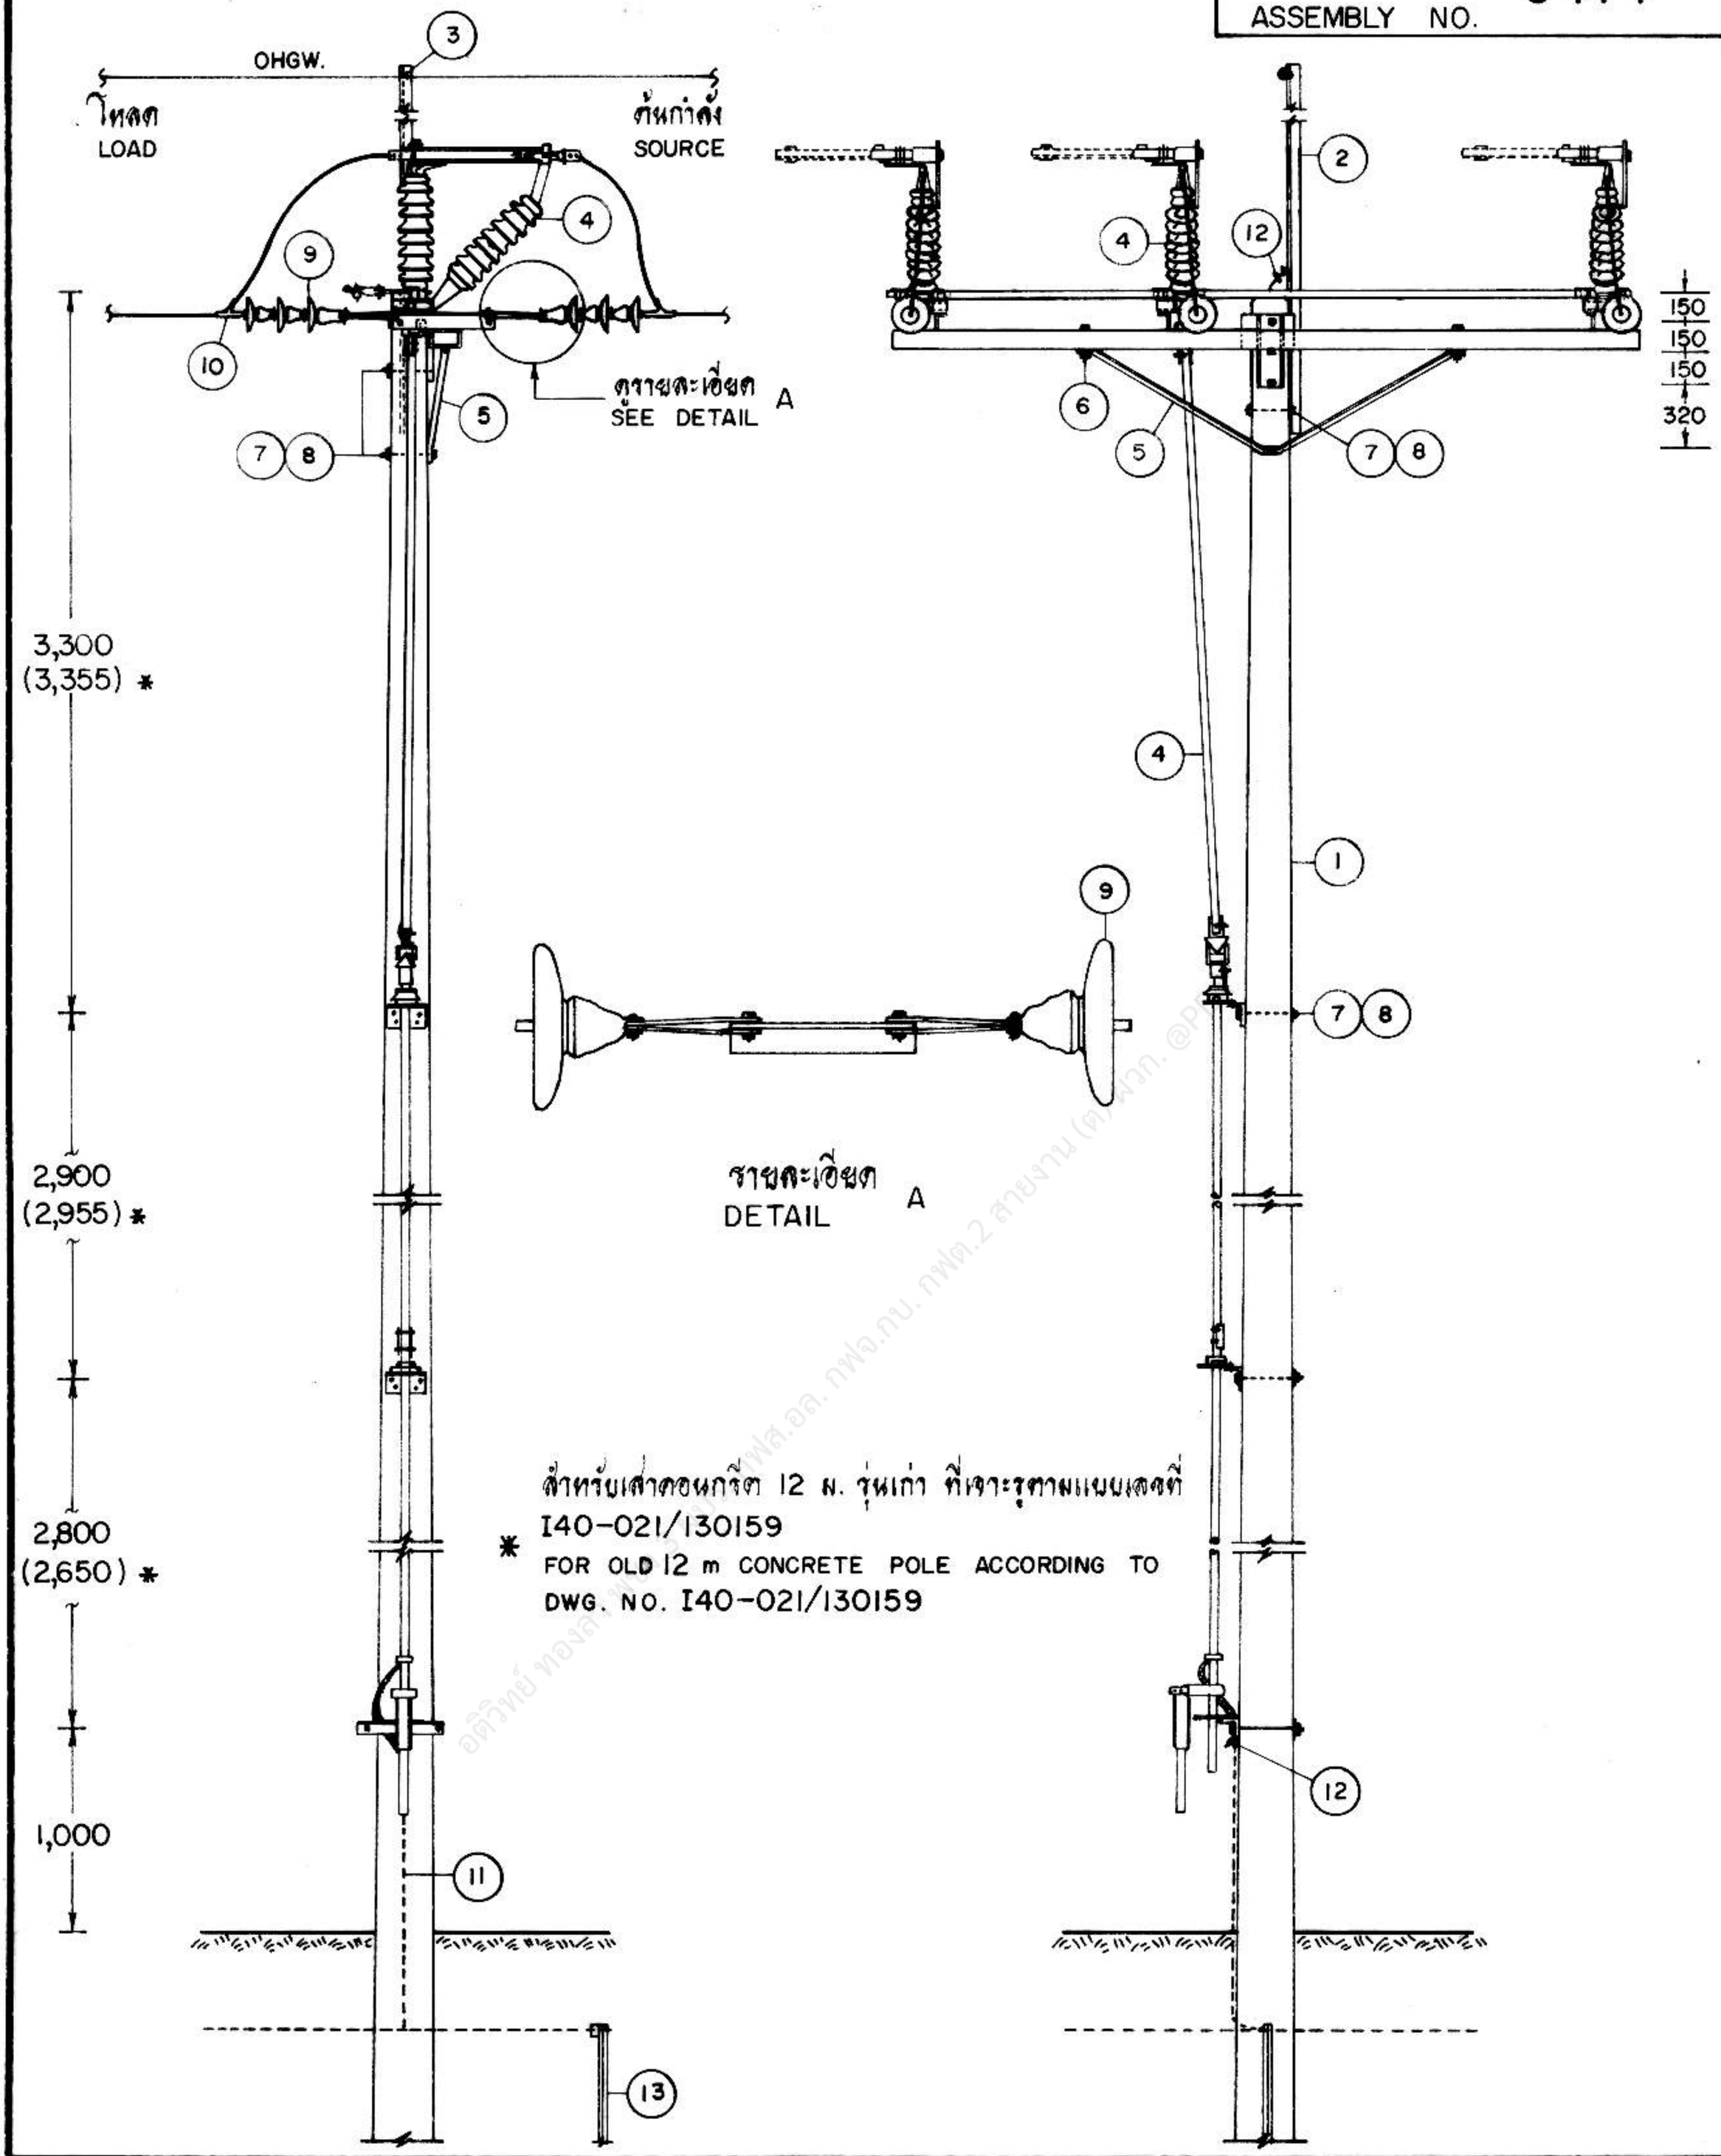


กองวิศวกรรมไฟฟ้าและเครื่องกล ฝ่ายวิศวกรรม	การไฟฟ้าส่วนภูมิภาค	ใช้แทนแบบ ถูกแทนโดยแบบ เขียนเสร็จวันที่ 17 ธ.ค. 23 แก้แบบวันที่ มิติเป็น มม. มาตราส่วน 1 : 50
ผู้เขียน ผู้สำรวจ วิศวกร หัวหน้าแผนก หัวหน้ากอง ผู้อำนวยการฝ่าย	ผู้ว่าการ 25 ธ.ค. 23	
รองผู้ว่าการฝ่ายโทดนัด	การติดตั้งสวิตช์เปิดได้เมื่อมีโหลด 3 ขา 33 kV (โหลดเบรคสวิตช์) 33 kV TRIPLE POLE LOAD INTERRUPTER SWITCH INSTALLATION (LOAD BREAK SWITCH)	แบบเลขที่ SAI-015/23092 แผ่นที่ 1 ของจำนวน 4 แผ่น

25 ธ.ค. 2523

ลักษณะการติดตั้งโหลดเบรคสวิทช์ในระบบจำหน่ายวงจรเดี่ยว

THE ARRANGEMENT OF LOAD BREAK SWITCH INSTALLATION IN SINGLE CIRCUIT LINE

การประกอบเลขที่ ASSEMBLY NO. 3414

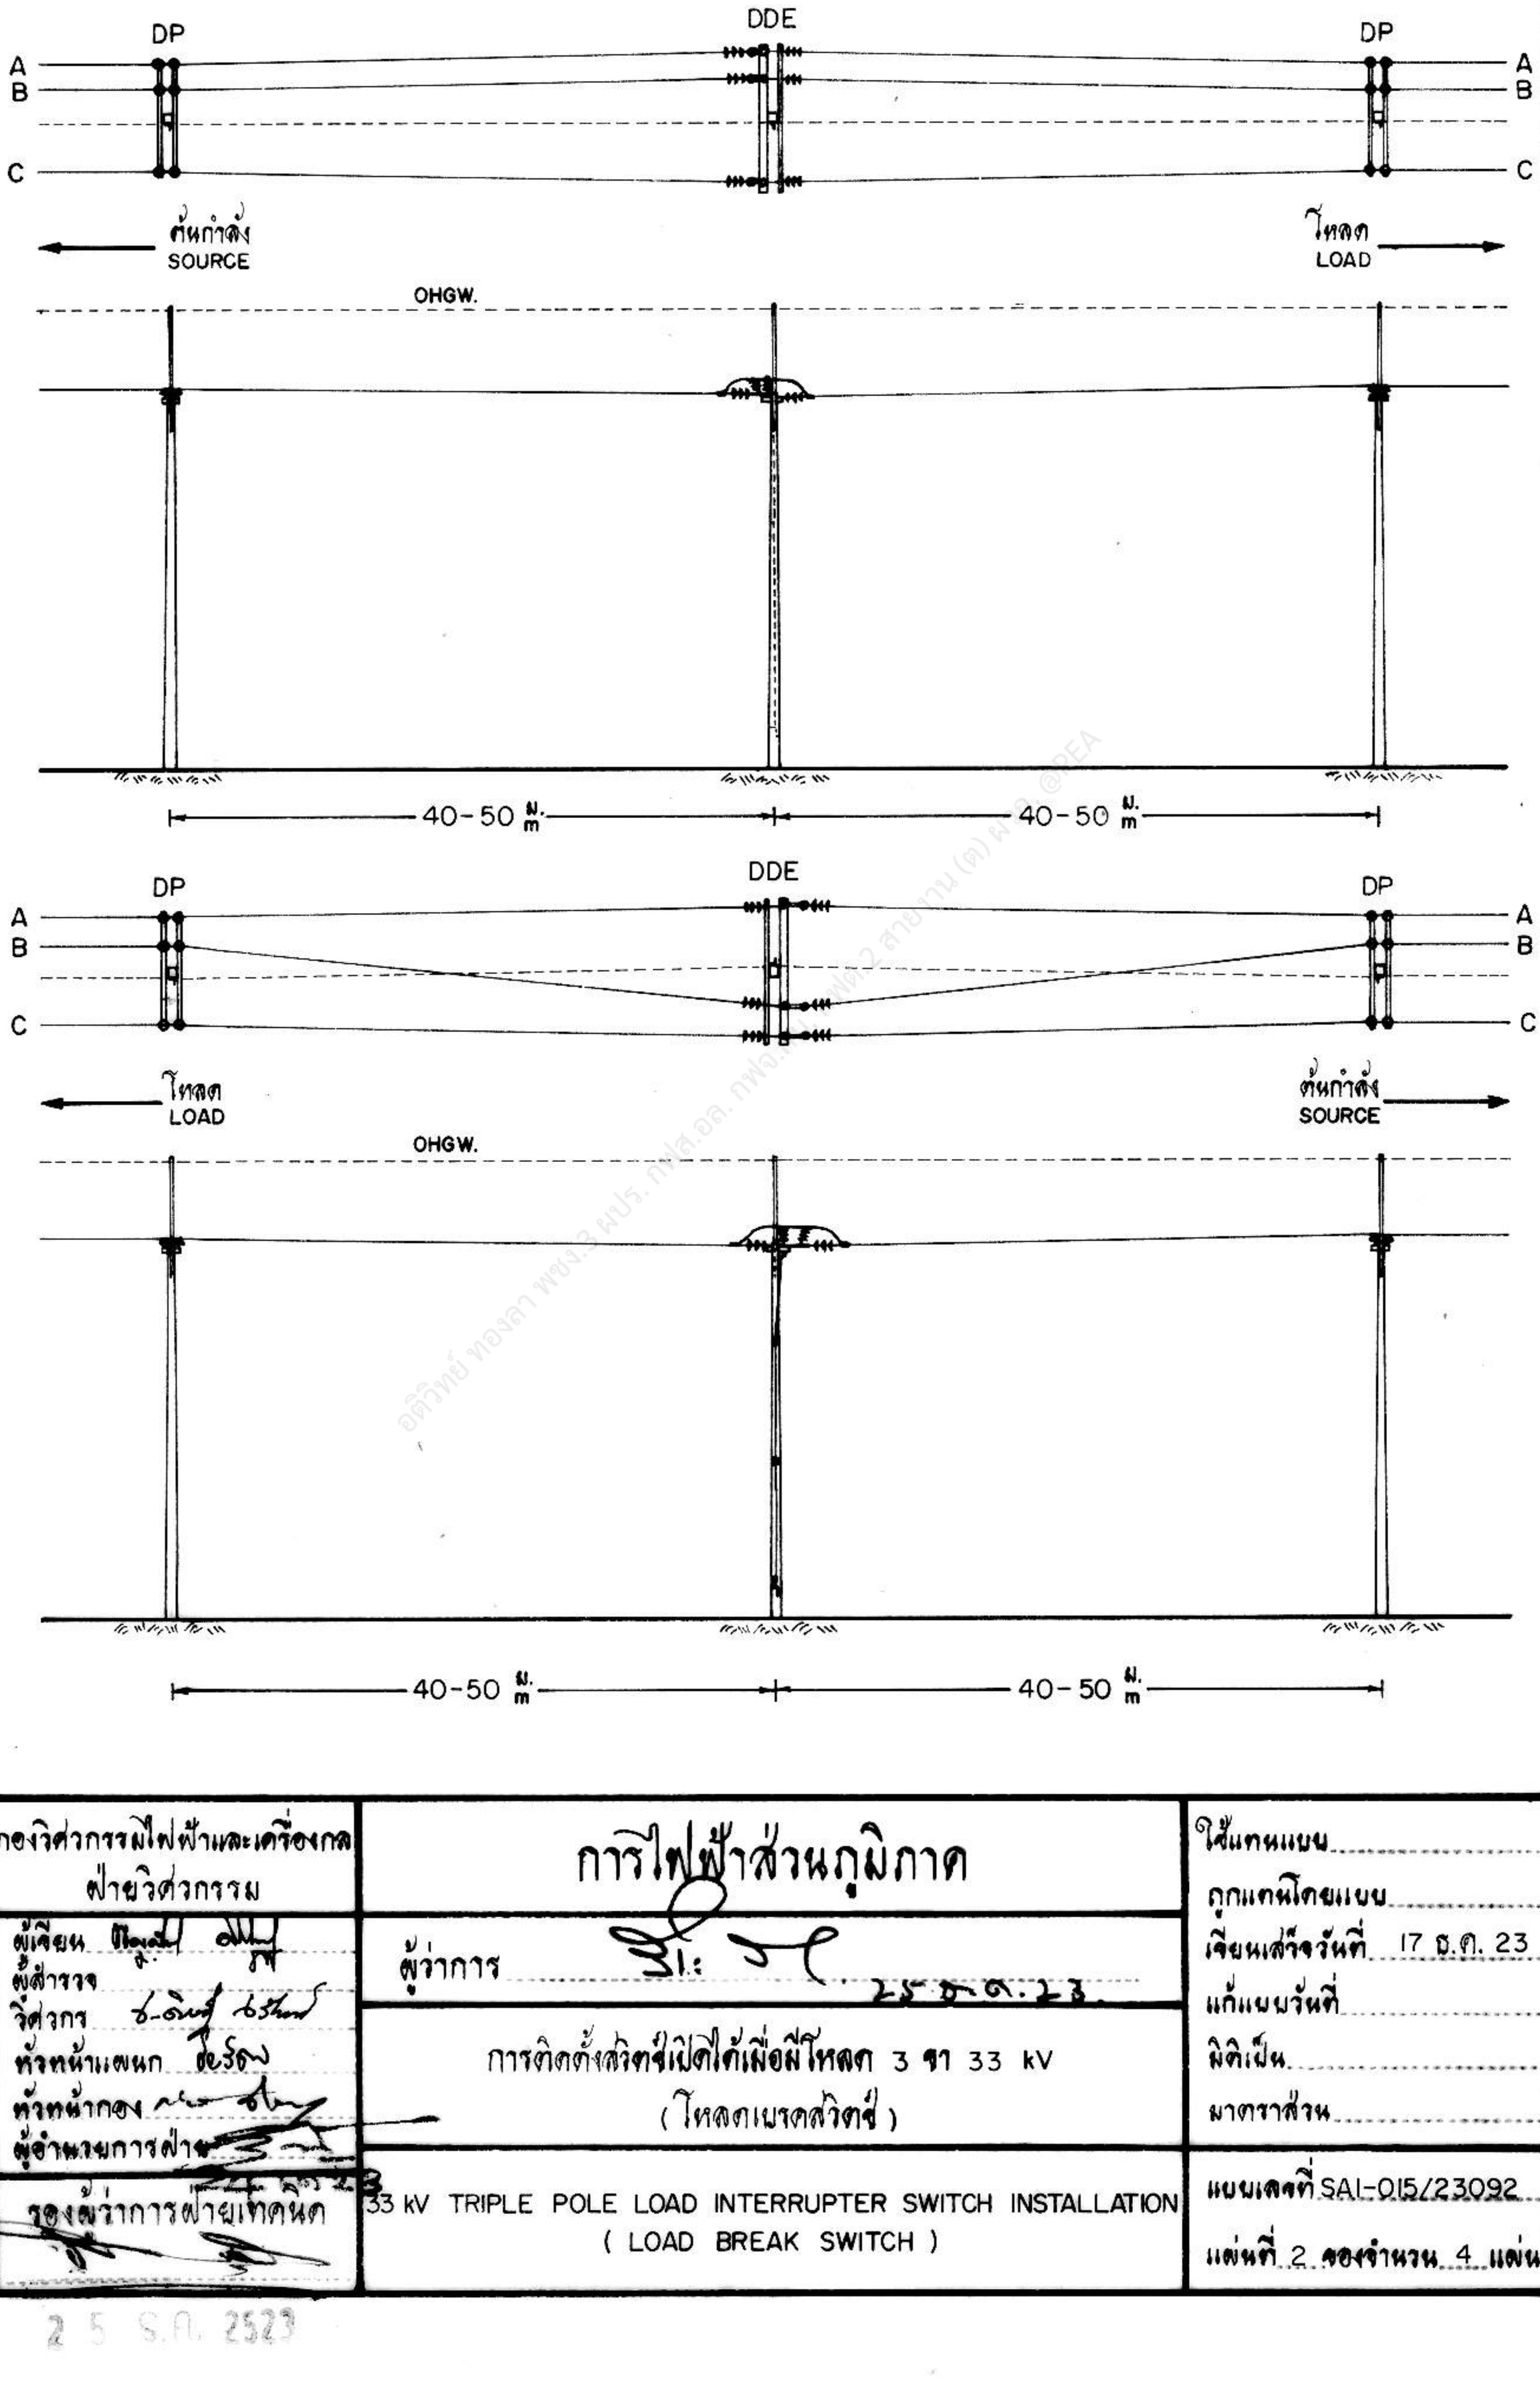

กองวิศวกรรมไฟฟ้าและเครื่องกล ฝ่ายวิศวกรรม	การไฟฟ้าส่วนภูมิภาค	ใช้แทนแบบ ..... ถูกแทนโดยแบบ ..... เขียนเสร็จวันที่ 17 ธ.ค. 23 แก้แบบวันที่ ..... มิติเป็น ..... มาตราส่วน .....
ผู้เขียน ..... ผู้สำรวจ ..... วิศวกร ..... หัวหน้าแผนก ..... หัวหน้ากอง ..... ผู้อำนวยการฝ่าย	ผู้ว่าการ ..... 25 ธ.ค. 23	
	การติดตั้งสวิทช์เปิดได้เมื่อมีโหลด 3 ขา 33 kV (โหลดเบรคสวิทช์)	
รองผู้ว่าการฝ่ายเทคนิค	33 kV TRIPLE POLE LOAD INTERRUPTER SWITCH INSTALLATION (LOAD BREAK SWITCH)	แบบเลขที่ SAI-015/23092 แผ่นที่ 2 ของจำนวน 4 แผ่น

25 S.A. 2523


การประกอบเลขที่ 3414
ASSEMBLY NO.

ข้อกำหนดการติดตั้ง

1. ตำแหน่งการติดตั้งสวิตช์เปิดได้เมื่อมีโหลด(โหลดเบรคสวิตช์) ในระบบจำหน่ายแรงสูง ดูแบบเลขที่ SAI-015/20026
2. ระยะห่างระหว่างเสาต้นที่ติดตั้งโหลดเบรคสวิตช์กับเสาต้นถัดไปไม่เกิน 50 ม. และที่เสาต้นถัดจากเสาต้นติดตั้งสวิตช์ให้ก่อสร้างโดยติดตั้งลูกถ้วยก้านตรงคู่รับสาย
3. กรณีที่ติดตั้งเป็นสวิตช์ตัดตอนโหลดในสายระบบจำหน่าย ให้พิจารณาติดตั้งโหลดเบรคสวิตช์โดยคำนึงให้ส่วนที่เป็นใบมีดของสวิตช์ติดตั้งอยู่ทางด้านโหลดเสมอ
4. กรณีที่ติดตั้งในวงจรบน หรือวงจรล่างของสายจำหน่าย ที่พาดมากกว่าหนึ่งวงจร ให้ดำเนินการตามข้อแนะนำ การติดตั้งสวิตช์สามขา เปิดพร้อมกันในระบบจำหน่ายแรงสูง ตามแบบเลขที่ SAI-015/22045
5. ชุดกระบอกสำหรับดับอาร์ค จะมีอายุการใช้งานตัดกระแสเต็มพิกัดที่ 600 แอมป์ ได้ไม่น้อยกว่า 25 ครั้ง

RECOMMENDATION

1. LOCATION OF LOAD BREAK SWITCH IN H.T. DISTRIBUTION SYSTEM, SEE DWG. NO. SAI-015/20026
2. SPAN LENGTH BETWEEN SWITCH POLE AND ADJACENT POLES SHALL NOT EXCEED 50 m. THE ADJACENT POLES SHALL BE CONSTRUCTED BY INSTALLING DOUBLE PIN INSULATOR (DP) STRUCTURE .
3. FOR POLE TOP MOUNTING AS LINE SWITCHING, THE SWITCH BLADE SHALL BE FIXED AT THE LOAD - SIDE OF LINE .
4. IN CASE OF INSTALLATION AT THE UPPER OR LOWER CIRCUIT IN DOUBLE CIRCUIT DISTRIBUTION LINE, CONSTRUCTED AS THE SUGGESTIONS OF TRIPLE POLE GROUP OPERATED SWITCH INSTALLATION IN DWG. NO. SAI-015/22045
5. THE OPERATING LIFE EXPECTANCY OF THE INTERRUPTING ELEMENT AT 600 A IS AT LEAST 25 OPERATIONS.

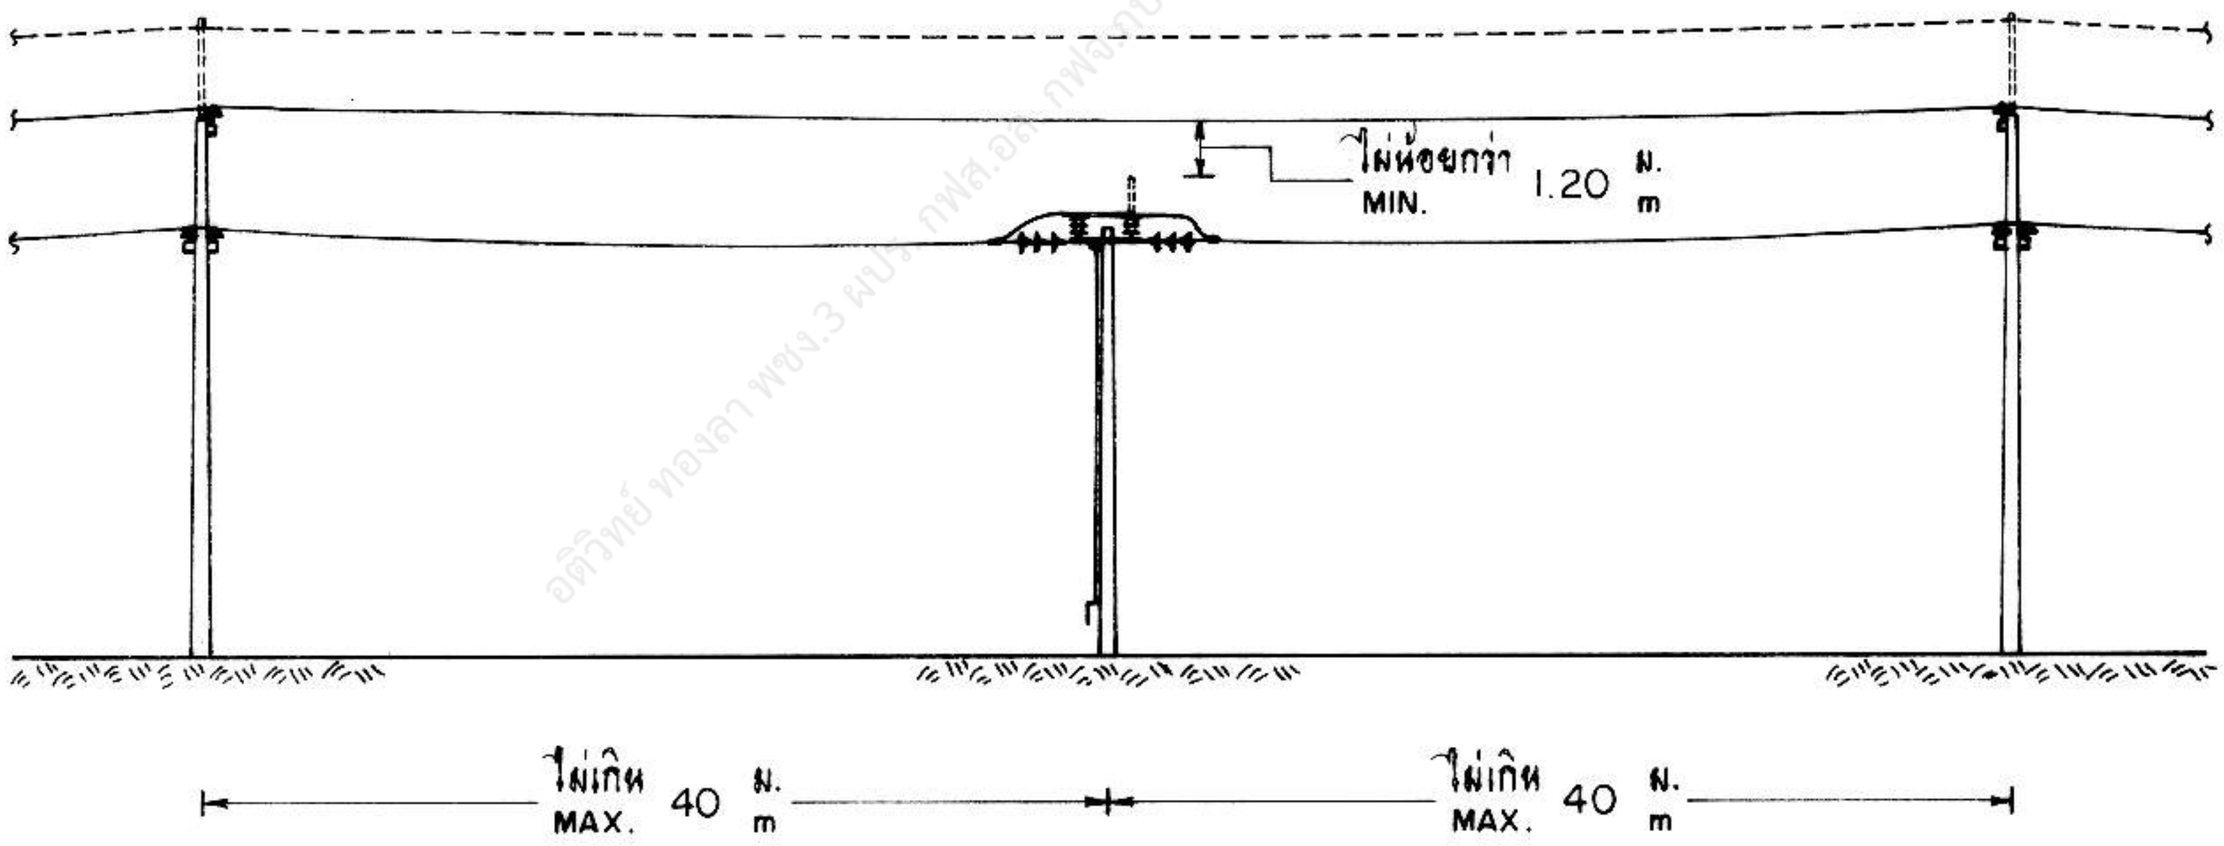

การติดตั้งสวิตช์สามขาที่วงจรล่าง
TRIPLE POLE SWITCH AT LOWER CIRCUIT

กองวิศวกรรมไฟฟ้าและเครื่องกล ฝ่ายวิศวกรรม	การไฟฟ้าส่วนภูมิภาค	ใช้แทนแบบ ถูกแทนโดยแบบ เขียนเสร็จวันที่ 17 ธ.ค. 23
ผู้เขียน ผู้สำรวจ วิศวกร หัวหน้าแผนก หัวหน้ากอง ผู้อำนวยการฝ่าย	ผู้ว่าการ การติดตั้งสวิตช์เปิดได้เมื่อมีโหลด 3 ขา 33 kV (โหลดเบรคสวิตช์)	แก้แบบวันที่ มิติเป็น มาตราส่วน
รองผู้ว่าการฝ่ายเทคนิค	33 kV TRIPLE POLE LOAD INTERRUPTER SWITCH INSTALLATION (LOAD BREAK SWITCH)	แบบเลขที่ SAI-015/23092 แผ่นที่ 3 ของจำนวน 4 แผ่น

25 S.H. 2525

การประกอบเลขที่ ASSEMBLY NO. 3414

บัญชีวัสดุ
BILL OF MATERIAL

ลำดับที่ ITEM	รายละเอียด DESCRIPTION	จำนวน REQ'D	วัสดุเลขที่ MAT. NO.
1	เสาคอนกรีต 12 ม. POLE, CONCRETE 12 m LONG	1	00010004
2	เหล็กฉากรับสายล่อฟ้า OVERHEAD GROUND WIRE BAYONET	1	01010006
3	กราวด์วายรีแคล้มป์แบบ J 1152 GROUND WIRE CLAMP J 1152	1	01230205
4	สวิตช์เปิดได้เมื่อมีโหลด สวิตช์ 3 ขา 33 kV, 600 แอมป์ พร้อมฐานสวิตช์ อุปกรณ์ประกอบสำหรับติดตั้ง และคันโยกสวิตช์ TRIPLE POLE LOAD INTERRUPTER SWITCH 33 kV, 600 A COMPLETE WITH MOUNTING ACCESSORIES AND OPERATING HANDLE ASSEMBLY	1 ชุด set	04070101
5	เหล็กฉากรับคอนสาย ขนาด 50X50X6 มม. ช่วงกว้าง 1,800 มม. ดรอพ 450 มม. BRACE, ANGLE STEEL 50X50X6 mm, 1,800 mm WIDE 450 mm DROP	1	01200007
6	สลักเกลียว M 16 X 130 มม. BOLT, MACHINE, M 16 X 130 mm	2	01110200
7	สลักเกลียว M 16 X 250 มม. BOLT, MACHINE, M 16 X 250 mm	8	01110203
8	แหวนสี่เหลี่ยมแบน 52X52X4.5 มม. รู Ø 18 มม. มอก. 258 WASHER, SQUARE, FLAT, 52X52X4.5 mm HOLE Ø 18 mm TIS 258	7	01180100
9	ลูกถ้วยแขวน มอก. 354 แบบ ง (แบบ 52-4) INSULATOR, SUSPENSION TYPE, TIS 354 TYPE D (CLASS 52-4)	18	03020002
10	สเตรนแคล้มป์ สำหรับสายอะลูมิเนียม อะลูมิเนียมอัลลอย และ อะลูมิเนียมแกนเหล็ก CLAMP, STRAIN, FOR Al, Al-ALLOY AND ACSR	6	03110000 03110101
11	ลวดเหล็กตีเกลียว 50/7 ต.มม. ดิน 48201 St II WIRE, STEEL STRANDED, 50/7 mm^2 DIN 48201 St II	11 ม. m	01100004
12	ยูแคล้มป์ สลัก 1 ตัว M 8 (ไวร์โรป คลิ๊ป) CLAMP, SINGLE U-BOLT M 8 (WIRE ROPE CLIP)	3	01230000
13	หลักดิน 60X60X5 มม. ยาว 2 ม. ROD, GROUND 60X60X5 mm, 2 m LONG	1	01220002

หมายเหตุ
1. รายละเอียดการประกอบสวิตช์เปิดได้เมื่อมีโหลด ดูจากคู่มือที่แนบมาพร้อมกับสวิตช์
2. สวิตช์เปิดได้เมื่อมีโหลดอาจเรียกชื่อเป็น โหลดเบรคสวิตช์, โหล่ดอินเตอร์รัพเตอร์สวิตช์ หรือโหลดเซ็กชั่นนาไลเซอร์ ก็ได้เช่นกัน
3. การติดตั้งนี้เป็นสวิตช์เปิดได้เมื่อมีโหลด ผลิตภัณฑ์ S & C (ALDUTI-RUPTER SWITCH)

NOTES
1. DETAIL OF ASSEMBLY, SEE THE INSTRUCTION MANUAL WHICH IS ENCLOSED WITH THE SWITCH.
2. THE OTHER NAMES OF 'LOAD BREAK SWITCH ARE LOAD INTERRUPTER SWITCH OR LOAD SECTIONALIZER.
3. THIS LOAD BREAK SWITCH INSTALLATION IS S & C (ALDUTI-RUPTER SWITCH).

กองวิศวกรรมไฟฟ้าและเครื่องกล ฝ่ายวิศวกรรม	การไฟฟ้าส่วนภูมิภาค	ใช้แทนแบบ ถูกแทนโดยแบบ เขียนเสร็จวันที่ 17 ธ.ค. 23 แก้แบบวันที่ มิติเป็น มาตราส่วน
ผู้เขียน ผู้สำรวจ วิศวกร หัวหน้าแผนก หัวหน้ากอง ผู้อำนวยการฝ่าย	ผู้ว่าการ การติดตั้งสวิตช์เปิดได้เมื่อมีโหลด 3 ขา 33 kV (โหลดเบรคสวิตช์)	
รองผู้ว่าการฝ่ายเทคนิค	33 kV TRIPLE POLE LOAD INTERRUPTER SWITCH INSTALLATION (LOAD BREAK SWITCH)	แบบเลขที่ SAI-015/23092 แผ่นที่ 4 ของจำนวน 4 แผ่น

25 S.A. 2523