การประกอบเลขที่
ASSEMBLY NO. 0548

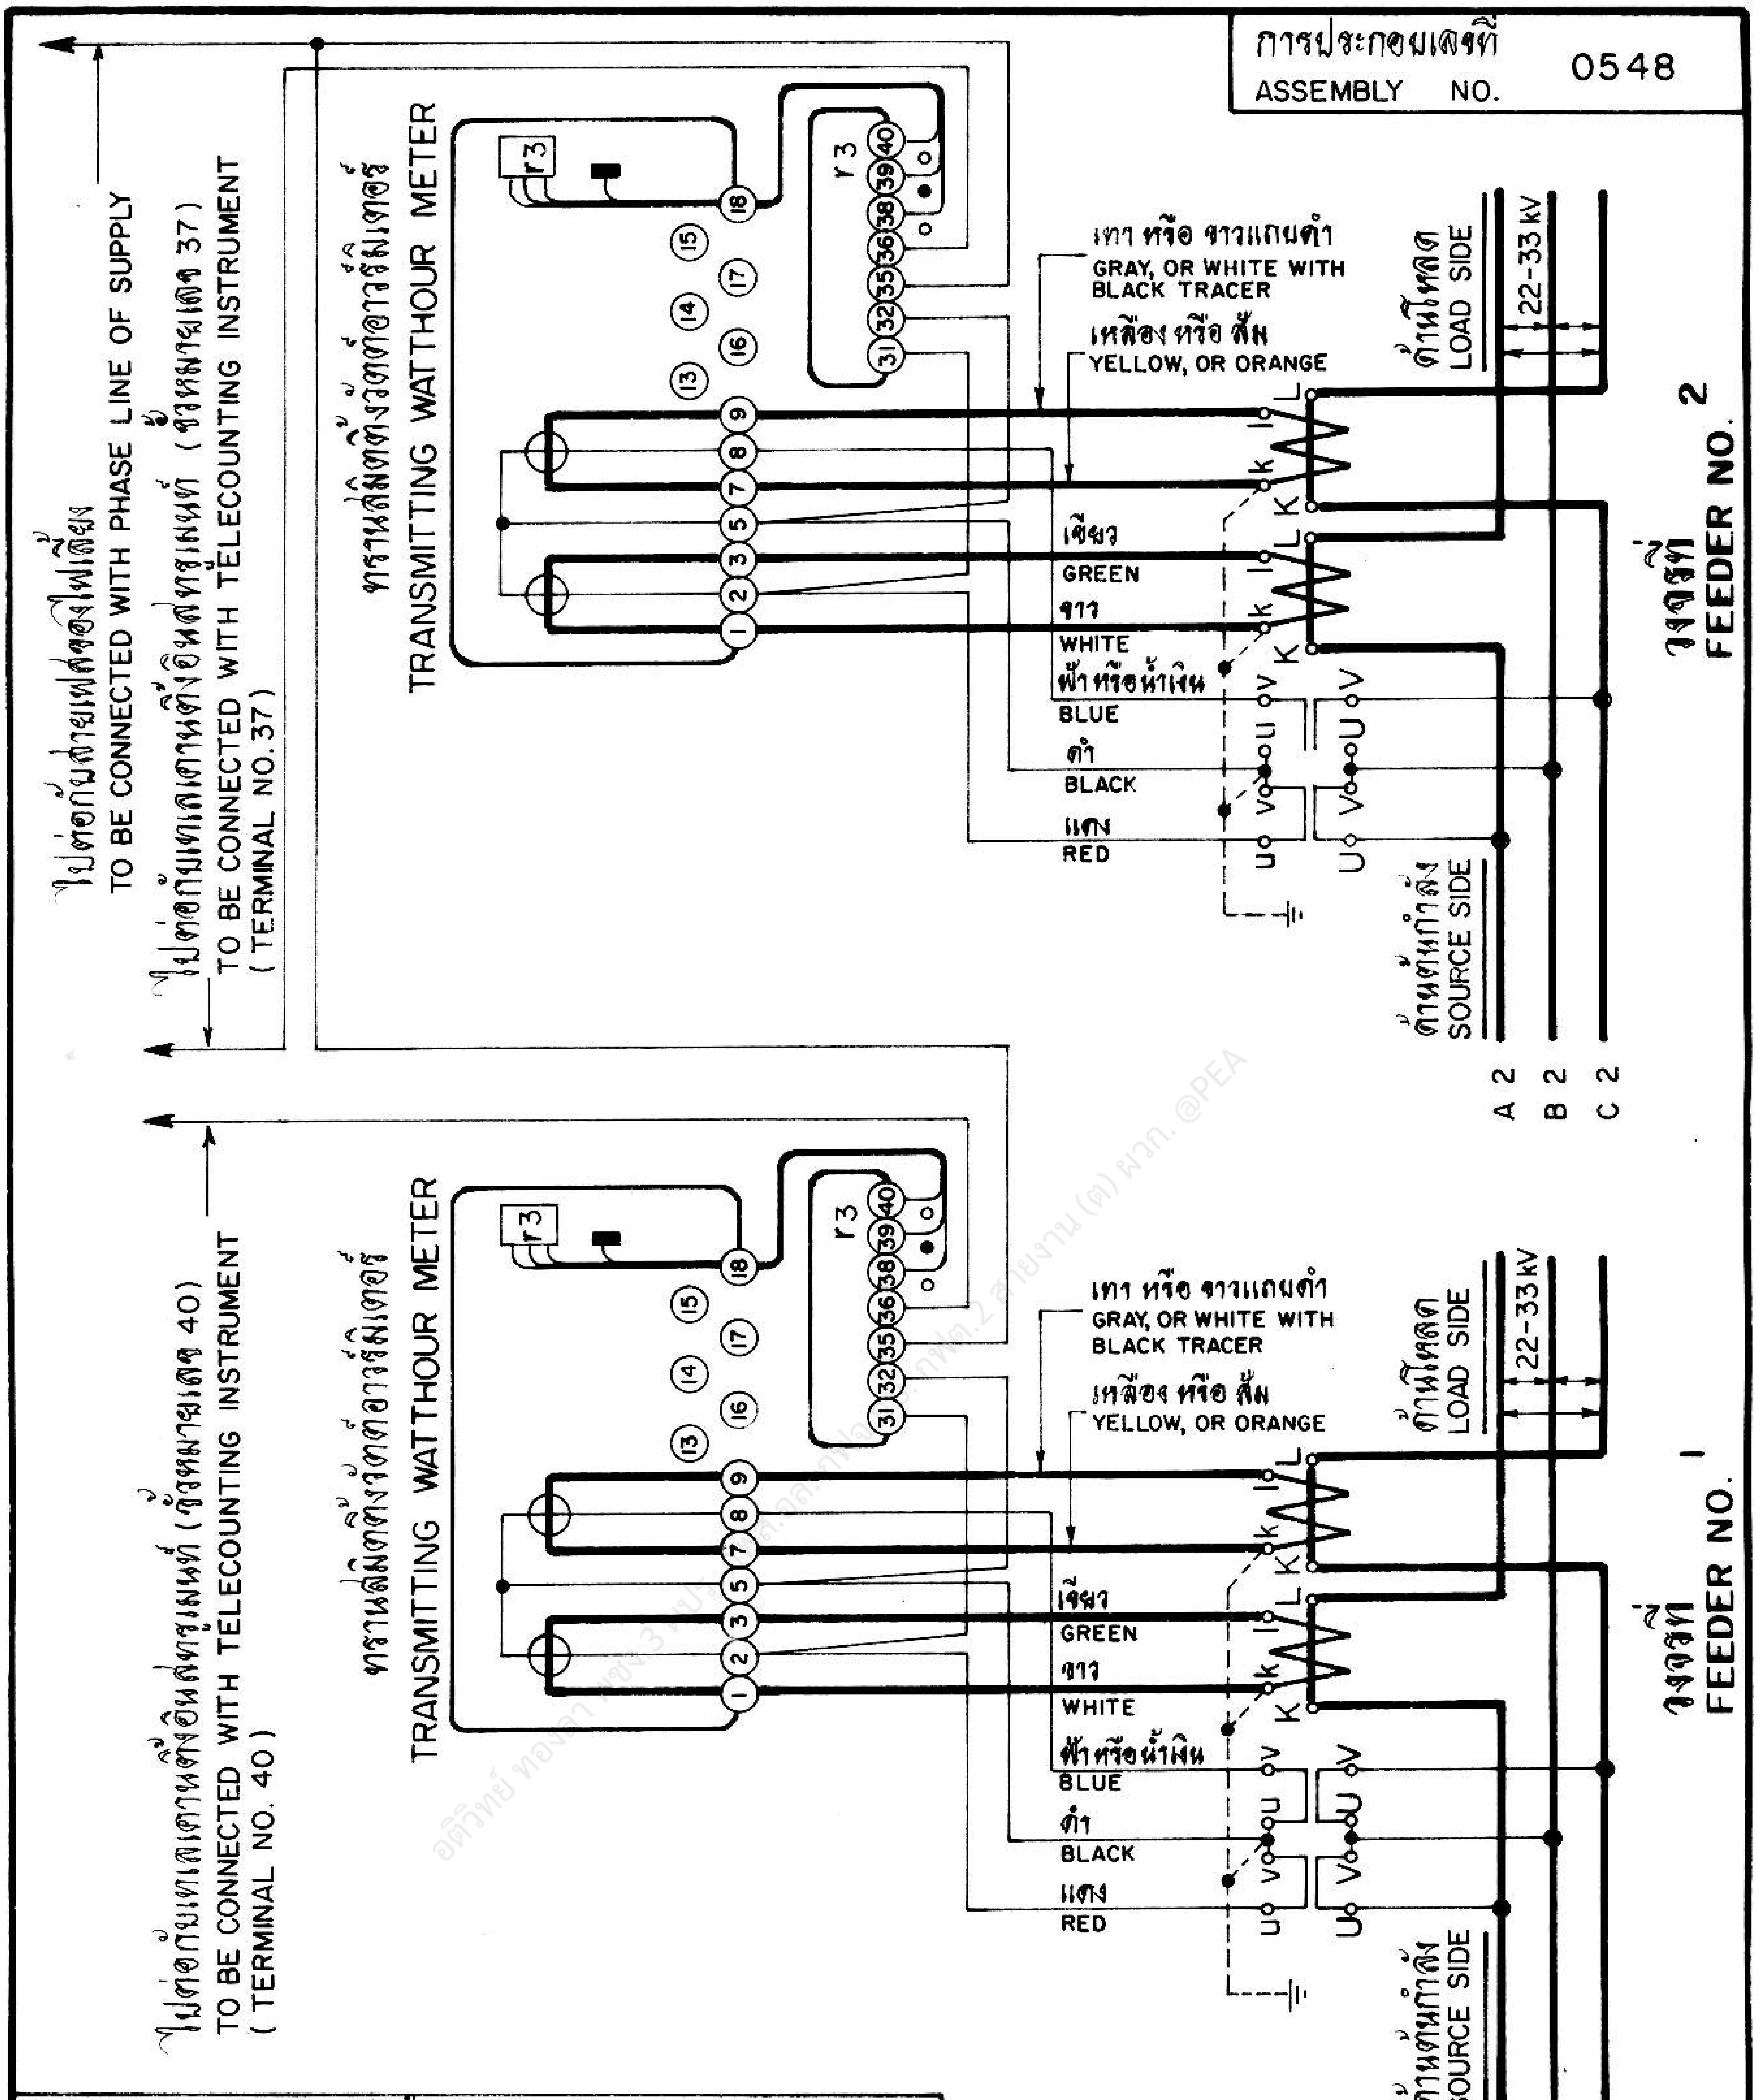
ไปต่อกับสายเฟสของไฟเลี้ยง
TO BE CONNECTED WITH PHASE LINE OF SUPPLY
ไปต่อกับเทเลเคาน์ติ้งอินสตรูเมนท์ (ขั้วหมายเลข 37)
TO BE CONNECTED WITH TELECOUNTING INSTRUMENT (TERMINAL NO.37)
ไปต่อกับเทเลเคาน์ติ้งอินสตรูเมนท์ (ขั้วหมายเลข 40)
TO BE CONNECTED WITH TELECOUNTING INSTRUMENT (TERMINAL NO. 40)
ทรานสมิตติ้งวัตต์อาวร์มิเตอร์
TRANSMITTING WATTHOUR METER
r3
1 2 3 5 7 8 9 13 14 15 16 17 18 31 32 35 36 38 39 40
เทา หรือ ขาวแถบดำ
GRAY, OR WHITE WITH BLACK TRACER
เหลือง หรือ ส้ม
YELLOW, OR ORANGE
เขียว
GREEN
ขาว
WHITE
ฟ้าหรือน้ำเงิน
BLUE
ดำ
BLACK
แดง
RED
L l k K
u v U V
ด้านโหลด
LOAD SIDE
ด้านต้นกำลัง
SOURCE SIDE
22-33 kV
วงจรที่
FEEDER NO. 2
FEEDER NO. 1
A 2 B 2 C 2
A 1 B 1 C 1

การต่อสายตามแผนผังนี้ ใช้สำหรับรีโมทมิเตอริงอีควิปเมนท์ ผลิตภัณฑ์ LANDIS & GYR LTD. เท่านั้น

กองวิศวกรรมไฟฟ้าและเครื่องกล
ฝ่ายวิศวกรรม

ผู้เขียน
ผู้สำรวจ
วิศวกร
หัวหน้าแผนก
ผู้อำนวยการกอง
ผู้อำนวยการฝ่าย

รองผู้ว่าการฝ่ายเทคนิค
4 ส.ค. 2537

การไฟฟ้าส่วนภูมิภาค

ผู้ว่าการ -5 ส.ค. 2537

แผนผังแสดงการต่อรีโมทมิเตอริงอีควิปเมนท์
สำหรับระบบจำหน่ายแรงสูง 22 - 33 kV 2 วงจร

REMOTE METERING EQUIPMENT CONNECTION DIAGRAM
FOR 2 FEEDERS, 22 - 33 kV DISTRIBUTION LINE

ใช้แทนแบบ
ถูกแทนโดยแบบ
เขียนเสร็จวันที่ 20 ก.ค. 37
แก้แบบวันที่
มิติเป็น
มาตราส่วน
แบบเลขที่ SA4-015/37020
แผ่นที่ 1 ของจำนวน 3 แผ่น

การประกอบเลขที่
ASSEMBLY NO. 0548

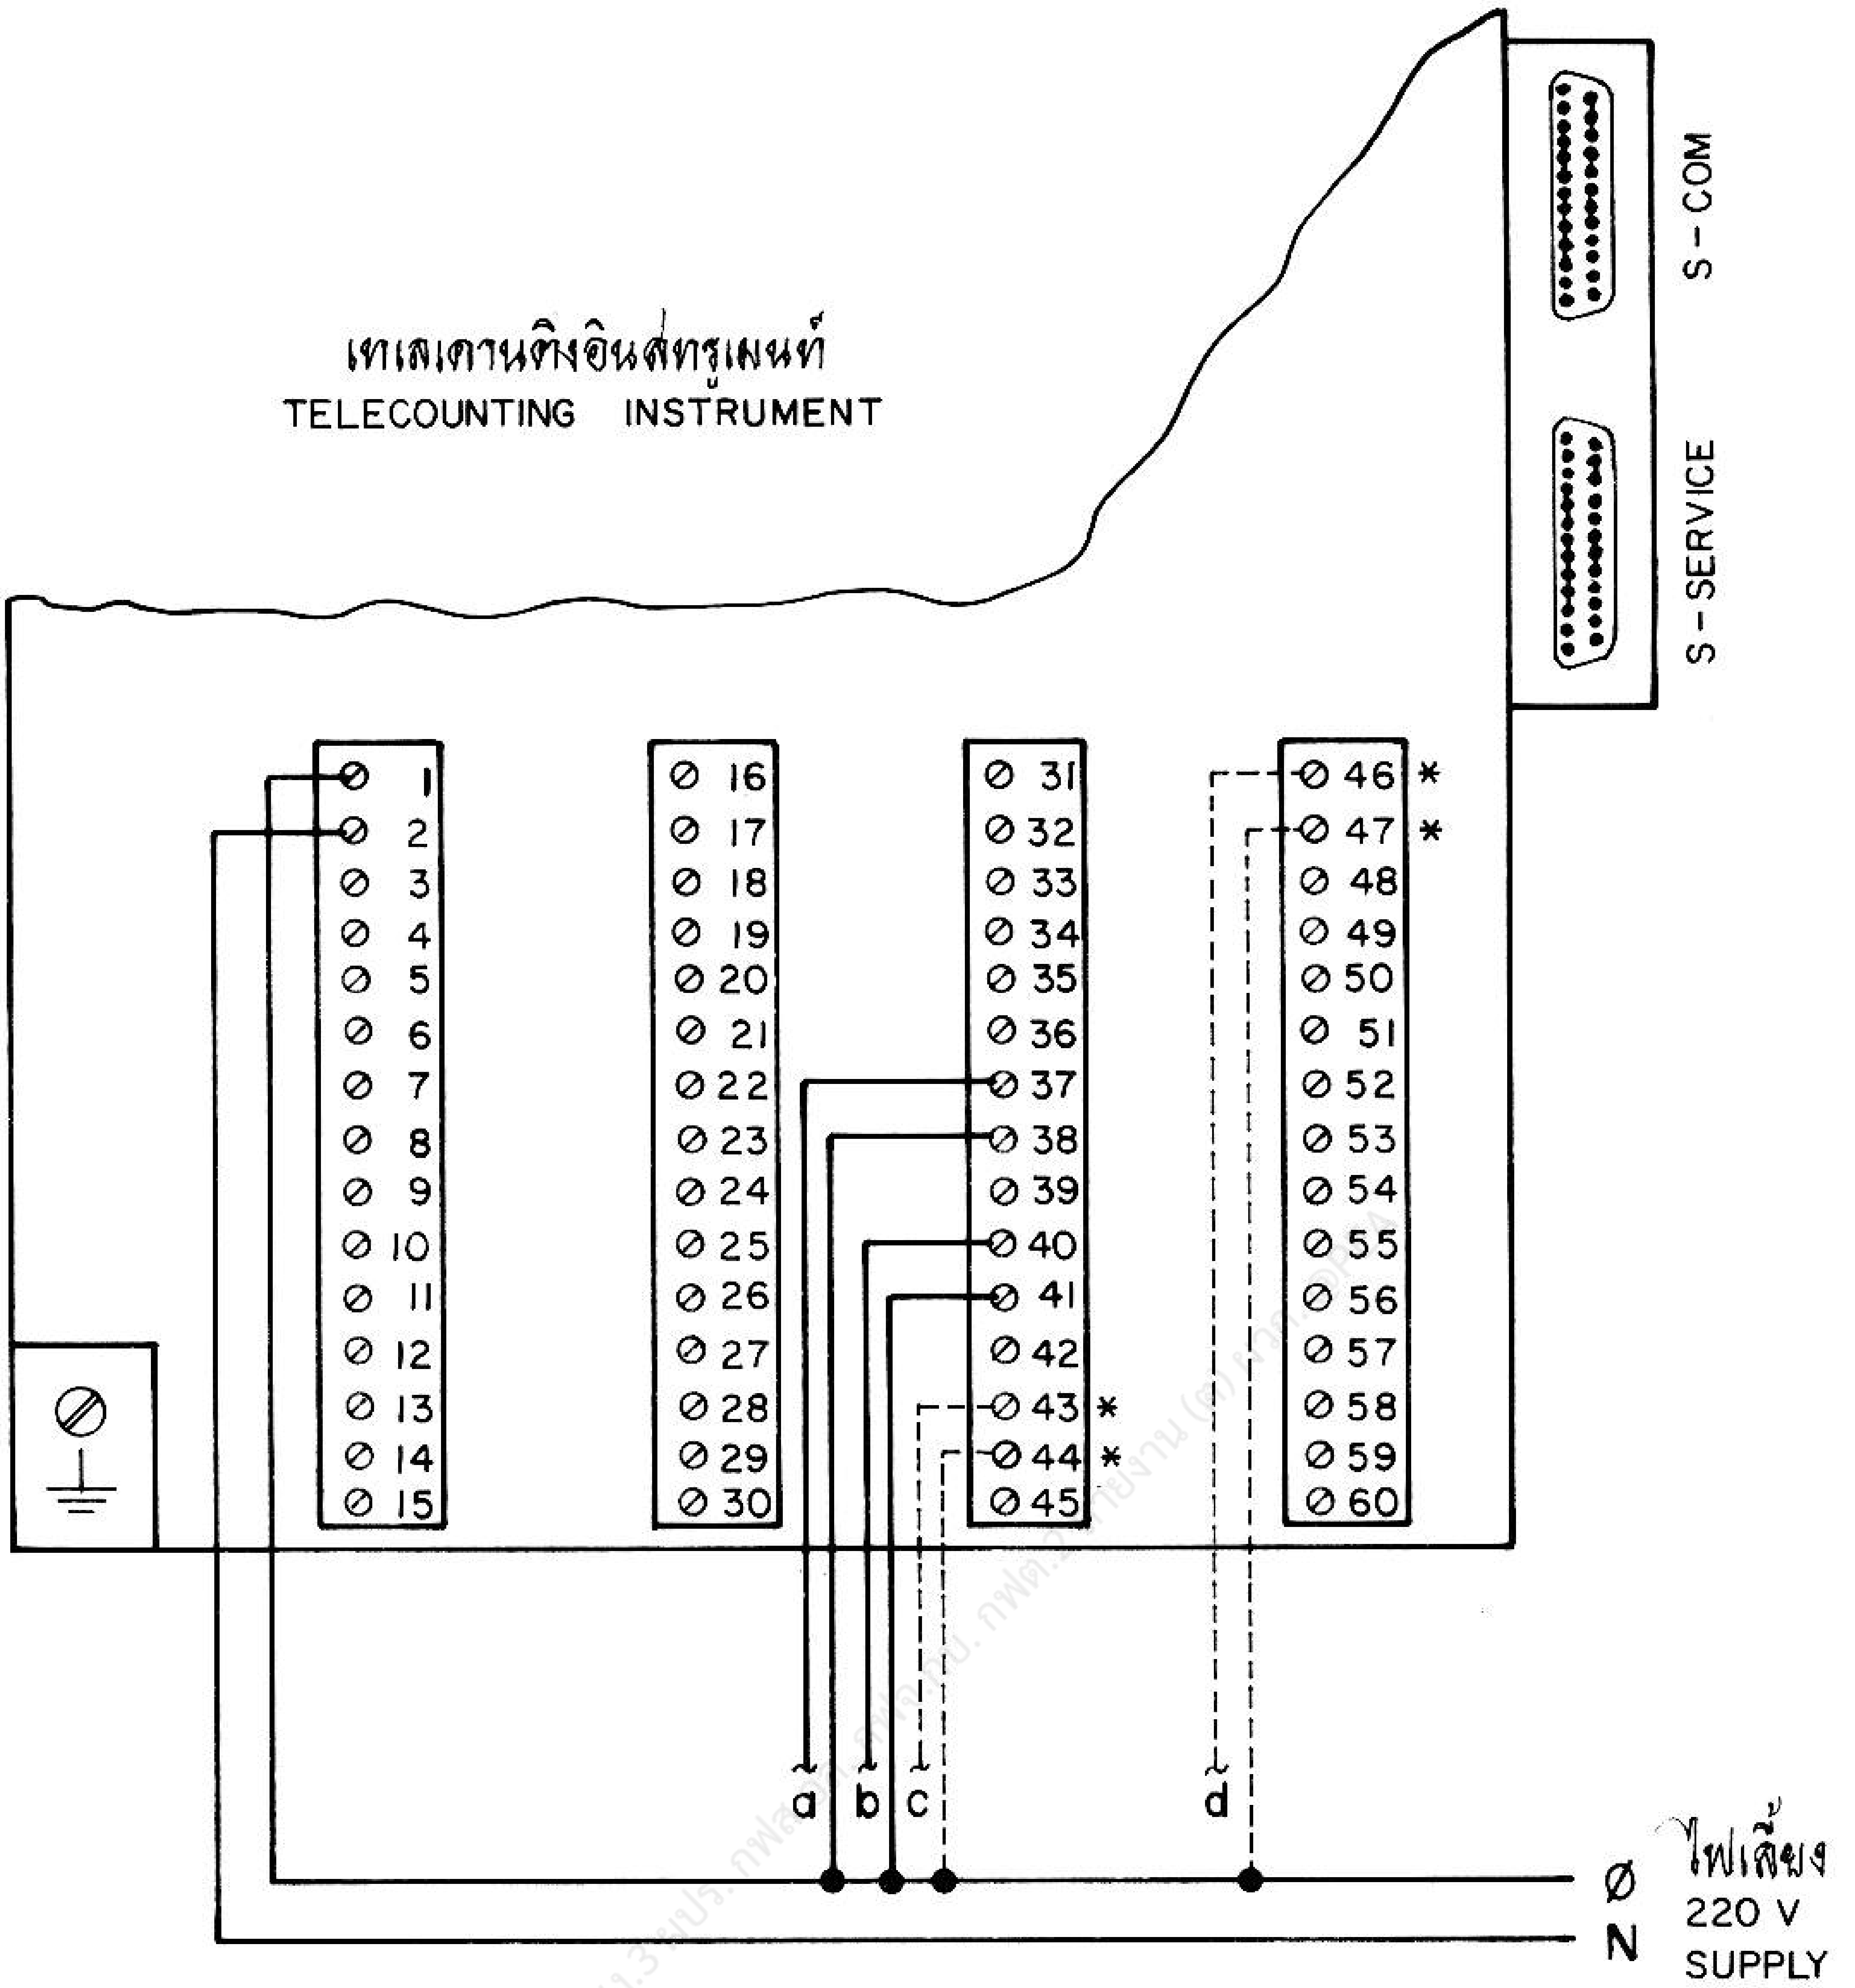
เทเลเคาน์ติงอินสทรูเมนท์
TELECOUNTING INSTRUMENT
S-COM
S-SERVICE
1
2
3
4
5
6
7
8
9
10
11
12
13
14
15
16
17
18
19
20
21
22
23
24
25
26
27
28
29
30
31
32
33
34
35
36
37
38
39
40
41
42
43 *
44 *
45
46 *
47 *
48
49
50
51
52
53
54
55
56
57
58
59
60
a
b
c
d
Ø
N
ไฟเลี้ยง
220 V
SUPPLY

หมายเหตุ

* สำหรับสายต่อกับทรานสมิตติ้งวัตต์อาวร์มิเตอร์ วงจรที่ 3 และ วงจรที่ 4 ตามลำดับ

NOTE

* FOR CONNECTION WITH TRANSMITTING WATTHOUR METER, FEEDER NO. 3 AND FEEDER NO. 4 RESPECTIVELY .

การต่อสายตามแผนผังนี้ ใช้สำหรับรีโมทมิเตอริงอีควิปเมนท์
ผลิตภัณฑ์ LANDIS & GYR LTD. เท่านั้น

กองวิศวกรรมไฟฟ้าและเครื่องกล ฝ่ายวิศวกรรม	**การไฟฟ้าส่วนภูมิภาค**	ใช้แทนแบบ.......... ถูกแทนโดยแบบ..........
ผู้เขียน.......... ผู้สำรวจ.......... วิศวกร.......... หัวหน้าแผนก.......... ผู้อำนวยการกอง.......... ผู้อำนวยการฝ่าย..........	ผู้ว่าการ.......... 5 ส.ค. 2537 ผวภ. แผนผังแสดงการต่อรีโมทมิเตอริงอีควิปเมนท์ สำหรับระบบจำหน่ายแรงสูง 22 - 33 kV 2 วงจร	เขียนเสร็จวันที่ 20 ก.ค.37 แก้แบบวันที่.......... ผิดเป็น.......... มาตราส่วน..........
รองผู้ว่าการฝ่ายเทคนิค	REMOTE METERING EQUIPMENT CONNECTION DIAGRAM FOR 2 FEEDERS, 22 - 33 kV DISTRIBUTION LINE	แบบเลขที่ SA4-015/37020 แผ่นที่ 2 ของจำนวน 3 แผ่น

4 ส.ค. 2537

การประกอบเลขที่
ASSEMBLY NO. 0548

หมายเหตุ

1 การต่อสายตามแผนผังนี้ ใช้สำหรับรีโมทมิเตอริงอีควิปเมนท์ ผลิตภัณฑ์ของ LANDIS & GYR LTD. เท่านั้น

2 ใช้สายคอนโทรลเคเบิล ขนาด 7 X 2.5 ต.มม. (วัสดุเลขที่ 4278) สำหรับต่อระหว่าง พีที. ซีที. กับทรานสมิตติ้งวัตต์อาวร์มิเตอร์

3 ใช้สายคอนโทรลเคเบิล ขนาด 4 X 4 ต.มม.(วัสดุเลขที่ 4279) สำหรับต่อระหว่างทรานสมิตติ้งวัตต์อาวร์มิเตอร์ กับเทเลเคานติ้งอินสทรูเมนท์

4 ใช้สายทองแดงหุ้มฉนวน PVC 750 โวลต์ 70 °C ขนาด 2.5 ต.มม. สำหรับต่อสายระหว่างเทเลเคานติ้งอินสทรูเมนท์ กับไฟเลี้ยง

NOTES

1 THIS CONNECTION DIAGRAM IS ONLY FOR REMOTE METERING EQUIPMENT MANUFACTURED BY LANDIS & GYR LTD. .

2 USE CONTROL CABLE SIZE 7 X 2.5 mm^2 (MAT. NO. 4278) FOR CONNECTION BETWEEN PT., CT. AND TRANSMITTING WATTHOUR METER.

3 USE CONTROL CABLE SIZE 4 X 4 mm^2 (MAT. NO. 4279) FOR CONNECTION BETWEEN TRANSMITTING WATTHOUR METER AND TELECOUNTING INSTRUMENT.

4 USE 2.5 mm, 750 V, 75 °C, PVC INSULATED Cu CABLE FOR CONNECTION BETWEEN TELECOUNTING INSTRUMENT AND SUPPLY.

	แบบอ้างอิง REFERENCE DRAWING	แบบเลขที่ DWG. NO.	การประกอบเลขที่ ASSEMBLY NO.
1	การต่อลงดินระบบแรงสูง และแรงต่ำ แผ่นที่ 15 และ 17 H.T. AND L.T. EARTHING SYSTEM, SHEET NO. 15 AND NO. 17	S02-015/23039	9701

อดิวิทย์ ทองลา พชง.3 ผปร. กฟส.อล. กฟจ.กบ. [illegible] 2 สายงาน (ต) [illegible] @PEA

กองวิศวกรรมไฟฟ้าและเครื่องกล
ฝ่ายวิศวกรรม

ผู้เขียน
ผู้สำรวจ
วิศวกร
หัวหน้าแผนก
ผู้อำนวยการกอง
ผู้อำนวยการฝ่าย

รองผู้ว่าการฝ่ายเทคนิค
4 ส.ค. 2537

การไฟฟ้าส่วนภูมิภาค

ผู้ว่าการ -5.ส.ค.2537

แผนผังแสดงการต่อรีโมทมิเตอริงอีควิปเมนท์
สำหรับระบบจำหน่ายแรงสูง 22 - 33 kV 2 วงจร

REMOTE METERING EQUIPMENT CONNECTION DIAGRAM
FOR 2 FEEDERS, 22 - 33 kV DISTRIBUTION LINE

ใช้แทนแบบ
ถูกแทนโดยแบบ
เขียนเสร็จวันที่ 20 ก.ค.37
แก้แบบครั้งที่
มิติเป็น
มาตราส่วน
แบบเลขที่ SA4-015/37020
แผ่นที่ 3 ของจำนวน 3 แผ่น