การประกอบเลขที่ **5401**
ASSEMBLY NO.

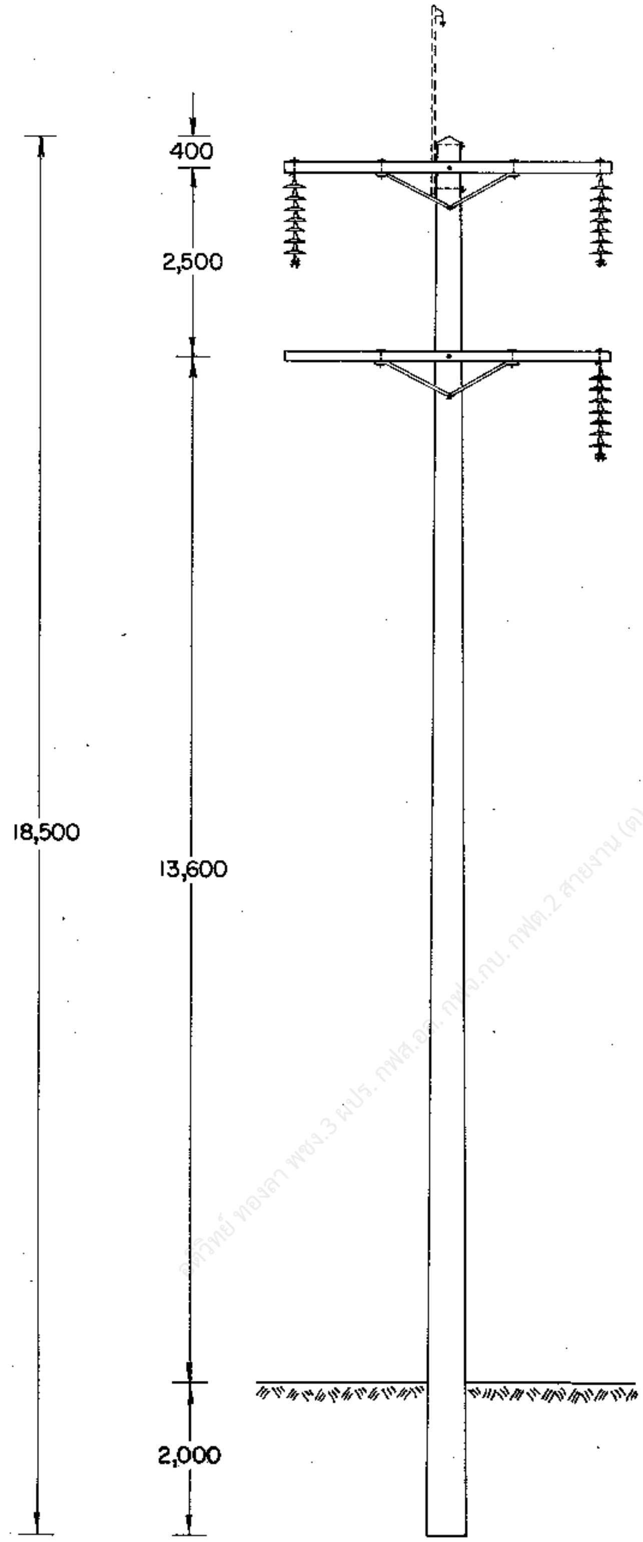

อดิวิทย์ ทองลา พชง.3 ผปร. กฟส.อค. กฟจ.กบ. กฟต.2 สายงาน (ต) ผวก. @PEA

กองวิศวกรรมไฟฟ้าและเครื่องกล
ฝ่ายวิศวกรรม

ผู้เขียน ....
ผู้ตรวจ ....
วิศวกร ....
หัวหน้าแผนก ชัยรัตน์
หัวหน้ากอง ....
ผู้อำนวยการฝ่าย ....
รองผู้ว่าการฝ่ายเทคนิค ....

การไฟฟ้าส่วนภูมิภาค

ผู้ว่าการ .... 24 มี.ค. 23

115 kV วงจรเดี่ยว สายไฟฟ้าเดี่ยว
เสาสำหรับทางตรง ใช้เสาขนาด 18.50 ม.
แบบ SS - TG - 2

115 kV SINGLE CIRCUIT SINGLE CONDUCTOR
TANGENT STRUCTURE 18.50 m POLE
TYPE SS — TG — 2

ใช้แทนแบบ ....
ถูกแทนโดยแบบ ....
เขียนเสร็จวันที่ 4 ม.ค. 23
แก้แบบวันที่ ....
มิติเป็น มม.
มาตราส่วน 1 : 100

แบบเลขที่ SAI-015/23019
แผ่นที่ 1 ของจำนวน 3 แผ่น

19 ธ.ค. 2525

การประกอบเลขที่
ASSEMBLY NO. **5401**

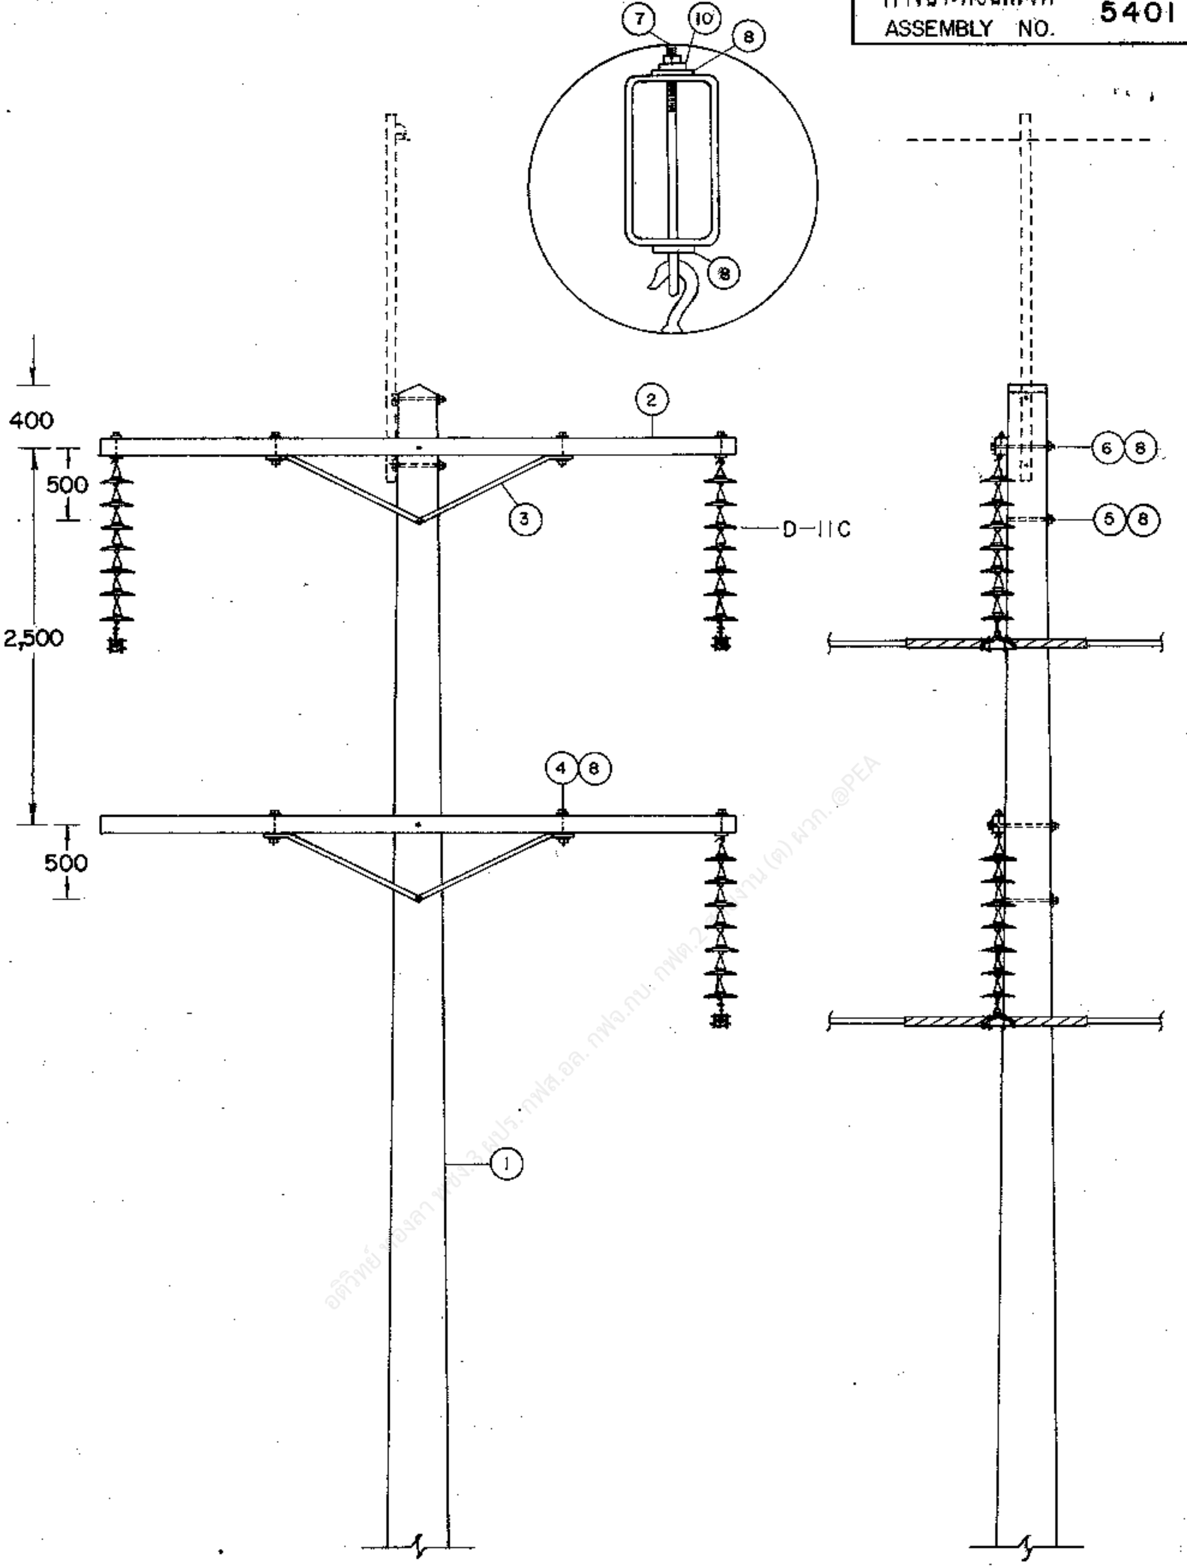

กองวิศวกรรมไฟฟ้าและเครื่องกล
ฝ่ายวิศวกรรม

ผู้เขียน
ผู้ตรวจ
วิศวกร
หัวหน้าแผนก ชัยรัตน์
หัวหน้ากอง
ผู้อำนวยการฝ่าย
รองผู้ว่าการฝ่ายเทคนิค

การไฟฟ้าส่วนภูมิภาค

ผู้ว่าการ .... 24 มิ.ค. 23

115 kV วงจรเดี่ยว สายไฟฟ้าเดี่ยว
เสาสำหรับทางตรง ใช้เสาขนาด 18.50 ม.
แบบ SS-TG-2

115 kV SINGLE CIRCUIT SINGLE CONDUCTOR
TANGENT STRUCTURE 18.50 m POLE
TYPE SS-TG-2

ใช้แทนแบบ..........
ถูกแทนโดยแบบ..........
เขียนเสร็จวันที่ 4 ม.ค. 23
แก้แบบวันที่..........
มิติเป็น มม.
มาตราส่วน 1 : 50
แบบเลขที่ SAI-015/23019
แผ่นที่ 2 ของจำนวน 3 แผ่น

1 มิ.ย. 2523

การประกอบเลขที่
ASSEMBLY NO. **5401**

บัญชีวัสดุ
BILL OF MATERIAL

ลำดับที่ ITEM	รายละเอียด DESCRIPTION	จำนวน REQ'D	วัสดุเลขที่ MAT. NO.
1	เสาคอนกรีต 18.5 ม. POLE, CONCRETE 18.5 m. LONG	1	00010009 (0039)
2	คอนสายแบบเหล็ก ขนาด 100 X 50 X 3.2 มม. ยาว 4.20 ม. CROSSARM, STEEL 100 X 50 X 3.2 mm , 4.20 m LONG	2	00120001 (0116)
3	เหล็กฉากรับคอนสาย ขนาด 50 X 50 X 6 มม. ช่วงกว้าง 1,800 มม. ดรอพ 450 มม. BRACE, ANGLE STEEL 50 X 50 X 6 mm , 1,800 mm WIDE 450 mm DROP	2	01200007 (0119)
4	สลักเกลียว M 16 X 130 มม. BOLT, MACHINE, M 16 X 130 mm	4	01110200 (0220) *
5	สลักเกลียว M 16 X 350 มม. BOLT, MACHINE, M 16 X 350 mm	2	01110205 (0225)
6	สลักเกลียว M 20 X 400 มม. BOLT, MACHINE, M 20 X 400 mm	2	01110301 (0233)
7	สลักห่วง โอแวล M 16 X 150 มม. BOLT, OVAL EYE M 16 X 150 mm	3	01150000 (0257)
8	แหวนสี่เหลี่ยมแบน 52X52X4.5 มม. รู Ø 18 มม. มอก. 258 WASHER, SQUARE, FLAT 52X52X4.5 mm HOLE Ø 18 mm TIS 258	12	01180100 (0355)
9	แหวนสี่เหลี่ยมแบน 62X62X6 มม. รู Ø 22 มม. มอก. 258 WASHER, SQUARE, FLAT 62X62X6 mm HOLE Ø 22 mm TIS 258	4	01180101 (0356)
10	แหวนสปริง M 16 มอก. 259 WASHER, LOCK, M 16, TIS 259	3	01180301 (0365)

รายละเอียด
DETAIL

D-11C	การประกอบลูกถ้วยแขวน SUSPENSION INSULATOR ASSEMBLY	3	
D-10A	ฐานรากเสา POLE FOUNDATION	1	

กองวิศวกรรมไฟฟ้าและเครื่องกล ฝ่ายวิศวกรรม	การไฟฟ้าส่วนภูมิภาค	ใช้แทนแบบ..........
ผู้เขียน.......... ผู้ตรวจ.......... วิศวกร.......... หัวหน้าแผนก.......... หัวหน้ากอง.......... ผู้อำนวยการฝ่าย..........	ผู้ว่าการ.......... 24 มี.ค. 23	ถูกแทนโดยแบบ.......... เขียนเสร็จวันที่ 4 ม.ค. 23 แก้แบบวันที่.......... มิติเป็น.......... มาตราส่วน..........
	115 kV วงจรเดี่ยว สายไฟฟ้าเดี่ยว เสาสำหรับทางตรง ใช้เสาขนาด 18.50 ม. แบบ SS-TG-2	
รองผู้ว่าการฝ่ายเทคนิค	115 kV SINGLE CIRCUIT SINGLE CONDUCTOR TANGENT STRUCTURE 18.50 m POLE TYPE SS-TG-2	แบบเลขที่ SAI-015/23019 แผ่นที่ 3 ของจำนวน 3 แผ่น

มี.ค. 2523

อติวิทย์ ทองลา พชง.3 ผปร. กฟส.อล. กฟจ.กบ. กฟฉ.2 สายงาน (ด) ผวก. @PEA