
กาประกอบเลขที่ ASSEMBLY NO. 3210

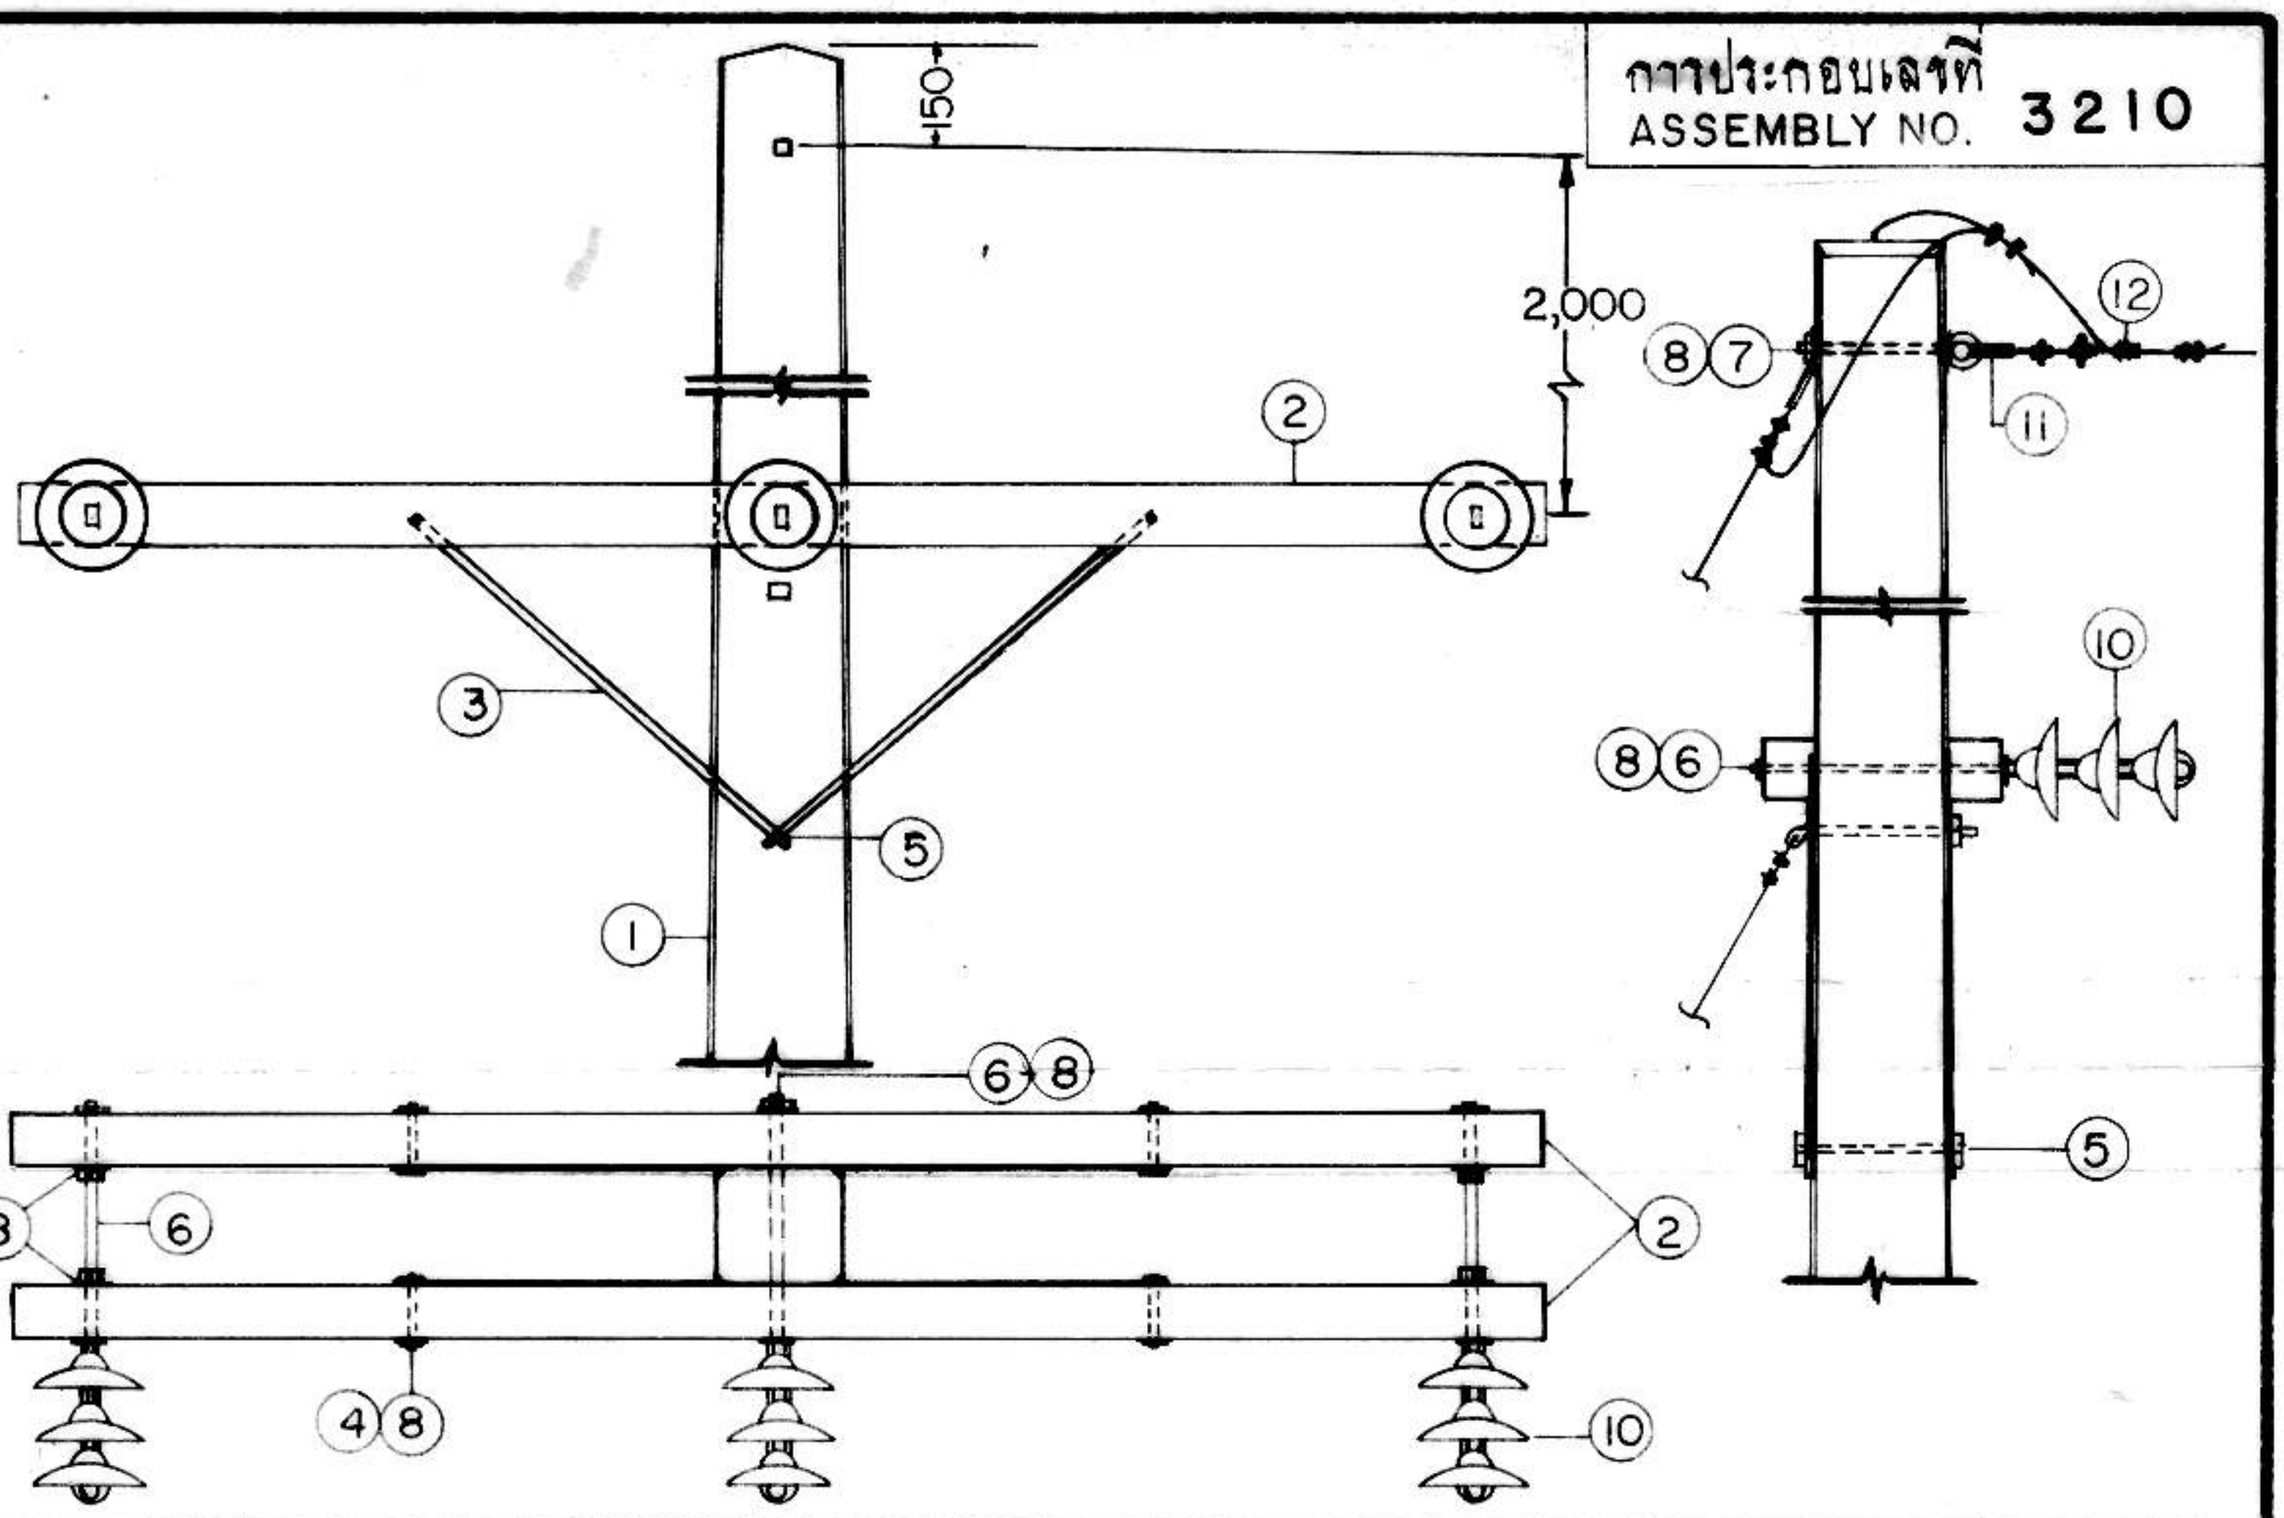

BILL OF MATERIAL

ITEM	DESCRIPTION	REQ'D	MAT. NO.
1	เสาคอนกรีต 14 เมตร POLE, CONCRETE 14 m LONG	1	00010005 (0035)
2	ไม้คอนสายขนาด 100X120X3,000 มม. CROSSARM (H.T.) WOOD, 100X120X3,000 mm	2	00100003 (0101)
3	เหล็กประกันไม้คอนขนาด 40X6X1,000 มม BRACE, FLAT, FOR CROSSARM , 40X6X1,000 mm	4	01200002 (0121)
4	สลักเกลียว M 16X130 มม. BOLT, MACHINE, M 16X130 mm	4	01110200 (0220)
5	สลักเกลียว M 16X250 มม. BOLT, MACHINE, M 16X250 mm	1	01110203 (0223)
6	สลักเกลียวห่วงกลม M 16X450 มม. BOLT, EYE, DOUBLE ARMING, M 16X450 mm	3	01130001 (0247)
7	สลักห่วงกลม M 16X200 มม. BOLT, ROUND EYE, M 16X200 mm	1	01140001 (0253)
8	แหวนเหล็กแบนขนาด 52X52X4.5 มม. รู Ø18 มม. มอก. 258 WASHER, SQUARE, FLAT, 52X52X4.5 mm HOLE Ø18 mm TIS 258	15	01180100 (0355)
9	แหวนสปริง M 16 มอก. 259 WASHER, LOCK, M16 TIS 259	—	01180301 (0365)
10	ลูกถ้วยแขวน มอก. 354 แบบ ง (แบบ 52-4) INSULATOR, SUSPENSION, TYPE TIS 354 TYPE D (CLASS 52-4)	9	03020002 (0415)
11	กามทิมเบิลสำหรับสายขนาด 50-95 ตร.มม. THIMBLE, GUY FOR STEEL WIRE 50-95 mm^2	1	01210302 (0150)
12	ยูแคล้มป์ สลัก 1 ด้าน M 8 CLAMP, SINGLE U-BOLT M 8	4	01230000 (0165)

กองวิศวกรรมและวางแผน	การไฟฟ้าส่วนภูมิภาค	ใช้แทนแบบ .....
ผู้เขียน	ผู้ว่าการ	ถูกแทนโดยแบบ .....
สถาปนิก	การประกอบไม้คอนต่อกันเสาคอนกรีตใน ระบบ 33 kV เมื่อเข้าสายเสาต้นสุดท้าย	เขียนเสร็จวันที่ 20 ส.ค. 13
วิศวกร		แก้แบบวันที่ .....
หัวหน้าแผนก		มิติเป็น ม.ม.
ผู้อำนวยการกอง		มาตราส่วน 1 : 30
รองผู้ว่าการฝ่ายเทคนิค	33 kV DOUBLE CROSSARM ASSEMBLY ON CONCRETE POLE, DEAD END CONSTRUCTION	แบบเลขที่ I50-015/130316
		แผ่นที่ 1 รวมจำนวน 1 แผ่น