
กาวปะกอบเลขที่ ASSEMBLY NO. 0511

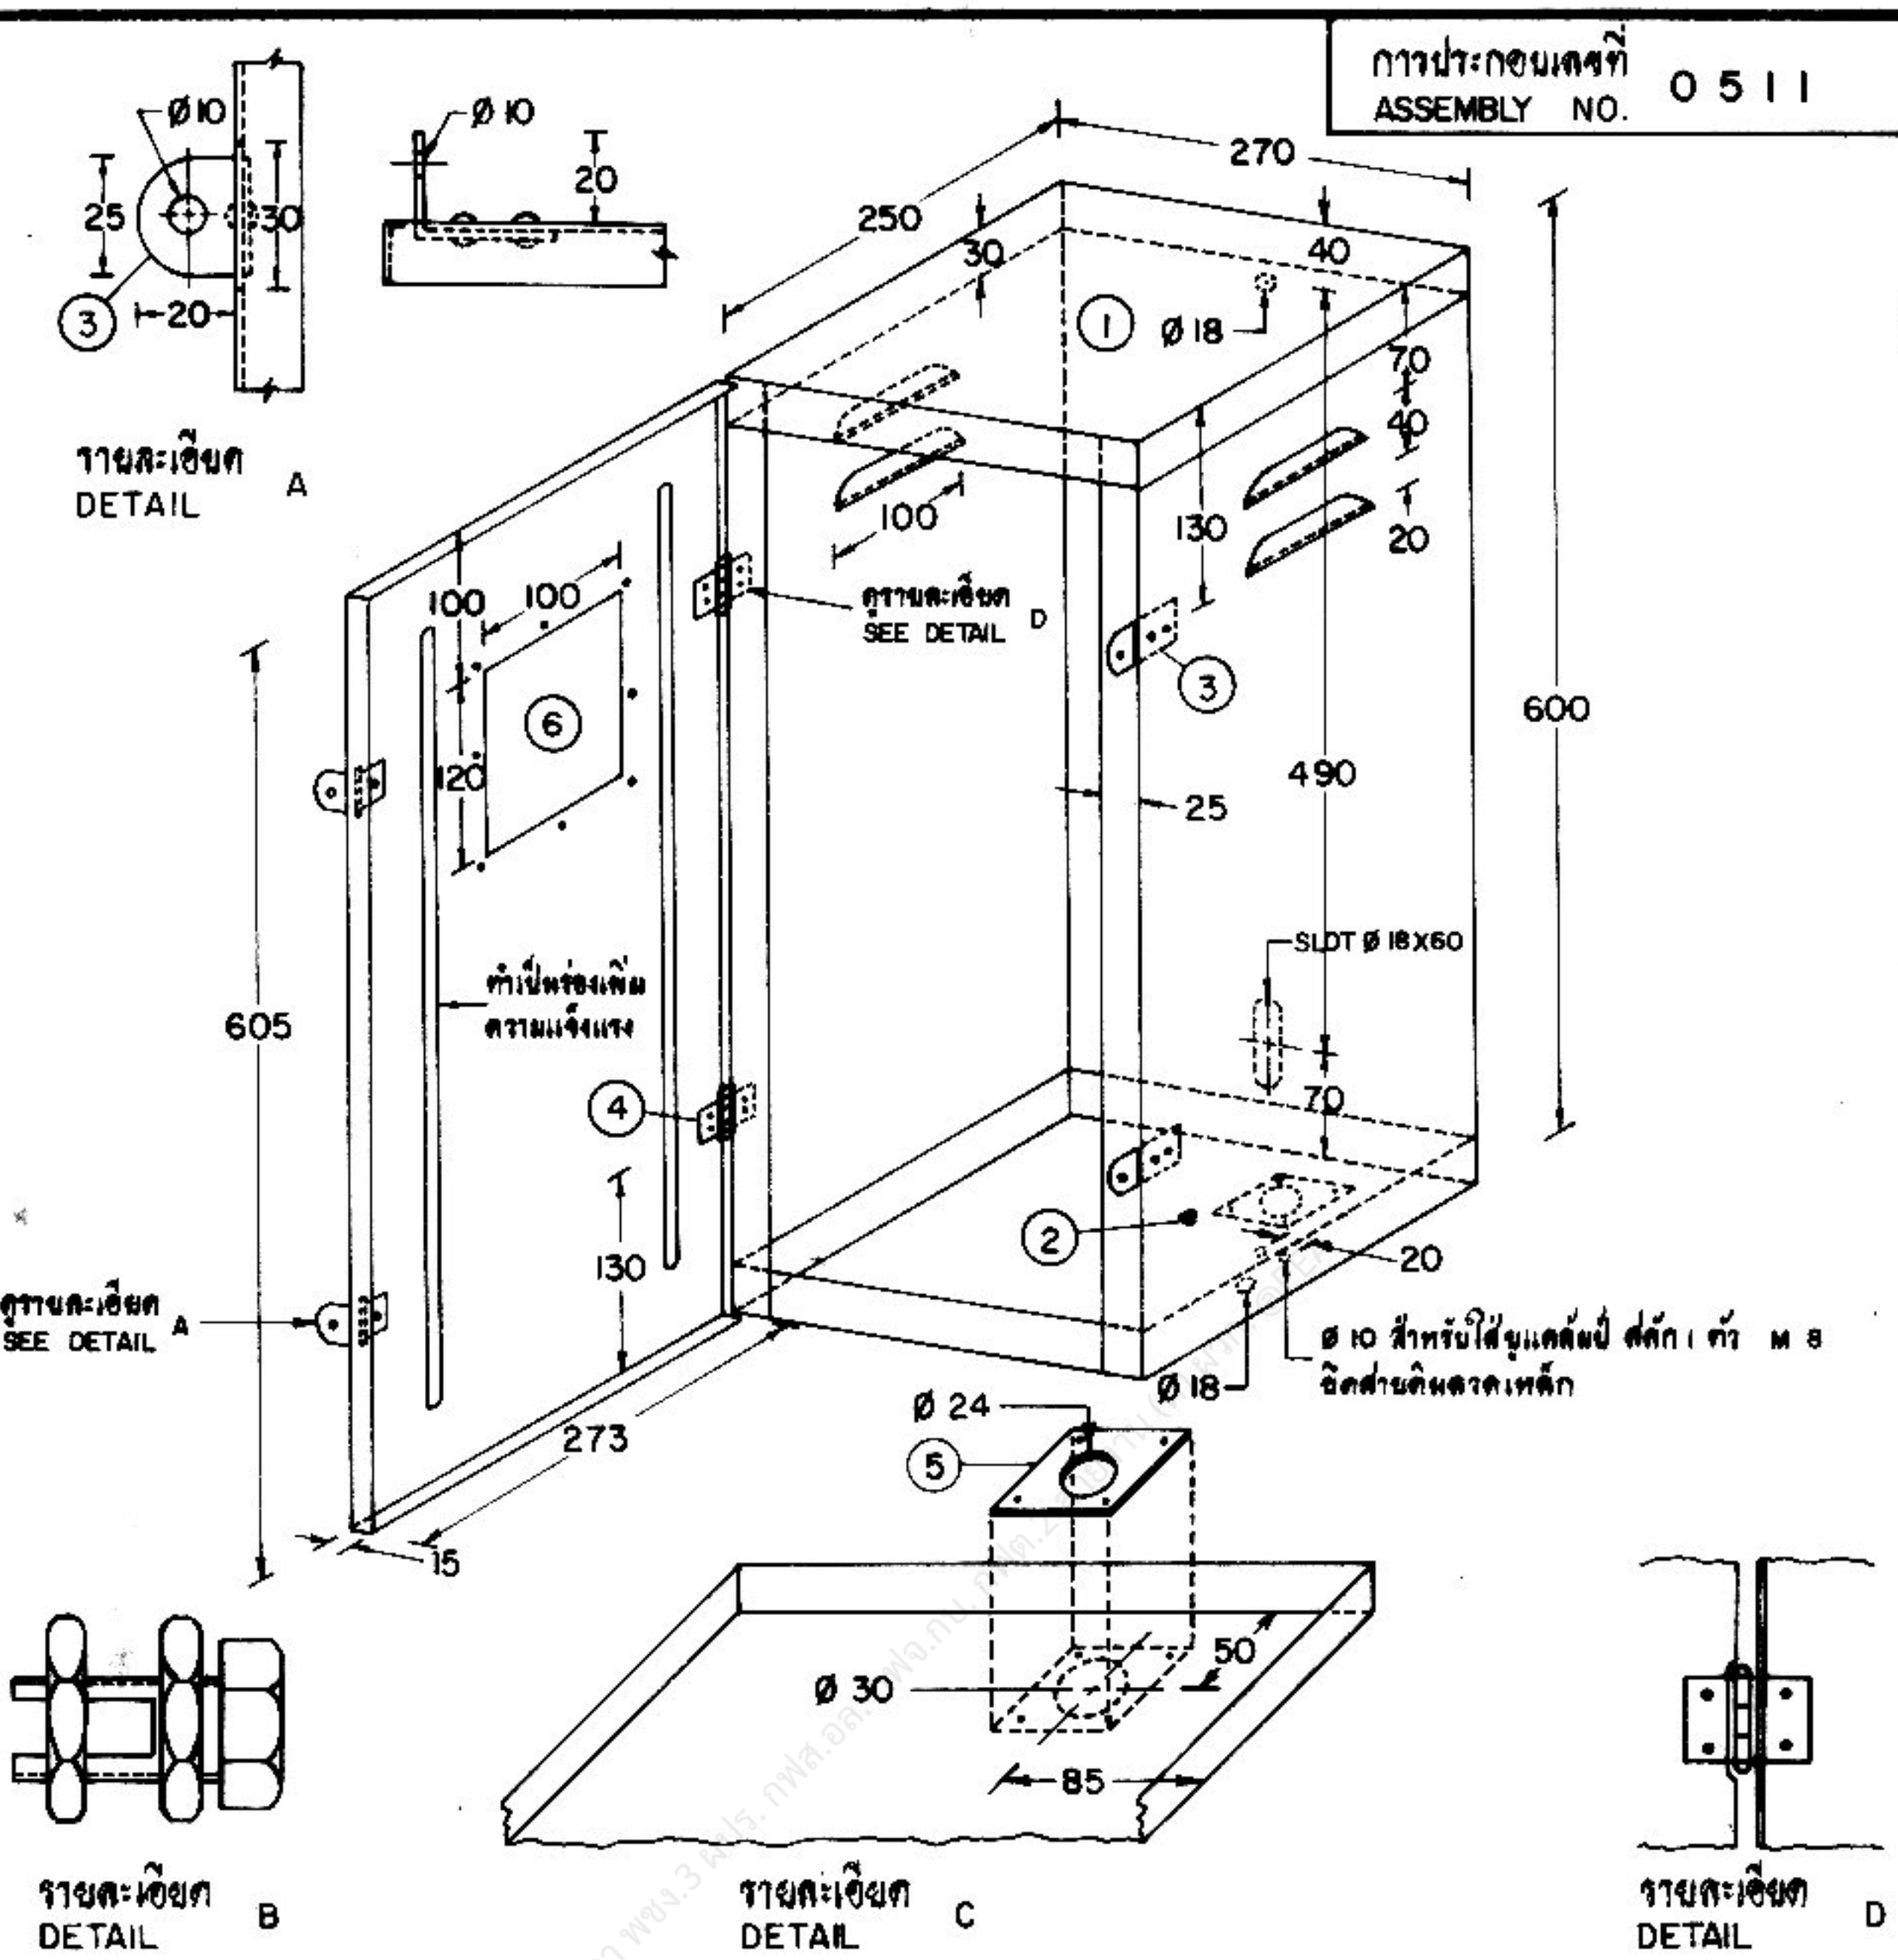

1. ตู้ทำด้วยแผ่นอะลูมิเนียม ความหนา 1.5 มม.
2. จั้วยึดสายดินรับสายทองแดง ขนาด 4–16 ต.มม. ประกอบด้วยสกรูทองเหลืองพร้อมน็อต 2 ตัว (ดูรายละเอียด B)
3. แผ่นเหล็กอาบสังกะสี ความหนา 1.2 มม. พร้อมหมุดย้ำแบบไม่เป็นสนิม
4. บานพับทองเหลือง และหมุดย้ำแบบไม่เป็นสนิม
5. แผ่นเบ็คเกอร์ไลต์ (BAKELITE) ขนาด 50 x 50 มม. หนา 8 มม. (5/16") สำหรับร้อยสาย ตัดและเจาะรูตามรูป และยึดด้วยหมุดย้ำแบบไม่เป็นสนิม (ดูรายละเอียด C)
6. หน้าต่างพลาสติกใสทนความร้อน (ARCYLIC) หรือเทียบเท่า

กองวิศวกรรมไฟฟ้าและเครื่องกล ฝ่ายวิศวกรรม	การไฟฟ้าส่วนภูมิภาค	ใช้แทนแบบ ..... ถูกแทนโดยแบบ ..... เขียนแล้วเมื่อวันที่ 17 ก.ย. 22 แก้ไขเมื่อวันที่ 6 พ.ย. 27 มิติเป็น มม. มาตราส่วน 1 : 75
ผู้เขียน ผู้สำรวจ วิศวกร หัวหน้าแผนก หัวหน้ากอง ผู้อำนวยการฝ่าย	ผู้ว่าการ	
กองผู้ว่าการฝ่ายแผนก	ตู้อะลูมิเนียมใช้นอกอาคารสำหรับดีมานด์มิเตอร์ OUTDOOR ALUMINIUM CABINET FOR DEMAND METER	แบบเลขที่ SAI-015/22048 แผ่นที่ 1 ของจำนวน 1 แผ่น

21 ก.ย. 2522