การประกอบเลขที่ ASSEMBLY NO. 5276

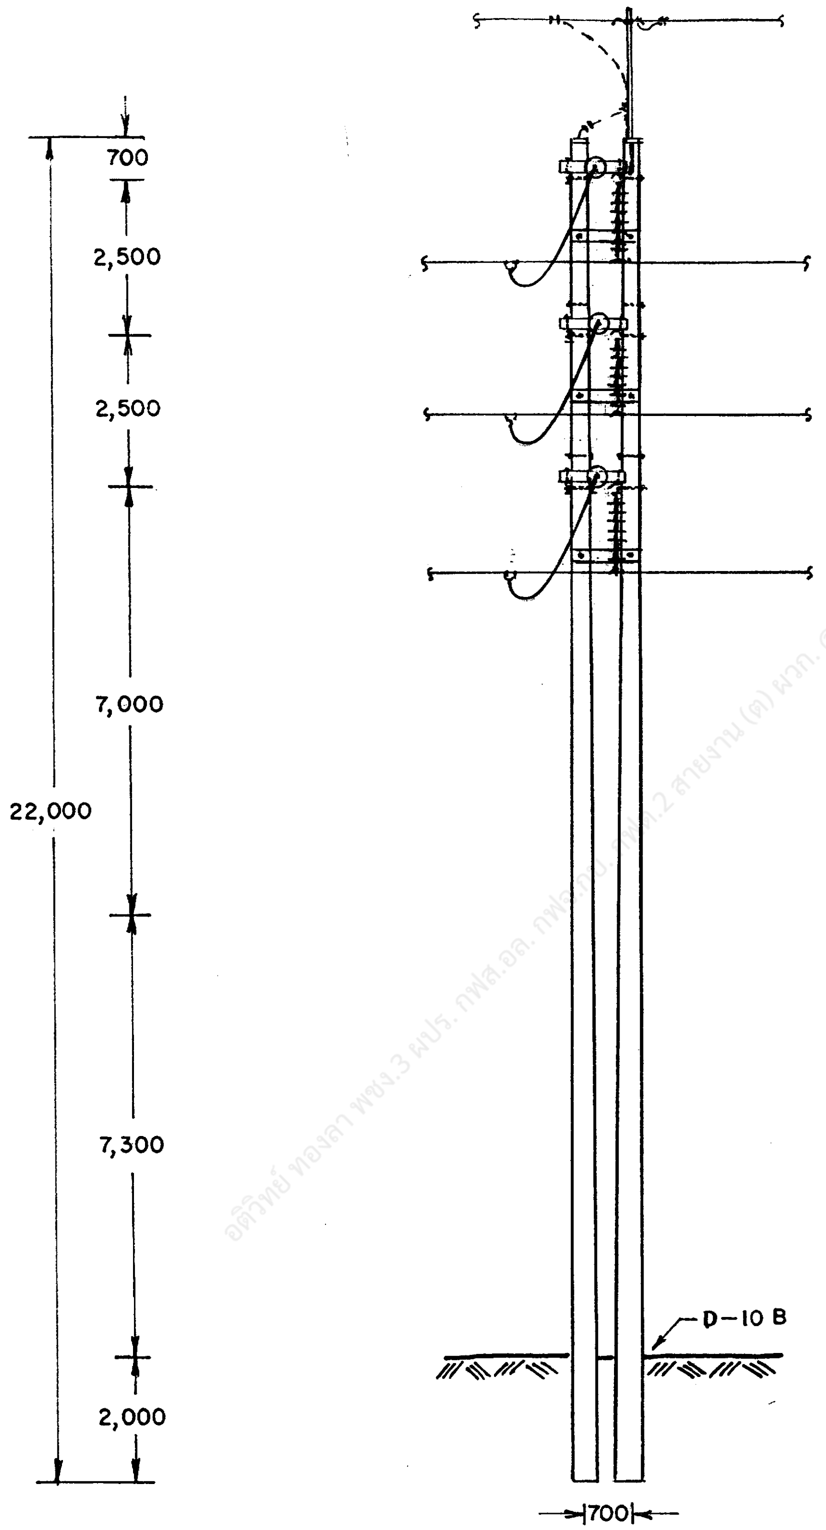

อดิวิทย์ ทองลา พชง.3 ผปร. กฟส.อล. [illegible] 2 สายงาน (ต) ผวก. @PEA

กองวิศวกรรมไฟฟ้าและเครื่องกล ฝ่ายวิศวกรรม	การไฟฟ้าส่วนภูมิภาค	ใช้แทนแบบ ถูกแทนโดยแบบ
ผู้เขียน ผู้สำรวจ วิศวกร หัวหน้าแผนก ผู้อำนวยการกอง ผู้อำนวยการฝ่าย	ผู้ว่าการ 4 ส.ค. 2540 115 kV วงจรเดียว สายไฟฟ้าคู่ เสาต้นต่อแยกสาย แบบ SD-TL-5	เขียนเสร็จวันที่ 30 พ.ค.40 แก้แบบวันที่ มิติเป็น มิลลิเมตร มาตราส่วน 1 : 125
รองผู้ว่าการเทคนิคและบริการ	115 kV SINGLE CIRCUIT DOUBLE CONDUCTOR FOR TAP LINE STRUCTURE TYPE SD-TL-5	แบบเลขที่ SAI-015/40015 แผ่นที่ 1 ของจำนวน 4 แผ่น

4 ส.ค. 2540

การประกอบเลขที่
ASSEMBLY NO. **5276**

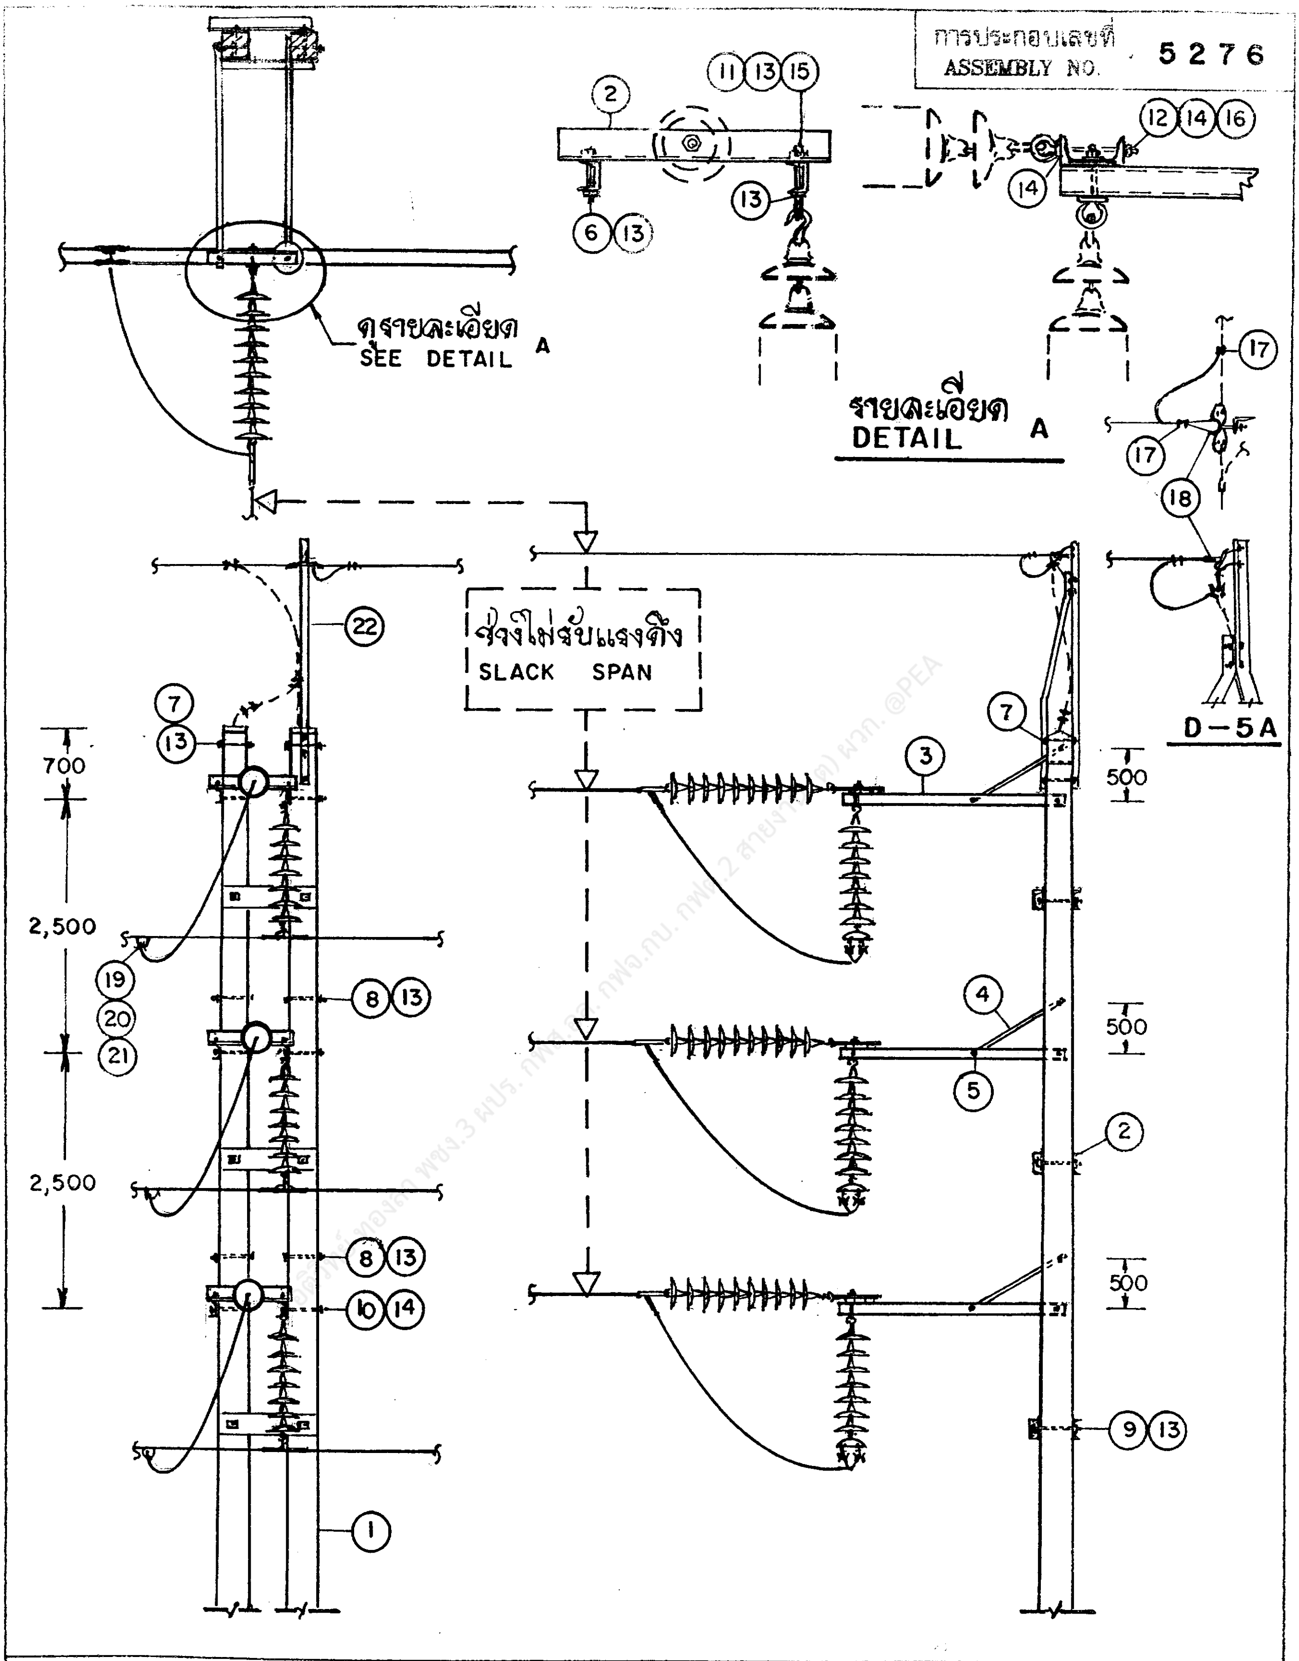

กองวิศวกรรมไฟฟ้าและเครื่องกล ฝ่ายวิศวกรรม	การไฟฟ้าส่วนภูมิภาค	ใช้แทนแบบ ถูกแทนโดยแบบ
ผู้เขียน ผู้สำรวจ วิศวกร หัวหน้าแผนก ผู้อำนวยการกอง ผู้อำนวยการฝ่าย	ผู้ว่าการ	เขียนเสร็จวันที่ 30 พ.ค. 40 แก้แบบวันที่
	115 kV วงจรเดี่ยว สายไฟฟ้าคู่ 4 ส.ค. 2540 เสาต้นต่อแยกสาย แบบ SD-TL-5	มิติเป็น มิลลิเมตร มาตราส่วน 1:25, 1:75
รองผู้ว่าการเทคนิคและบริการ	115 kV SINGLE CIRCUIT DOUBLE CONDUCTOR FOR TAP LINE STRUCTURE TYPE SD-TL-5	แบบเลขที่ SAI-015/40015 แผ่นที่ 2 ของจำนวน 4 แผ่น

4 ส.ค. 2540

การประกอบเลขที่
ASSEMBLY NO. **5276**

บัญชีวัสดุ
BILL OF MATERIAL

ลำดับที่ ITEM	รายละเอียด DESCRIPTION	จำนวน REQ'D	วัสดุเลขที่ MAT. NO.
1	เสาคอนกรีต 22 ม. POLE, CONCRETE, 22.0 mm LONG	2	00010011
2	เหล็กรูปรางน้ำ 200 X 80 x 7.5 มม. ยาว 1,000 มม. STEEL CHANNEL 200 x 80 x 7.5 mm, 1,000 mm LONG	9	01000400
3	คอนเหล็กแบบท้าวแขน ขนาด [100x50x5มม. ยาว 2.25 ม. มอก.116 STEEL, ALLEY ARM, [100x50x5 mm, 2.25 M LONG, TIS 116	3	01000100
4	เหล็กประกับไม้คอน ขนาด 40x6 มม. ยาว 1,000 มม. BRACE, FLAT, FOR CROSSARM 40x6 mm, 1,000 mm LONG	3	01200002
5	สลักเกลียวหัวหกเหลี่ยม M 16x75 มม. BOLT, MACHINE, HEXAGON, M 16x75 mm	3	01110400
6	สลักเกลียว M 16x170 มม. BOLT, MACHINE, M 16x170 mm	3	01110203
7	สลักเกลียว M 16x300 มม. BOLT, MACHINE, M 16x300 mm	5	01110204
8	สลักเกลียว M 16x350 มม. BOLT, MACHINE, M 16x350 mm	4	01110205
9	สลักเกลียว M 16x450 มม. BOLT, MACHINE, M 16x450 mm	6	01110207
10	สลักเกลียว M 20x350 มม. BOLT, MACHINE, M.20x350 mm	3	01110300
11	สลักห่วงโอแวล M 16x150 มม. BOLT, OVAL EYE, M 16x150 mm	3	01150000
12	สลักห่วงโอแวล M 20x350 มม. BOLT, OVAL EYE, M 20x350 mm	3	01150100
13	แหวนรองแบบเรียบ ประเภทจัตุรัสขนาดใหญ่ 52x52x4.5มม. เส้นผ่านศูนย์กลางรู 18 มม. มอก. 258 WASHER, PLAIN, SQUARE, LARGE 52x52x4.5 mm HOLE DIA. 18 mm TIS 258	22	01180100
14	แหวนรองแบบเรียบ ประเภทจัตุรัสขนาดใหญ่ 62x62x6 มม. เส้นผ่านศูนย์กลางรู 22 มม. มอก. 258 WASHER, PLAIN, SQUARE, LARGE 62x62x6 mm HOLE DIA. 22 mm TIS 258	12	01180101
15	แหวนสปริง M 16 มอก. 259 WASHER, LOCK, M 16 TIS 259	3	01180301
16	แหวนสปริง M 20 มอก. 259 WASHER, LOCK, M 20 TIS 259	3	01180302
17	แคล้มป์สลัก 3 ตัว สำหรับลวดเหล็กตีเกลียว 35 ต.มม. CLAMP, TRIPLE BOLTS, FOR STEEL STRANDED WIRE 35 Sq.mm	2	01180303
18	กายทิมเบิล สำหรับลวดเหล็ก 35-50 ต.มม. หรือ 50-95 ต.มม. THIMBLE, GUY, FOR STEEL WIRE 35-50 Sq.mm OR 50-95 Sq.mm	2	หรือ 01210303 OR 01210304
19	คอนเนคเตอร์แบบ T ชนิดบีบ สำหรับสายอะลูมิเนียม 400 ต.มม. กับแผ่นรองชนิด 4 รู CONNECTOR, T-TYPE, COMPRESSION, FOR AL CONDUCTOR MAIN 400 Sq.mm TO NEMA 4-HOLE	6	02500100
20	หางปลา เจาะรู 4 รู ตามมาตรฐาน NEMA สำหรับสายอะลูมิเนียม 400 ต.มม. TERMINAL, COMPRESSION, STRAIGHT PAD, NEMA 4-HOLE, FOR AL 400 Sq.mm	3	02420201

กฟส.อล. กฟจ.กบ. กฟต.2 สายงาน (ต) ผวก. @PEA

กองวิศวกรรมไฟฟ้าและเครื่องกล
ฝ่ายวิศวกรรม

ผู้เขียน สมนึก สาคร
ผู้สำรวจ
วิศวกร
หัวหน้าแผนก
ผู้อำนวยการกอง
ผู้อำนวยการฝ่าย

รองผู้ว่าการเทคนิคและบริการ
4 ส.ค. 2540

การไฟฟ้าส่วนภูมิภาค

ผู้ว่าการ
4 ส.ค. 2540

115 kV วงจรเดี่ยว สายไฟฟ้าคู่
เสาต้นต่อแยกสาย
แบบ SD-TL-5

115 kV SINGLE CIRCUIT DOUBLE CONDUCTOR
FOR TAP LINE STRUCTURE
TYPE SD-TL-5

ใช้แทนแบบ ....
ถูกแทนโดยแบบ ....
เขียนเสร็จวันที่ 21 พ.ค. 40
แก้แบบวันที่ ....
มิติเป็น ....
มาตราส่วน ....

แบบเลขที่ SA1-015/40015
แผ่นที่ 3 ของจำนวน 4 แผ่น

การประกอบเลขที่
ASSEMBLY NO. 5276

ลำดับที่ ITEM	บัญชีวัสดุ BILL OF MATERIAL รายละเอียด DESCRIPTION	จำนวน REQ'D	วัสดุเลขที่ MAT. NO.
21	แผ่นอะลูมิเนียมรูปตัว U สำหรับต่อเชื่อมพร้อมสลักเกลียวและแหวน ALUMINIUM PAD COUPLER, U-SHAPE COMP. WITH BOLTS AND WASHERS	3	-
22	เหล็กฉากรับสายล่อฟ้าทางโค้ง 65 x 65 x 6 มม. ยาว 2,500 มม. STEEL ANGLE, OVERHEAD GROUND WIRE CORNER BAYONET 65x65x6 mm 2,500 mm LOHG	1	01180003

ลำดับที่ ITEM	รายละเอียด DETAIL		
D-5A	การต่อสายล่อฟ้า OVERHEAD GROUND WIRE CONNECTION	1	
D-10B	ฐานรากเสา POLE FOUNDATION	1	
D-3C หรือ/OR D-4C	การประกอบลูกถ้วยแขวน SUSPENSION INSULATOR ASSEMBLY การประกอบลูกถ้วยแขวน SUSPENSION INSULATOR ASSEMBLY	3	
D-17C	การประกอบลูกถ้วยแขวน SUSPENSION INSULATOR ASSEMBLY	3	

ทองลา ปร. กฟส.อล. กฟจ.กบ. กฟต.2 สายงาน (ต) ฟภก. @PEA

หมายเหตุ

หากการต่อแยกสายเป็นแบบสายไฟฟ้าคู่ ให้เปลี่ยน [D-3C หรือ D-4C] เป็น [D-13C หรือ D-14C] ตัดรายการที่ 21 ออกและเพิ่มจำนวนรายการที่ 20 เป็น 6 ชุด

NOTES

IF TAP LINE IS DOUBLE CONDUCTOR, USED [D-13C OR D-14C] INSTEAD OF [D-3C OR D-4C] . AND OMITED ITEM NO.21 AND ADD ITEM NO.20 TO 6 SETS .

กองวิศวกรรมไฟฟ้าและเครื่องกล
ฝ่ายวิศวกรรม

ผู้เขียน สมนึก สาคร
ผู้สำรวจ
วิศวกร
หัวหน้าแผนก
ผู้อำนวยการกอง
ผู้อำนวยการฝ่าย

รองผู้ว่าการเทคนิคและบริการ
4 ส.ค. 2540

การไฟฟ้าส่วนภูมิภาค

ผู้ว่าการ
4 ส.ค. 2540

115 kV วงจรเดี่ยว สายไฟฟ้าคู่
เสาต้นต่อแยกสาย
แบบ SD-TL-5

115 kV SINGLE CIRCUIT DOUBLE CONDUCTOR
FOR TAP LINE STRUCTURE
TYPE SD-TL-5

ใช้แทนแบบ
ถูกแทนโดยแบบ
เขียนเสร็จวันที่ 21 พ.ค. 40
แก้แบบวันที่
มิติเป็น
มาตราส่วน

แบบเลขที่ SA1-015/40015
แผ่นที่ 4 ของจำนวน 4 แผ่น