การประกอบเลขที่
ASSEMBLY NO. 5687 E

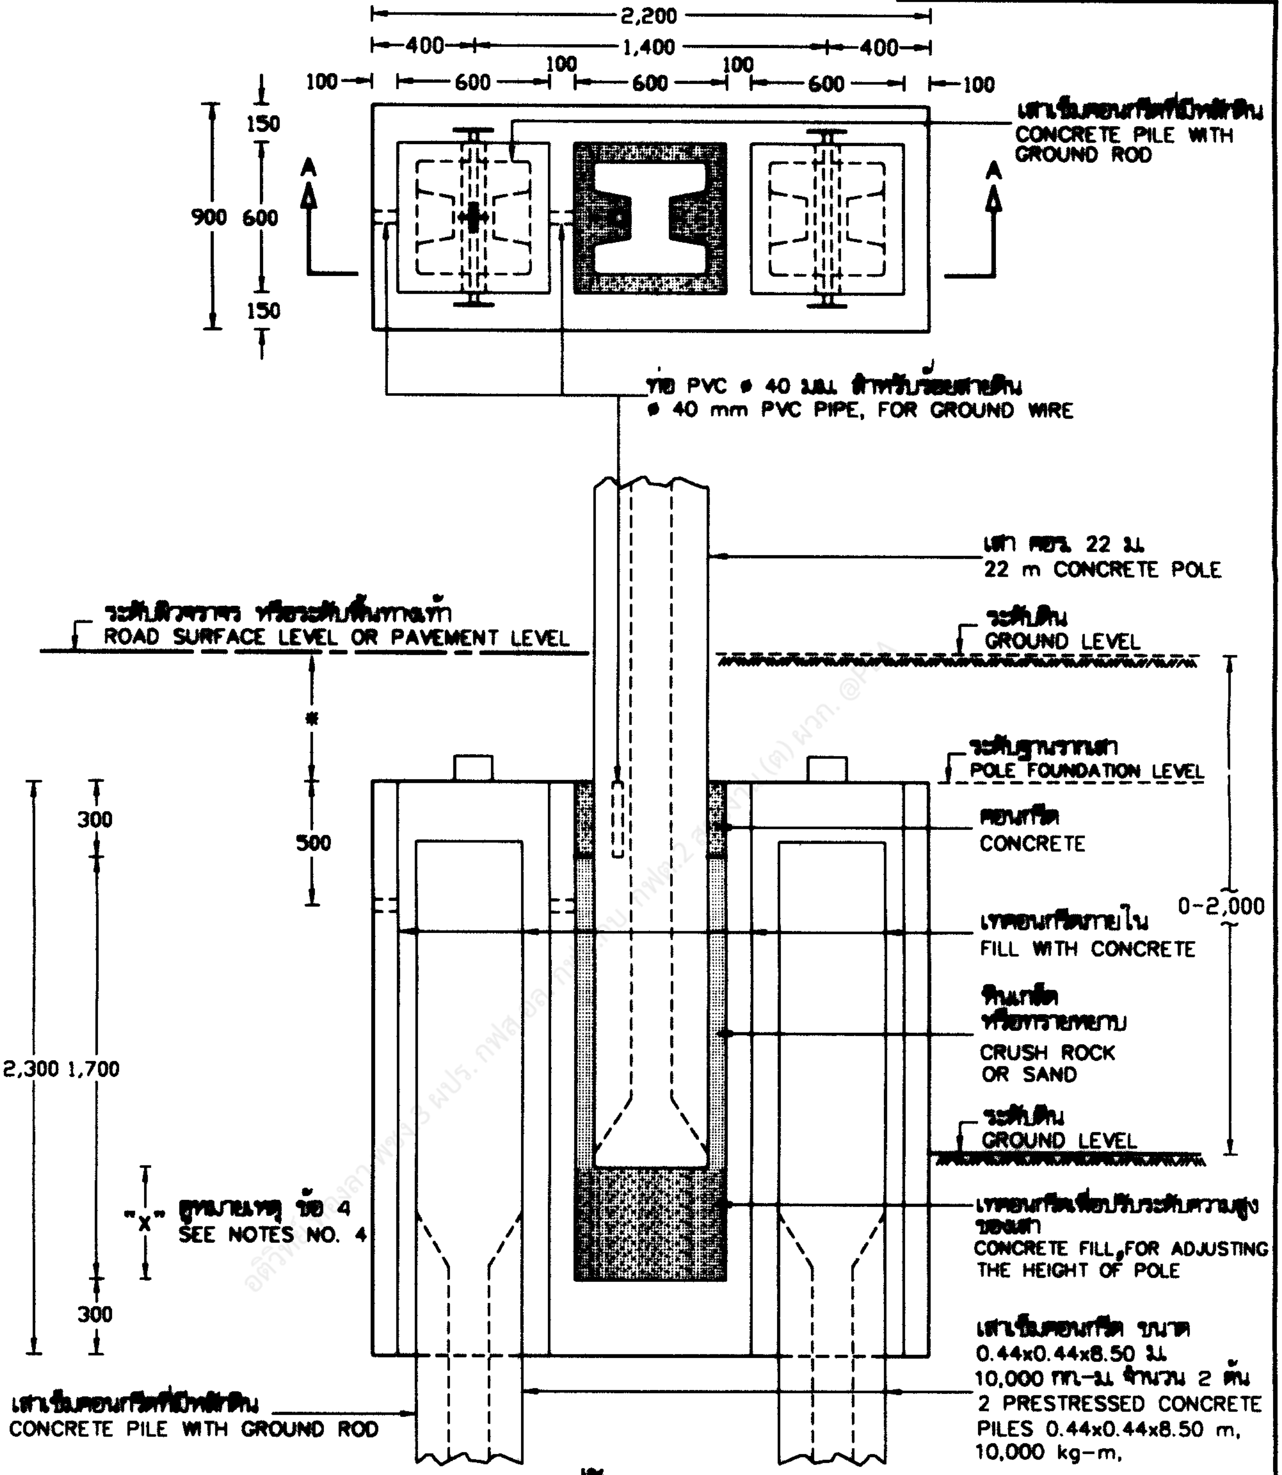
2,200
400
1,400
400
100
600
100
600
100
600
100
150
900
600
150
A
A
เสาเข็มคอนกรีตที่มีหลักดิน
CONCRETE PILE WITH GROUND ROD
ท่อ PVC ø 40 มม. สำหรับร้อยสายดิน
ø 40 mm PVC PIPE, FOR GROUND WIRE
เสา คอร. 22 ม.
22 m CONCRETE POLE
ระดับผิวจราจร หรือระดับพื้นทางเท้า
ROAD SURFACE LEVEL OR PAVEMENT LEVEL
ระดับดิน
GROUND LEVEL
*
500
ระดับฐานรากเสา
POLE FOUNDATION LEVEL
คอนกรีต
CONCRETE
0-2,000
เทคอนกรีตภายใน
FILL WITH CONCRETE
หินเกล็ด
หรือทรายหยาบ
CRUSH ROCK
OR SAND
ระดับดิน
GROUND LEVEL
300
2,300
1,700
"X" ดูหมายเหตุ ข้อ 4
SEE NOTES NO. 4
300
เทคอนกรีตเพื่อปรับระดับความสูงของเสา
CONCRETE FILL, FOR ADJUSTING THE HEIGHT OF POLE
เสาเข็มคอนกรีต ขนาด
0.44x0.44x8.50 ม.
10,000 กก.-ม. จำนวน 2 ต้น
2 PRESTRESSED CONCRETE PILES 0.44x0.44x8.50 m, 10,000 kg-m,
เสาเข็มคอนกรีตที่มีหลักดิน
CONCRETE PILE WITH GROUND ROD

รูปตัด A-A
SECTION

กองมาตรฐานระบบไฟฟ้า
ฝ่ายมาตรฐานและความปลอดภัย

การไฟฟ้าส่วนภูมิภาค

ผู้เขียน ..สมชาย..........
ผู้ตรวจ ....
วิศวกร ....
หัวหน้าแผนก ....
ผู้อำนวยการกอง ....
ผู้อำนวยการฝ่าย ....
รองผู้ว่าการวางแผนและพัฒนาระบบไฟฟ้า
....

ผู้ว่าการ ....

รายละเอียดที่ 10A 23 ก.ย. 2547
ฐานรากเสา (แบบที่ 19 ชนิดหล่อสำเร็จรูป)

DETAIL 10A
POLE FOUNDATION (TYPE 19, PRECAST TYPE)

ใช้แทนแบบ SA1-015/45014
ถูกแทนโดยแบบ ....
เขียนเสร็จวันที่ .10. มี.ค. 2547
แก้แบบวันที่ ....
หน่วยเป็น มิลลิเมตร
มาตราส่วน ....1:30....
แบบเลขที่ SA1-015/47022
แผ่นที่ .1. ของจำนวน .2. แผ่น

23 ก.ย. 2547

การประกอบเลขที่ ASSEMBLY NO. 5687 E

หมายเหตุ

1 ใช้ในกรณีทางตรงหรือทางโค้ง ที่ไม่มีสายยึดโยง (กรณีพื้นที่ก่อสร้างฐานรากเสามีระดับต่ำกว่าระดับผิวจราจร หรือระดับพื้นทางเท้า 0.00-2.00 ม.)

2 ดูรายละเอียดเพิ่มเติมใน แบบเลขที่ IB2-011/44014

3* ดูข้อกำหนดการติดตั้งฐานรากเสาในเขตทางหลวง ตามแบบเลขที่ SA1-015/43012 (การประกอบเลขที่ 5687)

4 ระยะ "X"= 450 มม. สำหรับการก่อสร้างฐานรากเสา ในพื้นที่ทางหลวงที่ไม่มีทางเท้า ส่วนพื้นที่อื่นๆ ระยะ "X"= 0 มม.

NOTES

1 USE FOR STRAIGHT OR ANGLE LINE WITHOUT GUY (IN CASE OF GROUND SURFACE LEVEL IS BETWEEN 0.00–2.00 m LOWER THAN ROAD SURFACE LEVEL OR PAVEMENT LEVEL) .

2 SEE ADDITIONAL DETAIL, DWG. NO. IB2-011/44014 .

3* SEE RECOMMENDATION, FOR POLE FOUNDATION INSTALLATION IN HIGHWAY AREA, DWG. NO SA1-015/43012 (ASSEMBLY NO. 5687) .

4 THE "X" IS 450 mm HEIGHT FOR FOUNDATION CONSTRUCTION IN HIGHWAY AREA WHICH HAVE NO PAVEMENT, OTHER AREA THE "X" IS ZERO .

อติวิทย์ ทองลา พชง.3 ผปร. กฟส.อล. กฟจ.กน. กฟฉ.2 สายงาน (ต) ผวก. @PEA

กองมาตรฐานระบบไฟฟ้า
ฝ่ายมาตรฐานและความปลอดภัย

ผู้เขียน ...สมชาย...
ผู้ตรวจ ...
วิศวกร ...
หัวหน้าแผนก ...
ผู้อำนวยการกอง ...
ผู้อำนวยการฝ่าย ...

รองผู้ว่าการวางแผนและพัฒนาระบบไฟฟ้า

การไฟฟ้าส่วนภูมิภาค

ผู้ว่าการ ...

รายละเอียดที่ 10A 23 ก.ย. 2547
ฐานรากเสา (แบบที่ 19 ชนิดสำเร็จรูป)

DETAIL 10A
POLE FOUNDATION (TYPE 19, PRECAST TYPE)

ใช้แทนแบบ SA1-015/45014
ถูกแทนโดยแบบ ...
เขียนเสร็จวันที่ 10 ส.ค. 2547
แก้แบบวันที่ ...
หน่วยเป็น ...
มาตราส่วน ...
แบบเลขที่ SA1-015/47022
แผ่นที่ 2 ของจำนวน 2 แผ่น

23 ก.ย. 2547