การประกอบเลขที่ ASSEMBLY NO.	5427

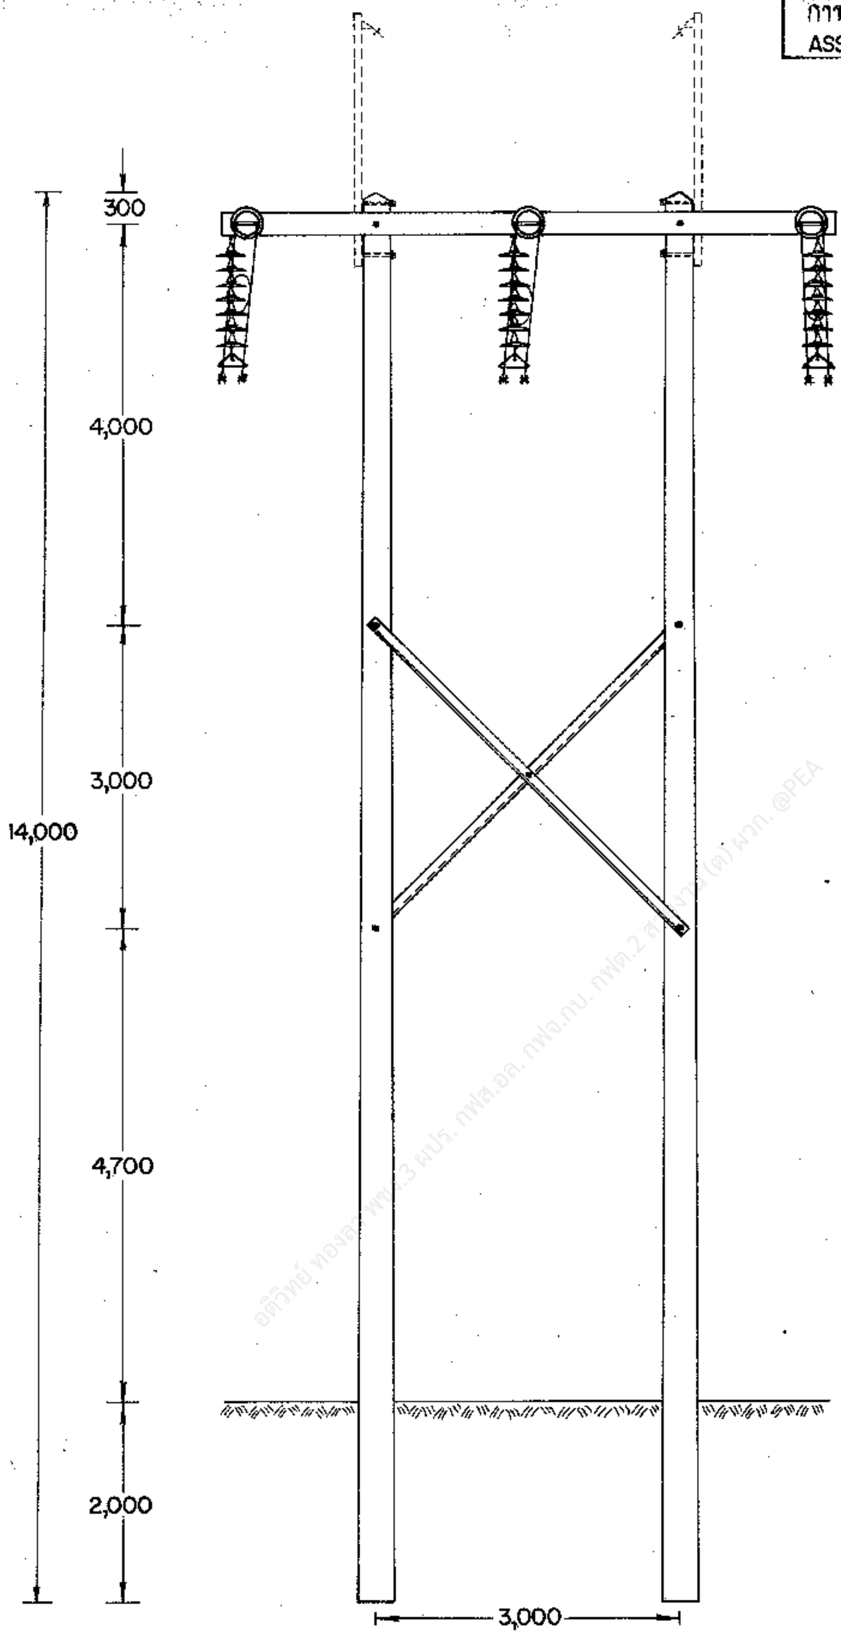

กองวิศวกรรมไฟฟ้าและเครื่องกล ฝ่ายวิศวกรรม	# การไฟฟ้าส่วนภูมิภาค	ใช้แทนแบบ ถูกแทนโดยแบบ
ผู้เขียน ผู้สำรวจ วิศวกร หัวหน้าแผนก หัวหน้ากอง ผู้อำนวยการฝ่าย	ผู้ว่าการ 24 มิ.ย. 23	เขียนเสร็จวันที่ 4 มค. 23 แก้แบบวันที่ คิดเป็น มม. มาตราส่วน 1 : 75
	115 kV วงจรเดี่ยว สายไฟฟ้าคู่ เสาคู่แบบ H-FRAME ใช้เสาขนาด 14 ม. แบบ SD-HF-1	
รองผู้ว่าการฝ่ายเทคนิค	115 kV SINGLE CIRCUIT DOUBLE CONDUCTOR H-FRAME STRUCTURE 14 m POLE TYPE SD-HF-1	แบบเลขที่ SAI-015/23024 แผ่นที่ 1 ของจำนวน 4 แผ่น

[illegible] ธ.ค. 2523

อดิวิทย์ ทองลา พชง.3 ผปร. กฟส.อล. กฟจ.กน. กฟต.2 สายงาน (ต) ผวก. @PEA

การประกอบเลขที่ 5427
ASSEMBLY NO.

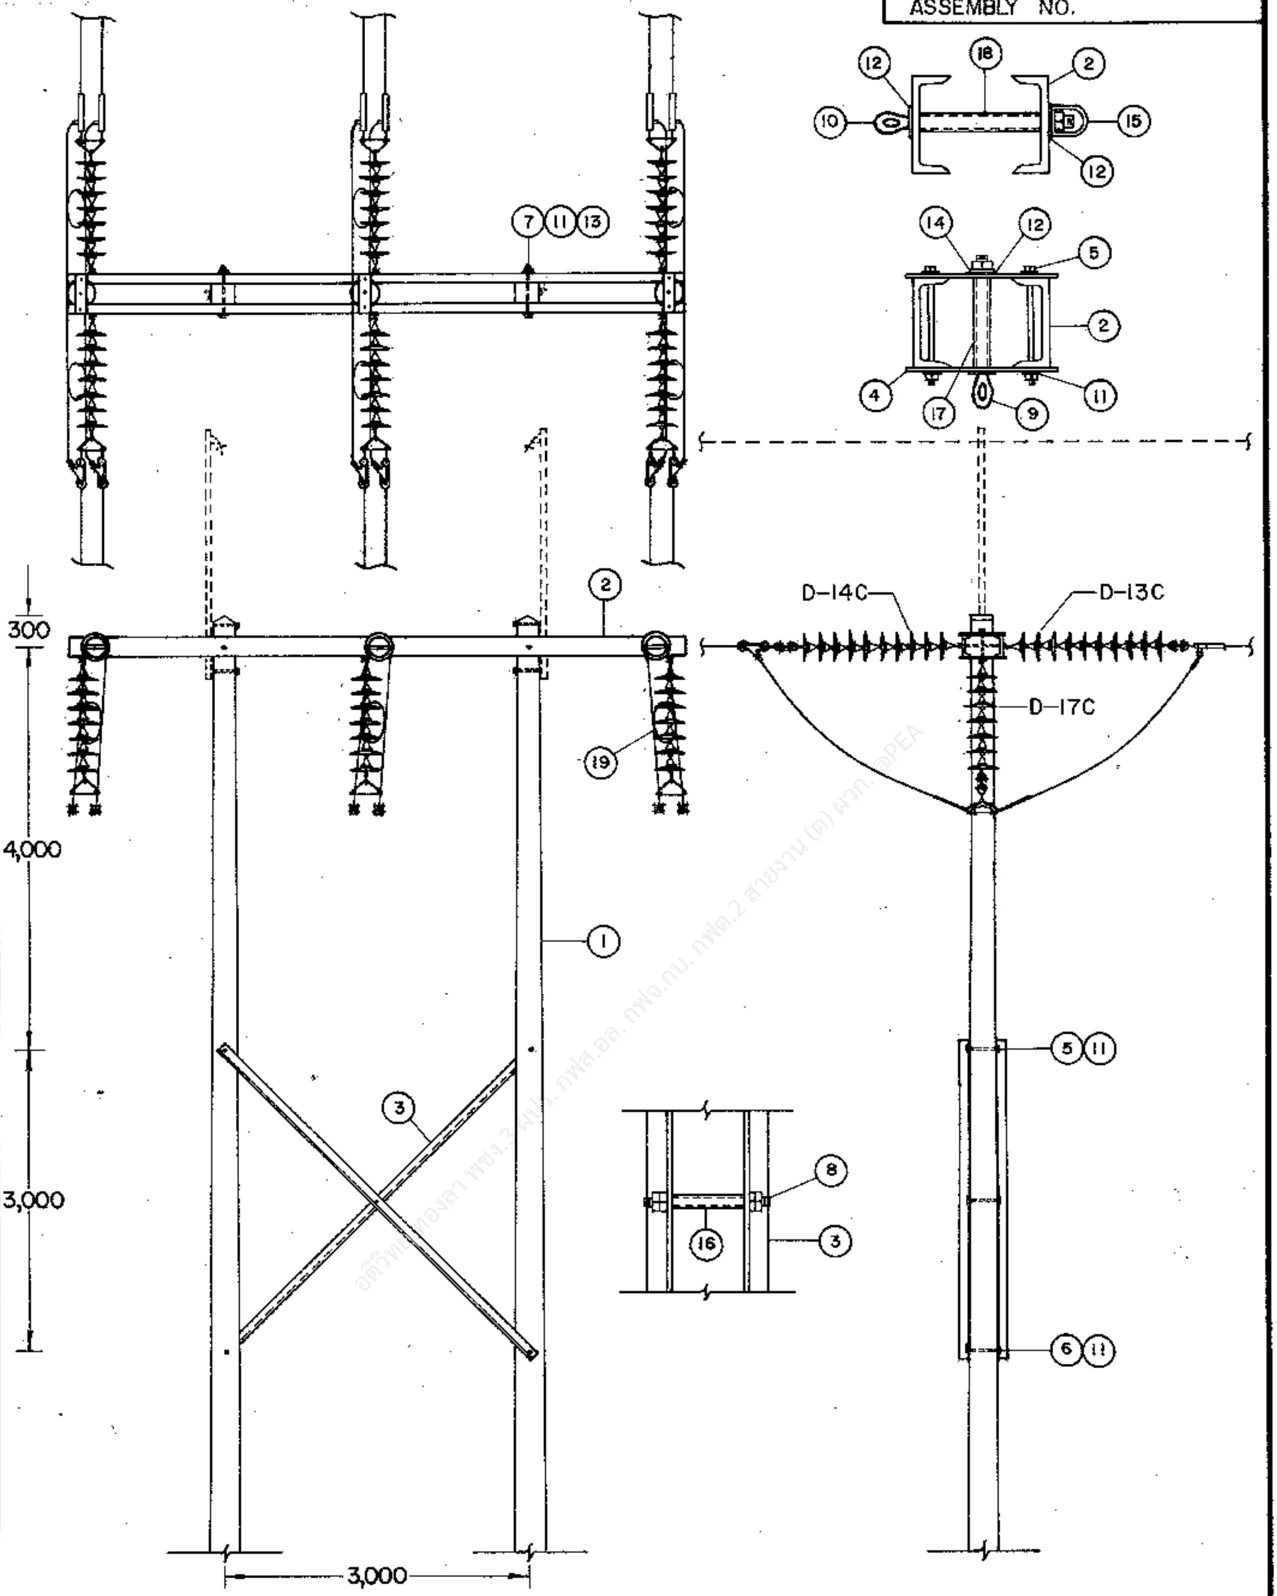

12
18
2
10
15
12
14
12
5
2
4
11
17
9
7 11 13
2
300
D-14C
D-13C
D-17C
19
4,000
1
5 11
3
8
16
3
3,000
6 11
3,000

อดิวิทย์ ทองลา พชง.3 ผปร. กฟส.อล. กฟจ.กบ. กฟต.2 สายงาน (ต) ผวก. @PEA

กองวิศวกรรมไฟฟ้าและเครื่องกล
ฝ่ายวิศวกรรม

ผู้เขียน
ผู้สำรวจ
วิศวกร
หัวหน้าแผนก
หัวหน้ากอง
ผู้อำนวยการฝ่าย

รองผู้ว่าการฝ่ายเทคนิค

การไฟฟ้าส่วนภูมิภาค

ผู้ว่าการ .... 24 มี.ค. 23

115 kV วงจรเดี่ยว สายไฟฟ้าคู่
เสาคู่แบบ H-FRAME ใช้เสายาว 14 ม.
แบบ SD - HF - 1

115 kV SINGLE CIRCUIT DOUBLE CONDUCTOR
H-FRAME STRUCTURE 14 m POLE
TYPE SD-HF-1

ใช้แทนแบบ........
ถูกแทนโดยแบบ........
เขียนเสร็จวันที่ 4 ม.ค. 23
แก้แบบวันที่........
มิติเป็น มม.
มาตราส่วน 1 : 75

แบบเลขที่ SAL-015/23024
แผ่นที่ 2 ของจำนวน 4 แผ่น

19 มี.ค. 2523

การประกอบเลขที่ ASSEMBLY NO. 5427

บัญชีวัสดุ
BILL OF MATERIAL

ลำดับที่ ITEM	รายละเอียด DESCRIPTION	จำนวน REQ'D	วัสดุเลขที่ MAT. NO.
1	เสาคอนกรีต 14 ม. POLE, CONCRETE 14 m LONG	2	00010006 (0036)
2	เหล็กรูปรางน้ำ ขนาด 200 X 80 X 7.5 มม. ยาว 6.00 ม. (ดูรายละเอียด A) STEEL CHANNEL 200 X 80 X 7.5 mm , 6.00 m LONG (SEE DETAIL A)	2	0100040l (2676)
3	เหล็กฉาก ขนาด 75 X 75 X 6 มม. ยาว 4.50 ม. (ดูรายละเอียด B) STEEL ANGLE 75 X 75 X 6 mm , 4.50 m LONG (SEE DETAIL B)	2	01010102 (2678)
4	แผ่นเหล็ก ขนาด 6 X 100 X 450 มม. (เจาะรูกึ่งกลางให้เป็นขนาด Ø 22 มม.) PLATE, STEEL 6 X 100 X 450 mm (DRILLING THE CENTER HOLE Ø 22 mm)	6	01030002 (0143)
5	สลักเกลียว M 16 X 250 มม. BOLT, MACHINE, M 16 X 250 mm	8	01110203 (0223)
6	สลักเกลียว M 16 X 300 มม. BOLT, MACHINE, M 16 X 300 mm	2	01110204 (0224)
7	สลักเกลียว M 16 X 400 มม. BOLT, MACHINE, M 16 X 400 mm	2	01110206 (0226)
8	สลักเกลียวตลอด M 16 X 400 มม. BOLT, DOUBLE ARMING M 16 X 400 mm	1	01120000 (0243)
9	สลักห่วงโอแวล M 20 X 350 มม. BOLT, OVAL EYE M 20 X 350 mm	3	01150100 (0260)
10	สลักห่วงโอแวล M 20 X 450 มม. BOLT, OVAL EYE M 20 X 450 mm	3	01150101 (0261)
11	แหวนสี่เหลี่ยมแบน 52X52X4.5 มม. รู Ø 18 มม. มอก. 258 WASHER, SQUARE, FLAT 52X52X4.5 mm HOLE Ø 18 mm TIS 258	20	01180100 (0355)
12	แหวนสี่เหลี่ยมแบน 62 X 62 X 6 มม. รู Ø 22 มม. มอก. 258 WASHER, SQUARE, FLAT 62 X 62 X 6 mm HOLE Ø 22 mm TIS 258	12	01180101 (0356)
13	แหวนสปริง M 16 มอก. 259 WASHER, LOCK, M 16, TIS 259	2	01180301 (0365)
14	แหวนสปริง M 20 มอก. 259 WASHER, LOCK, M 20, TIS 259	3	01180302 (0366)
15	ตาเล็ก สำหรับสลักเกลียว EYELET FOR BOLT M 20	3	01180002 (0346)
16	ท่อเหล็ก ชื่อขนาด 20 มม. หนา 2.65 มม. ยาว 220 มม. PIPE, IRON DIA. 20 mm ID, 2.65 mm THICKNESS, 220 mm LONG	1	—
17	ท่อเหล็ก ชื่อขนาด 25 มม. หนา 3.25 มม. ยาว 200 มม. PIPE, IRON DIA. 25 mm ID, 3.25 mm THICKNESS, 200 mm LONG	3	—
18	ท่อเหล็ก ชื่อขนาด 25 มม. หนา 3.25 มม. ยาว 310 มม. PIPE, IRON DIA. 25 mm ID, 3.25 mm THICKNESS, 310 mm LONG	3	—
19	ปรีฟอร์มแยกสาย SPACER, HELICAL ROD, PREFORMED	6	—

กองวิศวกรรมไฟฟ้าและเครื่องกล
ฝ่ายวิศวกรรม

ผู้เขียน
ผู้ตรวจ
วิศวกร
หัวหน้าแผนก
หัวหน้ากอง
ผู้อำนวยการฝ่าย
รองผู้ว่าการฝ่ายเทคนิค

การไฟฟ้าส่วนภูมิภาค

ผู้ว่าการ 24 มี.ค.23

115 kV วงจรเดี่ยว สายไฟฟ้าคู่
เสาคู่แบบ H-FRAME ใช้เสาขนาด 14 ม.
แบบ SD-HF-1

115 kV SINGLE CIRCUIT DOUBLE CONDUCTOR
H-FRAME STRUCTURE 14 m POLE
TYPE SD-HF-1

ใช้แทนแบบ
ถูกแทนโดยแบบ
เขียนเสร็จวันที่ 4 ม.ค. 23
แก้แบบวันที่
มิติเป็น
มาตราส่วน
แบบเลขที่ SAI-015/23024
แผ่นที่ 3 ของจำนวน 4 แผ่น

การประกอบเลขที่
ASSEMBLY NO. 5427

บัญชีวัสดุ
BILL OF MATERIAL

ลำดับที่ ITEM	รายละเอียด DESCRIPTION	จำนวน REQ'D	วัสดุเลขที่ MAT. NO.
D-13C	การประกอบลูกถ้วยแขวน SUSPENSION INSULATOR ASSEMBLY	3	
D-14C	การประกอบลูกถ้วยแขวน SUSPENSION INSULATOR ASSEMBLY	3	
D-17C	การประกอบลูกถ้วยแขวน SUSPENSION INSULATOR ASSEMBLY	3	
D-10A	ฐานรากเสา POLE FOUNDATION	2	

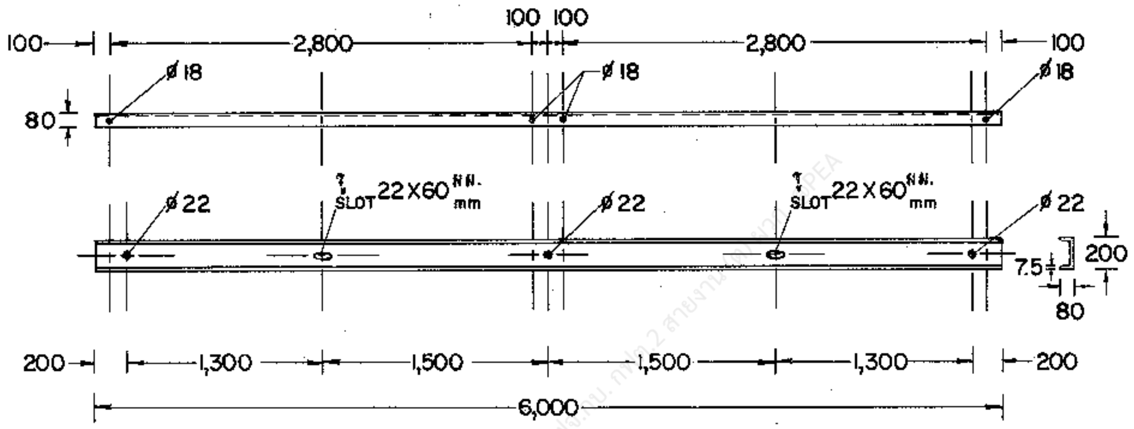

100 100
100
2,800
2,800
100
ø18
ø18
ø18
80
รู SLOT 22X60 มม. mm
รู SLOT 22X60 มม. mm
ø22
ø22
ø22
7.5
200
80
200
1,300
1,500
1,500
1,300
200
6,000

รายละเอียด
DETAIL A

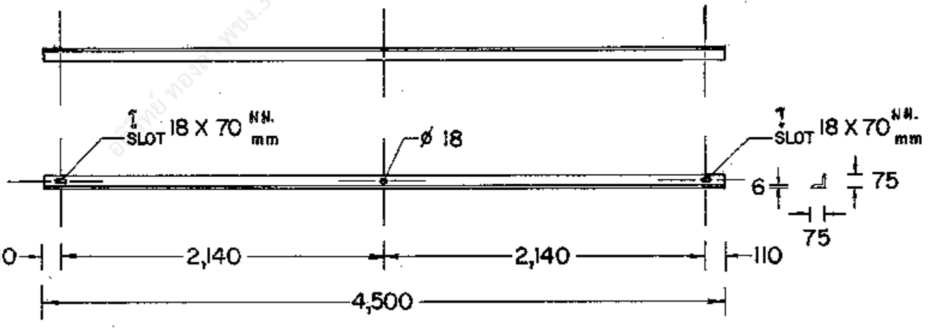

รู SLOT 18 X 70 มม. mm
ø18
รู SLOT 18 X 70 มม. mm
6
75
75
110
2,140
2,140
110
4,500

รายละเอียด
DETAIL B

กองวิศวกรรมไฟฟ้าและเครื่องกล ฝ่ายวิศวกรรม	การไฟฟ้าส่วนภูมิภาค	ใช้แทนแบบ ถูกแทนโดยแบบ
ผู้เขียน ผู้สำรวจ วิศวกร หัวหน้าแผนก หัวหน้ากอง ผู้อำนวยการฝ่าย	ผู้ว่าการ 24 มี.ค. 23	เขียนเสร็จวันที่ 4 ม.ค. 23 แก้แบบวันที่
	115 kV วงจรเดี่ยว สายไฟฟ้าคู่ เสาคู่แบบ H-FRAME ใช้เสาขนาด 14 ม. แบบ SD-HF-1	มิติเป็น มม. มาตราส่วน 1 : 50
28 มี.ค. 23 รองผู้ว่าการฝ่ายเทคนิค	115 kV SINGLE CIRCUIT DOUBLE CONDUCTOR H-FRAME STRUCTURE 14 m POLE TYPE SD-HF-1	แบบเลขที่ SAI-015/23024 แผ่นที่ 4 จากจำนวน 4 แผ่น

19 มี.ค. 2523