การประกอบเลขที่ ASSEMBLY NO. 3806

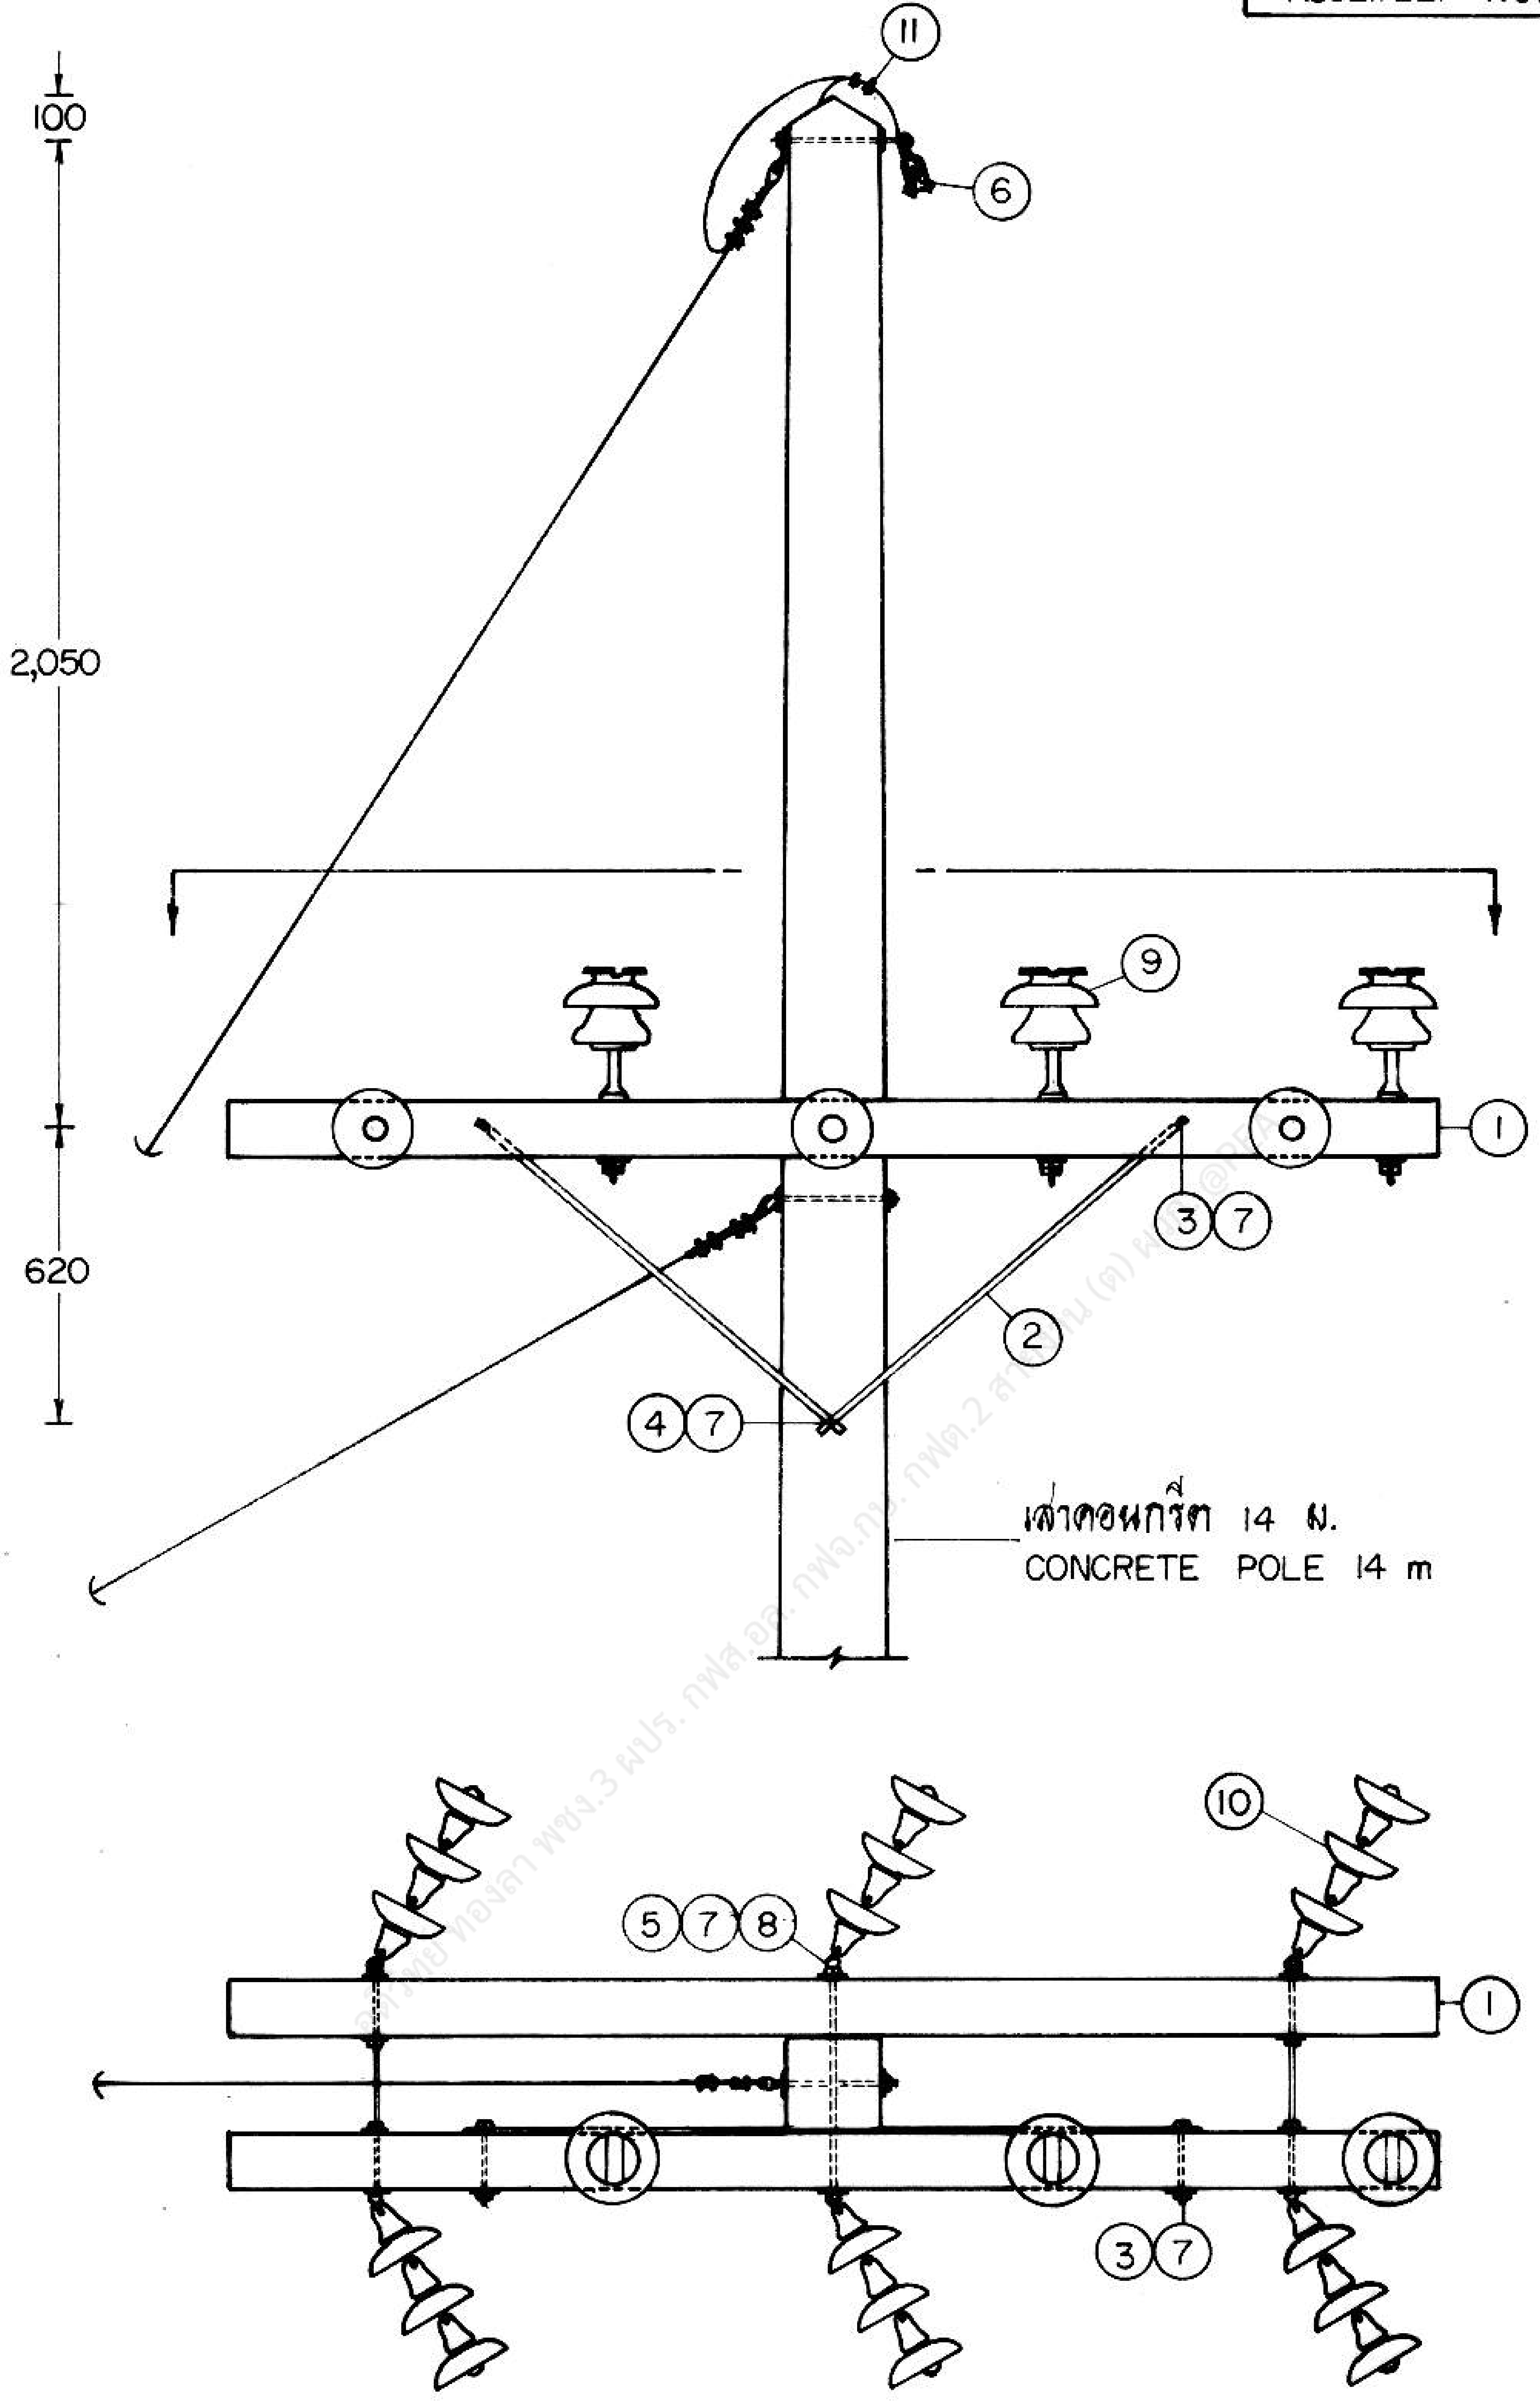
11
6
100
2,050
620
9
1
3 7
2
4 7
เสาคอนกรีต 14 ม.
CONCRETE POLE 14 m
10
5 7 8
1
3 7

กองวิศวกรรมไฟฟ้าและเครื่องกล
ฝ่ายวิศวกรรม

ผู้เขียน
ผู้สำรวจ
วิศวกร
หัวหน้าแผนก
หัวหน้ากอง
ผู้อำนวยการฝ่าย

รองผู้ว่าการฝ่ายเทคนิค

การไฟฟ้าส่วนภูมิภาค

ผู้ว่าการ 4 มิ.ย. 24

การประกอบคอน คอร.สปัน กับเสาคอนกรีต
ระบบ 33 kV
สำหรับทางโค้ง 30° - 60°

SPUN PRESTRESSED CONCRETE CROSSARM ASSEMBLY
33 kV SYSTEM
ANGLE STRUCTURE 30°-60°

ใช้แทนแบบ
ถูกแทนโดยแบบ
เขียนเสร็จวันที่ 28 พ.ค. 24
แก้แบบวันที่
มิติเป็น มม.
มาตราส่วน 1 : 25

แบบเลขที่ SAI-015/24016
แผ่นที่ 1 จากจำนวน 2 แผ่น

การประกอบเลขที่
ASSEMBLY NO. 3806

บัญชีวัสดุ
BILL OF MATERIAL

ลำดับที่ ITEM	รายละเอียด DESCRIPTION	จำนวน REQ D	วัสดุเลขที่ MAT. NO.
1	คอน คอร. สปัน (สำหรับเข้าปลายสาย) 120 X 120 X 2,500 มม. CROSSARM, SPUN PRESTRESSED (FOR DEADENDING) 120 X 120 X 2,500 mm	2	00110004
2	เหล็กประกับไม้คอน 40 X 6 X 1,000 มม. BRACE, FLAT, FOR CROSSARM 40 X 6 X 1,000 mm	2	01200002
3	สลักเกลียว M 16 X 170 มม. BOLT, MACHINE, M 16 X 170 mm	2	01110201
4	สลักเกลียว M 16 X 250 มม. BOLT, MACHINE, M 16 X 250 mm	1	01110203
5	สลักเกลียวห่วงกลม M 16 X 500 มม. BOLT, DOUBLE ARMING, ROUND EYE, M 16 X 500 mm	3	01130002
6	กราวด์วายร์แคล้มป์ สำหรับเสาคอนกรีต GROUND WIRE SUPPORT AND CLAMP, FOR CONCRETE POLE	1	01230201
7	แหวนสี่เหลี่ยมแบน 52 X 52 X 4.5 มม. รู Ø 18 มม. มอก. 258 WASHER, SQUARE, FLAT 52 X 52 X 4.5 mm HOLE Ø 18 mm TIS 258	13	01180100
8	นัทรูปห่วง M 16 DIN 582 NUT, EYE, M 16 DIN 582	3	01180001
9	ลูกถ้วยก้านตรง 33 kV มอก. 279 แบบ ค (แบบ 56-3) พร้อมก้าน INSULATOR, PIN TYPE, 33 kV TIS 279 TYPE C (CLASS 56-3) COMP. WITH PIN	3	03000002 03100001
10	ลูกถ้วยแขวน มอก. 354 แบบ ง (แบบ 52-4) INSULATOR, SUSPENSION TYPE, TIS 354 TYPE D (CLASS 52-4)	18	03020002
11	ยูแคล้มป์ สลัก 1 ตัว M 8 (ไวร์ โร้ป คลิ๊พ) CLAMP, SINGLE U-BOLT, M 8 (WIRE ROPE CLIP)	3	01230000

หมายเหตุ

1 รายละเอียดและข้อกำหนดการใช้งานของ คอน คอร. สปัน (สำหรับเข้าปลายสาย) ดูแบบเลขที่ SAI-015/24011

2 ชุดยึดโยงด้านข้างสำหรับโครงสร้างทางโค้ง 30°-60° เลือกขนาดสายยึดโยงได้จากหลักเกณฑ์ ในแบบเลขที่ SAI-015/21051

NOTES

1 DETAIL AND APPLICATION OF SPUN PRESTRESSED CONCRETE CROSSARM (FOR DEADENDING) SEE DWG. NO. SAI-015/24011

2 FOR SIDE GUYING, SELECT SIZE OF GUY WIRE FROM REGULATION IN DWG. NO. SAI-015/21051

กองวิศวกรรมไฟฟ้าและเครื่องกล ฝ่ายวิศวกรรม	การไฟฟ้าส่วนภูมิภาค	ใช้แทนแบบ ถูกแทนโดยแบบ
ผู้เขียน ผู้สำรวจ วิศวกร หัวหน้าแผนก หัวหน้ากอง ผู้อำนวยการฝ่าย	ผู้ว่าการ 4 มิ.ย. 24 การประกอบคอน คอร. สปัน กับเสาคอนกรีต ระบบ 33 kV สำหรับทางโค้ง 30°-60°	เขียนเสร็จวันที่ 28 พ.ค. 24 แก้แบบวันที่ มิติเป็น มาตราส่วน
รองผู้ว่าการฝ่ายเทคนิค	SPUN PRESTRESSED CONCRETE CROSSARM ASSEMBLY 33 kV SYSTEM ANGLE STRUCTURE 30°-60°	แบบเลขที่ SAI-015/24016 แผ่นที่ 2 ของจำนวน 2 แผ่น