

การประกอบเลขที่ ASSEMBLY NO. 0524

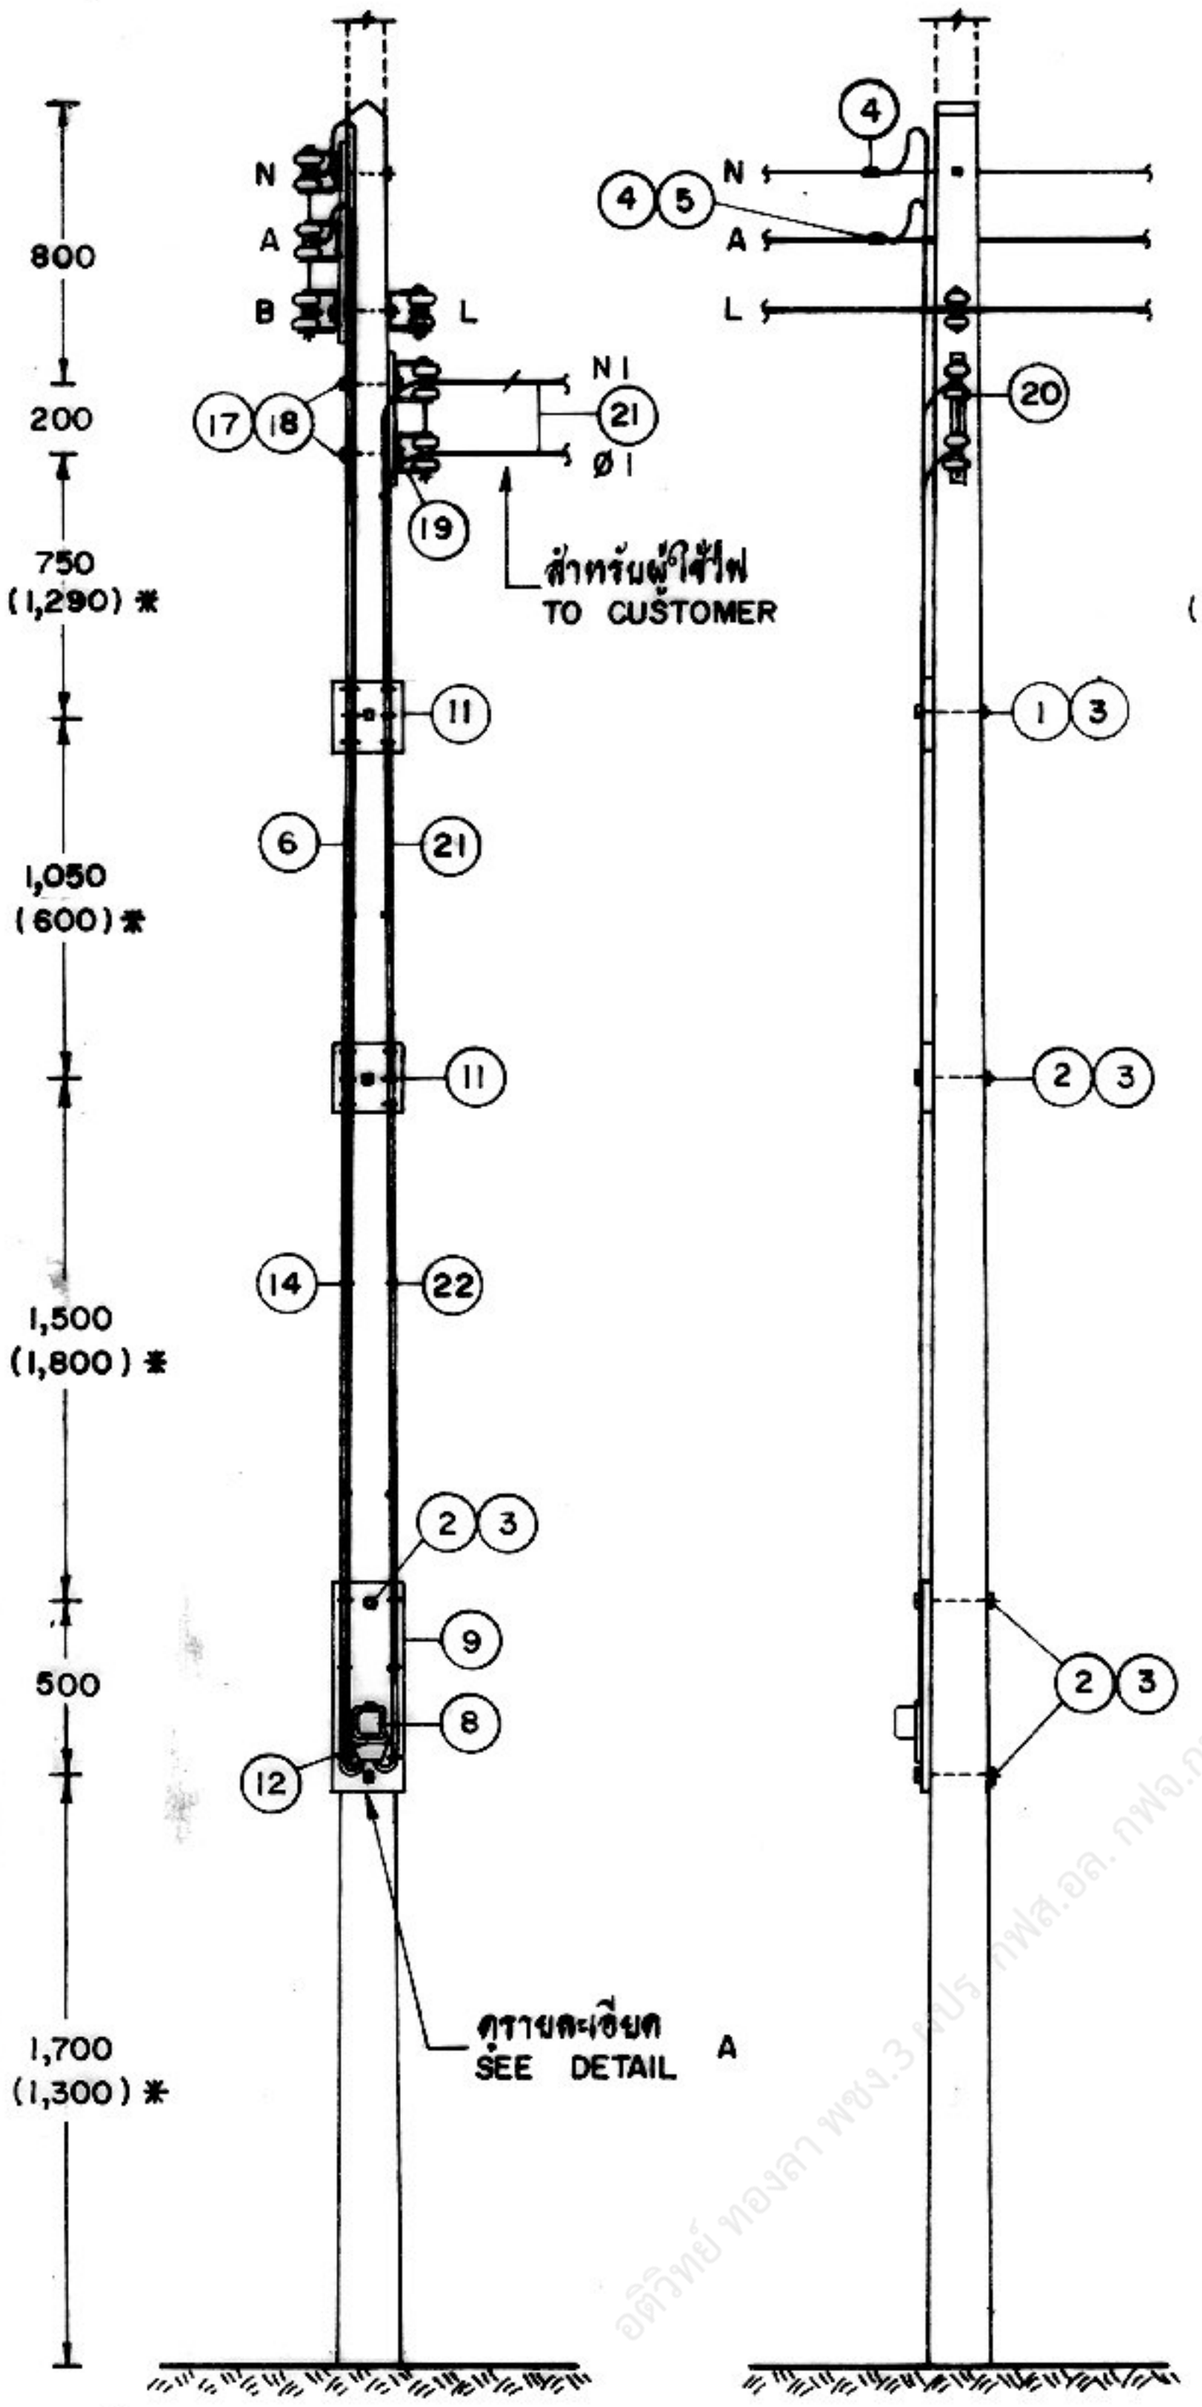

แบบที่ TYPE 1

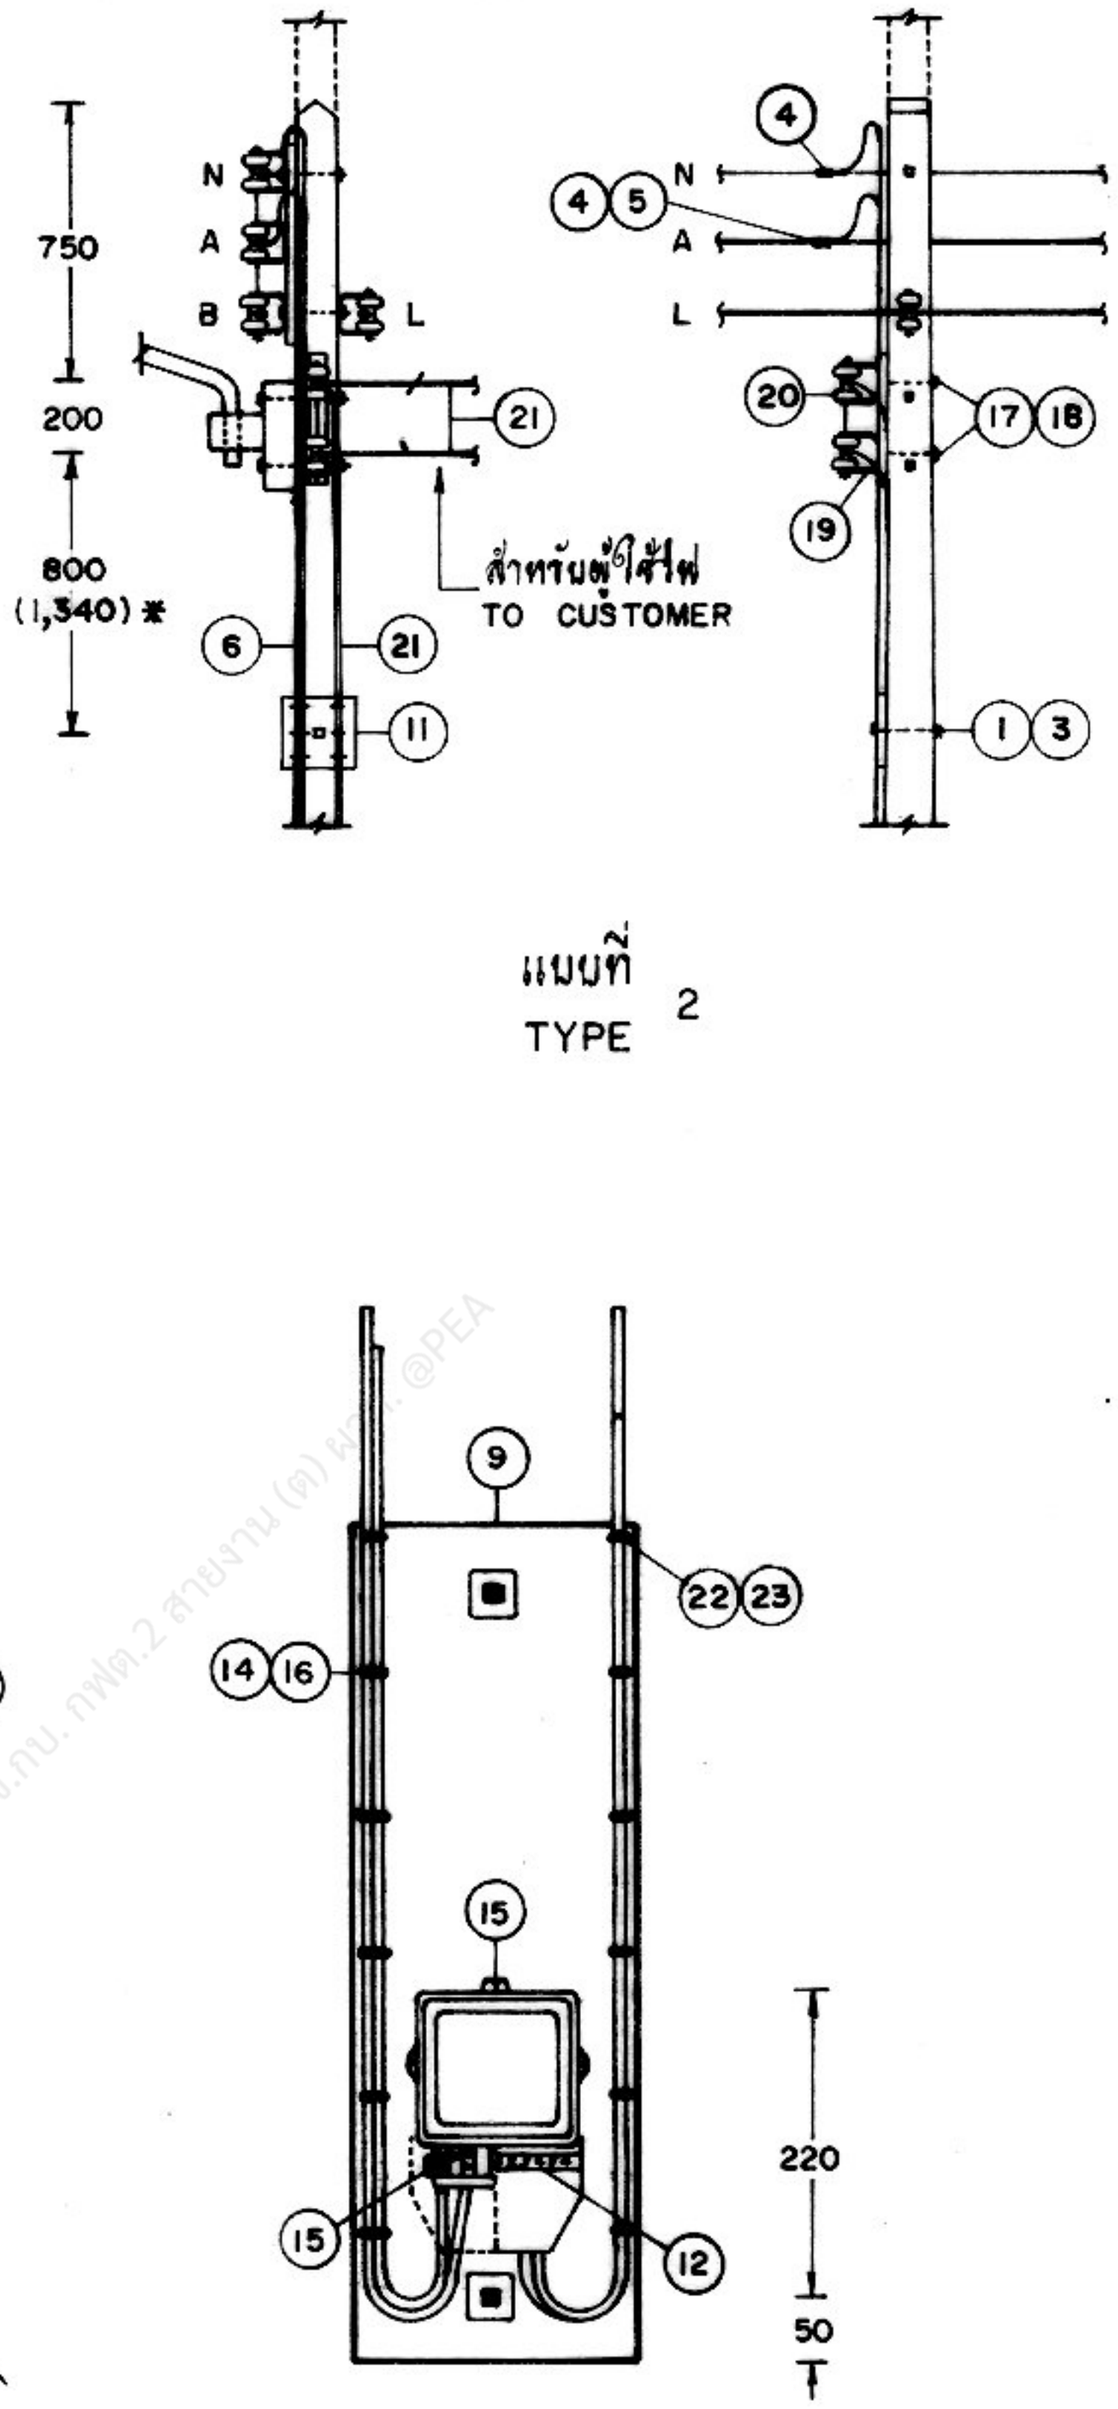

แบบที่ TYPE 2


รายละเอียด DETAIL A

* สำหรับเสาคอนกรีต 8 ม. รุ่นเก่า ที่เขาะรูตามแบบเลขที่ 140-021/130159
FOR OLD 8 m CONCRETE POLE ACCORDING TO DWG. NO. 140-021/130159


กองวิศวกรรมไฟฟ้าและเครื่องกล ฝ่ายวิศวกรรม	การไฟฟ้าส่วนภูมิภาค	ใช้แทนแบบ ถูกแทนโดยแบบ เขียนเสร็จวันที่ 20 มิ.ย. 23 แก้แบบวันที่ 8 ก.ค. 26 * มิติเป็น มม. มาตราส่วน 1 : 40
ผู้เขียน ผู้สำรวจ วิศวกร หัวหน้าแผนก หัวหน้ากอง ผู้อำนวยการฝ่าย	ผู้ว่าการ 13 พ.ย. 2523 การติดตั้งมิเตอร์ 1 เฟส 220 โวลต์ ขนาด 3-5 แอมป์ บนเสาคอนกรีต 8 ม. จำนวน 1 เครื่อง	
รองผู้ว่าการฝ่ายเทคนิค	3-5 A, 1-Ø, 220 V METER INSTALLATION ON 8 m CONCRETE POLE 1 UNIT	แบบเลขที่ SAI-015/23071 แผ่นที่ 1 รองจำนวน 6 แผ่น

10 พ.ย. 2523

การประกอบเลขที่ ASSEMBLY NO. 0524

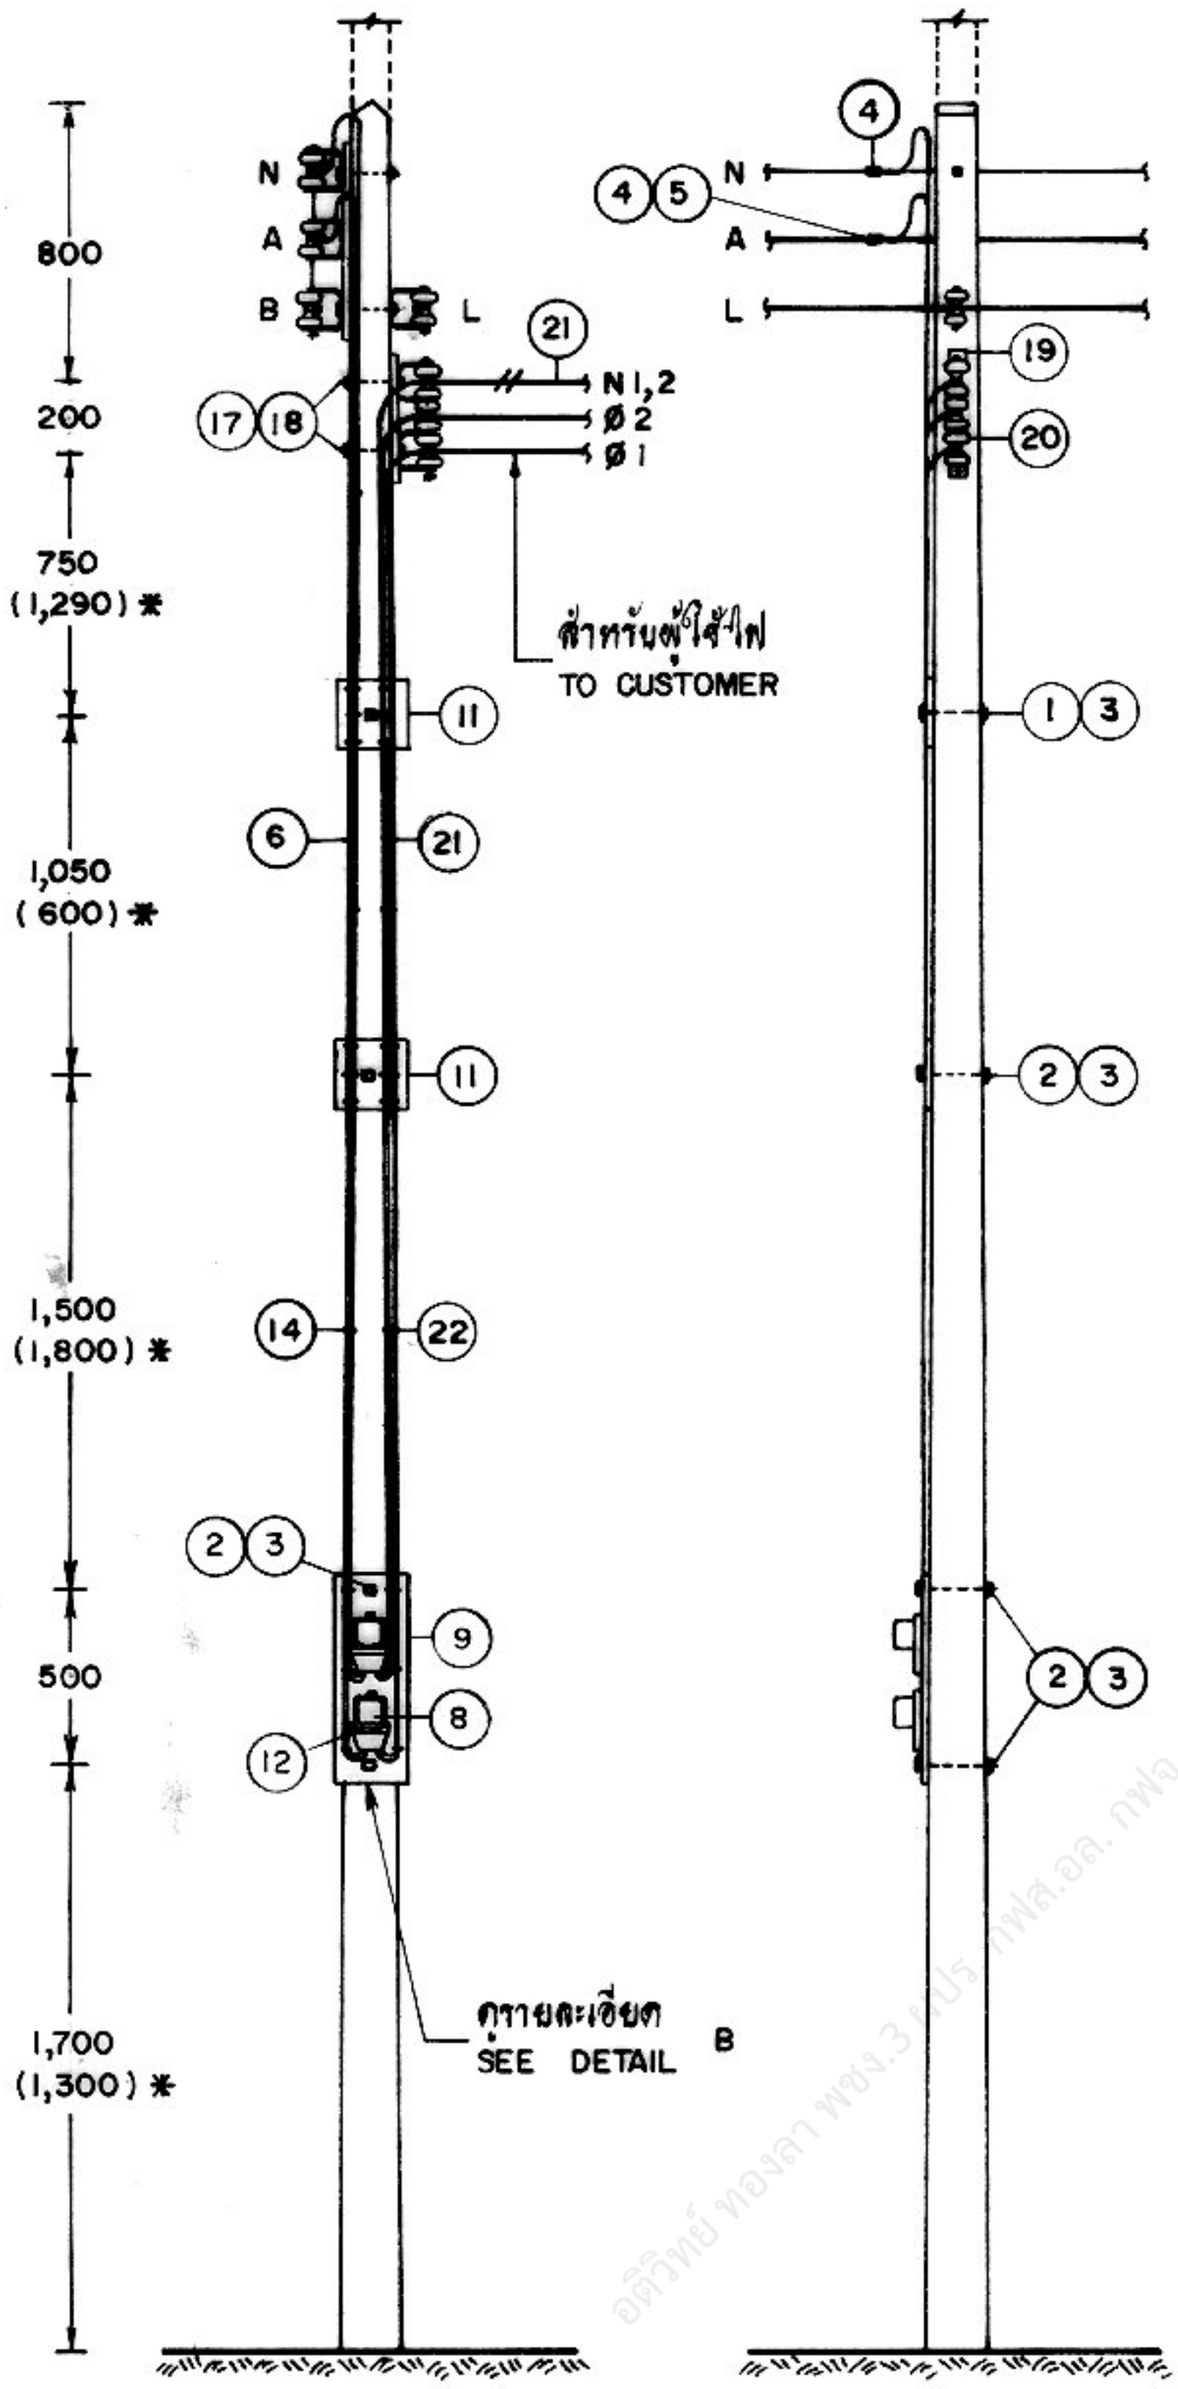

แบบที่ TYPE 1

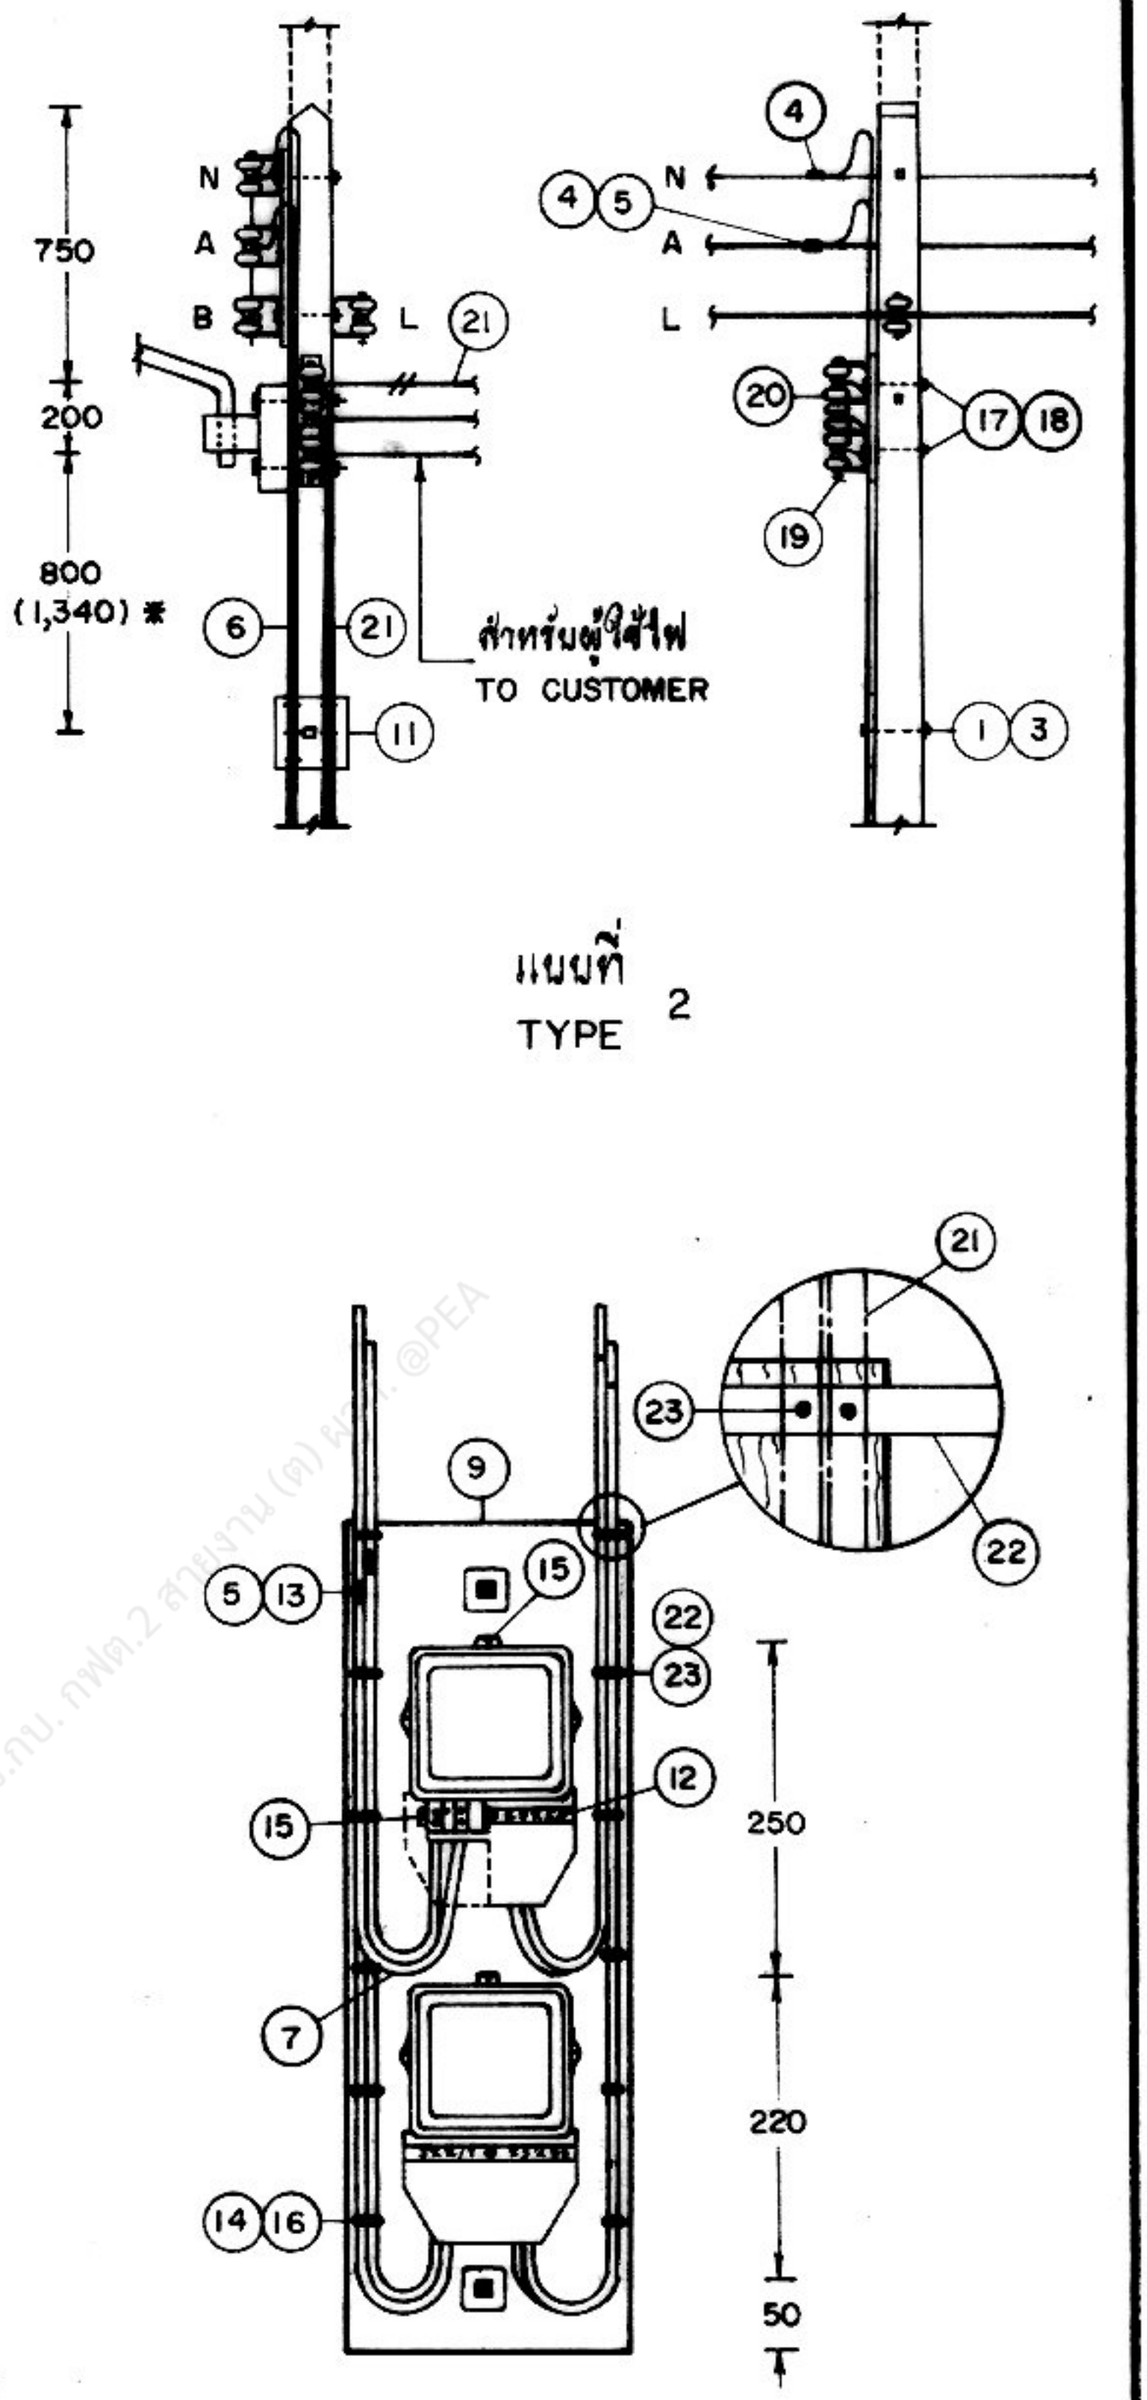

แบบที่ TYPE 2


รายละเอียด DETAIL B

* สำหรับเสาคอนกรีต 8 ม. รุ่นเก่า ที่เจาะรูตามแบบเลขที่ I40–021/130159
FOR OLD 8 m CONCRETE POLE ACCORDING TO DWG. NO. I40–021/130159


กองวิศวกรรมไฟฟ้าและเครื่องกล ฝ่ายวิศวกรรม	การไฟฟ้าส่วนภูมิภาค	ใช้แทนแบบ ถูกแทนโดยแบบ เสนอเสร็จวันที่ 20 มิ.ย. 23 แก้แบบวันที่ 8 ก.พ. 26 * มิติเป็น มม. มาตราส่วน 1 : 40
ผู้เขียน ผู้สำรวจ วิศวกร หัวหน้าแผนก หัวหน้ากอง ผู้อำนวยการฝ่าย	ผู้ว่าการ 13 พ.ย 2523 การติดตั้งมิเตอร์ 1 เฟส 220 โวลต์ ขนาด 3-5แอมป์ บนเสาคอนกรีต 8 ม. 2 จำนวน 2 เครื่อง	
รองผู้ว่าการฝ่ายเทคนิค	3-5 A, 1-Ø, 220 V METER INSTALLATION ON 8 m CONCRETE POLE 2 2 UNITS	แบบเลขที่ SAI-015/23071 แผ่นที่ 2 ของจำนวน 6 แผ่น

10 พ.ย. 2523

การประกอบเลขที่ 0524
ASSEMBLY NO.

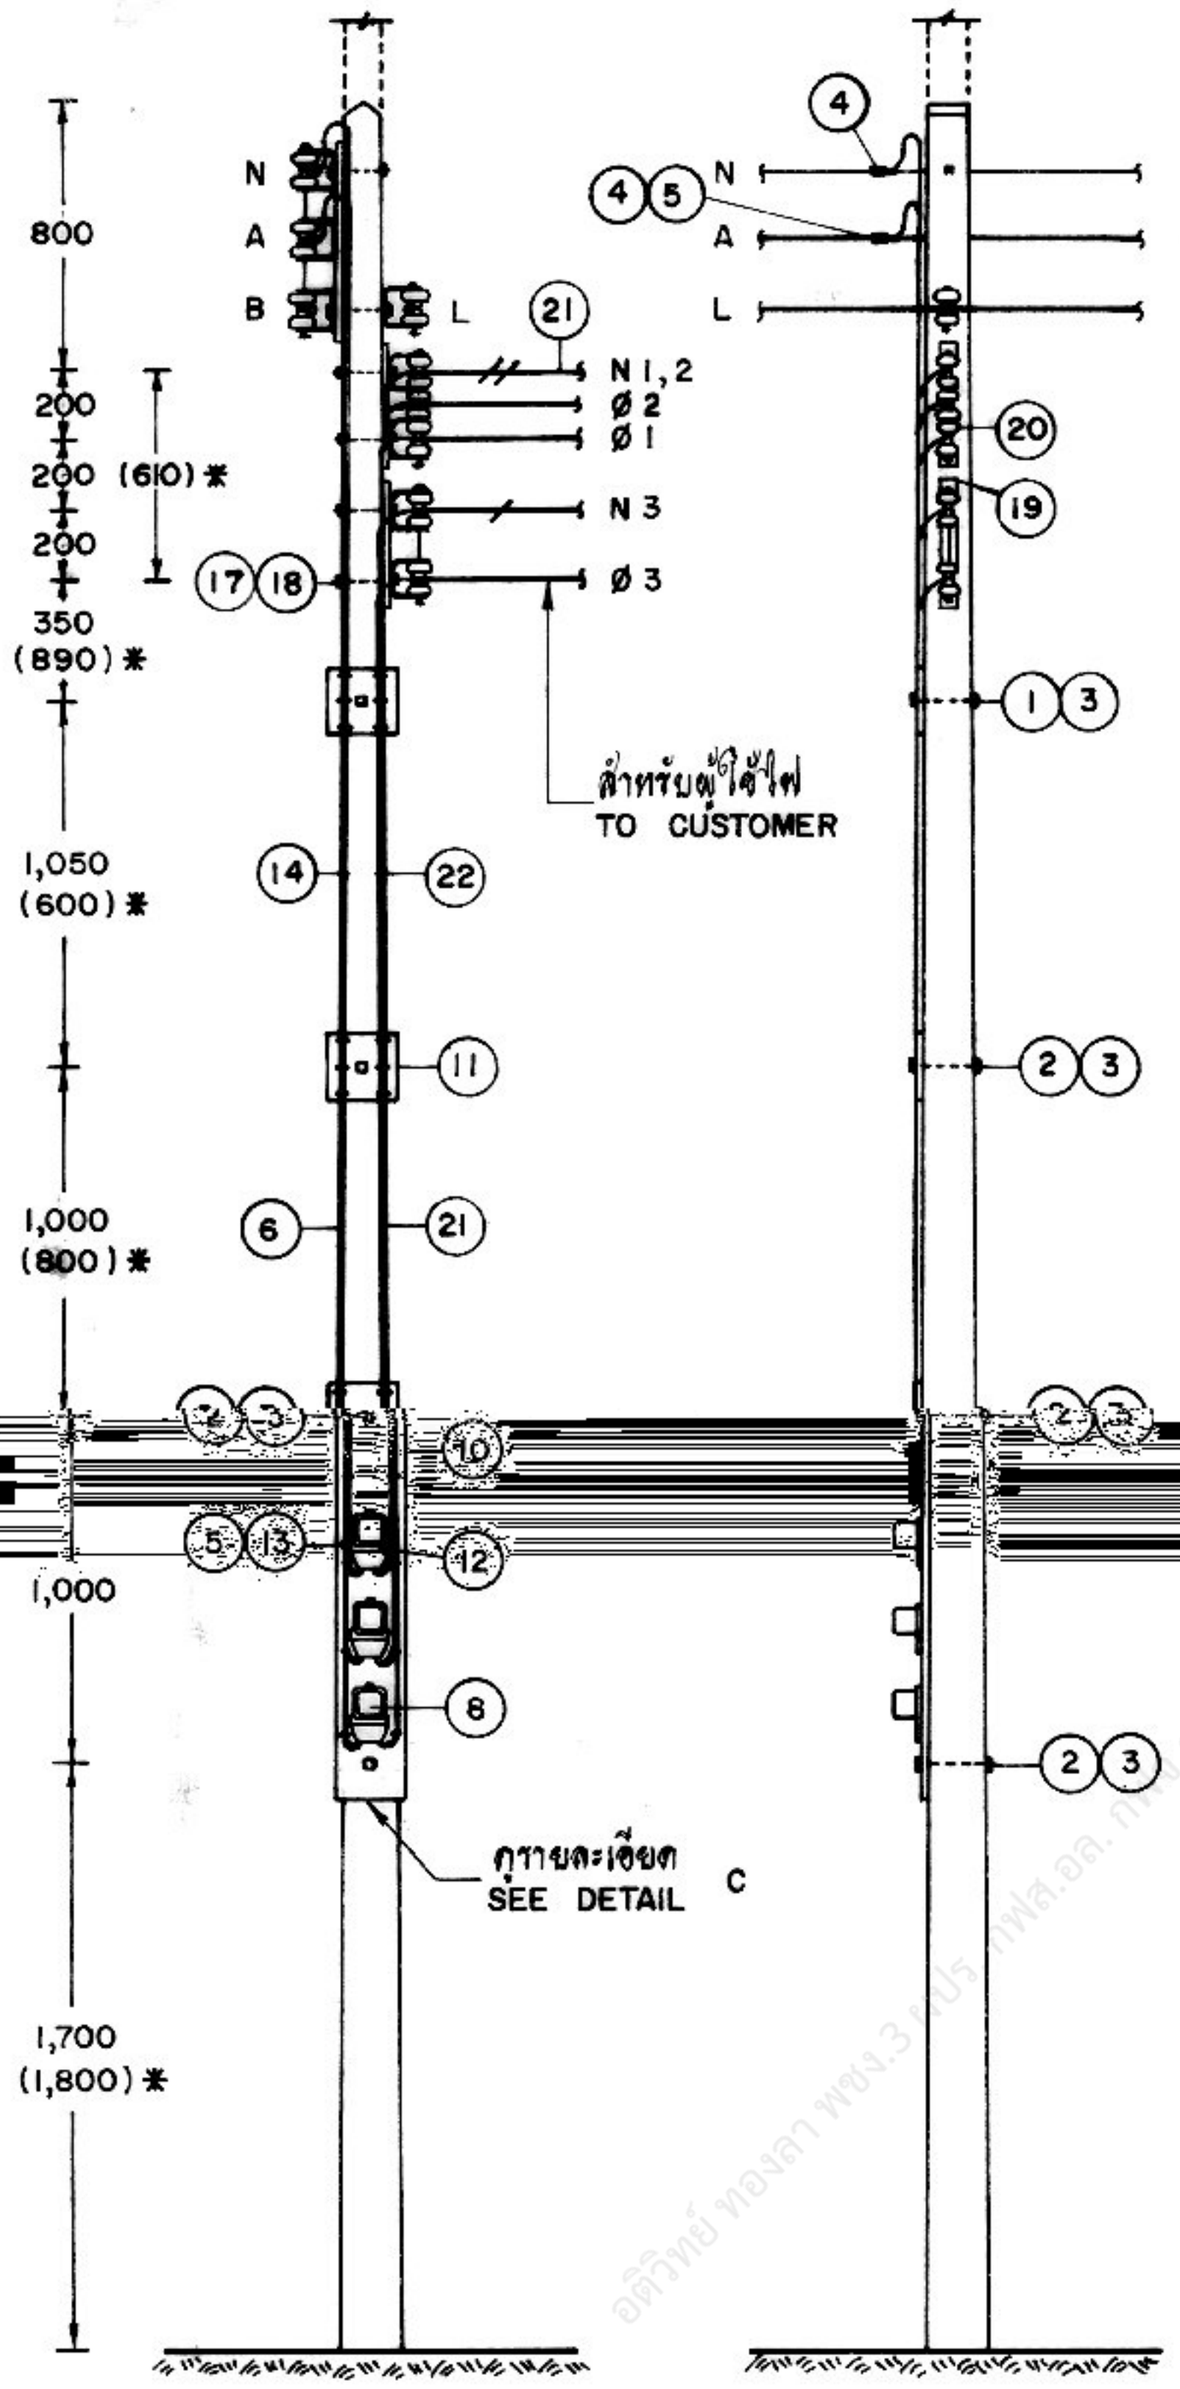

แบบที่ 1
TYPE

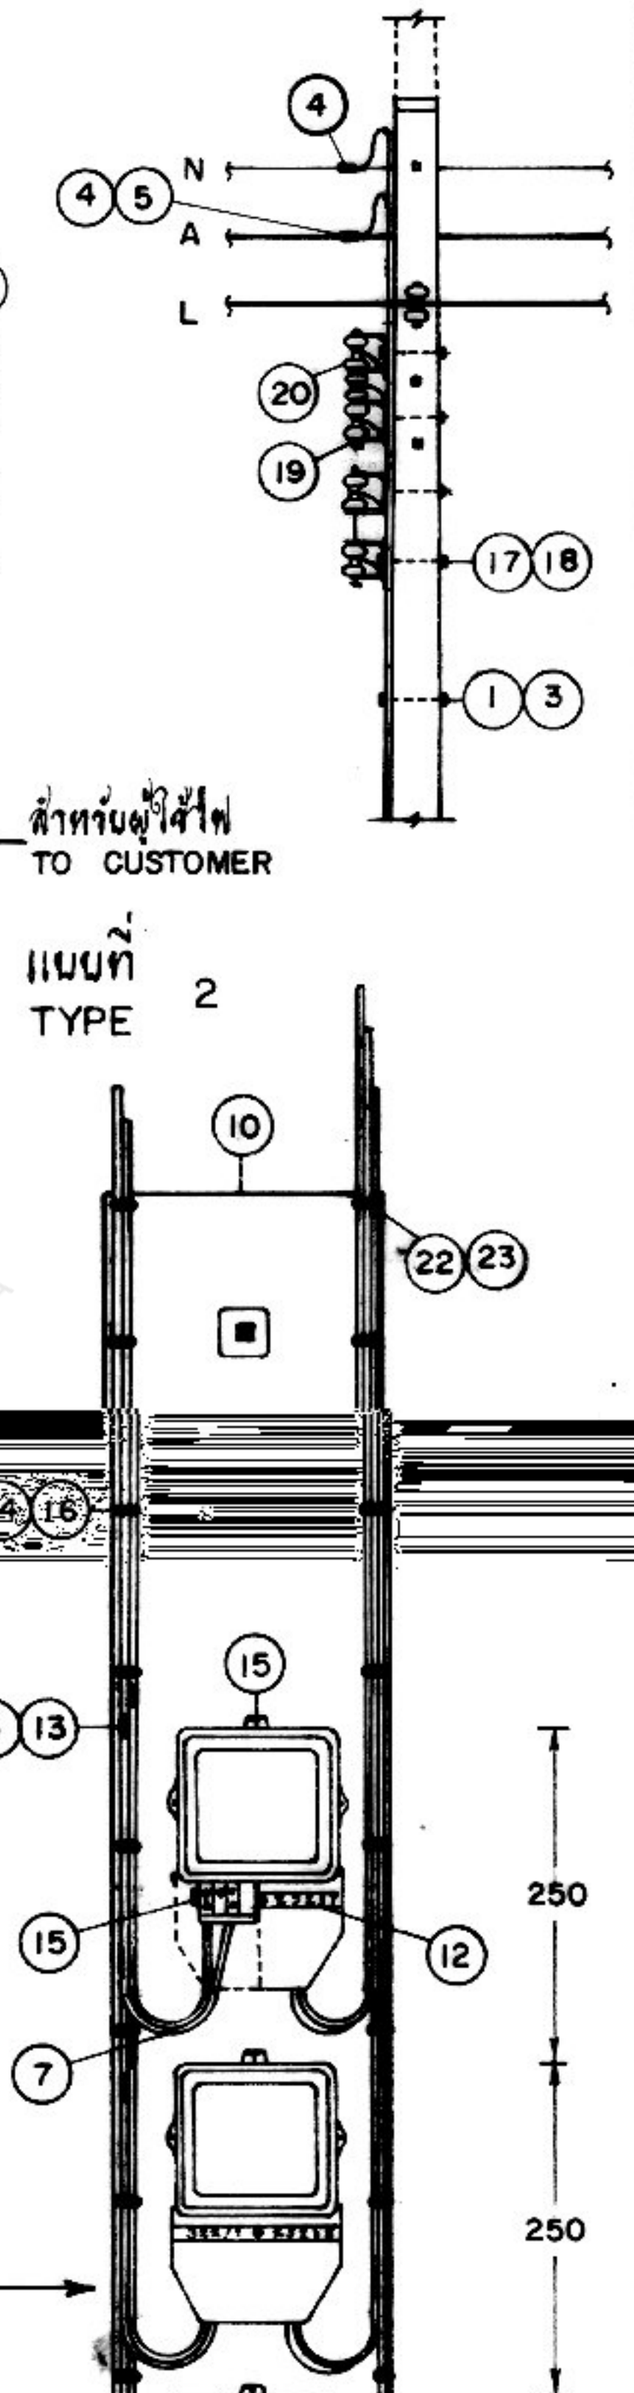


แบบที่ 2
TYPE

รายละเอียด C
DETAIL


* สำหรับเสาคอนกรีต 8 ม. รุ่นเก่าที่เจาะรูตามแบบเลขที่ 140–021/130159
FOR OLD 8 m CONCRETE POLE ACCORDING TO DWG. NO. 140–021/130159


กองวิศวกรรมไฟฟ้าและเครื่องกล ฝ่ายวิศวกรรม	การไฟฟ้าส่วนภูมิภาค	ใช้แทนแบบ ถูกแทนโดยแบบ เขียนเสร็จวันที่ 20 มิ.ย. 23 แก้แบบวันที่ 8 ก.ค. 26 * มิติเป็น มม. มาตราส่วน 1 : 40
ผู้เขียน ผู้สำรวจ วิศวกร หัวหน้าแผนก หัวหน้ากอง ผู้อำนวยการฝ่าย	ผู้ว่าการ 13 พ.ย. 2522 การติดตั้งมิเตอร์ 1 เฟส 220 โวลต์ ขนาด 3-5 แอมป์ บนเสาคอนกรีต 8 ม. 3 จำนวน 3 เครื่อง	
รองผู้ว่าการฝ่ายเทคนิค 10 พ.ย. 2523	3-5 A, 1-Ø, 220 V METER INSTALLATION ON 8 m CONCRETE POLE 3 3 UNITS	แบบเลขที่ SAI-015/23071 แผ่นที่ 3 ของจำนวน 6 แผ่น


การประกอบเลขที่ 0524
ASSEMBLY NO.

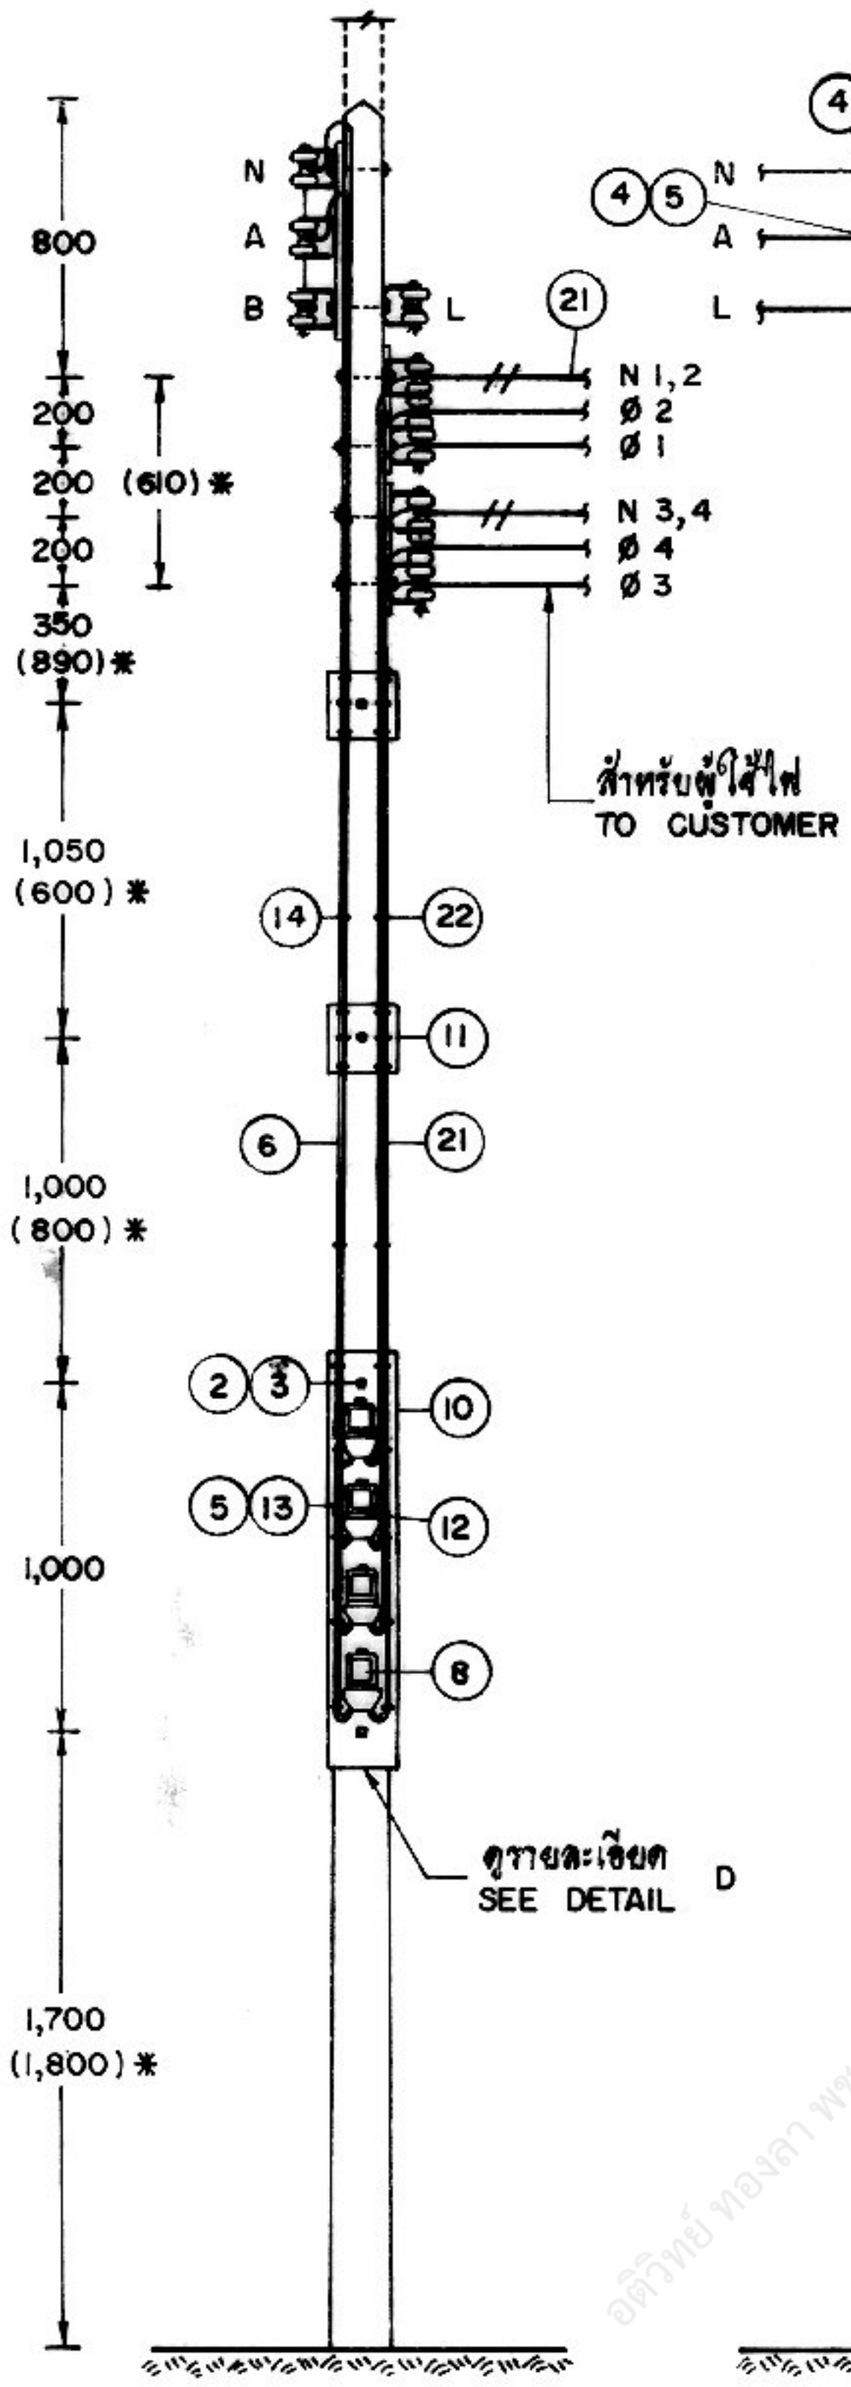

แบบที่ 1
TYPE 1

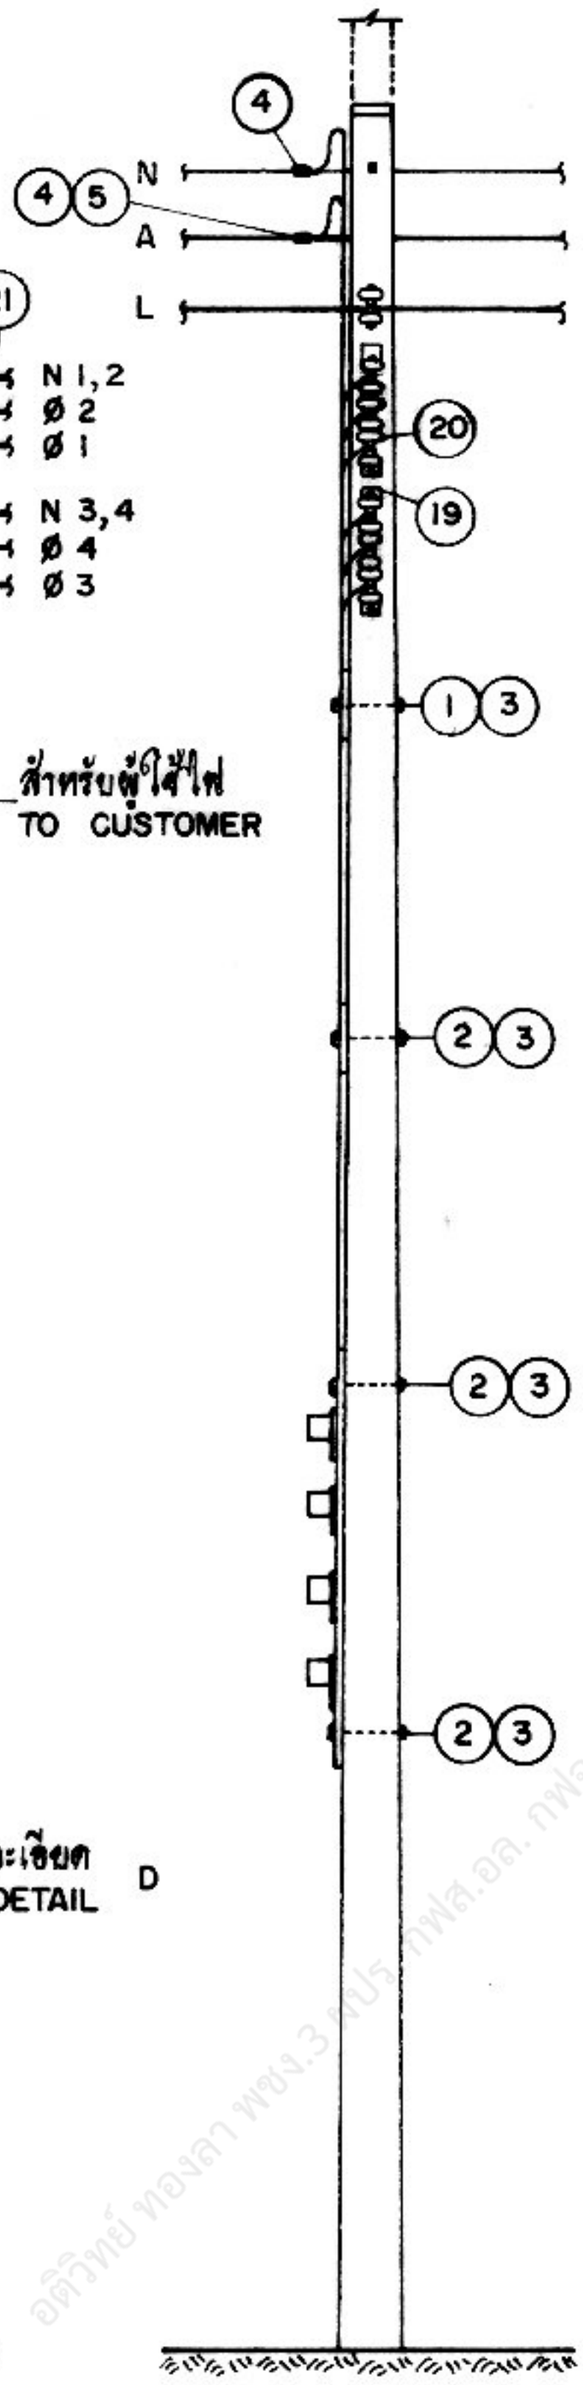

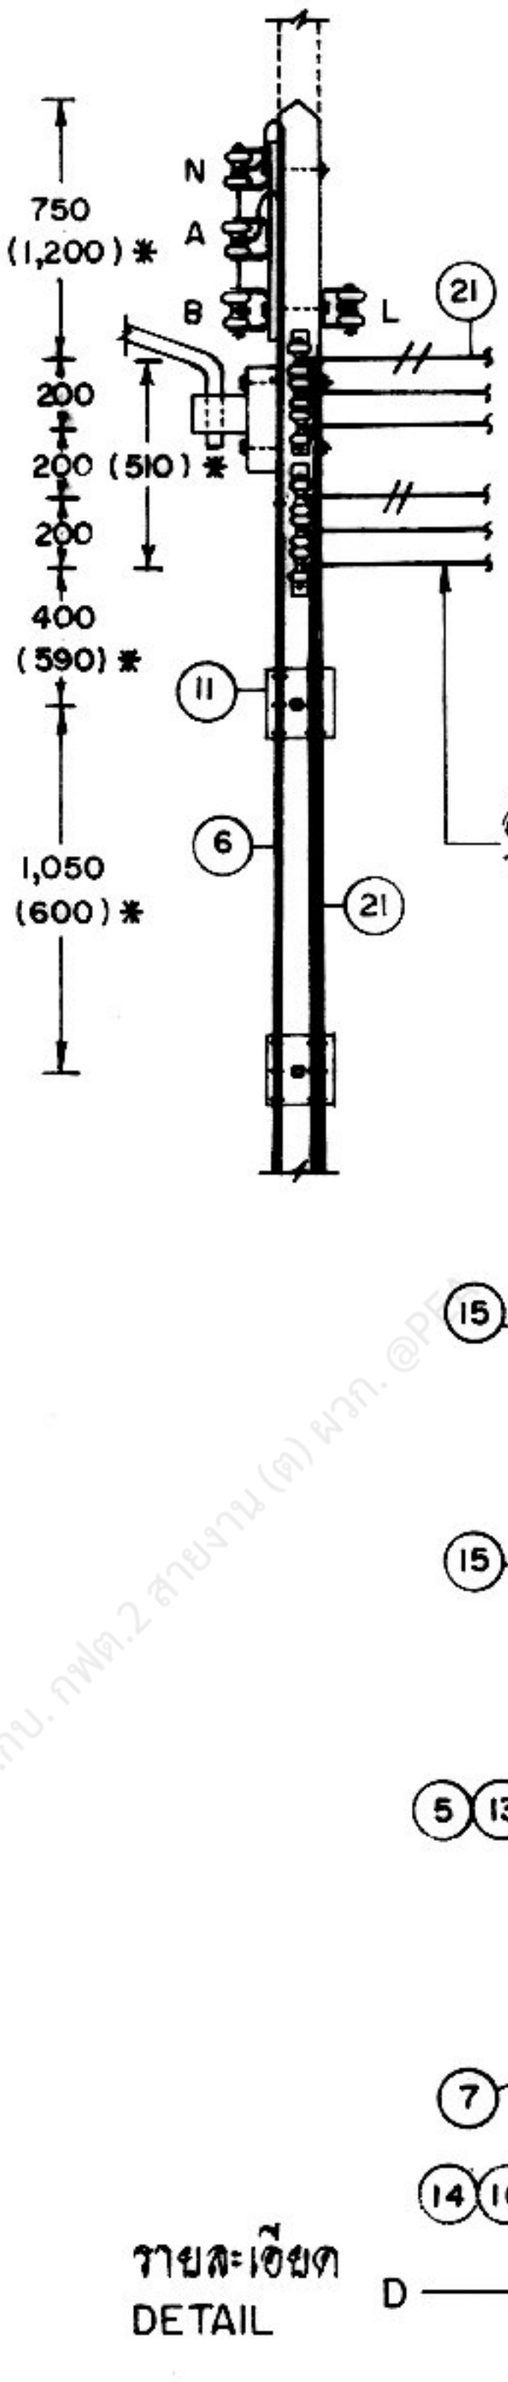

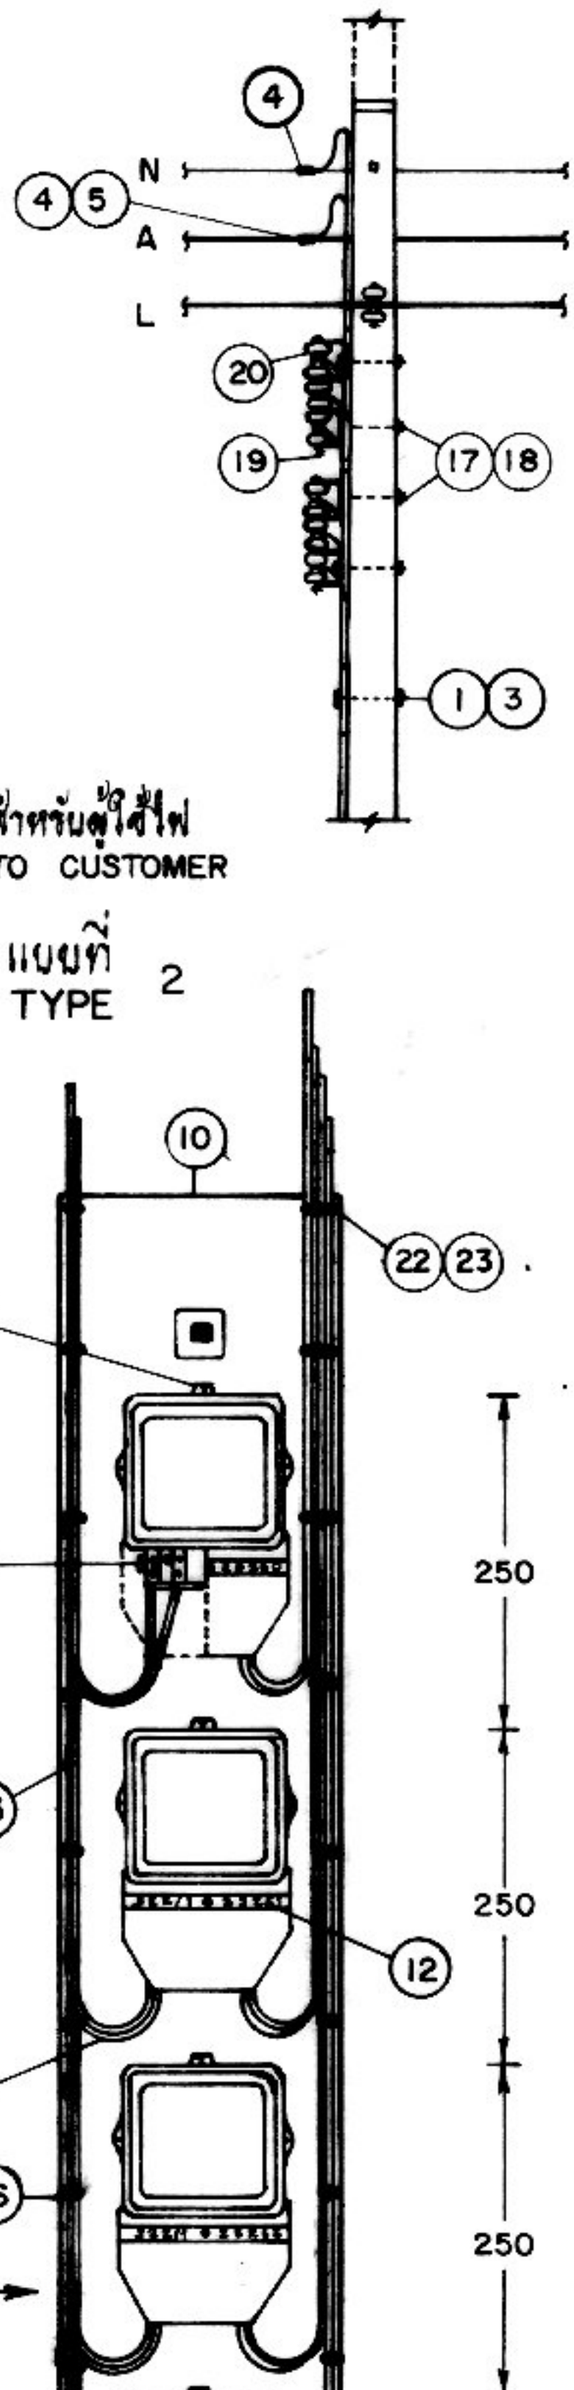

แบบที่ 2
TYPE 2

* สำหรับเสาคอนกรีต 8 ม. รุ่นเก่า ที่เจาะรูตามแบบเลขที่ 140-021/130159
FOR OLD 8 m CONCRETE POLE ACCORDING TO DWG. NO. 140-021/130159

กองวิศวกรรมไฟฟ้าและเครื่องกล ฝ่ายวิศวกรรม	การไฟฟ้าส่วนภูมิภาค	ใช้แทนแบบ ถูกแทนโดยแบบ
ผู้เขียน ผู้สำรวจ วิศวกร หัวหน้าแผนก หัวหน้ากอง ผู้อำนวยการฝ่าย	ผู้ว่าการ 13 พ.ย. 2523 การติดตั้งมิเตอร์ 1 เฟส 220 โวล์ต ขนาด 3-5 แอมป์ บนเสาคอนกรีต 8 ม. 4 จำนวน 4 เครื่อง	เขียนเสร็จวันที่ 20 มิ.ย. 23 แก้แบบวันที่ 8 ก.ย. 26 * มิติเป็น มม. มาตราส่วน 1 : 40
รองผู้ว่าการฝ่ายเทคนิค 10 พ.ย. 2523	3-5 A, 1-Ø, 220 V METER INSTALLATION ON 8 m CONCRETE POLE 4 4 UNITS	แผนเลขที่ SAI-015/23071 แผ่นที่ 4 จองจำนวน 6 แผ่น

การประกอบเลขที่ ASSEMBLY NO. 0524

บัญชีวัสดุในส่วนที่ กฟภ. ลงทุน
BILL OF MATERIAL FOR PEA.

ลำดับที่ ITEM	รายละเอียด DESCRIPTION	จำนวน REQ'D 1	2	3	4	วัสดุเลขที่ MAT. NO.
1	สลักเกลียว M 16 X 200 มม. BOLT, MACHINE, M 16 X 200 mm	1	1	1	1	01110202
	สลักเกลียว M 16 X 250 มม. สำหรับเสาคอนกรีต 12 ม. BOLT, MACHINE, M 16 X 250 mm, FOR 12 m CONCRETE POLE	1	1	1	1	01110203
2	สลักเกลียว M 16 X 250 มม. BOLT, MACHINE, M 16 X 250 mm	3	3	3	3	01110203
	สลักเกลียว M 16 X 300 มม. สำหรับเสาคอนกรีต 12 ม. BOLT, MACHINE, M 16 X 300 mm, FOR 12 m CONCRETE POLE	3	3	3	3	01110204
3	แหวนสี่เหลี่ยมแบน 52 X 52 X 4.5 มม. รู Ø 18 มม. มอก. 258 WASHER, SQUARE, FLAT, 52 X 52 X 4.5 mm, HOLE Ø 18 mm TIS 258	8	8	8	8	01180100
4	พี.จี. คอนเนคเตอร์ หรือคอนเนคเตอร์ชนิดบีบ สำหรับสายอะลูมิเนียม ขนาด 16-70 ต.มม. CONNECTOR, PARALLEL GROOVE, OR COMPRESSION TYPE, Al 16-70 mm²	2	2	2	2	02300101 or 02210001-2
5	PVC เทป กว้าง 19 มม. (ใช้ความยาว 2 ม. ต่อ 1 จุด) มอก. 386 PVC TAPE, 19 mm WIDE (2 m LONG PER POINT) TIS 386	5 N.m.	7 N.m.	9 N.m.	11 N.m.	02180001 or 02180002
6	สายอะลูมิเนียมหุ้มฉนวนเข้ามิเตอร์แรงต่ำ 0.6/1 kV 16 ต.มม. CONDUCTOR, NAYY OR NAY, Al 0.6/1 kV, 16 mm²	11 N.m.	11 N.m.	11 N.m.	11 N.m.	02070101
7	สายอะลูมิเนียมหุ้มฉนวนเข้ามิเตอร์แรงต่ำ 0.6/1 kV 10 ต.มม. CONDUCTOR, NAYY OR NAY, Al 0.6/1 kV, 10 mm²	-	0.8 N.m.	1.6 N.m.	2.4 N.m.	02070100
8	วัตต์อาวร์มิเตอร์ 1 เฟส 2 สาย 220 โวลต์ ใช้ภายนอก METER, WATTHOUR, SINGLE-PHASE, 2 WIRE 220 V, WEATHER PROOF	1	2	3	4	06000000-1
9	แป้นไม้รองรับมิเตอร์ไส่แล้ว ขนาด 60 X 20 X 2 ซม. METER PLATE, HARD WOOD, SURFACE FINISHED, 60 X 20 X 2 cm	1	1	-	-	—
10	แป้นไม้รองรับมิเตอร์ไส่แล้ว ขนาด 120 X 20 X 2 ซม. METER PLATE, HARD WOOD, SURFACE FINISHED, 120 X 20 X 2 cm	-	-	1	1	—
11	แป้นไม้สำหรับยึดสายเข้า และออกจากมิเตอร์ ไส่แล้ว ขนาด 20 X 20 X 2 ซม. CABLE PLATE, HARD WOOD, SURFACE FINISHED, 20 X 20 X 2 cm	2	2	2	2	—
12	หมายเลขผู้ใช้ไฟ (ดูตัวอย่างข้างล่าง) NUMBER OF CUSTOMER	1	2	3	4	—
13	พี.จี. คอนเนคเตอร์สลักเดียว หรือคอนเนคเตอร์ชนิดบีบ สำหรับสายอะลูมิเนียม ขนาด 10-16 ต.มม. CONNECTOR, PARALLEL GROOVE, SINGLE BOLT, OR COMPRESSION TYPE, Al MAIN 16 mm² TAP OFF 10 mm²	-	2	4	6	02300201 or 02320000
14	เข็มขัดรัดสาย (ทำด้วยลวดอะลูมิเนียมแบน 1 X 10 มม.) ช่วงระยะ 50 ซม. CABLE STRAP (MADE OF ARMOUR TAPE 1 X 10 mm) AT 50 cm INTERVALS	2 N.m.	2 N.m.	3 N.m.	3 N.m.	02200000
15	ตะปูเกลียวชุบโครเมียม ขนาด 15-20 มม. SCREW, CHROME PLATED, SIZE 15-20 mm	3	6	9	12	
16	ตะปูหัวกลมแบน ยาว 15-20 มม. Ø 1 มม. มอก. 113 NAIL, ROUND, MILD STEEL WIRE 15-20 mm LONG Ø 1 mm TIS 113	24	24	40	40	

ตัวอย่างหมายเลขผู้ใช้ไฟ

แผ่นอะลูมิเนียม ขนาด 15 X 100 มม. หนา 0.5 มม.

รู Ø 3.5 มม.

322/1 • 25241

ใช้ที่ตอกตัวเลข ขนาดความสูง 10 มม. ตอก แล้วทาด้วยสีดำ ตามรอยตัวเลข

กองวิศวกรรมไฟฟ้าและเครื่องกล ฝ่ายวิศวกรรม	**การไฟฟ้าส่วนภูมิภาค**	ใช้แทนแบบ ถูกแทนโดยแบบ
ผู้เขียน ผู้สำรวจ วิศวกร หัวหน้าแผนก หัวหน้ากอง ผู้อำนวยการฝ่าย	ผู้ว่าการ 13 พ.ย. 2523	เขียนเสร็จวันที่ 20 มิ.ย. 23 แก้แบบวันที่ 8 ก.ย. 26 มิติเป็น มาตราส่วน
รองผู้ว่าการฝ่ายเทคนิค 10 พ.ย. 2523	การติดตั้งมิเตอร์ 1 เฟส 220 โวลต์ ขนาด 3-5 แอมป์ บนเสาคอนกรีต 8 ม. 3-5 A, 1-Ø, 220 V METER INSTALLATION ON 8 m CONCRETE POLE	แบบเลขที่ SAI-015/23071 แผ่นที่ 5 ของจำนวน 6 แผ่น

การประกอบเลขที่ ASSEMBLY NO. 0524

บัญชีวัสดุในส่วนของผู้ใช้ไฟ
BILL OF MATERIAL FOR CUSTOMER

ลำดับที่ ITEM	รายละเอียด DESCRIPTION	จำนวน REQ'D 1	2	3	4	วัสดุเลขที่ MAT. NO.
17	สลักเกลียว M 16 X 200 มม. BOLT, MACHINE, M 16 X 200 mm	2	2	4	4	01110202
	สลักเกลียว M 16 X 250 มม. สำหรับเสาคอนกรีต 12 ม. BOLT, MACHINE, M 16 X 250 mm, FOR 12 m CONCRETE POLE	2	2	4	4	01110203
18	แหวนสี่เหลี่ยมแบน 52 X 52 X 4.5 มม. รู Ø 18 มม. มอก. 258 WASHER, SQUARE, FLAT, 52 X 52 X 4.5 mm, HOLE Ø 18 mm TIS 258	2	2	4	4	01180100
19	แร็ค 2 X 200 มม. แบบหลังยื่น RACK, SECONDARY, MEDIUM PRESSED STEEL, 2 X 200 mm, EXTENDED RACK	1	1	2	2	03130000
20	ลูกถ้วยแรงต่ำ มอก.227 แบบ ข (แบบ 53-2) INSULATOR, SPOOL TYPE, L.T. TIS 227 TYPE B (CLASS 53-2)	2	3	5	6	03030000
21	สายอะลูมิเนียม หรือสายทองแดงหุ้มฉนวน PVC 750 โวลต์ 75°ซ. CABLE, Al OR Cu, PVC - INSULATED, 750 V, 75°C					02070100
22	เข็มขัดรัดสาย (ทำด้วยเทปอะลูมิเนียมแบน 1 X 10 มม.) ช่วงระยะ 50 ซม. CABLE STRAP (MADE OF ARMOUR TAPE 1 X 10 mm) AT 50 cm INTERVALS	3 น.ม.	3 น.ม.	6 น.ม.	6 น.ม.	02200000
23	ตะปูหัวกลมแบน ยาว 15-20 มม. Ø 1 มม. มอก. 113 NAIL, ROUND MILD STEEL WIRE 15-20 mm LONG Ø 1 mm TIS 113	24	24	40	40	

<u>ข้อแนะนำในการติดตั้งแร็คแรงต่ำรับสายหลังมิเตอร์</u>

1. ในกรณีที่ติดตั้งมิเตอร์ใหม่ จำนวน 3 หรือ 4 เครื่องในคราวเดียวกัน สามารถพิจารณาใช้แร็ค 4 X 200 มม. (วัสดุเลขที่ 0467) แทนแร็ค 2 X 200 มม. วัสดุลำดับที่ 19 ได้ โดยลดจำนวนสลักเกลียววัสดุลำดับที่ 17 ลงเหลือ 2 ชุด และลดจำนวนแหวนสี่เหลี่ยมวัสดุลำดับที่ 18 ลงเหลือ 2 อัน
2. ในกรณีที่ติดตั้งมิเตอร์ จำนวน 3 หรือ 4 เครื่อง บนเสาคอนกรีต 8 ม. รุ่นเก่าที่เจาะรูตามแบบเลขที่ 140-021/130159 ให้ติดตั้งแร็ค 4 X 200 มม. รับสายหลังมิเตอร์แทนแร็ค 2 X 200 มม. วัสดุลำดับที่ 19 โดยลดจำนวนวัสดุอุปกรณ์เช่นเดียวกับข้อ 1

<u>ข้อแนะนำในการจัดทำเข็มขัดรัดสายอะลูมิเนียมแบน 1 X 10 มม.</u>

— ถ้าเป็นสายเข้ามิเตอร์ ขนาด 3-5 แอมป์ จำนวน 1-4 เครื่อง ใช้สมอะลูมิเนียมแบน 1 X 10 มม. ยาว 10 ซม. ต่อหนึ่งจุด
— ถ้าเป็นสายออกจากมิเตอร์ จำนวน 1-2 เครื่อง ——"—— ยาว 15 ซม. ——"——
— ถ้าเป็นสายออกจากมิเตอร์ จำนวน 3-4 เครื่อง ——"—— ยาว 20 ซม. ——"——

<u>หมายเหตุ</u>

1. แบบนี้เหมาะสมสำหรับก่อสร้างในบริเวณเมือง หรือย่านชุมชน
2. การเข้าปลายสายอะลูมิเนียมหุ้ม PVC สีฟ้า และสายทองแดงหุ้มฉนวน ดูแบบเลขที่ SAI-015/21006 และ SAI-015/21005

<u>NOTES</u>

1. THIS CONSTRUCTION DRAWING IS SUITABLE FOR URBAN ARBA.
2. SKY BLUE PVC. INSULATED ALUMINIUM CONDUCTOR AND INSULATED COPPER CONDUCTOR DEAD-ENDING SEE DWG. NO. SAI-015/21006 AND SAI-015/21005 .

กองวิศวกรรมไฟฟ้าและเครื่องกล ฝ่ายวิศวกรรม	การไฟฟ้าส่วนภูมิภาค	ใช้แทนแบบ ถูกแทนโดยแบบ เขียนเสร็จวันที่ 20 มิ.ย. 23 แก้แบบวันที่ 8 ก.ย. 26 มิติเป็น มาตราส่วน
ผู้เขียน ผู้สำรวจ วิศวกร หัวหน้าแผนก หัวหน้ากอง ผู้อำนวยการฝ่าย	ผู้ว่าการ 13 พ.ย. 2523 การติดตั้งมิเตอร์ 1 เฟส 220 โวลต์ ขนาด 3-5 แอมป์ บนเสาคอนกรีต 8 ม.	
รองผู้ว่าการฝ่ายเทคนิค 10 พ.ย. 2523	3-5 A, 1-Ø, 220 V METER INSTALLATION ON 8 m CONCRETE POLE	แบบเลขที่ SAI-015/23071 แผ่นที่ 6 ของจำนวน 6 แผ่น