การประกอบเลขที่
ASSEMBLY NO. 5202

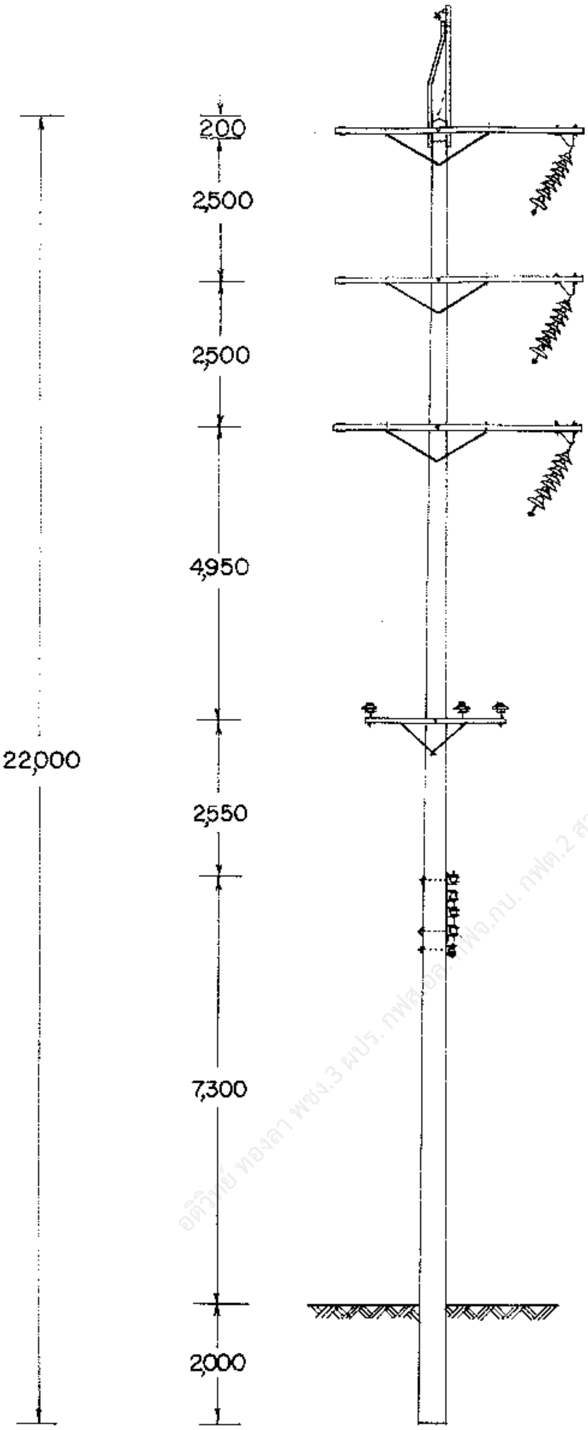

แบบ
TYPE SS-SA-1

อดิวิทย์ ทองลา พชง.3 ผปร. กฟส.อล. กฟจ.กบ. กฟต.2 สายงาน (ต) ผวก. @PEA

JAPANESE EXPERT TO PEA. Y. Yamada

กองวิศวกรรม
ผู้เขียน
สถาปนิก
วิศวกร
หัวหน้าแผนก
ผู้อำนวยการกอง
รองผู้ว่าการฝ่ายเทคนิค

การไฟฟ้าส่วนภูมิภาค
ผู้ว่าการ 26 มี.ค. 19

แบบโครงสร้างสายส่งระบบ 115 kV
วงจรเดี่ยว
แบบเสาสำหรับทางโค้ง

115 kV LINE STRUCTURE CONSTRUCTION
SINGLE CIRCUIT
SMALL ANGLE STRUCTURE

ใช้แทนแบบ
ถูกแทนโดยแบบ
เขียนเสร็จวันที่ 17 มี.ค. 19
แก้แบบเมื่อวันที่ 24 [illegible] 23
มิติเป็น [illegible]
มาตราส่วน [illegible]25
แบบเลขที่ S[illegible]015/19021
แผ่นที่ 1 ของจำนวน 3 แผ่น

สำเนา 33

การประกอบเลขที่
ASSEMBLY NO. 5202

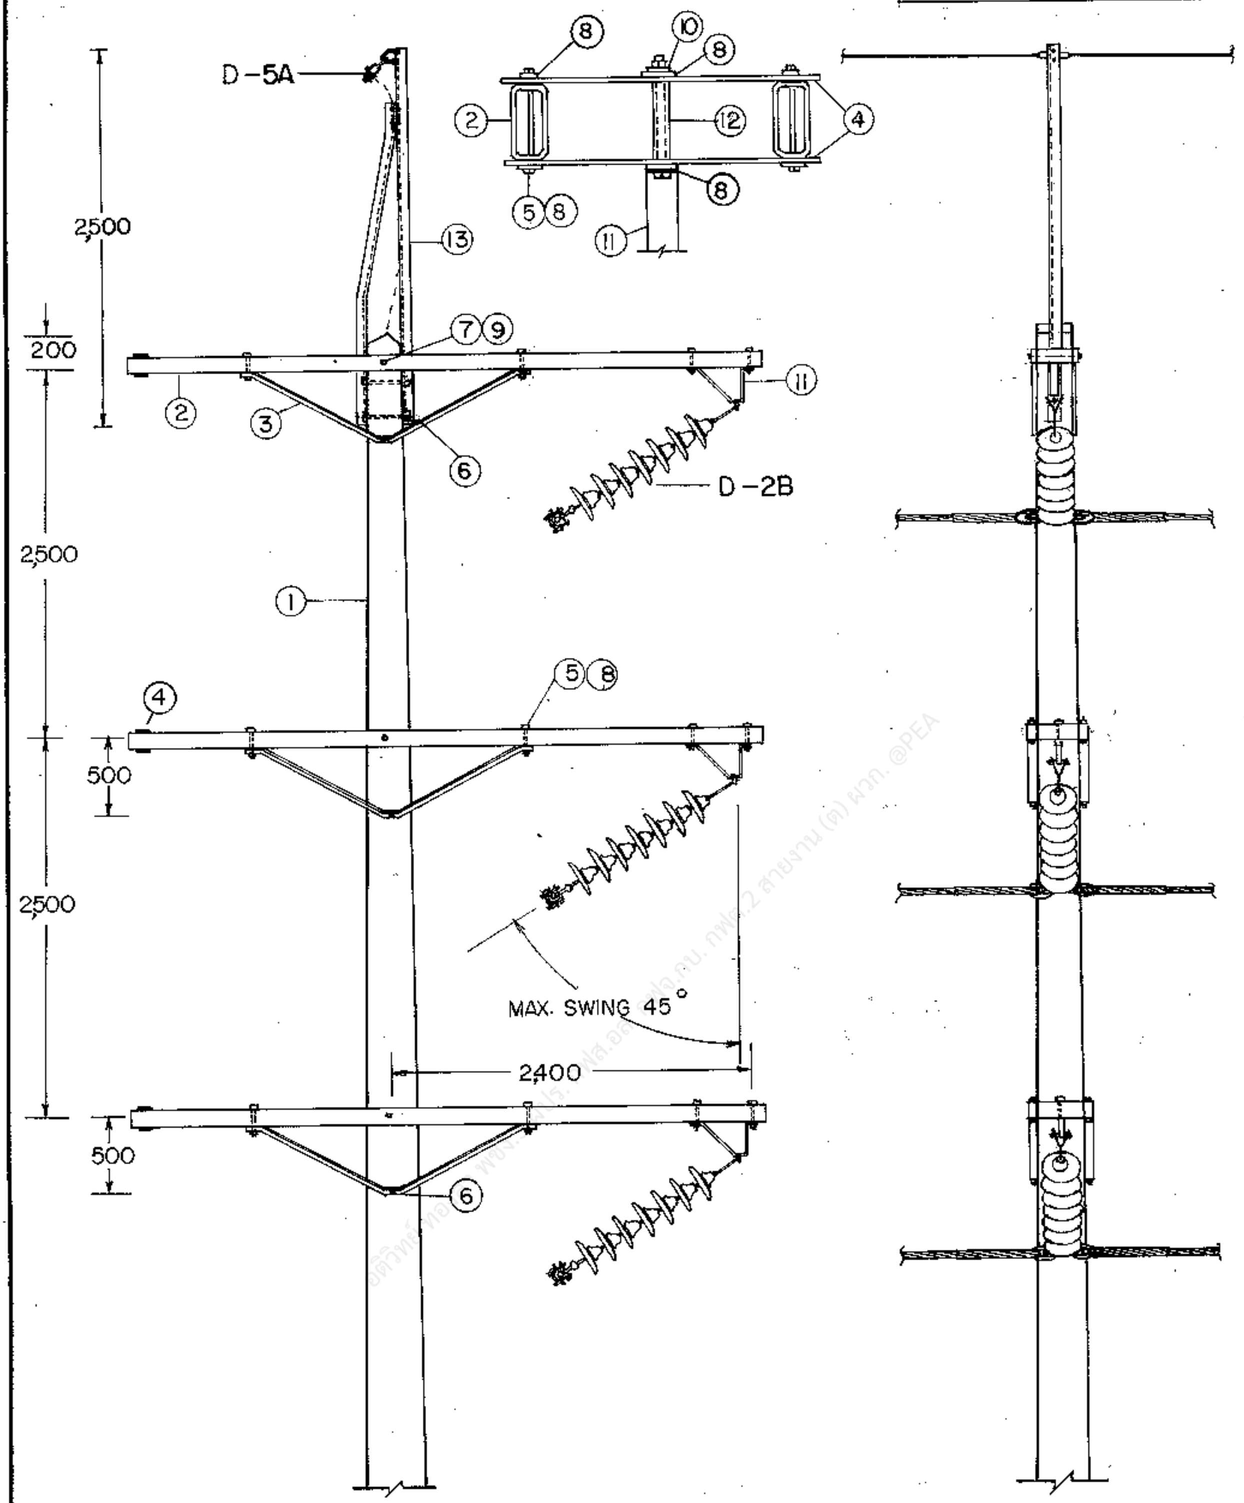
D-5A
⑧
⑩
⑧
②
⑫
④
⑤⑧
⑧
⑪
2,500
⑬
200
⑦⑨
②
③
⑪
⑥
D-2B
2,500
①
④
⑤⑧
500
2,500
MAX. SWING 45°
2400
500
⑥

JAPANESE EXPERT TO PEA.

กองวิศวกรรม

ผู้เขียน
สถาปนิก
วิศวกร
หัวหน้าแผนก
ผู้อำนวยการกอง

รองผู้ว่าการฝ่ายเทคนิค

การไฟฟ้าส่วนภูมิภาค

ผู้ว่าการ

แบบโครงสร้างเสาส่งระบบ 115 kV
วงจรเดียว
แบบเสาสำหรับทางโค้ง

115 kV LINE STRUCTURE CONSTRUCTION
SINGLE CIRCUIT
SMALL ANGLE STRUCTURE

ใช้แทนแบบ
ถูกแทนโดยแบบ
เขียนเสร็จวันที่ 17 มี.ค. 19
แก้แบบวันที่ 24 มี.ค. 23
มิติเป็น มม.
มาตราส่วน 1:50
แบบเลขที่ S02-015/19021
แผ่นที่ 2 ของจำนวน 3 แผ่น

การประกอบเลขที่
ASSEMBLY NO **5202**

บัญชีวัสดุ
BILL OF MATERIAL

ลำดับที่ ITEM	รายละเอียด DESCRIPTION	จำนวน REQ'D	วัสดุเลขที่ MAT. NO.
1	เสาคอนกรีต 22 ม. POLE, CONCRETE 22 m. LONG	1	00010011 (0041)
2	คอนสายแบบเหล็กขนาด 100x50x3.2 มม. ยาว 4.20 ม. CROSSARM, STEEL 100X50X3.2 mm 4.20 m LONG	6	00120001 (0116)
3	เหล็กฉากรับคอนสายขนาด 50 x 50 x 6 มม. ช่วงกว้าง 1800 มม. ดรอพ 450 มม. BRACE, ANGLE STEEL 50 x 50 x 6 mm 1800 mm WIDE 450 mm, DROP	6	00120007 (0119)
4	แผ่นเหล็กขนาด 6 x 100 x 450 มม. PLATE, STEEL 6 x 100 x 450 mm.	18	01030002 (0143)
5	สลักเกลียว M 16 x 170 มม. BOLT, MACHINE M 16 x 170 mm.	36	01110201 (0221)
6	สลักเกลียว M 16 x 350 มม. BOLT, MACHINE M 16 x 350 mm.	6	01110301 (0225)
7	สลักเกลียว M 20 x 450 มม. BOLT, MACHINE M 20 x 450 mm.	3	01110302 (0234)
8	แหวนสี่เหลี่ยมแบน 52X52X4.5 มม. รู Ø 18 มม. มอก. 258 WASHER, SQUARE, FLAT 52X52X4.5 mm. HOLE Ø 18 mm. TIS. 258	60	01180100 (0355)
9	แหวนสี่เหลี่ยมแบน 62 X 62 X 6 มม. รู Ø 22 มม. มอก. 258 WASHER, SQUARE, FLAT 62 X 62 X 6 mm. HOLE Ø 22 mm. TIS 258	6	01180101 (0356)
10	แหวนสปริง M 16 มอก. 259 WASHER, LOCK, M 16, TIS 259	6	01180301 (0365)
11	ที่แขวนลูกถ้วยทางโค้ง BRACKET, CORNER SUSPENSION	3	03140012 (0489)
12	ท่อเหล็กซือขนาด 20 มม. หนา 2.65 มม. ยาว 100 มม. มอก. 277 ประเภท 2 PIPE, IRON DIA. 20 mm ID, 2.65 mm THICKNESS, 100 mm LONG, TIS 277 TYPE 2	6	01050000 (0905)
13	เหล็กฉากรับสายล่อฟ้าทางโค้ง OVERHEAD GROUND WIRE CORNER BAYONET	1	01010005 (0136)
	รายละเอียด DETAIL		
D-2B	การประกอบลูกถ้วยแขวน SUSPENSION INSULATOR ASSEMBLY	3	
D-5A	การต่อสายล่อฟ้า OVERHEAD GROUND WIRE CONNECTION	1	
D-10A	ฐานรากเสา POLE FOUNDATION	1	

JAPANESE EXPERT TO PEA. Y. Yamada

กองวิศวกรรม

การไฟฟ้าส่วนภูมิภาค

ผู้เขียน
สถาปนิก
วิศวกร
หัวหน้าแผนก
ผู้อำนวยการกอง 15
รองผู้ว่าการฝ่ายเทคนิค

ผู้ว่าการ 26 มี.ค. 19

แบบโครงสร้างเสาส่งระบบ 115 kV
วงจรเดี่ยว
แบบเสาสำหรับทางโค้ง

115 kV LINE STRUCTURE CONSTRUCTION
SINGLE CIRCUIT
SMALL ANGLE STRUCTURE

ใช้แทนแบบ
ถูกแทนโดยแบบ
เขียนเสร็จวันที่ 17 มี.ค. 19
แก้แบบวันที่ 24 มี.ค. 23
มิติเป็น
มาตราส่วน
แบบเลขที่ S02–015/1902
แผ่นที่ 3 ของจำนวน 3 แผ่น