
การประกอบลงที่ ASSEMBLY NO. **5267**

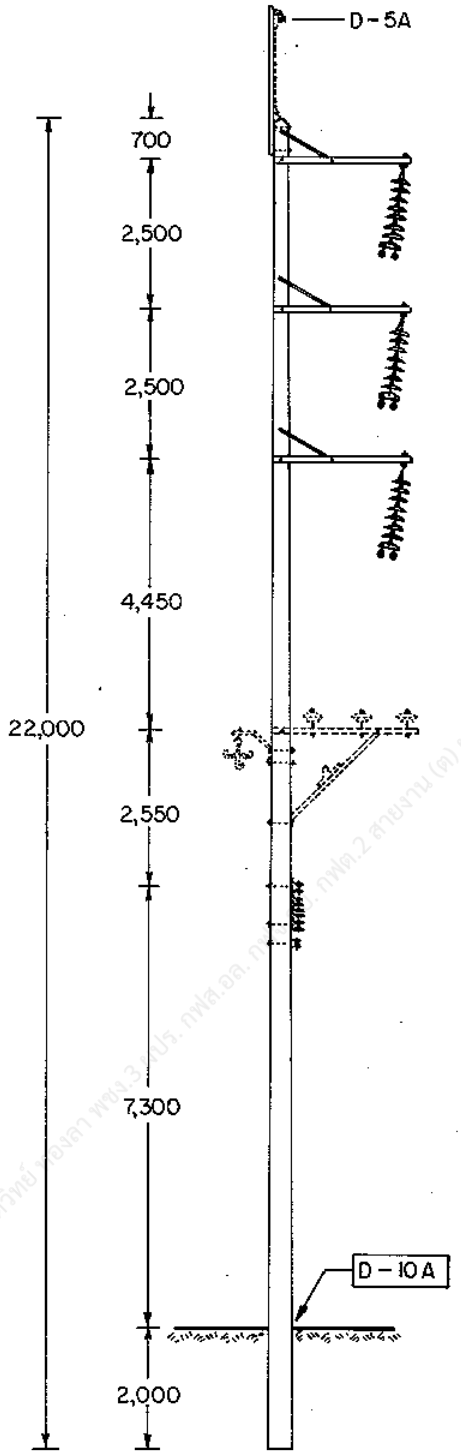

กองวิศวกรรมไฟฟ้าและเครื่องกล
ฝ่ายวิศวกรรม

ผู้เขียน
ผู้สำรวจ
วิศวกร
หัวหน้าแผนก
ผู้อำนวยการกอง
ผู้อำนวยการฝ่าย

รองผู้ว่าการฝ่ายเทคนิค

การไฟฟ้าส่วนภูมิภาค

ผู้ว่าการ


115 kV วงจรเดียว สายไฟฟ้าคู่
เสาต้นทางตรงก่อนเสาต้นเข้าปลายสาย
แบบ SD - TG - 4

115 kV SINGLE-CIRCUIT DOUBLE-CONDUCTOR
TANGENT STRUCTURE, ADJACENT TO DEADEND POLE
TYPE SD - TG - 4


ใช้แทนแบบ
ถูกแทนโดยแบบ
เขียนเสร็จวันที่ 3 ก.ย. 35
แก้แบบวันที่ 27 ก.ค. 38
มิติเป็น มิลลิเมตร
มาตราส่วน 1 : 125

แบบเลขที่ SAI-015/35004
แผ่นที่ 1 รวมจำนวน 3 แผ่น

การประกอบเลขที่ ASSEMBLY NO. 5267

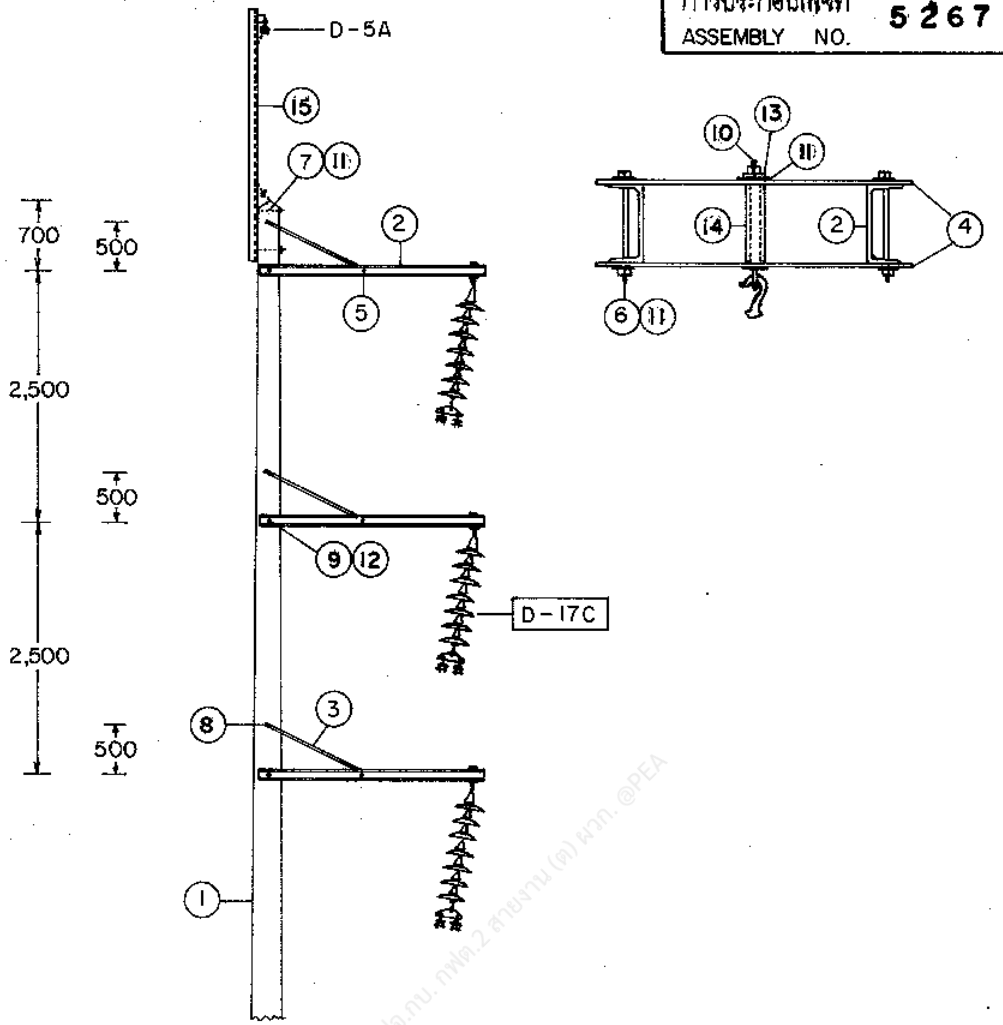

SD—TG—4

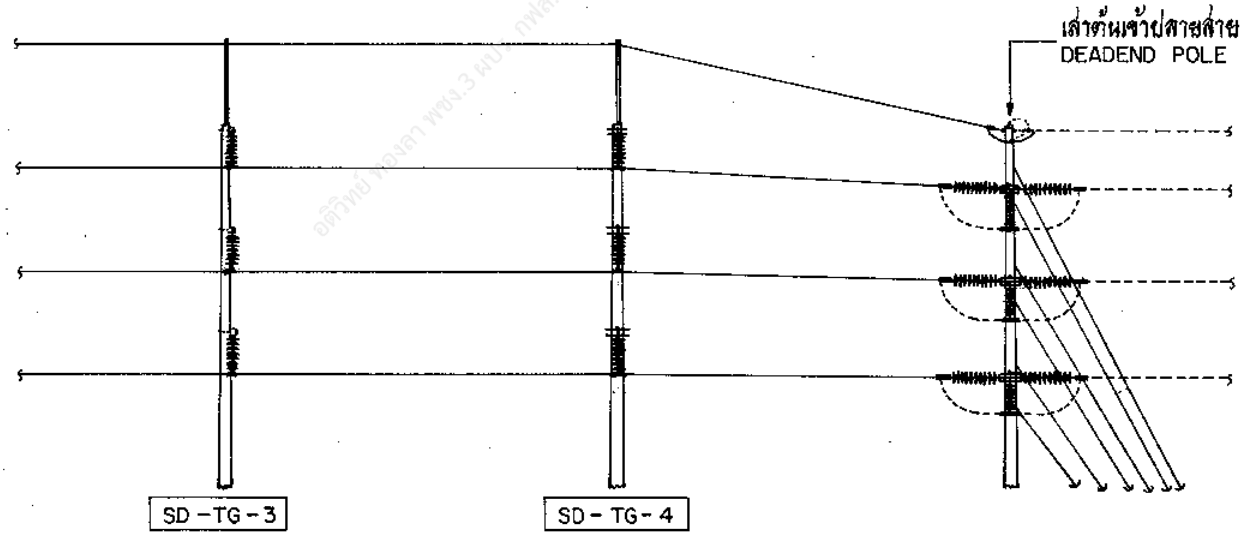

กองวิศวกรรมไฟฟ้าและเครื่องกล ฝ่ายวิศวกรรม	การไฟฟ้าส่วนภูมิภาค	ใช้แทนแบบ
ผู้เขียน ผู้สำรวจ วิศวกร หัวหน้าแผนก ผู้อำนวยการกอง ผู้อำนวยการฝ่าย	ผู้ว่าการ 27 ก.พ. 35 115 kV วงจรเดียว สายไฟฟ้าคู่ เสาต้นทางตรงก่อนเสาต้นเข้าปลายสาย แบบ SD – TG – 4	ถูกแทนโดยแบบ เขียนเสร็จวันที่ 3 ก.พ. 35 แก้แบบวันที่ 27 ก.ค. 38 มิติเป็น มิลลิเมตร มาตราส่วน 1 : 75
รองผู้ว่าการฝ่ายเทคนิค	115 kV SINGLE–CIRCUIT DOUBLE–CONDUCTOR TANGENT STRUCTURE, ADJACENT TO DEADEND POLE TYPE SD – TG – 4	แผนผังที่ SAI-015/35004 แผ่นที่ 2 ของจำนวน 3 แผ่น


การประกอบเลขที่ ASSEMBLY NO. **5267**

บัญชีวัสดุ BILL OF MATERIAL

สิ่งของที่ ITEM	รายละเอียด DESCRIPTION	จำนวน REQ'D	วัสดุเลขที่ MAT. NO.
1	เสาคอนกรีต 22 ม. POLE, CONCRETE, 22 m LONG	1	00010011 (0041)
2	ตอนเหล็กแบบทางแขวน ขนาด L 100 X 50 X 5 มม. ยาว 2.25 ม. มอก. 116 STEEL ALLEY ARM, L 100 X 50 X 5 mm, 2.25 m LONG, TIS 116	6	01000100 (6015)
3	เหล็กประกับตอน ขนาด 40 X 6 X 1,000 มม. BRACE, FLAT FOR CROSSARM, 40 X 6 X 100 mm	6	01200002 (0121)
4	แผ่นเหล็ก ขนาด 6 X 100 X 450 มม. PLATE, STEEL 6 X 100 X 450 mm	6	01030002 (0143)
5	สลักเกลียว M 16 X 75 มม. พร้อมแหวนกลม 2 อัน BOLT, MACHINE, M 16 X 75 mm, COMPLETE WITH 2 ROUND WASHERS	6	01110400 (0236)
6	สลักเกลียว M 16 X 170 มม. BOLT, MACHINE, M 16 X 170 mm,	6	01110201 (0221)
7	สลักเกลียว M 16 X 300 มม. BOLT, MACHINE, M 16 X 300 mm	3	01110204 (0224)
8	สลักเกลียว M 16 X 350 มม. BOLT, MACHINE, M 16 X 350 mm	2	01110205 (0225)
9	สลักเกลียว M 20 X 350 มม. BOLT, MACHINE, M 20 X 350 mm	3	01110300 (0232)
10	สลักห่วงโอเวล M 16 X 150 มม. BOLT, OVAL EYE, M 16 X 150 mm	3	01150000 (0257)
11	แหวนสี่เหลี่ยมจัตุรัส 52 X 52 X 4.5 มม. รู Ø 18 มม. มอก. 258 WASHER, SQUARE, FLAT 52 X 52 X 4.5 mm, HOLE Ø 18 mm, TIS 258	20	01180100 (0355)
12	แหวนสี่เหลี่ยมจัตุรัส 62 X 62 X 6 มม. รู Ø 22 มม. มอก. 258 WASHER, SQUARE, FLAT 62 X 62 X 6 mm, HOLE Ø 22 mm, TIS 258	6	01180101 (0356)
13	แหวนสปริง M 16 มอก. 259 WASHER, LOCK, M 16, TIS 259	3	01180301 (0365)
14	ท่อเหล็กขนาด 20 มม. หนา 2.65 มม. ยาว 100 มม. PIPE, IRON DIA. 20 mm I.D., 2.65 mm THICKNESS, 100 mm LONG	3	01050000 (0905)
15	เหล็กฉากรับสายล่อฟ้าทางตรง ขนาด 65 X 65 X 6 มม. ยาว 2,500 มม. มอก. 116 OVERHEAD GROUND WIRE BAYONET, 65 X 65 X 6 mm, 2,500 mm LONG, TIS 116	1	01010004 (0135)

รายละเอียด DESCRIPTION

D-17C	การประกอบลูกถ้วยแขวน SUSPENSION INSULATOR ASSEMBLY	3	
D-5A	การต่อสายล่อฟ้า OVERHEAD GROUND WIRE CONNECTION	1	
D-10A	ฐานรากเสา POLE FOUNDATION	1	

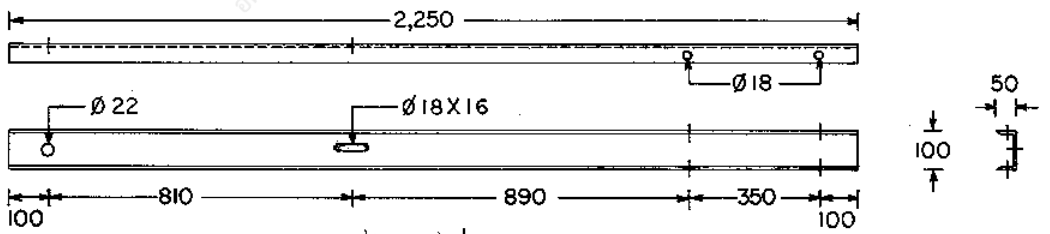

วัสดุลำดับที่ MATERIAL ITEM (2)

กองวิศวกรรมไฟฟ้าและเครื่องกล ฝ่ายวิศวกรรม ผู้เขียน ผู้สำรวจ วิศวกร หัวหน้าแผนก ผู้อำนวยการกอง ผู้อำนวยการฝ่าย รองผู้ว่าการฝ่ายเทคนิค 27 ก.พ. 2535	**การไฟฟ้าส่วนภูมิภาค** ผู้ว่าการ 27 ก.พ. 35 115 kV วงจรเดี่ยว สายไฟฟ้าคู่ เสาต้นทางตรงก่อนเสาต้นเข้าปลายสาย แบบ SD - TG - 4 115 kV SINGLE-CIRCUIT DOUBLE-CONDUCTOR TANGENT STRUCTURE, ADJACENT TO DEADEND POLE TYPE SD - TG - 4	ใช้แทนแบบ ถูกแทนโดยแบบ เขียนเสร็จวันที่ 3 ก.พ. 35 แก้แบบวันที่ 27 ก.ค. 38 ดิดเป็น มิลลิเมตร มาตราส่วน 1 : 20 แบบเลขที่ SAI-015/35004 แผ่นที่ 3 จากจำนวน 3 แผ่น