การประกอบเลขที่
ASSEMBLY NO. **5261**

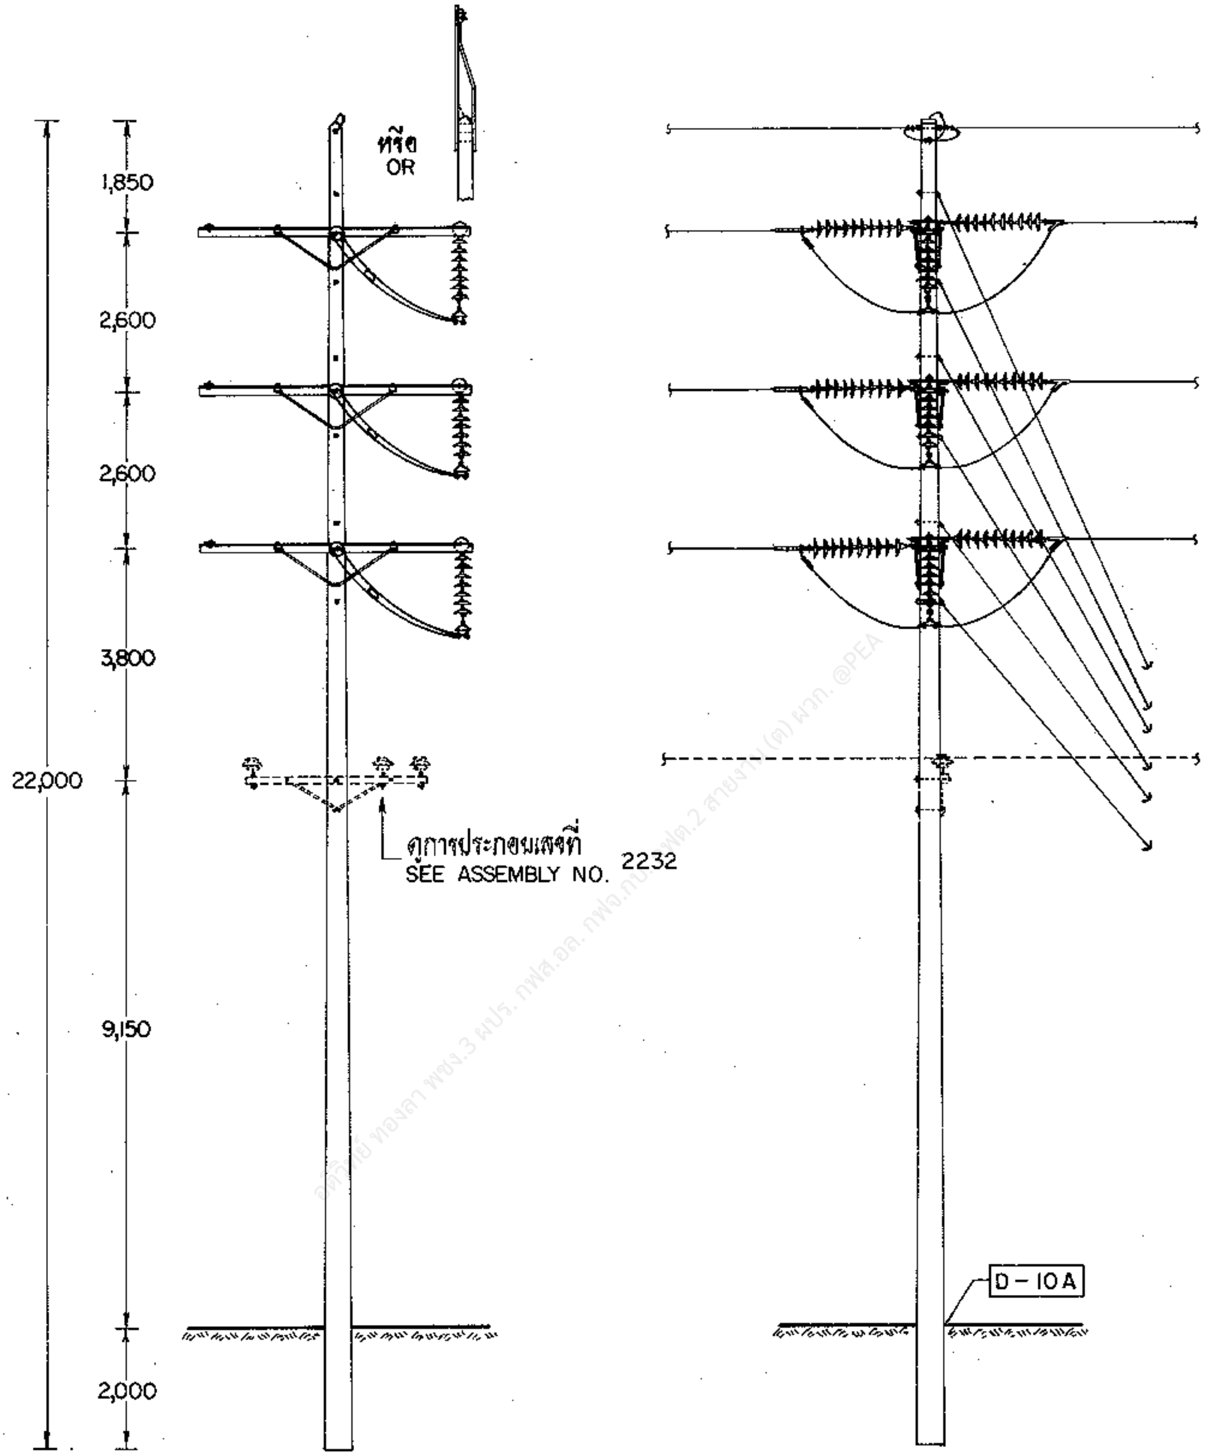

อดิวิทย์ ทองลา พชง.3 ผปร. กฟส.อล. กฟจ.กบ. กฟต.2 สายงาน(ต) ผวก. @PEA

กองวิศวกรรมไฟฟ้าและเครื่องกล
ฝ่ายวิศวกรรม

ผู้เขียน ทวีศักดิ์
ผู้สำรวจ
วิศวกร
หัวหน้าแผนก
ผู้อำนวยการกอง
ผู้อำนวยการฝ่าย
รองผู้ว่าการฝ่ายเทคนิค

การไฟฟ้าส่วนภูมิภาค

ผู้ว่าการ 29 พ.ค. 32

115 kV วงจรเดี่ยว สายไฟฟ้าคู่
โครงสร้างเสาเข้าปลายสายสองข้าง ก่อนเสาช่วงทางโค้ง
แบบ SD-AS-2

115 kV SINGLE CIRCUIT DOUBLE CONDUCTOR
DOUBLE DEADEND STRUCTURE, ADJACENT POLE TO ANGLE
TYPE SD-AS-2

ใช้แทนแบบ
ถูกแทนโดยแบบ
เขียนเสร็จวันที่ 2 ส.ค. 31
แก้แบบวันที่
มิติเป็น มิลลิเมตร
มาตราส่วน 1 : 125
แบบเลขที่ SAI-015/31059
แผ่นที่ 1 ของจำนวน 4 แผ่น

การประกอบเลขที่
ASSEMBLY NO. **5261**

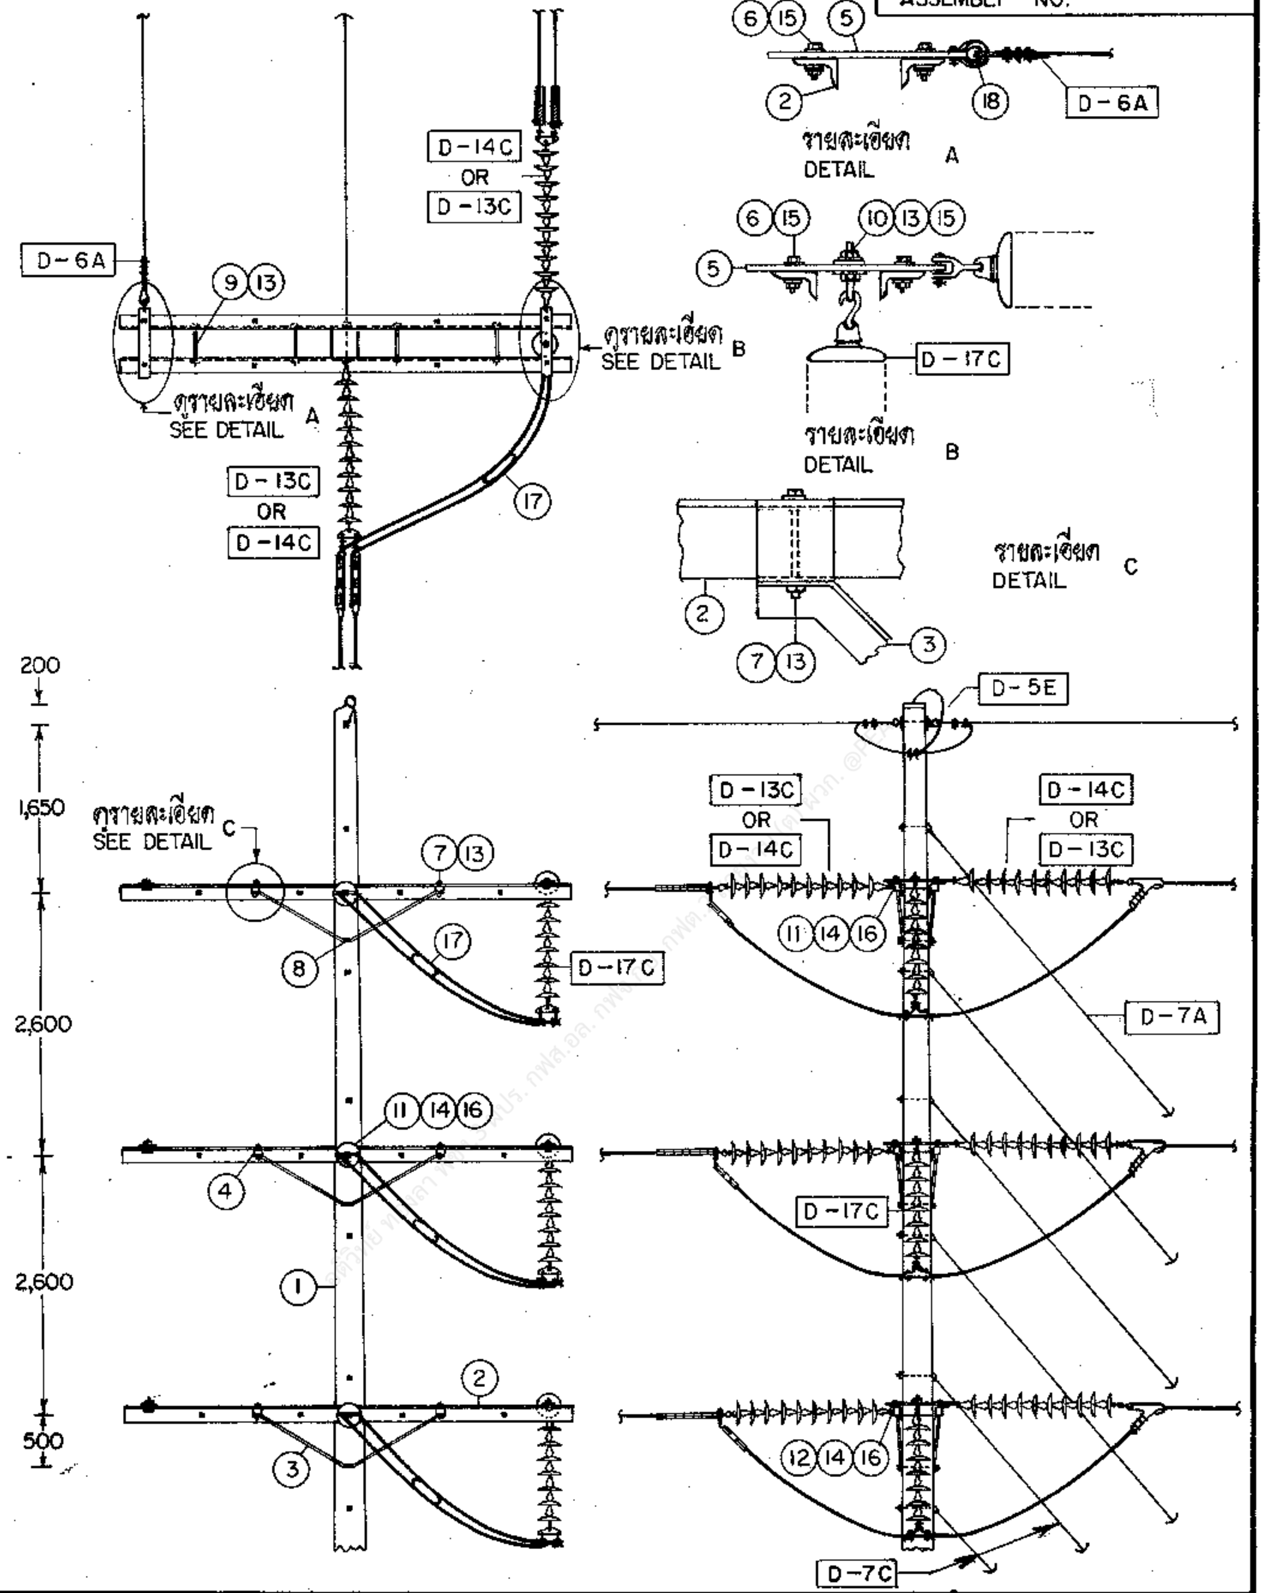

กองวิศวกรรมไฟฟ้าและเครื่องกล ฝ่ายวิศวกรรม	**การไฟฟ้าส่วนภูมิภาค**	ใช้แทนแบบ
ผู้เขียน ผู้สำรวจ วิศวกร หัวหน้าแผนก ผู้อำนวยการกอง ผู้อำนวยการฝ่าย	ผู้ว่าการ 29 พ.ค. 32	ถูกแทนโดยแบบ เขียนเสร็จวันที่ 2 ต.ค. 31 แก้แบบวันที่ 15 ก.ย. 40 มิติเป็น มิลลิเมตร มาตราส่วน 1 : 75
	115 kV วงจรเดียว สายไฟฟ้าคู่ โครงสร้างเสาเข้าปลายสายสองข้าง ก่อนเสาช่วงทางโค้ง แบบ SD-AS-2	
รองผู้ว่าการฝ่ายเทคนิค	115 kV SINGLE CIRCUIT DOUBLE CONDUCTOR DOUBLE DEADEND STRUCTURE, ADJACENT POLE TO ANGLE TYPE SD-AS-2	แบบเลขที่ SAI-015/31059 แผ่นที่ 2 ของจำนวน 4 แผ่น

[illegible] 2532

การประกอบเลขที่
ASSEMBLY NO. **5261**

บัญชีวัสดุ
BILL OF MATERIAL

ลำดับที่ ITEM	รายละเอียด DESCRIPTION	จำนวน REQ'D	วัสดุเลขที่ MAT. NO.
1	เสาคอนกรีต 22 ม. POLE, CONCRETE 22 m LONG	1	00010011 (0041)
2	คอนสายแบบเหล็กฉาก ขนาด 150 X 100 X 12 มม. ยาว 4.50 ม. CROSSARM, STEEL ANGLE 150 X 100 X 12 mm, 4.50 m LONG	6	00120002 (6001)
3	เหล็กฉากรับคอนสาย 50 X 50 X 6 มม. ช่วงกว้าง 1,800 มม. ดรอพ 450 มม. BRACE, ANGLE STEEL 50 X 50 X 6 mm, 1,800 mm WIDE, 450 mm DROP	6	01200007 (0119)
4	ท่อเหล็ก ขนาด 100 X 50 X 3.2 มม. ยาว 100 มม. ADAPTER, TUBE, RECTANGULAR STEEL, 100 X 50 X 3.2 mm, 100 mm LONG	—	01050200 (6004)
5	แผ่นเหล็กยึดสองปลาย ขนาด 12 X 100 X 760 มม. PLATE, STEEL, DOUBLE ARMING, 12 X 100 X 760 mm	6	01030102 (6006)
6	สลักเกลียว M 16 X 75 มม. พร้อมแหวนกลม 2 อัน BOLT, MACHINE, M 16 X 75 mm, COMPLETE WITH 2 ROUND WASHERS	12	01110400 (0236)
7	สลักเกลียว M 16 X 170 มม. BOLT, MACHINE, M 16 X 170 mm	12	01110201 (0221)
8	สลักเกลียว M 16 X 350 มม. BOLT, MACHINE, M 16 X 350 mm	3	01110205 (0225)
9	สลักเกลียวตลอด M 16 X 400 มม. BOLT, DOUBLE ARMING, M 16 X 400 mm	12	01120000 (0243)
10	สลักห่วงโอแวล M 16 X 150 มม. (เพิ่มนัทอีกหนึ่งอัน) BOLT, OVAL EYE, M 16 X 150 mm (ADD ONE SQUARE NUT)	3	01150000 (0257)
11	สลักห่วงโอแวล M 20 X 350 มม. BOLT, OVAL EYE, M 20 X 350 mm	2	01150100 (0260)
12	สลักห่วงโอแวล M 20 X 450 มม. BOLT, OVAL EYE, M 20 X 450 mm	1	01150101 (0261)
13	แหวนสี่เหลี่ยมแบน 52 X 52 X 4.5 มม. รู Ø 18 มม. มอก. 258 WASHER, SQUARE, FLAT 52 X 52 X 4.5 mm HOLE Ø 18 mm, TIS. 258	66	01180100 (0355)
14	แหวนสี่เหลี่ยมแบน 62 X 62 X 6 มม. รู Ø 22 มม. มอก. 258 WASHER, SQUARE, FLAT 62 X 62 X 6 mm, HOLE Ø 22 mm, TIS. 258	6	01180101 (0356)
15	แหวนสปริง M 16 มอก. 259 WASHER, LOCK, M 16, TIS. 259	15	01180301 (0365)
16	แหวนสปริง M 20 มอก. 259 WASHER, LOCK, M 20, TIS. 259	3	01180302 (0366)
17	ปรีฟอร์มแยกสาย SPACER, HELICAL ROD, PREFORMED	6	02240000 (0918)
18	ทิมเบิลเคลวิส สำหรับปรีฟอร์มเข้าปลายสาย CLEVIS, THIMBLE, FOR PREFORMED DEADEND	3	03140011 (0482)

กองวิศวกรรมไฟฟ้าและเครื่องกล
ฝ่ายวิศวกรรม

ผู้เขียน
ผู้สำรวจ
วิศวกร
หัวหน้าแผนก
ผู้อำนวยการกอง
ผู้อำนวยการฝ่าย

รองผู้ว่าการฝ่ายเทคนิค

การไฟฟ้าส่วนภูมิภาค

ผู้ว่าการ [illegible]

115 kV วงจรเดี่ยว สายไฟฟ้าคู่
โครงสร้างเสาเข้าปลายสายสองข้าง ก่อนเสาช่วงทางโค้ง
แบบ SD-AS-2

115 kV SINGLE CIRCUIT DOUBLE CONDUCTOR
DOUBLE DEADEND STRUCTURE, ADJACENT POLE TO ANGLE
TYPE SD-AS-2

ใช้แทนแบบ
ถูกแทนโดยแบบ
เขียนเสร็จวันที่ 2 ส.ค. 31
แก้แบบวันที่
มิติเป็น —
มาตราส่วน

แบบเลขที่ SAI-015/31059
แผ่นที่ 3 ของจำนวน 4 แผ่น

* อาจเปลี่ยนแปลงเป็นแบบอื่น โดยขึ้นอยู่กับสภาพของดิน

การประกอบเลขที่
ASSEMBLY NO. **5261**

รายละเอียด DETAIL			
D-13C	การประกอบลูกถ้วยแขวน SUSPENSION INSULATOR ASSEMBLY	3	
D-14C	การประกอบลูกถ้วยแขวน SUSPENSION INSULATOR ASSEMBLY	3	
D-17C	การประกอบลูกถ้วยแขวน SUSPENSION INSULATOR ASSEMBLY	3	
D-5E	การต่อสายล่อฟ้า OVERHEAD GROUND WIRE CONNECTION	1	
D-6A	การประกอบสายยึดโยงลวดเหล็กตีเกลียว 50 ต.มม. STEEL STRANDED WIRE 50 mm^2, GUY ASSEMBLY	3	
D-7A	การประกอบสายยึดโยงลวดเหล็กตีเกลียว 95 ต.มม. STEEL STRANDED WIRE 95 mm^2, GUY ASSEMBLY	4	
D-7C	การประกอบสายยึดโยงลวดเหล็กตีเกลียว 95 ต.มม. STEEL STRANDED WIRE 95 mm^2, GUY ASSEMBLY	2	
D-9B*	สมอบกคอนกรีต ตามแบบเลขที่ IBI-015/240027 (การประกอบเลขที่ 5652) CONCRETE ANCHOR ACCORDING TO DWG. NO. IBI-015/240027 (ASSEMBLY NO. 5652)	1	
D-10A*	ฐานรากเสา ตามแบบเลขที่ IBI-015/240025 (การประกอบเลขที่ 5668) POLE FOUNDATION ACCORDING TO. DWG. NO. IBI-015/240025 (ASSEMBLY NO. 5668)	1	

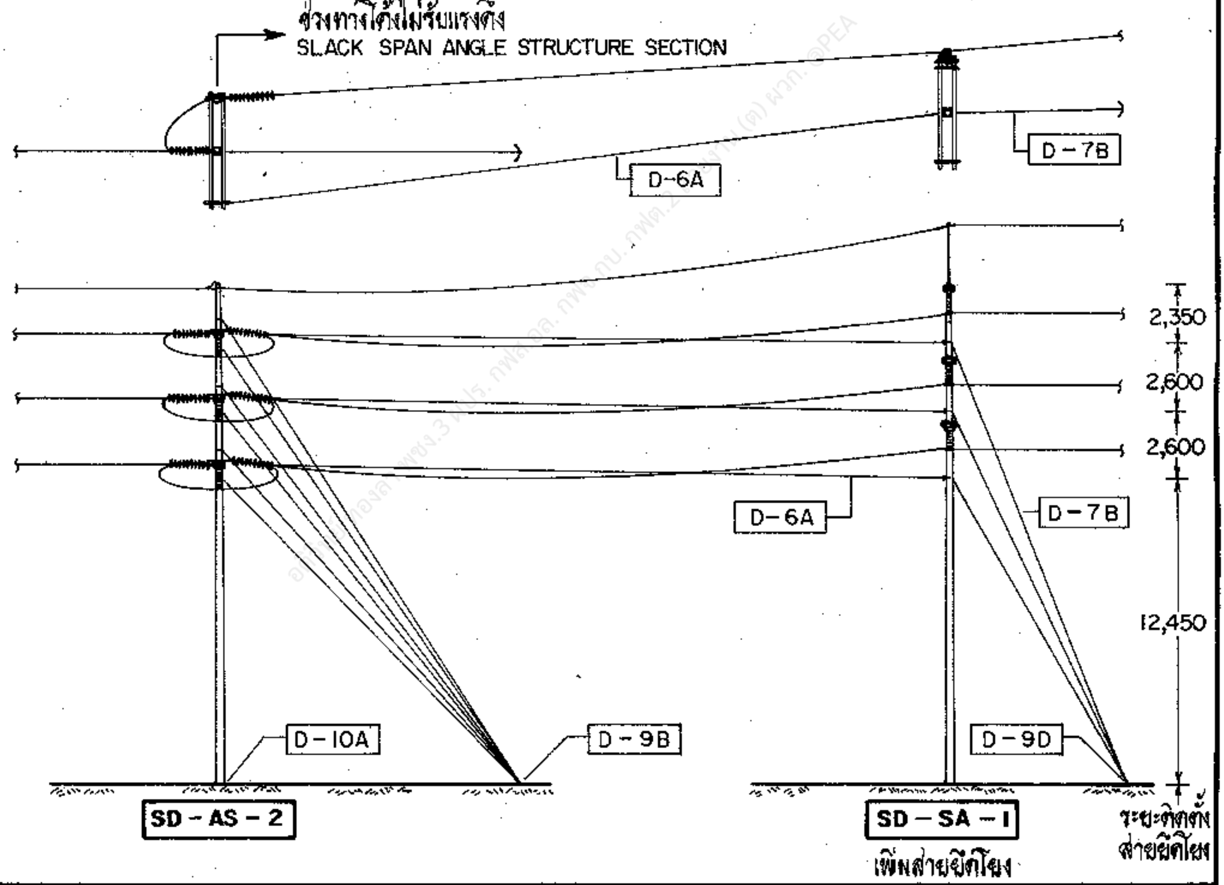

กองวิศวกรรมไฟฟ้าและเครื่องกล
ฝ่ายวิศวกรรม

ผู้เขียน
ผู้สำรวจ
วิศวกร
หัวหน้าแผนก
ผู้อำนวยการกอง
ผู้อำนวยการฝ่าย
รองผู้ว่าการฝ่ายเทคนิค

การไฟฟ้าส่วนภูมิภาค

ผู้ว่าการ ๒๑-๒-๗-๓๒

115 kV วงจรเดี่ยว สายไฟฟ้าคู่
โครงสร้างเสาเข้าปลายสายสองข้าง ก่อนเสาช่วงทางโค้ง
แบบ SD-AS-2

115 kV SINGLE CIRCUIT DOUBLE CONDUCTOR
DOUBLE DEADEND STRUCTURE, ADJACENT POLE TO ANGLE
TYPE SD-AS-2

ใช้แทนแบบ
ถูกแทนโดยแบบ
เขียนเสร็จวันที่ 2 ส.ค. 31
แก้แบบวันที่ 15 ก.ย. 40
มิติเป็น มิลลิเมตร
มาตราส่วน 1 : 300
แบบเลขที่ SAI-015/31059
แผ่นที่ 4 ของจำนวน 4 แผ่น

28 ม.ค. 25