การประกอบเลขที่
ASSEMBLY NO. 3218

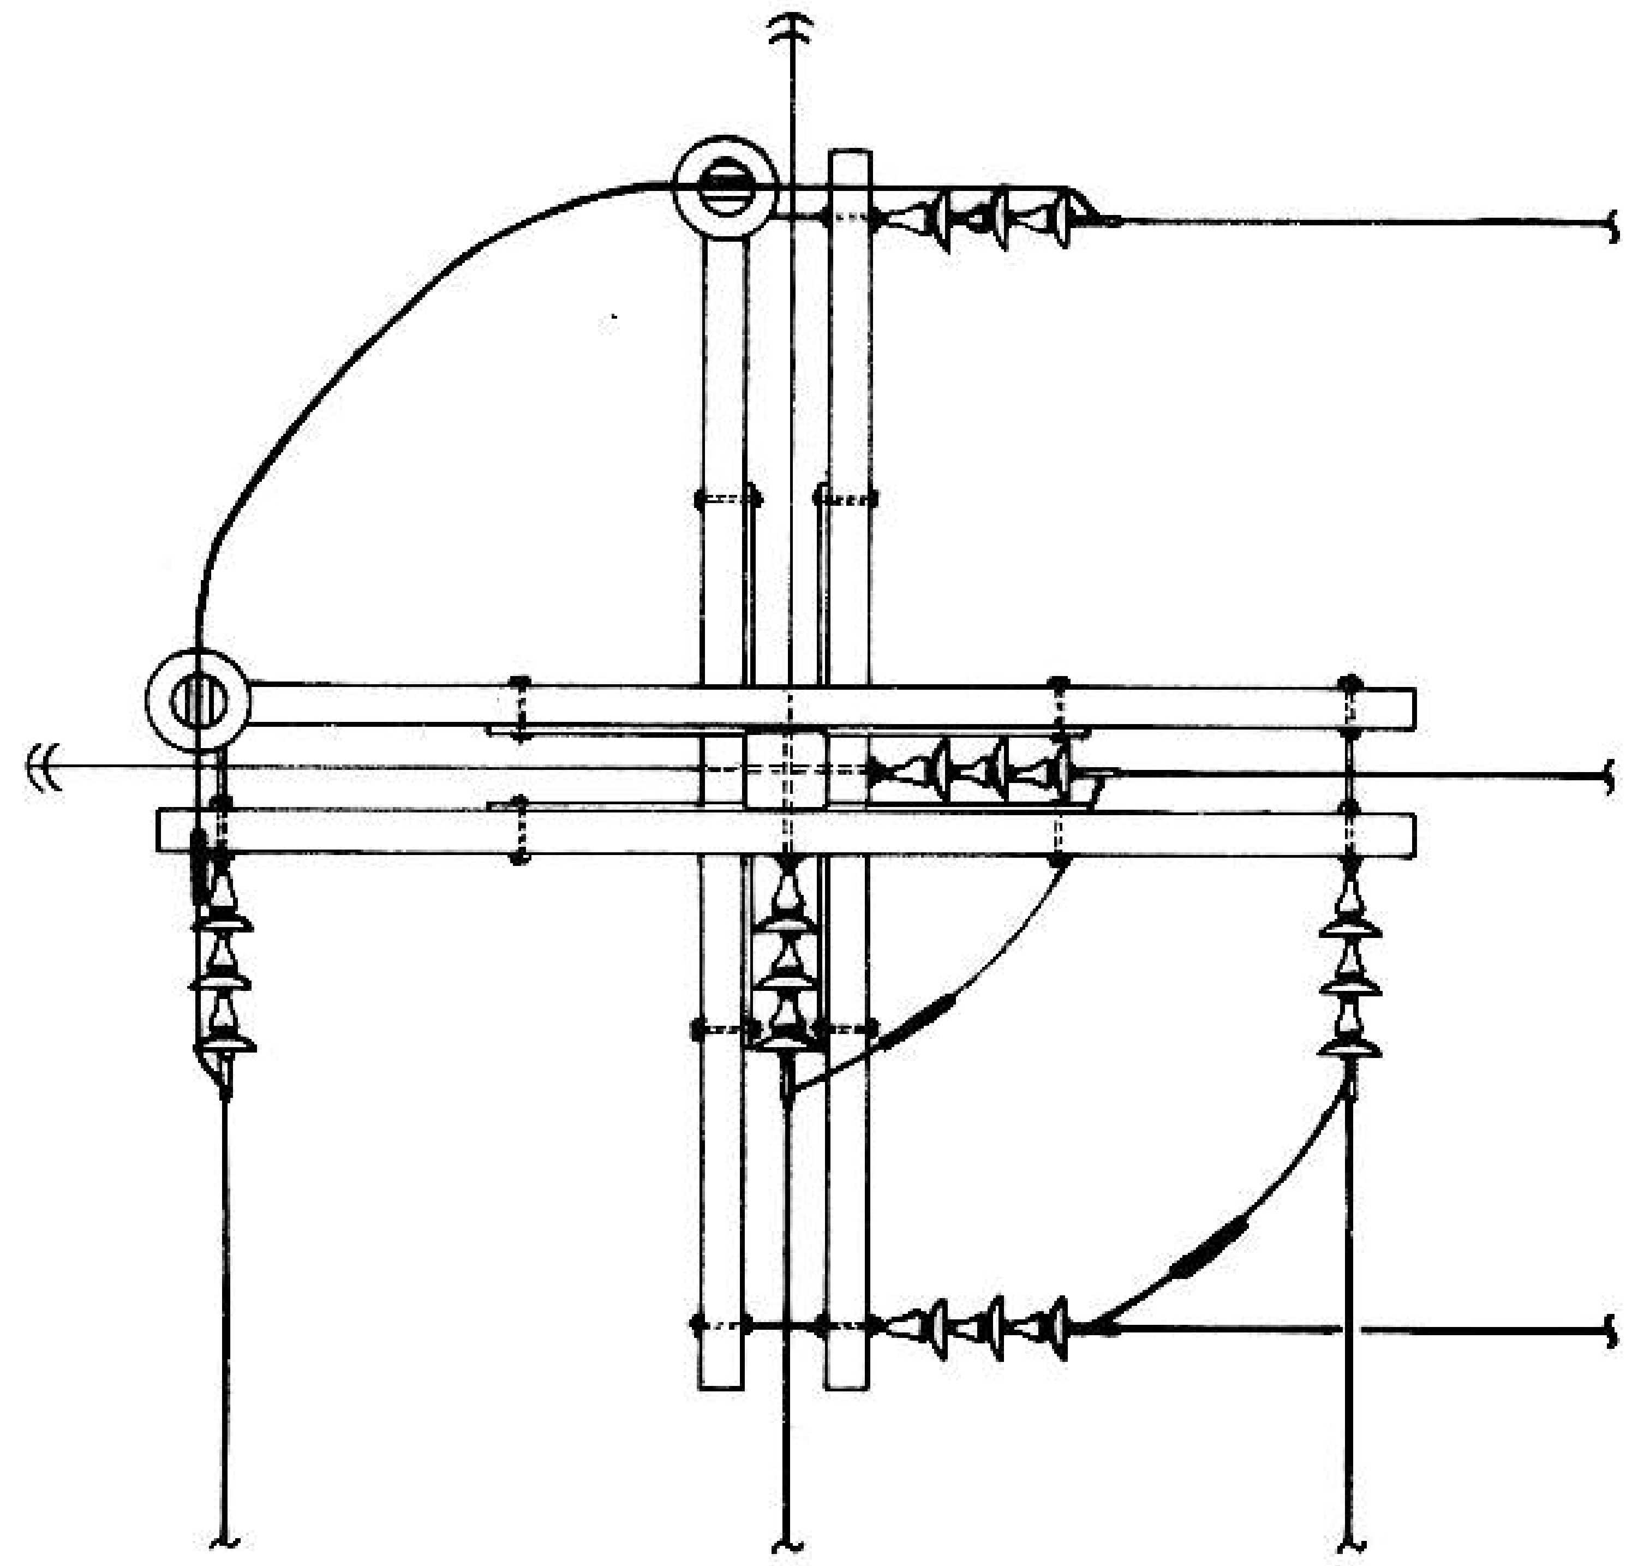

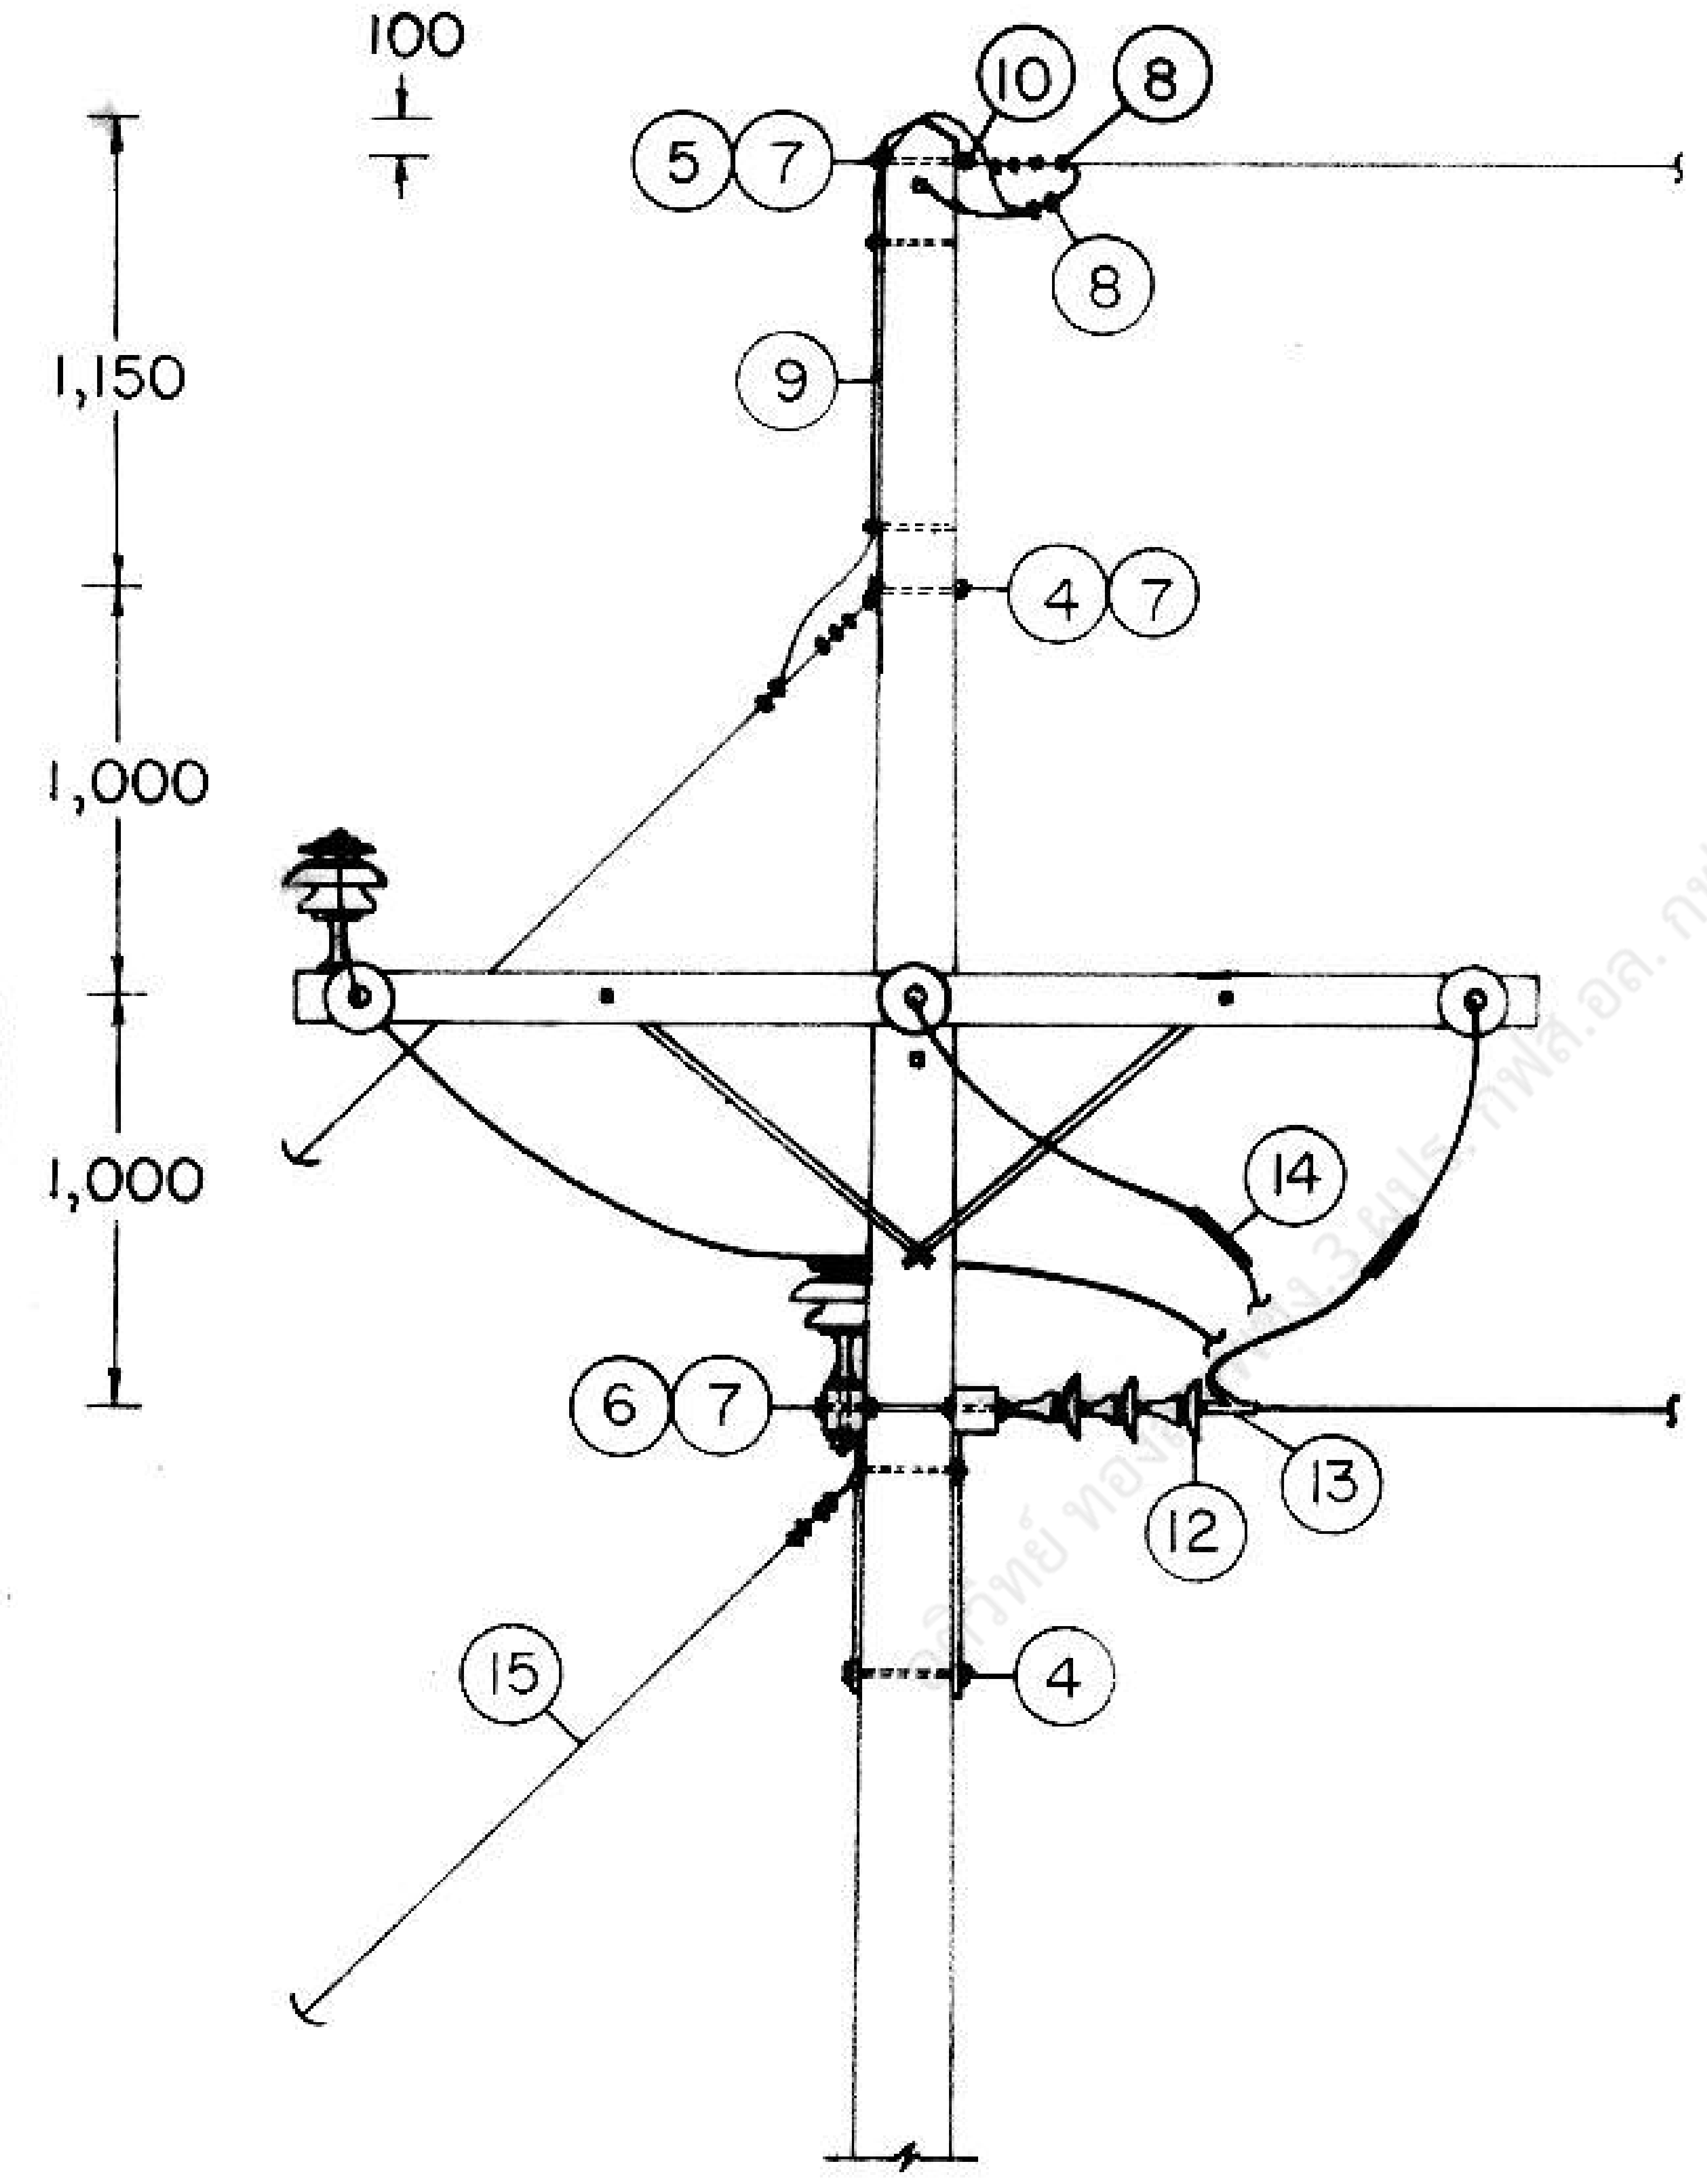

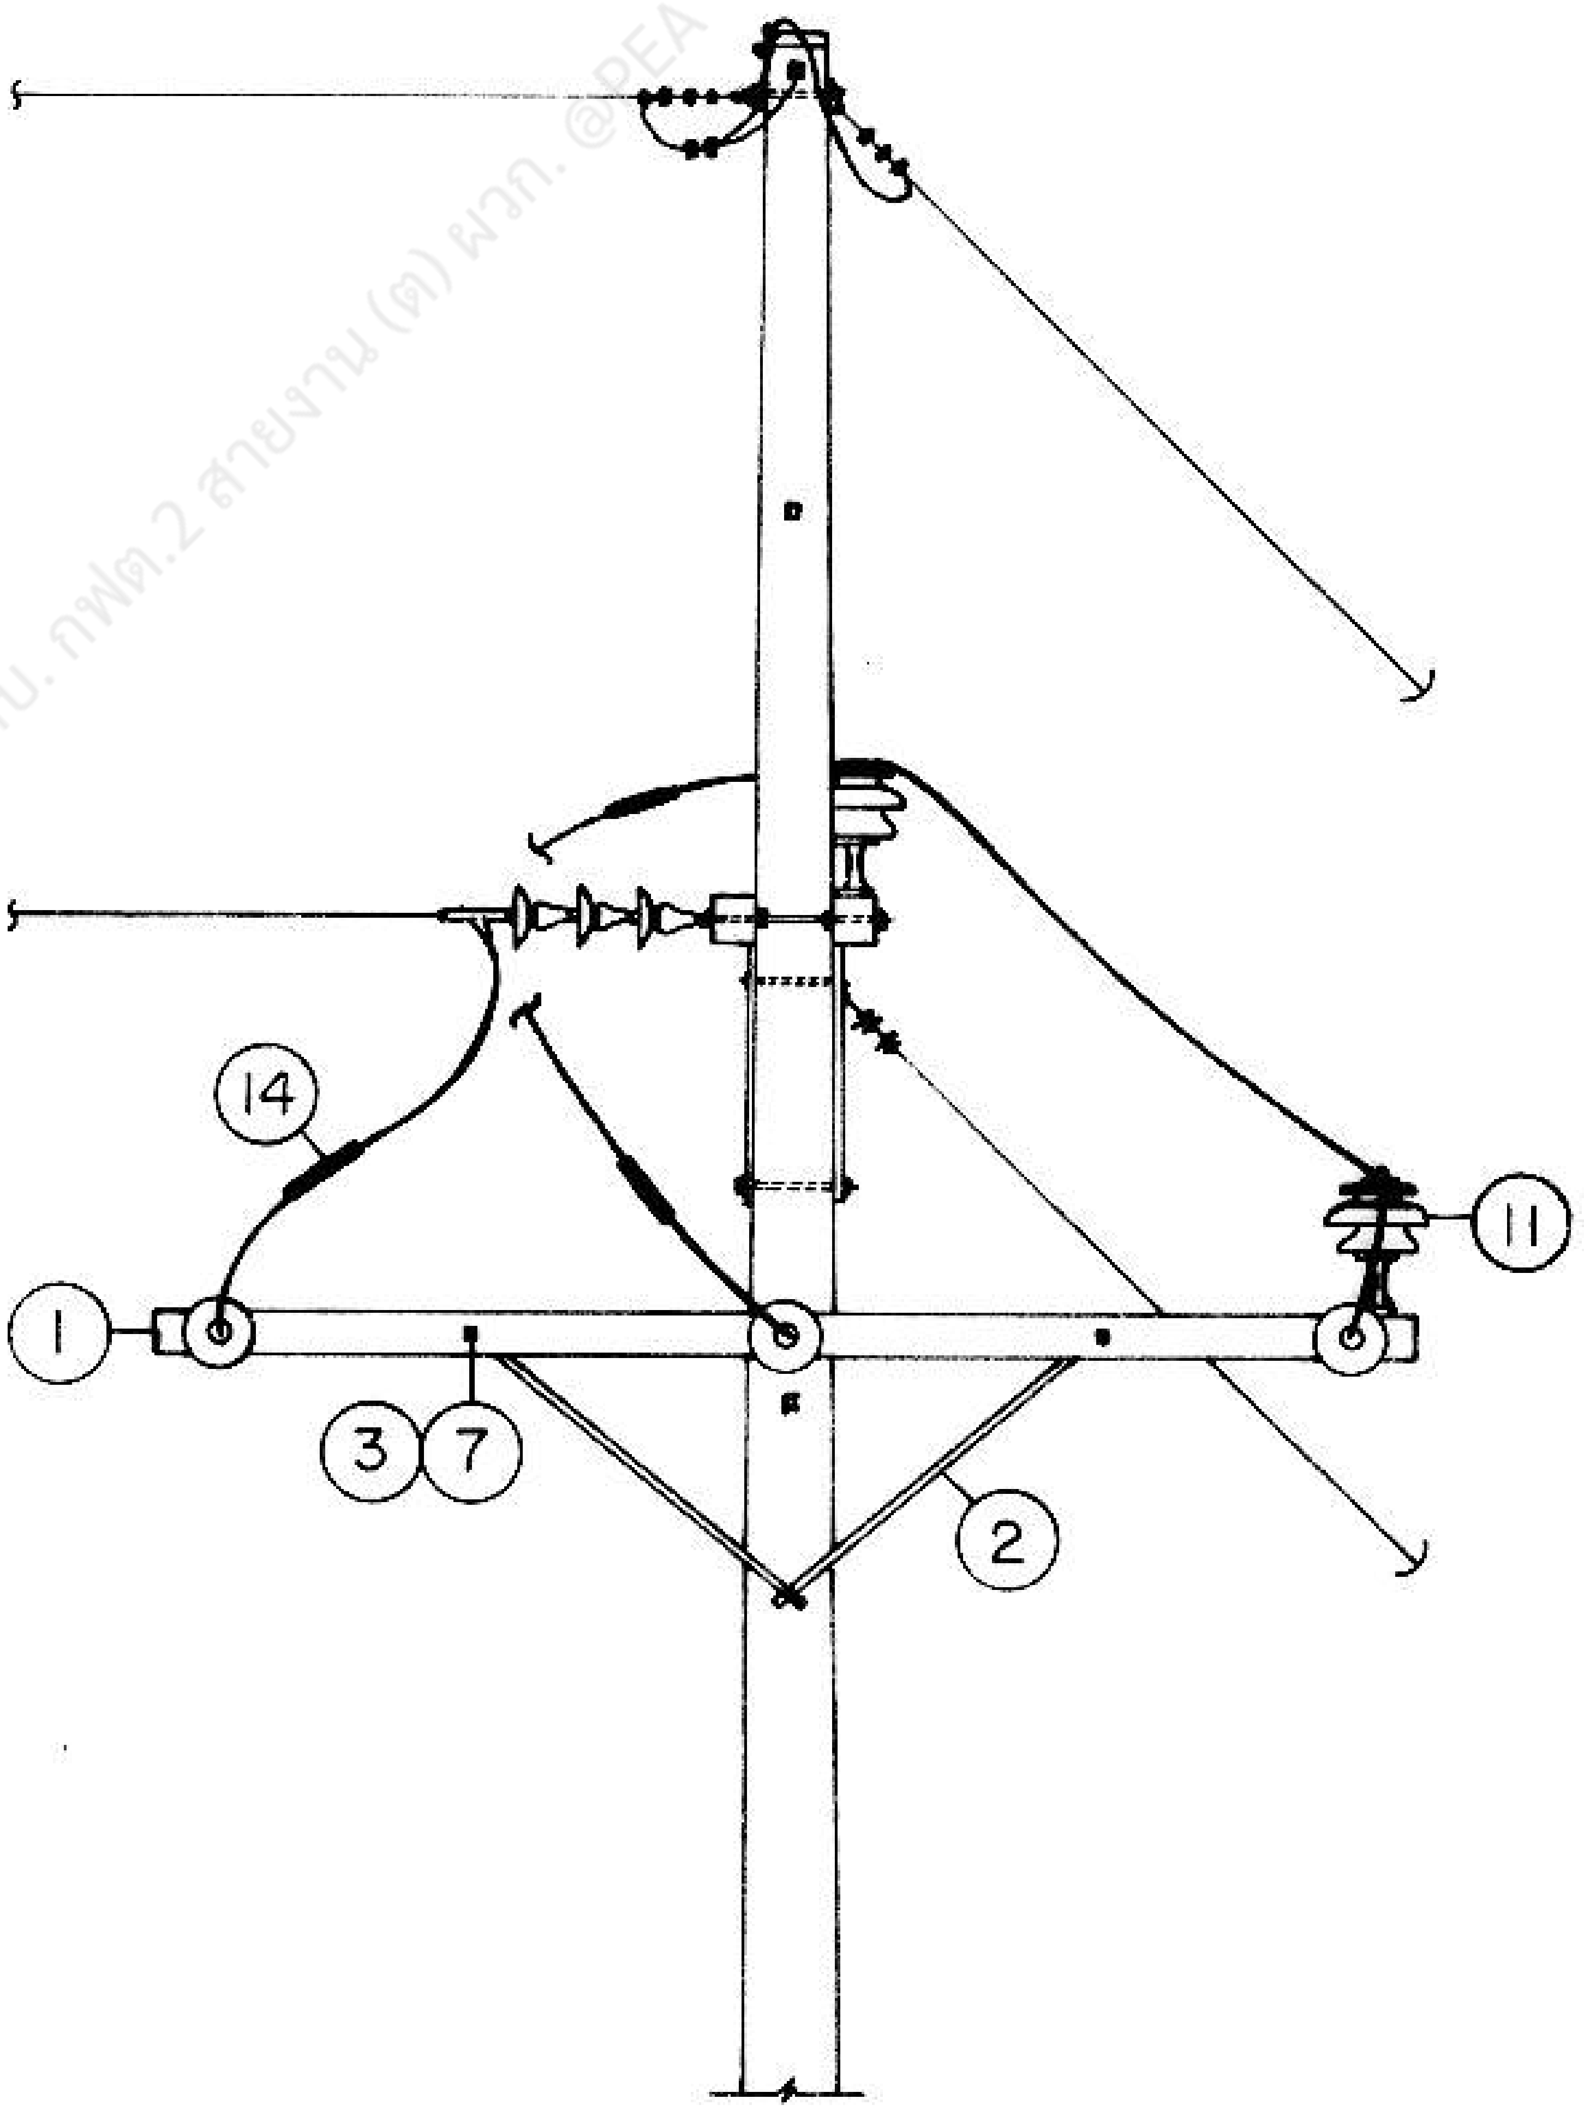

กฟส.อล. กฟจ.กบ. กฟต.2 สายงาน (ต) ผวก. ©PEA

กองวิศวกรรมไฟฟ้าและเครื่องกล
ฝ่ายวิศวกรรม

ผู้เขียน
ผู้สำรวจ
วิศวกร
หัวหน้าแผนก
หัวหน้ากอง
ผู้อำนวยการฝ่าย
รองผู้ว่าการฝ่ายเทคนิค

การไฟฟ้าส่วนภูมิภาค

ผู้ว่าการ 24 ม.ค. 21.

การติดตั้งบัคอาร์มระบบ 33 kV
สำหรับเสาต้นสุดท้าย

33 kV BUCKARM INSTALLATION
FOR DEADEND POLE

ใช้แทนแบบ
ถูกแทนโดยแบบ
เขียนเสร็จวันที่ 6 ม.ค. 21
แก้แบบวันที่
มิติเป็น มม.
มาตราส่วน
แบบเลขที่ SA1-015/21004
แผ่นที่ 1 ของจำนวน 2 แผ่น

การประกอบเลขที่
ASSEMBLY NO. 3218

บัญชีวัสดุ
BILL OF MATERIAL

ลำดับที่ ITEM	รายละเอียด DESCRIPTION	จำนวน REQ'D	วัสดุเลขที่ MAT. NO.
1	ไม้คอนสายแรงสูง 100 X 120 X 3,000 มม. CROSSARM, WOOD, H.T. 100 X 120 X 3,000 mm	2	00100003 (0101)
2	เหล็กประกับไม้คอน 40 X 6 X 1,000 มม. BRACE, FLAT FOR CROSSARM 40 X 6 X 1,000 mm	4	01200002 (0121)
3	สลักเกลียว M 16 X 130 มม. BOLT, MACHINE M 16 X 130 mm	4	01110200 (0220)
4	สลักเกลียว M 16 X 300 มม. BOLT, MACHINE M 16 X 300 mm	2	01110203 (0223)
5	สลักห่วงกลม M 16 X 250 มม. BOLT, ROUND EYE M 16 X 250 mm	1	01140001 (0253)
6	สลักเกลียวห่วงกลม M 16 X 450 มม. BOLT, DOUBLE ARMING ROUND EYE M 16 X 450 mm	3	01130001 (0247)
7	แหวนสี่เหลี่ยมแบน 52 X 52 X 4.5 มม. รู Ø 18 มม. มอก. 258 WASHER, SQUARE FLAT 52 X 52 X 4.5 mm HOLE Ø 18 mm TIS 258	17	01180100 (0355)
8	ยูแคล้มป์ สลัก 1 M 8 CLAMP, SINGLE U-BOLT M 8	4	01230000 (0165)
9	ลวดเหล็กตีเกลียว 25 ต.มม. มอก. 404 STEEL STRANDED WIRE 25 mm^2 TIS 404	2 ม. m	01100002 (0181)
10	กายทิมเบิ้ลสำหรับลวดเหล็ก 50-95 ต.มม. THIMBLE, GUY FOR STEEL WIRE 50—95 mm^2	1	01210304 (0150)
11	ลูกถ้วยก้านตรง 33 kV มอก. 279 แบบ ค (แบบ 56-3) พร้อมก้าน INSULATOR, PIN TYPE 33 kV TIS 279 TYPE C (CLASS 56-3) COMP. WITH PIN	2	03000002 03100001
12	ลูกถ้วยแขวน มอก. 354 แบบ ง (แบบ 52-4) INSULATOR, SUSPENSION TYPE TIS 354 TYPE D (CLASS 52-4)	9	03020002 (0415)
13	สเตรนแคล้มป์สำหรับสายอะลูมิเนียม อะลูมิเนียมอัลลอย และอะลูมิเนียมแกนเหล็ก ขนาดตามต้องการ CLAMP, STRAIN, FOR Al, Al-ALLOY AND ACSR SIZE AS REQ'D	3	03110004 - 03110101
14	หลอดต่อสายชนิดบีบไม่รับแรงดึง ขนาดตามต้องการ CONNECTOR, SPLICE COMPRESSION TYPE, TENSIONLESS SIZE AS REQ'D	3	02410001 - 02410005
15	การประกอบสายยึดโยงแบบ GY-33 GUY ASSEMBLY TYPE GY-33	1	

หมายเหตุ
1 ในกรณีขาดแคลนหลอดต่อสาย ให้ใช้พีจี คอนเนคเตอร์ 2 อัน แทนได้
2 ในกรณีที่ทำการก่อสร้างในตัวเมือง สายล่อฟ้าอาจไม่ต้องทำการยึดโยงได้

NOTES
1 IN CASE OF LACKING TENSIONLESS SPLICE CONNECTOR, PERMIT TO USE 2 P.G. CONNECTORS.
2 FOR URBAN CONSTRUCTION, GUY OF OVERHEAD GROUND WIRE MAY BE OMITTED.

กองวิศวกรรมไฟฟ้าและเครื่องกล
ฝ่ายวิศวกรรม

ผู้เขียน
ผู้สำรวจ
วิศวกร
หัวหน้าแผนก
หัวหน้ากอง
ผู้อำนวยการฝ่าย
รองผู้ว่าการฝ่ายเทคนิค

การไฟฟ้าส่วนภูมิภาค

ผู้ว่าการ 24 ม.ค. 21

การติดตั้งบัคอาร์มระบบ 33 kV
สำหรับเสาต้นสุดท้าย

33 kV BUCKARM INSTALLATION
FOR DEADEND POLE

ใช้แทนแบบ
ถูกแทนโดยแบบ
เขียนเสร็จวันที่ 6 ม.ค. 21
แก้แบบวันที่
มิติเป็น
มาตราส่วน

แบบเลขที่ SAI-015/21004
แผ่นที่ 2 ของจำนวน 2 แผ่น