การประกอบเลขที่
ASSEMBLY NO. **3228**

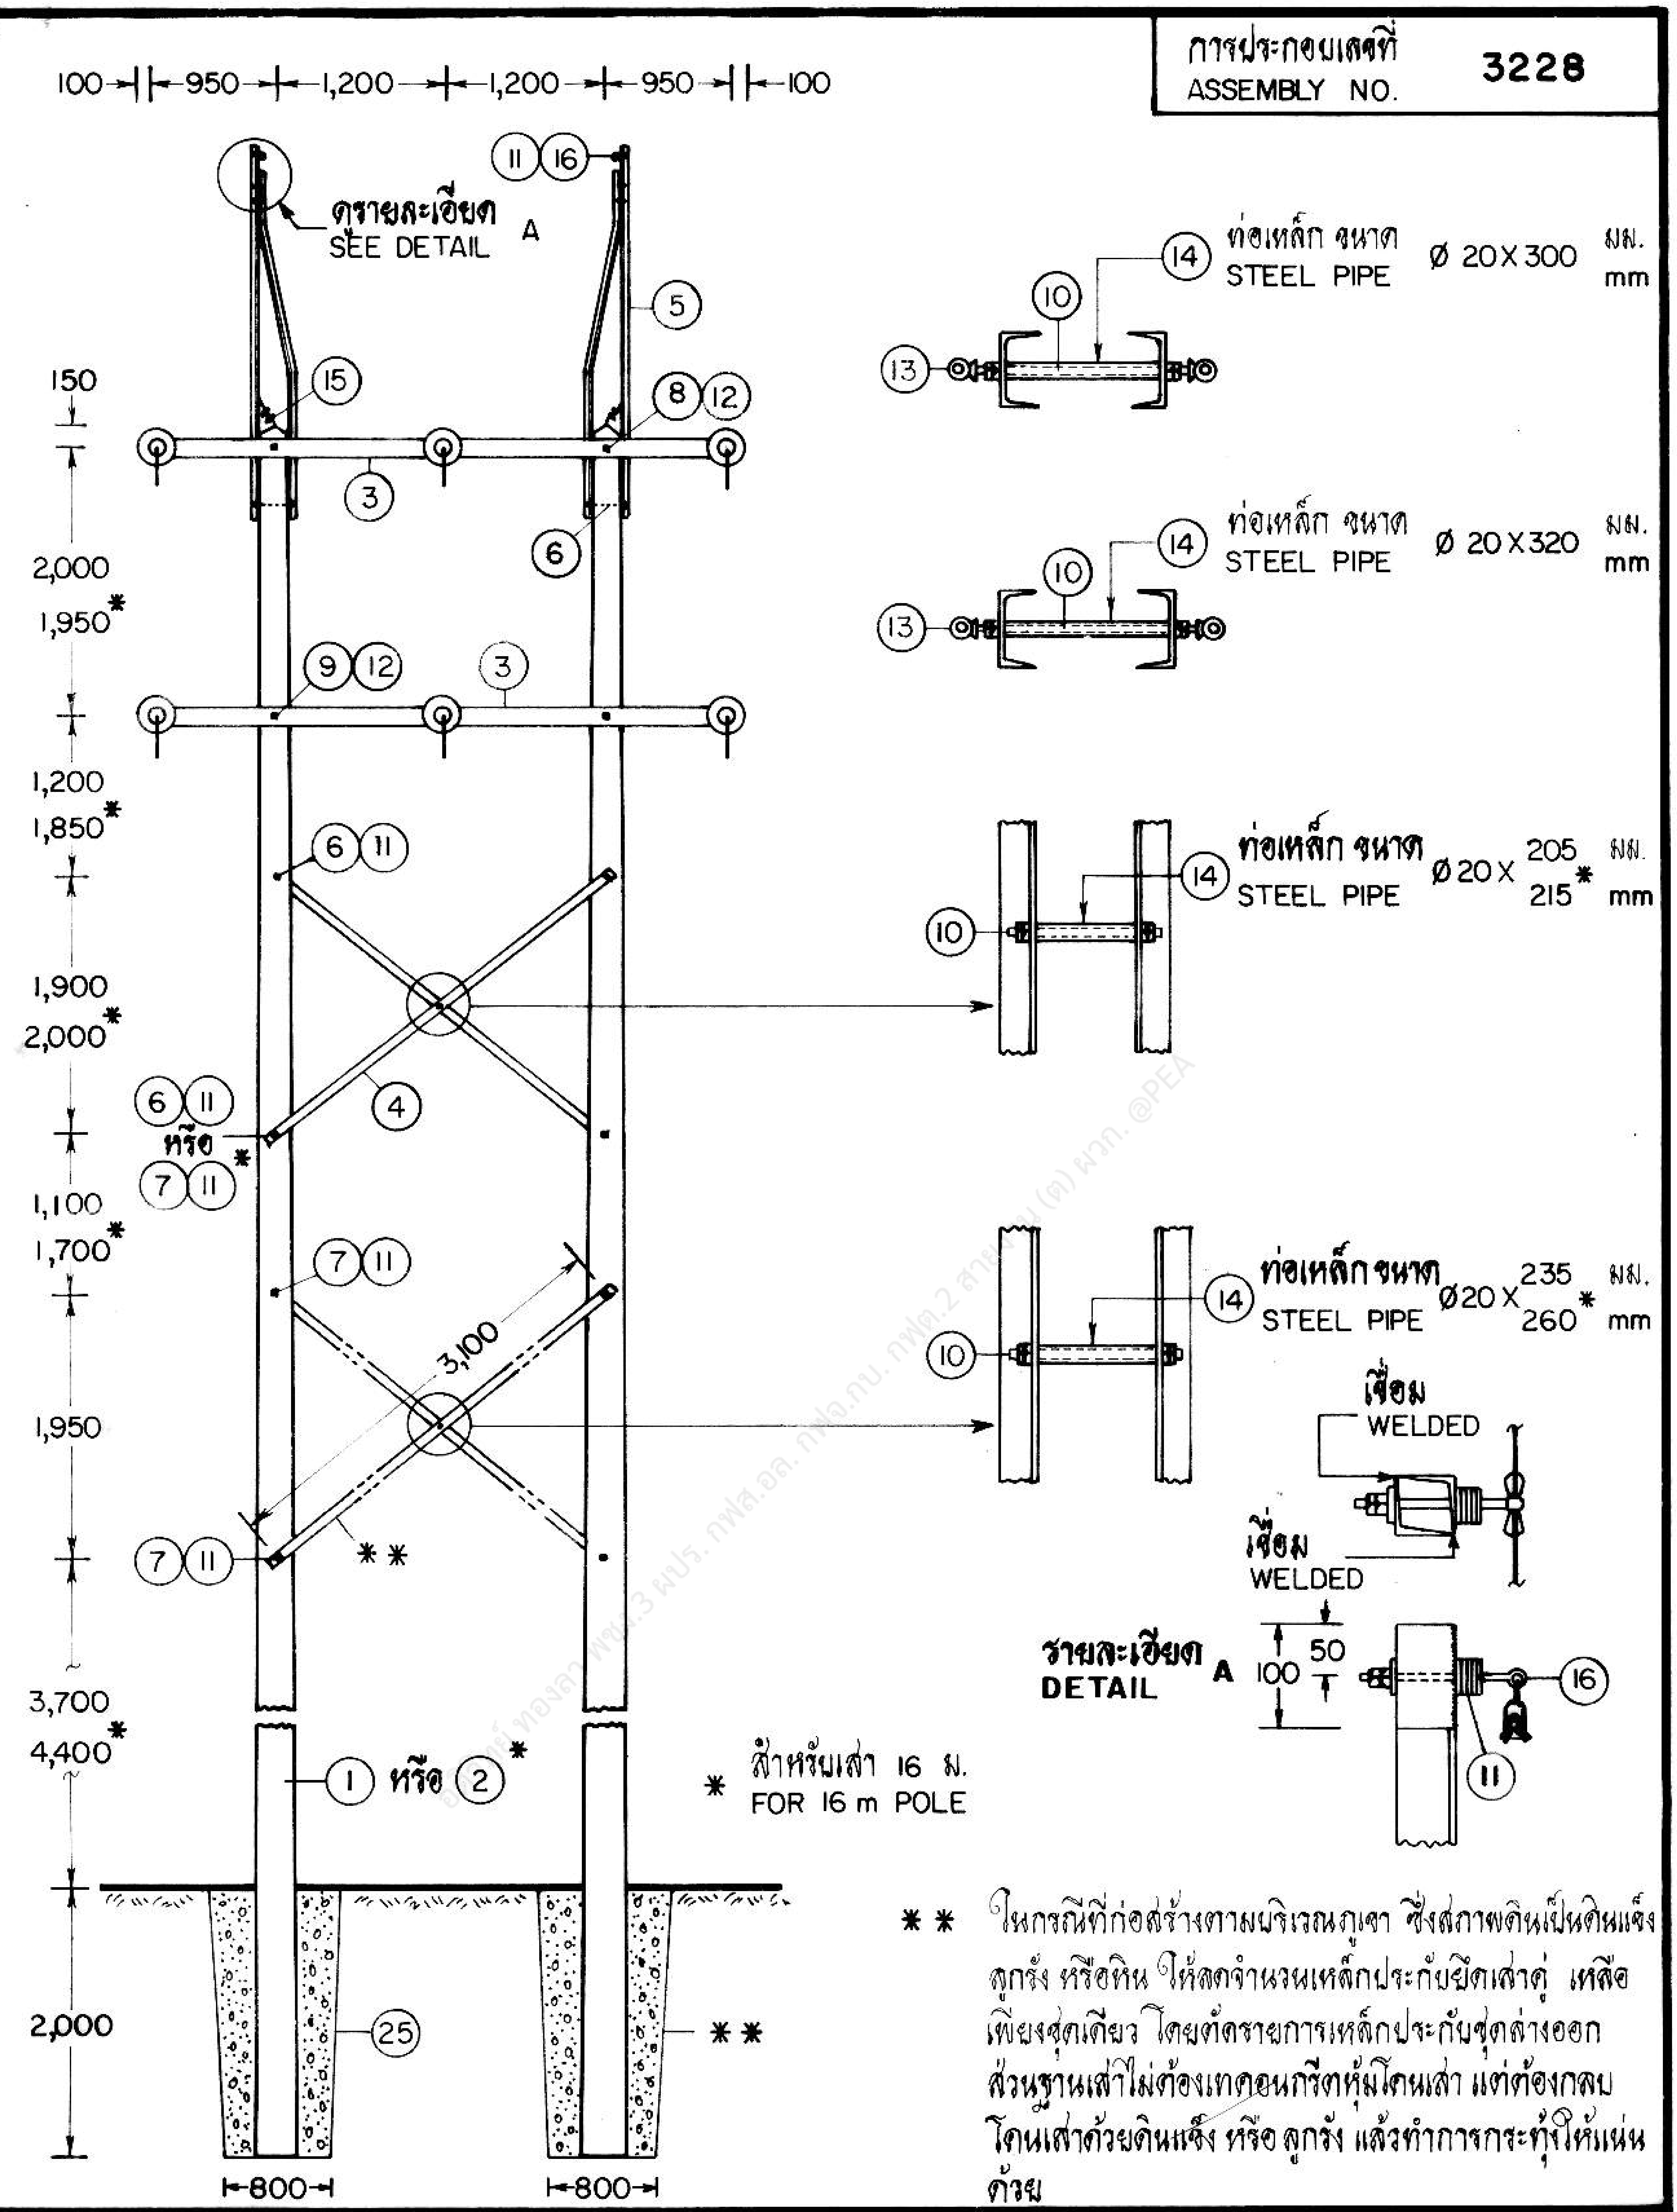

* สำหรับเสา 16 ม.
FOR 16 m POLE

* * ในกรณีที่ก่อสร้างตามบริเวณภูเขา ซึ่งสภาพดินเป็นดินแข็ง ลูกรัง หรือหิน ให้ลดจำนวนเหล็กประกับยึดเสาคู่ เหลือเพียงชุดเดียว โดยตัดรายการเหล็กประกับชุดล่างออก ส่วนฐานเสาไม่ต้องเทคอนกรีตหุ้มโคนเสา แต่ต้องกลบโคนเสาด้วยดินแข็ง หรือ ลูกรัง แล้วทำการกระทุ้งให้แน่นด้วย

ทองสา พชช.3 ผปร. กฟส.อล. กฟฉ.กบ. กฟต.2 สายงาน (ต) ผวก. @PEA

กองวิศวกรรมไฟฟ้าและเครื่องกล
ฝ่ายวิศวกรรม

ผู้เขียน
ผู้ตรวจ
วิศวกร
หัวหน้าแผนก
ผู้อำนวยการกอง
ผู้อำนวยการฝ่าย

รองผู้ว่าการฝ่ายเทคนิค

การไฟฟ้าส่วนภูมิภาค

ผู้ว่าการ 25 มี.ค. 31

มาตรฐานการก่อสร้างระบบ 33 kV 2 วงจร
ช่วง 120-200 ม.

33 kV, 2 CIRCUIT STANDARD CONSTRUCTION
SPAN 120-200 m

ใช้แทนแบบ
ถูกแทนโดยแบบ
เขียนเสร็จวันที่ 14 ก.ค. 30
แก้แบบวันที่
มิติเป็น มม.
มาตราส่วน 1 : 75

แบบเลขที่ SAI-015/30015
แผ่นที่ 1 ของจำนวน 4 แผ่น

การประกอบเลขที่
ASSEMBLY NO. **3228**

ชนิดของสายไฟฟ้า TYPE OF CONDUCTOR	พื้นที่หน้าตัดระบุ ต.มม. NOMINAL CROSS-SECTIONAL AREA mm²	จำนวนสายยึดโยง (ลวดเหล็กตีเกลียว 95 ต.มม.) NO. OF GUY WIRE SETS (STEEL STRANDED WIRE 95 mm²)
อะลูมิเนียมเปลือย BARE ALUMINIUM	185	6
อะลูมิเนียมแกนเหล็ก ACSR	50/8	4
	70/12, 95/15, 120/20	6
	185/30	8
อะลูมิเนียมอัลลอย ALUMINIUM-ALLOY	50	4
	70, 95, 120	6
	185	8

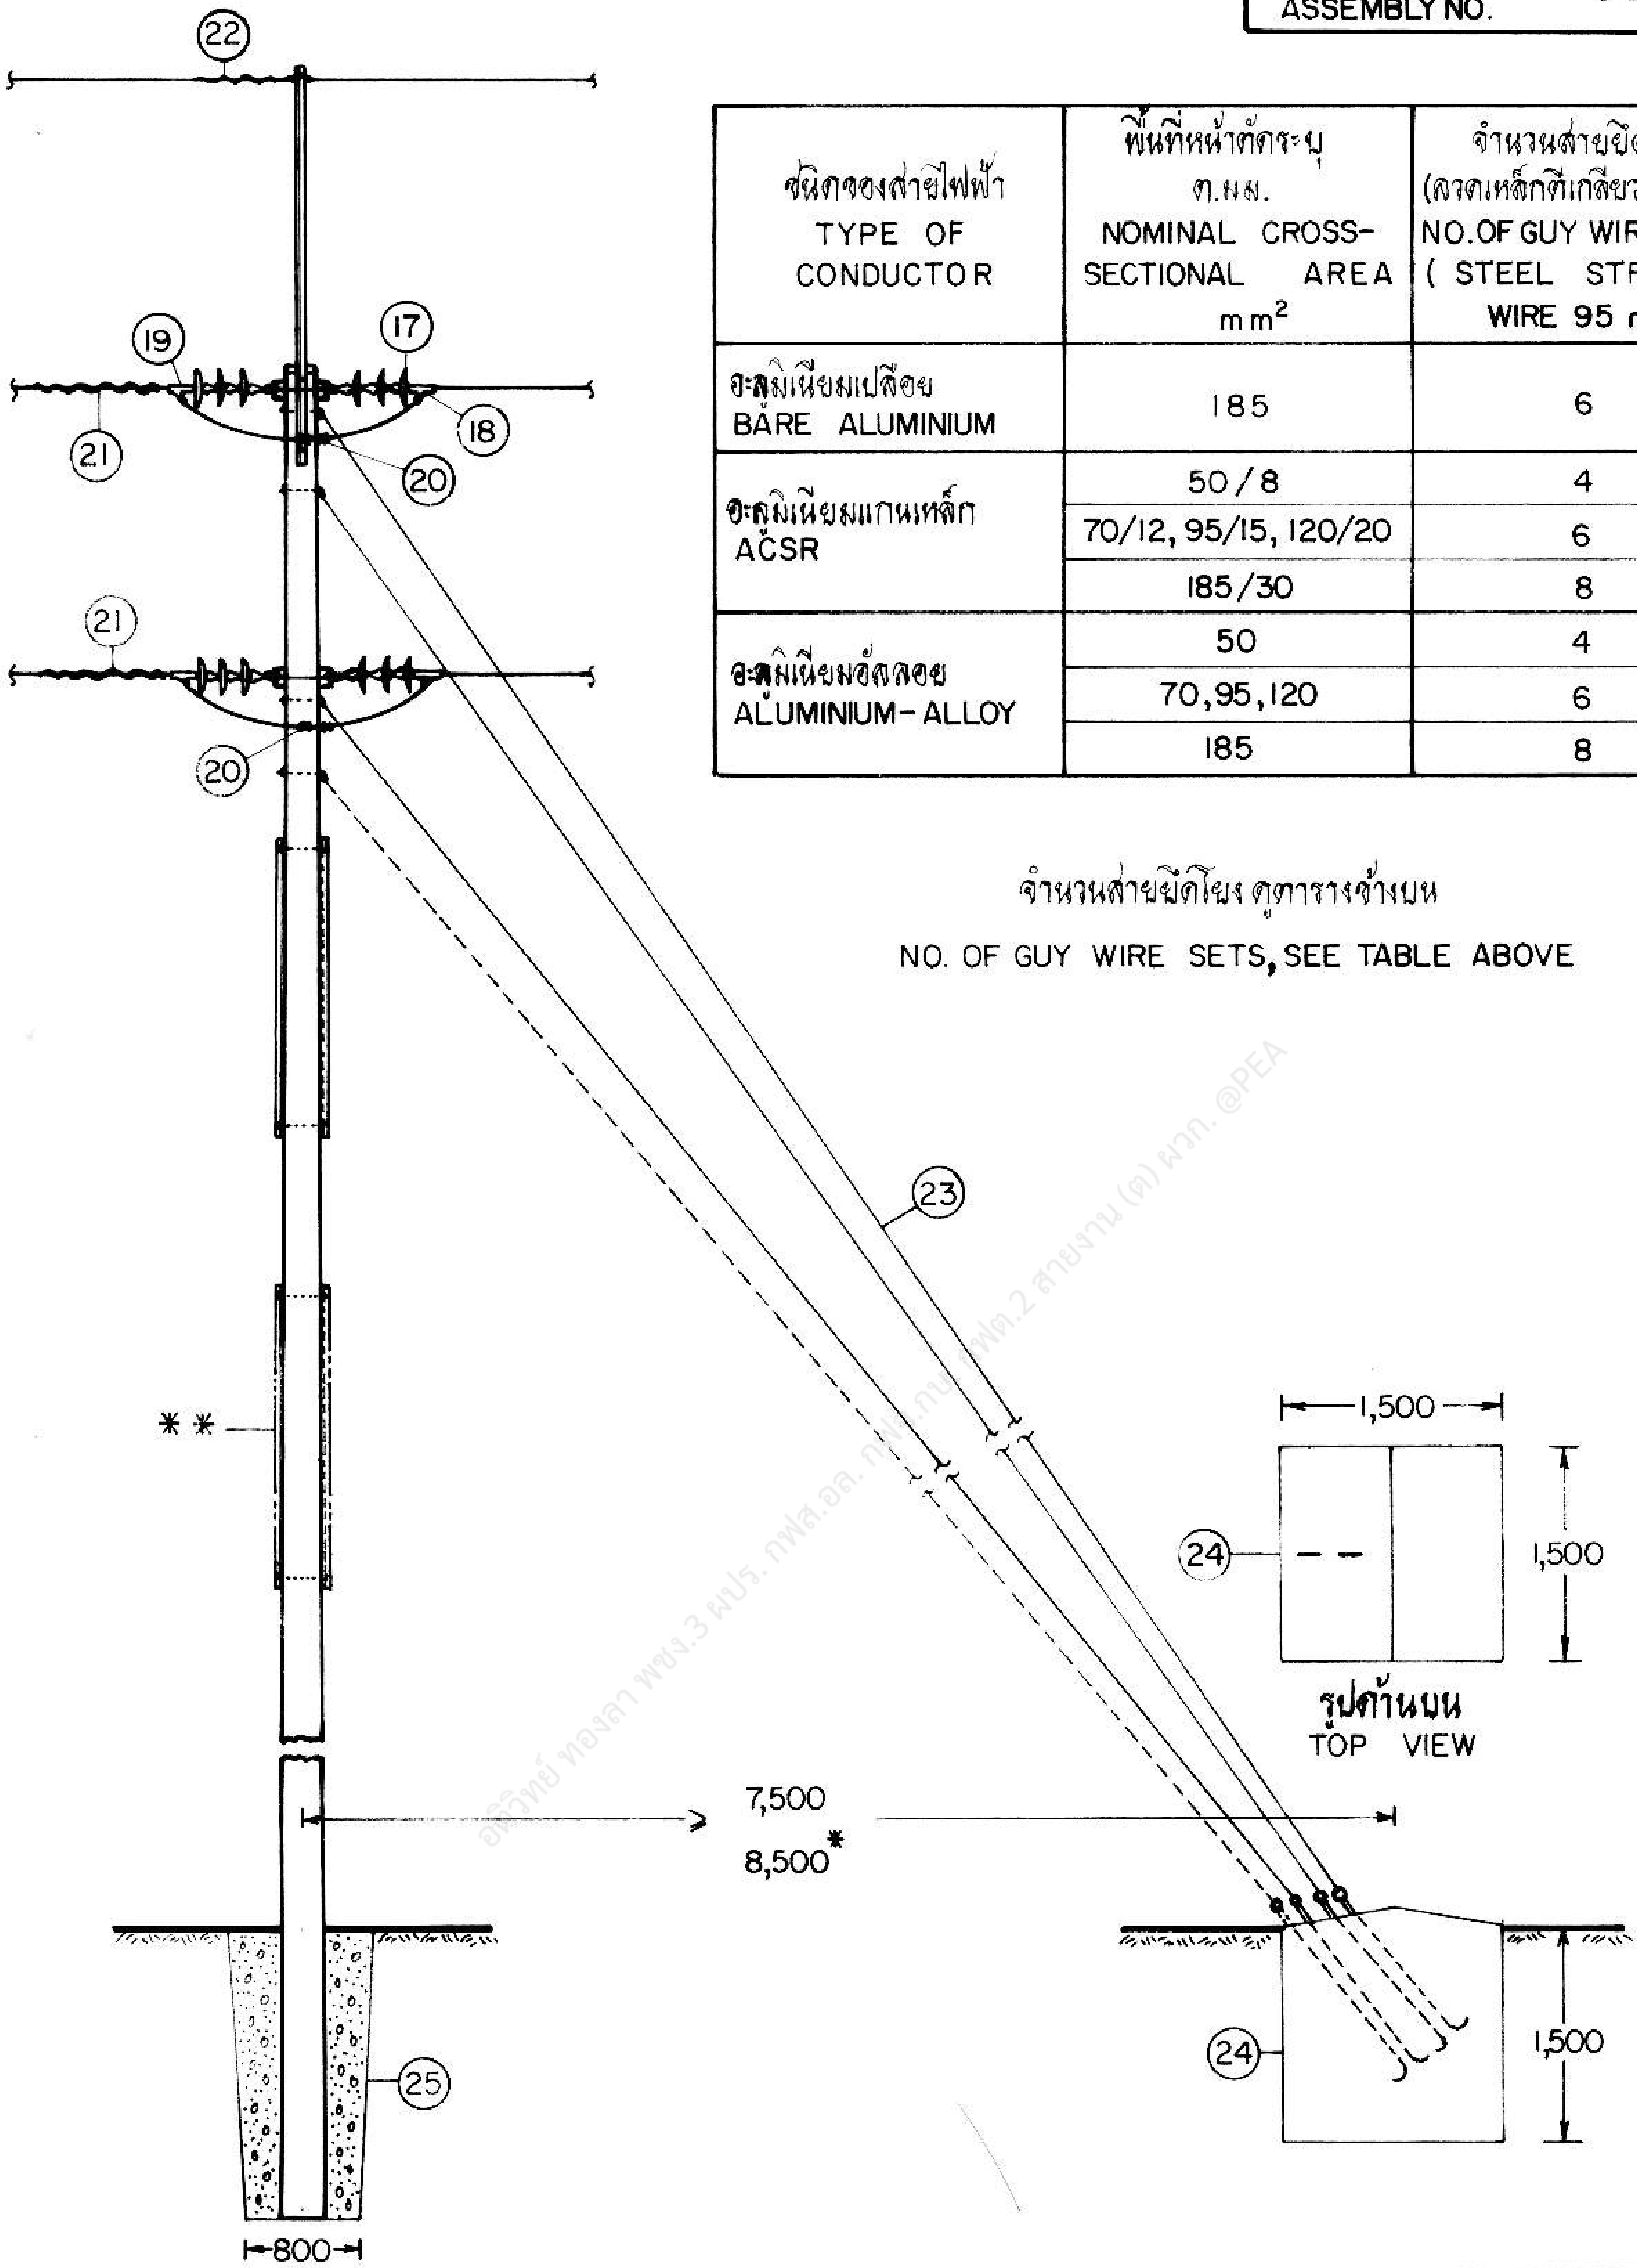

จำนวนสายยึดโยง ดูตารางข้างบน

NO. OF GUY WIRE SETS, SEE TABLE ABOVE

รูปด้านบน
TOP VIEW

อติวิทย์ ทองลา พชง.3 ผปร. กฟส.อล. กฟน. ฝฟต.2 สายงาน (ต) ผวก. @PEA

กองวิศวกรรมไฟฟ้าและเครื่องกล
ฝ่ายวิศวกรรม

ผู้เขียน
ผู้สำรวจ
วิศวกร
หัวหน้าแผนก
ผู้อำนวยการกอง
ผู้อำนวยการฝ่าย

รองผู้ว่าการฝ่ายเทคนิค

การไฟฟ้าส่วนภูมิภาค

ผู้ว่าการ 25 ม.ค. 31

มาตรฐานการก่อสร้างระบบ 33 kV 2 วงจร
ช่วง 120-200 ม.

33 kV, 2 CIRCUIT STANDARD CONSTRUCTION
SPAN 120-200 m

ใช้แทนแบบ
ถูกแทนโดยแบบ
เขียนเสร็จวันที่ 14 ก.ค. 30
แก้แบบวันที่
มิติเป็น มม.
มาตราส่วน 1 : 75

แบบเลขที่ SA1-015/30015
แผ่นที่ 2 ของจำนวน 4 แผ่น

การประกอบเลขที่ ASSEMBLY NO.	3228

บัญชีวัสดุ
BILL OF MATERIAL

ลำดับที่ ITEM	รายละเอียด DESCRIPTION	จำนวน REQ'D		วัสดุเลขที่ MAT. NO.
		I	II	
1	เสาคอนกรีตอัดแรง 14 ม. POLE, PRESTRESSED CONCRETE 14 m	2	-	00010006 (0036)
2	เสาคอนกรีตอัดแรง 16 ม. POLE, PRESTRESSED CONCRETE 16 m	-	2	00010008 (0038)
3	เหล็กรูปรางน้ำ ขนาด 150 X 75 X 6.5 มม. ยาว 4.50 ม. (น้ำหนัก 18.6 กก / ม.) STEEL CHANNEL 150 X 75 X 6.5 mm, 4.50 m LONG (WEIGHT 18.6 kg / m)	4	4	01000302 (0114)
4	เหล็กฉาก ขนาด 75 X 75 X 6 มม. ยาว 3.50 ม. (น้ำหนัก 6.87 กก. / ม.) STEEL ANGLE 75 X 75 X 6 mm, 3.50 m LONG (WEIGHT 6. 87 kg/m)	4 (2)	4 (2)	01010100 (0123)
5	เหล็กฉากรับสายล่อฟ้าทางโค้ง 60 X 60 X 6 มม. ยาว 3,000 และ 2,850 มม. OVERHEAD GROUND WIRE CORNER BAYONET 60 X 60 X 6 mm, 3,000 & 2,850 mm LONG	2	2	01010007 (0129)
6	สลักเกลียว M 16 X 250 มม. BOLT, MACHINE, M 16 X 250 mm	8	6	01110203 (0223)
7	สลักเกลียว M 16 X 300 มม. BOLT, MACHINE, M 16 X 300 mm	4 (0)	6 (2)	01110204 (0224)
8	สลักเกลียว M 16 X 350 มม. BOLT, MACHINE, M 16 X 350 mm	2	2	01110205 (0225)
9	สลักเกลียว M 16 X 400 มม. BOLT, MACHINE, M 16 X 400 mm	2	2	01110206 (0226)
10	สลักเกลียวตลอด M 16 X 400 มม. BOLT, DOUBLE ARMING, M 16 X 400 mm	8 (7)	8 (7)	01120000 (0243)
11	แหวนสี่เหลี่ยมแบน 52 X 52 X 4.5 มม. รู Ø 18 มม. มอก. 258 WASHER, SQUARE, FLAT 52 X 52 X 4.5 mm HOLE Ø 18 mm TIS 258	8 (4)	8 (4)	01180100 (0355)
12	แหวนสปริง M 16 มอก. 259 WASHER, LOCK M 16 TIS 259	4	4	01180301 (0365)
13	นัทรูปห่วง M 16 DIN 582 NUT, EYE M 16 DIN 582	12	12	01180001 (0345)
14	ท่อเหล็กขนาด Ø 20 มม. ความยาวตามต้องการ PIPE, STEEL Ø 20 mm, LENGTH AS REQUIRED	8 (7)	8 (7)	
15	ยูแคล้มป์ สลัก 1 ตัว M 8 CLAMP, SINGLE U-BOLT, M 8	4	4	01230000 (0165)
16	กราวด์วายแคล้มป์ สำหรับไม้คอนสาย GROUND WIRE SUPPORT AND CLAMP, FOR WOOD BAYONET	2	2	01230200 (0297)
17	ลูกถ้วยแขวน มอก.354 แบบ ง (แบบ 52-4) INSULATOR, SUSPENSION TYPE, TIS 354 TYPE D (CLASS 52-4)	36	36	01030100 (0145)
18	สเตรนแคล้มป์ สำหรับสายอะลูมิเนียม ขนาดตามต้องการ CLAMP, STRAIN, FOR Al; SIZE AS REQUIRED	6	6	03110000 03110201
19	สเตรนแคล้มป์ สำหรับสายอะลูมิเนียมแกนเหล็ก ขนาดตามต้องการ CLAMP, STRAIN, FOR ACSR; SIZE AS REQUIRED	6	6	03110000 03110201
20	พี.จี. คอนเนคเตอร์ สำหรับสายอะลูมิเนียมอะลูมิเนียมอัลลอย และอะลูมิเนียมแกนเหล็ก ขนาดตามต้องการ CONNECTOR, PARALLEL GROOVE, FOR Al, Al-ALLOY AND ACSR; SIZE AS REQ'D	12	12	02300103 02300104

กองวิศวกรรมไฟฟ้าและเครื่องกล
ฝ่ายวิศวกรรม

ผู้เขียน
ผู้สำรวจ
วิศวกร
หัวหน้าแผนก
ผู้อำนวยการกอง
ผู้อำนวยการฝ่าย

รองผู้ว่าการฝ่ายเทคนิค

การไฟฟ้าส่วนภูมิภาค

ผู้ว่าการ 25 ม.ค. 31

มาตรฐานการก่อสร้างระบบ 33 kV 2 วงจร
ช่วง 120-200 ม.

33 kV, 2 CIRCUIT STANDARD CONSTRUCTION
SPAN 120-200 m

ใช้แทนแบบ
ถูกแทนโดยแบบ
เขียนเสร็จวันที่ 14 ก.ค. 30
แก้แบบวันที่
มิติเป็น
มาตราส่วน

แบบเลขที่ SAI-015/30015

แผ่นที่ 3 ของจำนวน 4 แผ่น

การประกอบเลขที่
ASSEMBLY NO. 3228

บัญชีวัสดุ
BILL OF MATERIAL

ลำดับที่ ITEM	รายละเอียด DESCRIPTION	จำนวน REQ'D I	 II	วัสดุเลขที่ MAT. NO.
21	สไปแรลไวเบรชั่นแดมเปอร์ สำหรับสายอะลูมิเนียมอัลลอยและอะลูมิเนียมแกนเหล็กขนาดตามต้องการ SPIRAL VIBRATION DAMPER, FOR Al, ALLOY AND ACSR; SIZE AS REQUIRED	6	6	02200101- 02200103
22	สไปแรลไวเบรชั่นแดมเปอร์ สำหรับลวดเหล็กตีเกลียว 25 ต.มม. SPIRAL VIBRATION DAMPER, FOR STEEL STRANDED WIRE 25 mm^2	2	2	02200100 (0903)
23	สายยึดโยง GY-32 (ไม่รวมท่อนไม้) จำนวนที่ต้องการ ดูตารางในแผ่นที่ 2 GUY GY-32 (LOG ANCHOR NOT INCLUDED) QUANTITY SEE TABLE IN SHEET NO. 2			—
24	สมอบกคอนกรีต ขนาด 1.50 X 1.50 X 1.50 ม. (คอนกรีต 1:2:4) CONCRETE ANCHOR 1.50 X 1.50 X 1.50 m (CONCRETE 1:2:4)	2	2	—
25	คอนกรีต 1:3:5 CONCRETE 1:3:5	2.5 ม.^{3} (0) m^3	2.5 ม.^{3} (0) m^3	—

บัญชีวัสดุ ช่อง I สำหรับเสาคอนกรีต 14 ม.
ช่อง II สำหรับเสาคอนกรีต 16 ม.
จำนวนตัวเลขในวงเล็บ สำหรับงานก่อสร้างตามบริเวณภูเขาซึ่งสภาพดินเป็นดินแข็ง ลูกรัง หรือ หิน

หมายเหตุ

1. แบบก่อสร้างนี้ใช้สำหรับพาดสายข้ามแม่น้ำที่มีระยะช่วงเสา 120-200 ม. ส่วนกรณีอื่นให้พิจารณาความเหมาะสมเป็นพิเศษ เฉพาะแห่งไป
2. ระยะช่วงเสาสำหรับสายไฟฟ้า
   อะลูมิเนียมเปลือย ขนาด 185 ต.มม. ระยะช่วงเสาสูงสุด 185 ม.
   อะลูมิเนียมแกนเหล็ก ขนาด 50/8 ต.มม. ระยะช่วงเสาสูงสุด 195 ม.
3. ในกรณีสภาพดินอ่อนให้ใช้เสาตอม่อ หรือฐานคอนกรีตสำหรับเสาไฟฟ้า โดยพิจารณาเฉพาะแห่งให้เหมาะสมกับสภาพพื้นที่

NOTES

1. THIS CONSTRUCTION SHALL BE USED FOR CROSSING THE RIVER, HAVING LONG SPAN OF 120-200 m; ANOTHER CASE SHALL BE SPECIALLY CONSIDERED AT EACH LOCATION.
2. LIMIT SPAN FOR CONDUCTORS
   BARE Al CONDUCTOR 185 mm^2, MAXIMUM SPAN 185 m
   ACSR 50/8 mm^2, MAXIMUM SPAN 195 m
3. FOR BAD SOIL CONDITION, STUB POLE OR CONCRETE FOUNDATION FOR CONCRETE POLE SHALL BE USED ACCORDING TO THE SOIL CONDITION AT THAT LOCATION.

กองวิศวกรรมไฟฟ้าและเครื่องกล
ฝ่ายวิศวกรรม
ผู้เขียน
ผู้สำรวจ
วิศวกร
หัวหน้าแผนก
ผู้อำนวยการกอง
ผู้อำนวยการฝ่าย
รองผู้ว่าการฝ่ายเทคนิค

การไฟฟ้าส่วนภูมิภาค

ผู้ว่าการ 25 ม.ค. 31.

มาตรฐานการก่อสร้างระบบ 33 kV 2 วงจร
ช่วง 120-200 ม.

33 kV, 2 CIRCUIT STANDARD CONSTRUCTION
SPAN 120-200 m

ใช้แทนแบบ
ถูกแทนโดยแบบ
เขียนเสร็จวันที่
แก้แบบวันที่ 14 ก.ค. 30
มิติเป็น
มาตราส่วน
แบบเลขที่ SAI-015/30015
แผ่นที่ 4 จากจำนวน 4 แผ่น