การประกอบเลขที่ ASSEMBLY NO. 3701 C

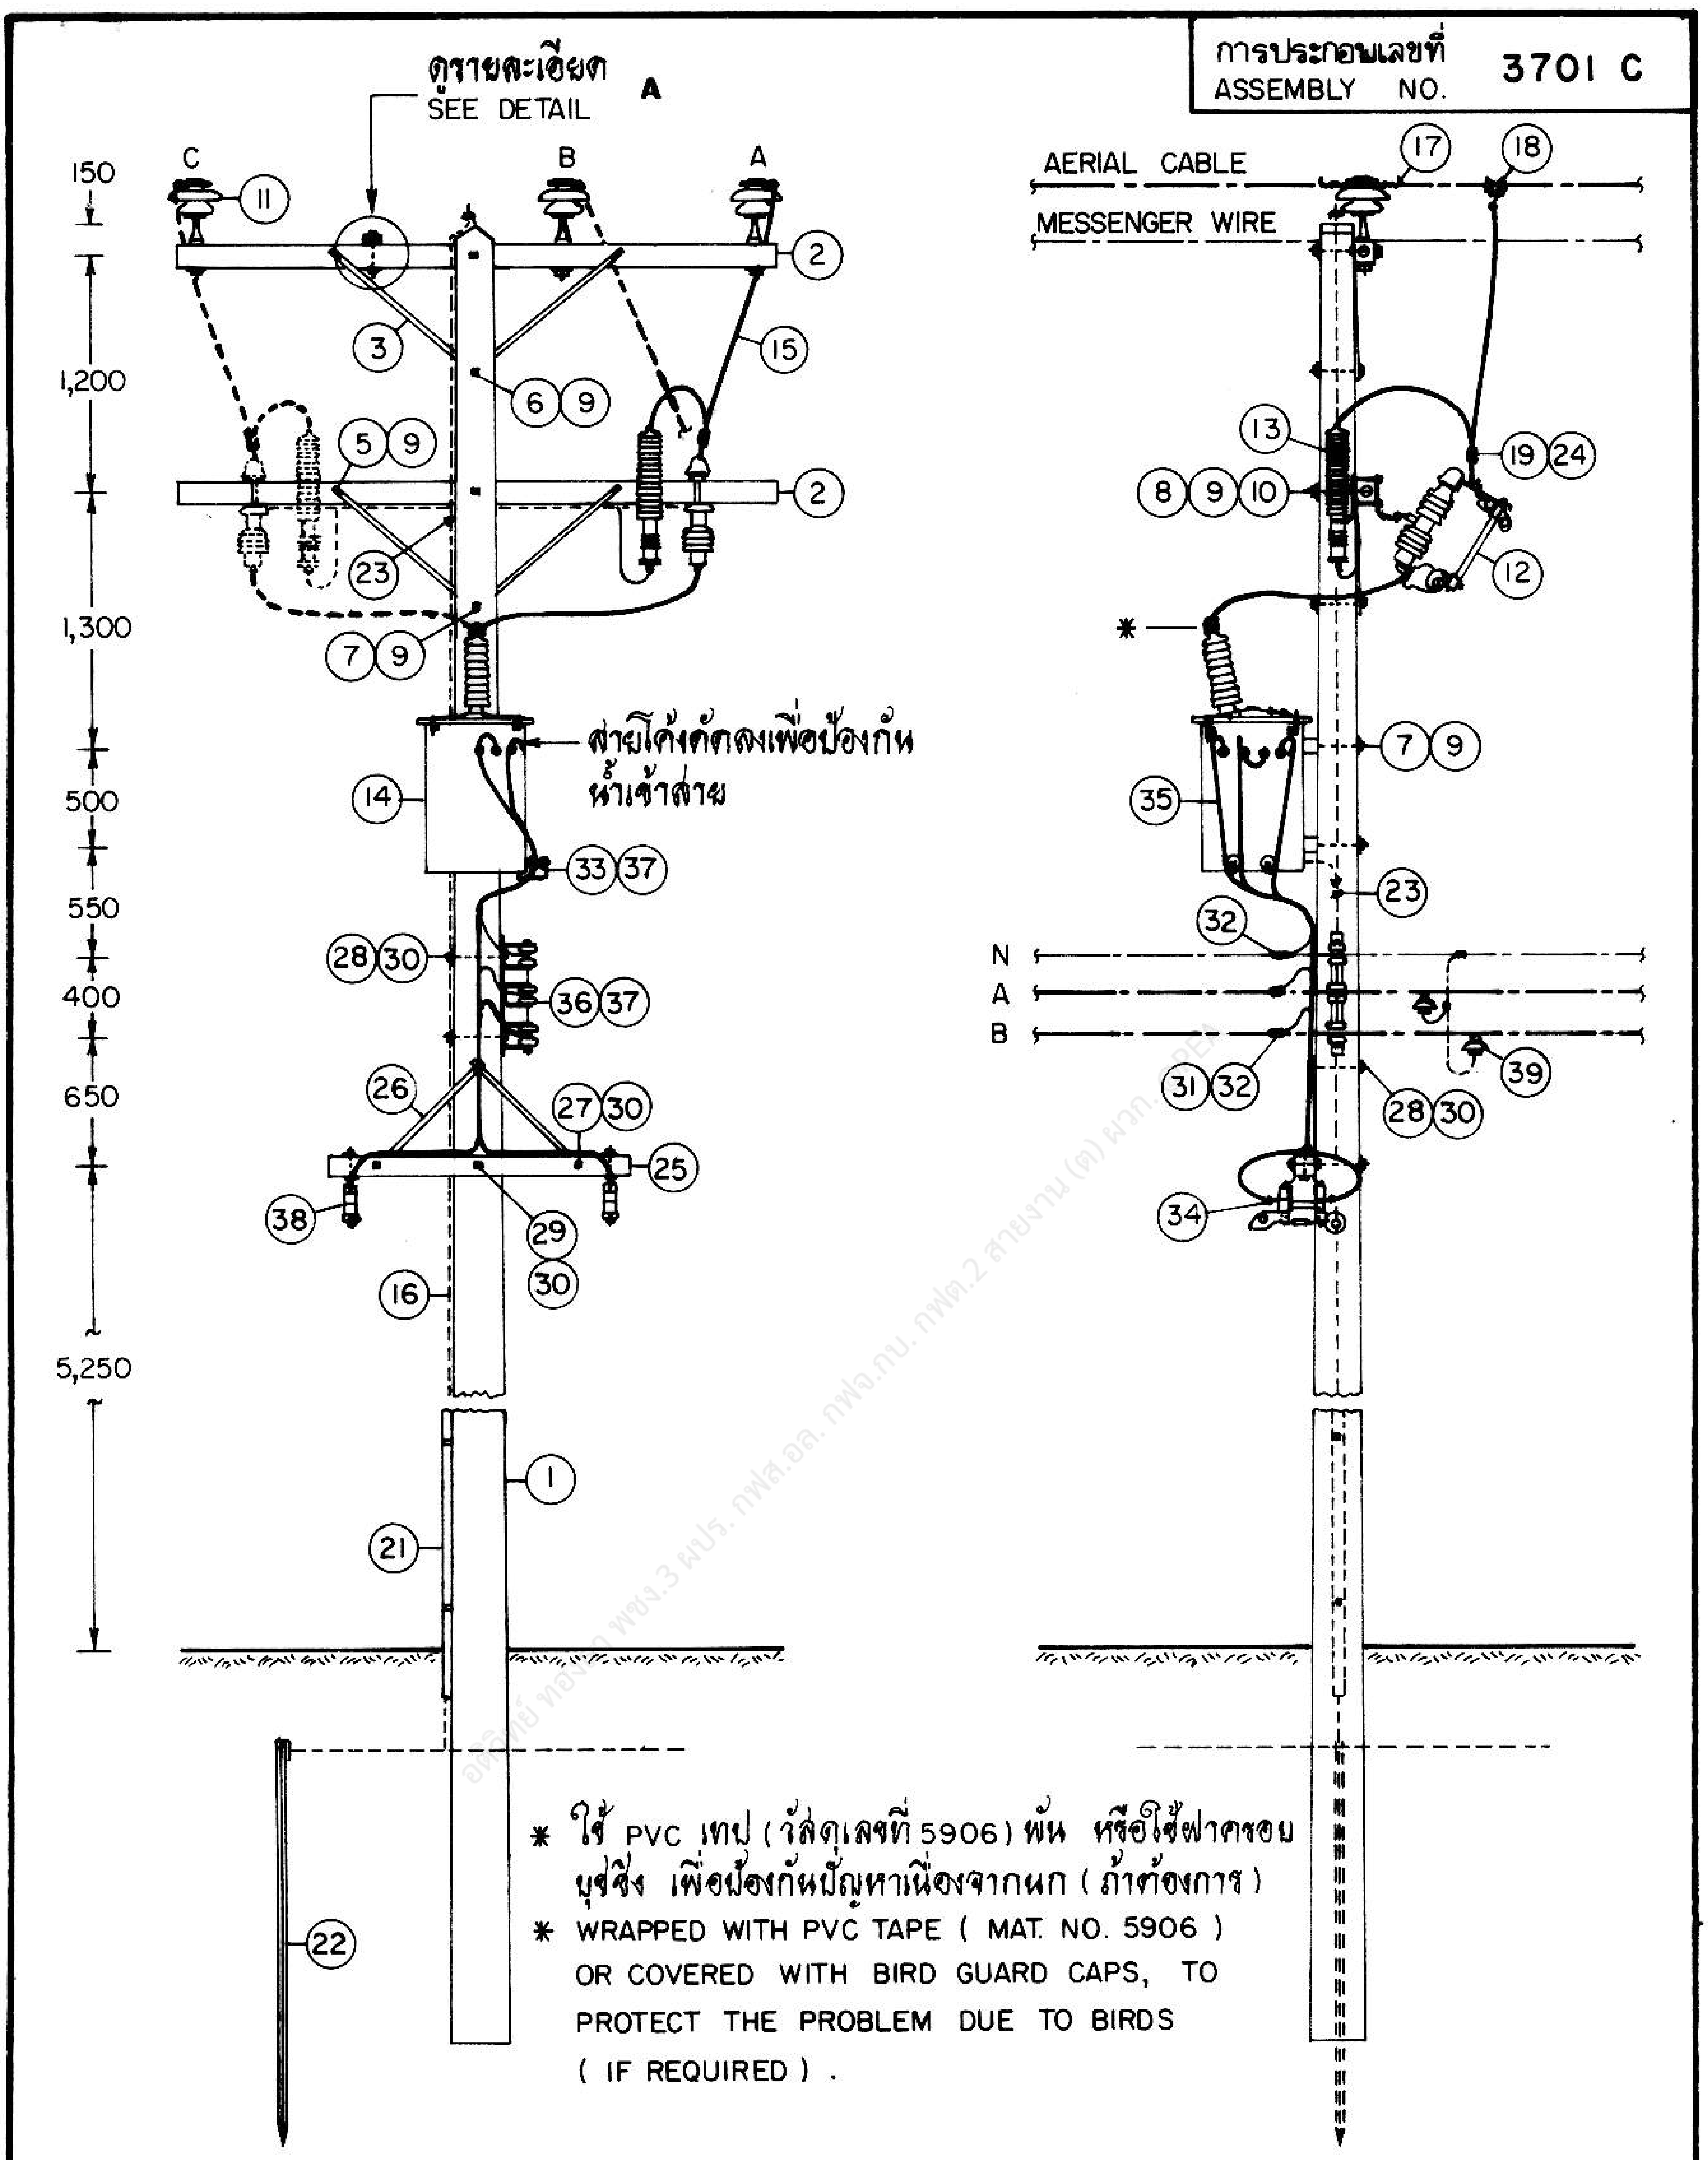

* ใช้ PVC เทป (วัสดุเลขที่ 5906) พัน หรือใช้ฝาครอบ
บุชชิ่ง เพื่อป้องกันปัญหาเนื่องจากนก (ถ้าต้องการ)

* WRAPPED WITH PVC TAPE (MAT. NO. 5906)
OR COVERED WITH BIRD GUARD CAPS, TO
PROTECT THE PROBLEM DUE TO BIRDS
(IF REQUIRED) .

พชง.3 ผปร. กฟส.อล. กฟจ.กบ. กฟต.2 สายงาน (ต) ผวก. PEA

กองวิศวกรรมไฟฟ้าและเครื่องกล
ฝ่ายวิศวกรรม

ผู้เขียน
ผู้สำรวจ
วิศวกร
หัวหน้าแผนก
ผู้อำนวยการกอง
ผู้อำนวยการฝ่าย

รองผู้ว่าการฝ่ายเทคนิค

การไฟฟ้าส่วนภูมิภาค

ผู้ว่าการ 30 มิ.ย. 31

การติดตั้งหม้อแปลงซิงเกิลบุชชิ่ง 19 kV
กรณีสายเมนเป็นเคเบิ้ลอากาศ
(I สำหรับคอนแขนธรรมดา)

19 kV SINGLE BUSHING TRANSFORMER INSTALLATION
H.T. AERIAL CABLE PRIMARY MAIN LINE
(I FOR CROSSARM)

ใช้แทนแบบ
ถูกแทนโดยแบบ
เขียนเสร็จวันที่ 17 มี.ค. 31
แก้แบบวันที่ 4 ก.ย. 35
มิติเป็น มม.
มาตราส่วน 1 : 50

แบบเลขที่ SAI-015/31011
แผ่นที่ 1 ของจำนวน 6 แผ่น

~~29 ส.ค. 2531~~

การประกอบเลขที่
ASSEMBLY NO. **3701 C**

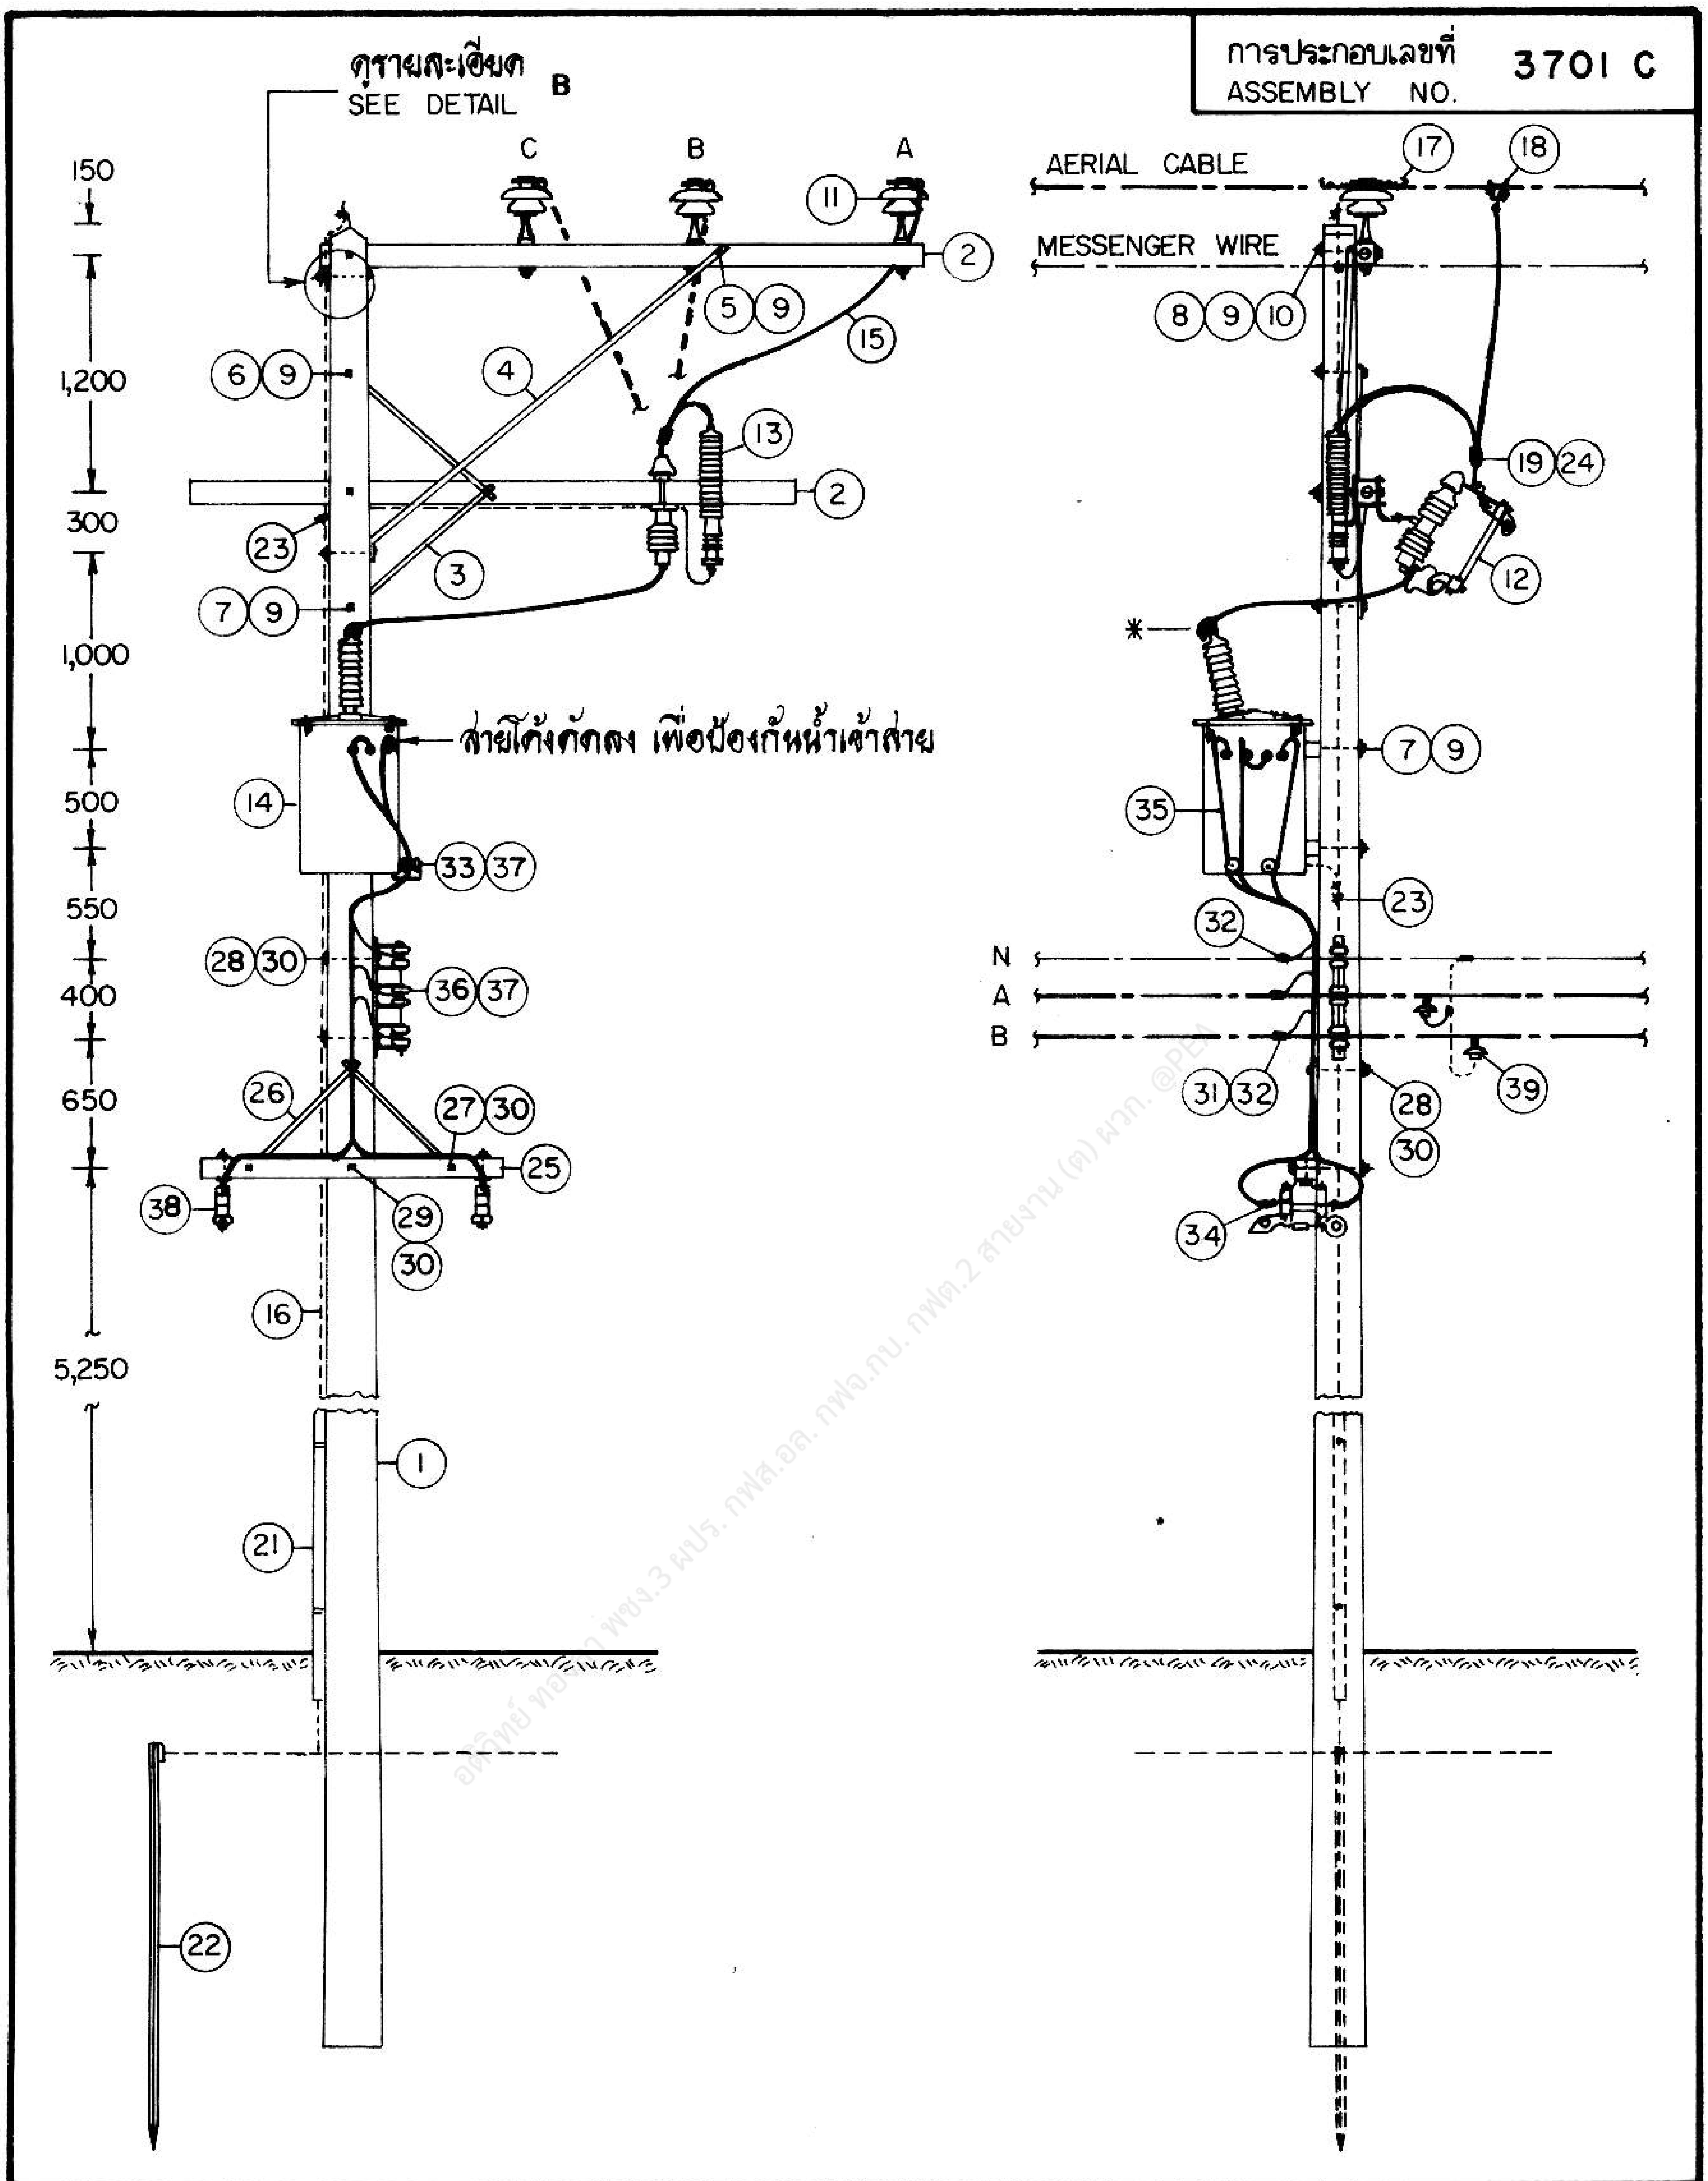

อดิทิพย์ ทอง[illegible] พชง.3 ผปร. กฟส.อล. กฟจ.กบ. กฟต.2 สายงาน (ต) ผวก. @PEA

กองวิศวกรรมไฟฟ้าและเครื่องกล
ฝ่ายวิศวกรรม
ผู้เขียน
ผู้สำรวจ
วิศวกร
หัวหน้าแผนก
ผู้อำนวยการกอง
ผู้อำนวยการฝ่าย
รองผู้ว่าการฝ่ายเทคนิค

การไฟฟ้าส่วนภูมิภาค

ผู้ว่าการ 30 มี.ค. 31

การติดตั้งหม้อแปลงซิงเกิลบุชชิ่ง 19 kV
กรณีสายเมนเป็นเคเบิลอากาศ
(II สำหรับคอนแบบท้าวแขน)

19 kV SINGLE BUSHING TRANSFORMER INSTALLATION
H.T. AERIAL CABLE PRIMARY MAIN LINE
(II FOR ALLEY ARM)

ใช้แทนแบบ
ถูกแทนโดยแบบ
เขียนเสร็จวันที่ 17 มี.ค. 31
แก้แบบวันที่ 4 ก.ย. 35
มิติเป็น มม.
มาตราส่วน 1 : 50
แบบเลขที่ SAI-015/31011
แผ่นที่ 2 ของจำนวน 6 แผ่น

29 ส.ค. 2531

การประกอบเลขที่ ASSEMBLY NO. **3701 C**

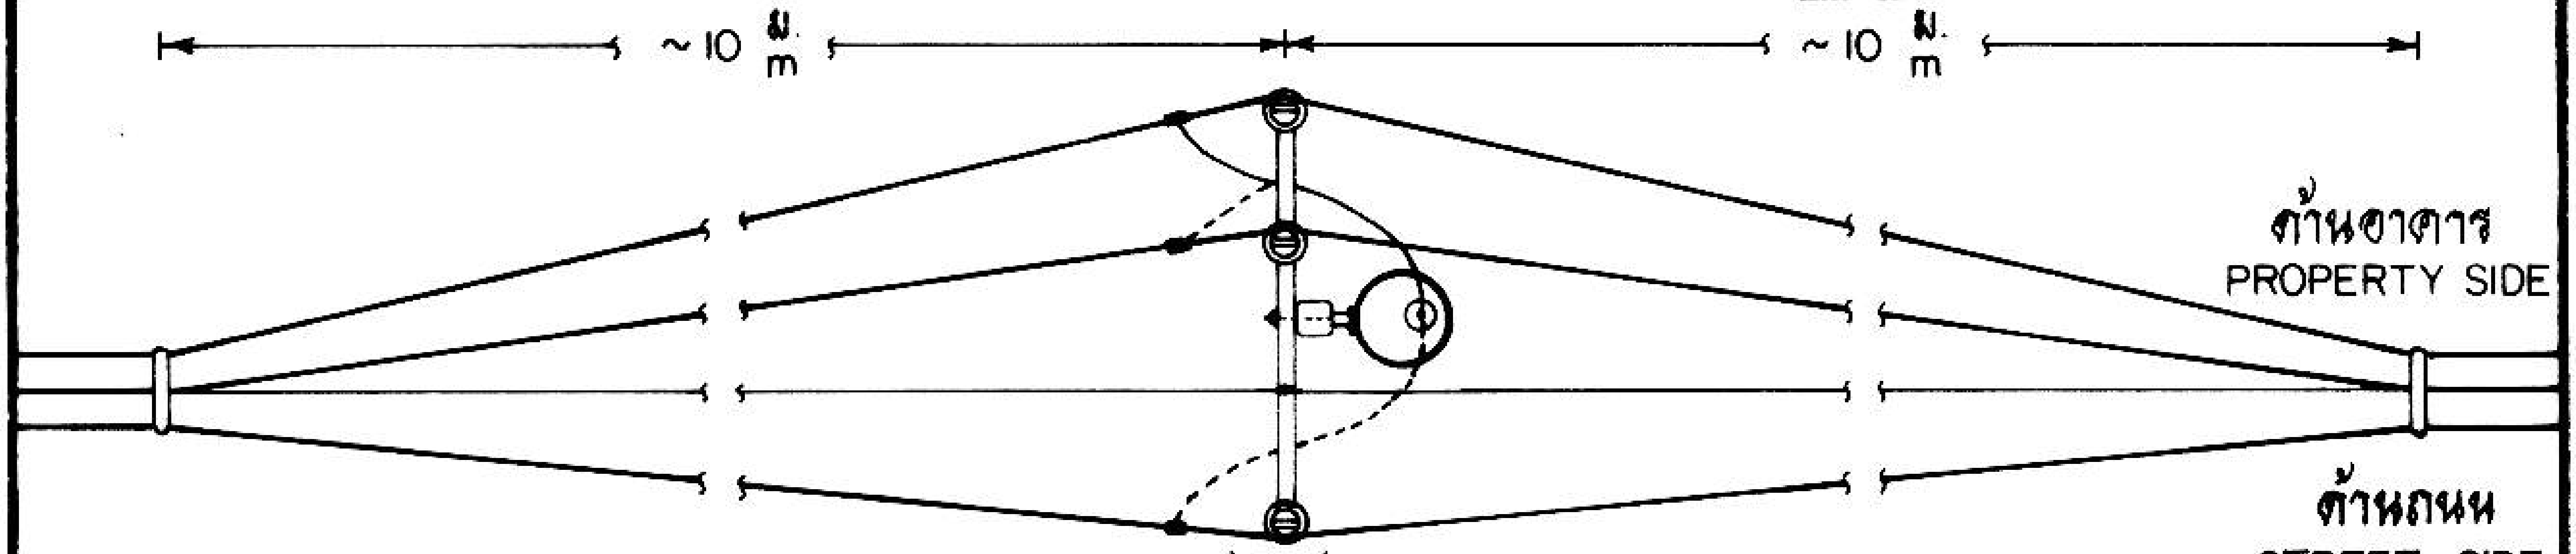

แบบ TYPE I สำหรับคอนแบบธรรมดา FOR CROSSARM

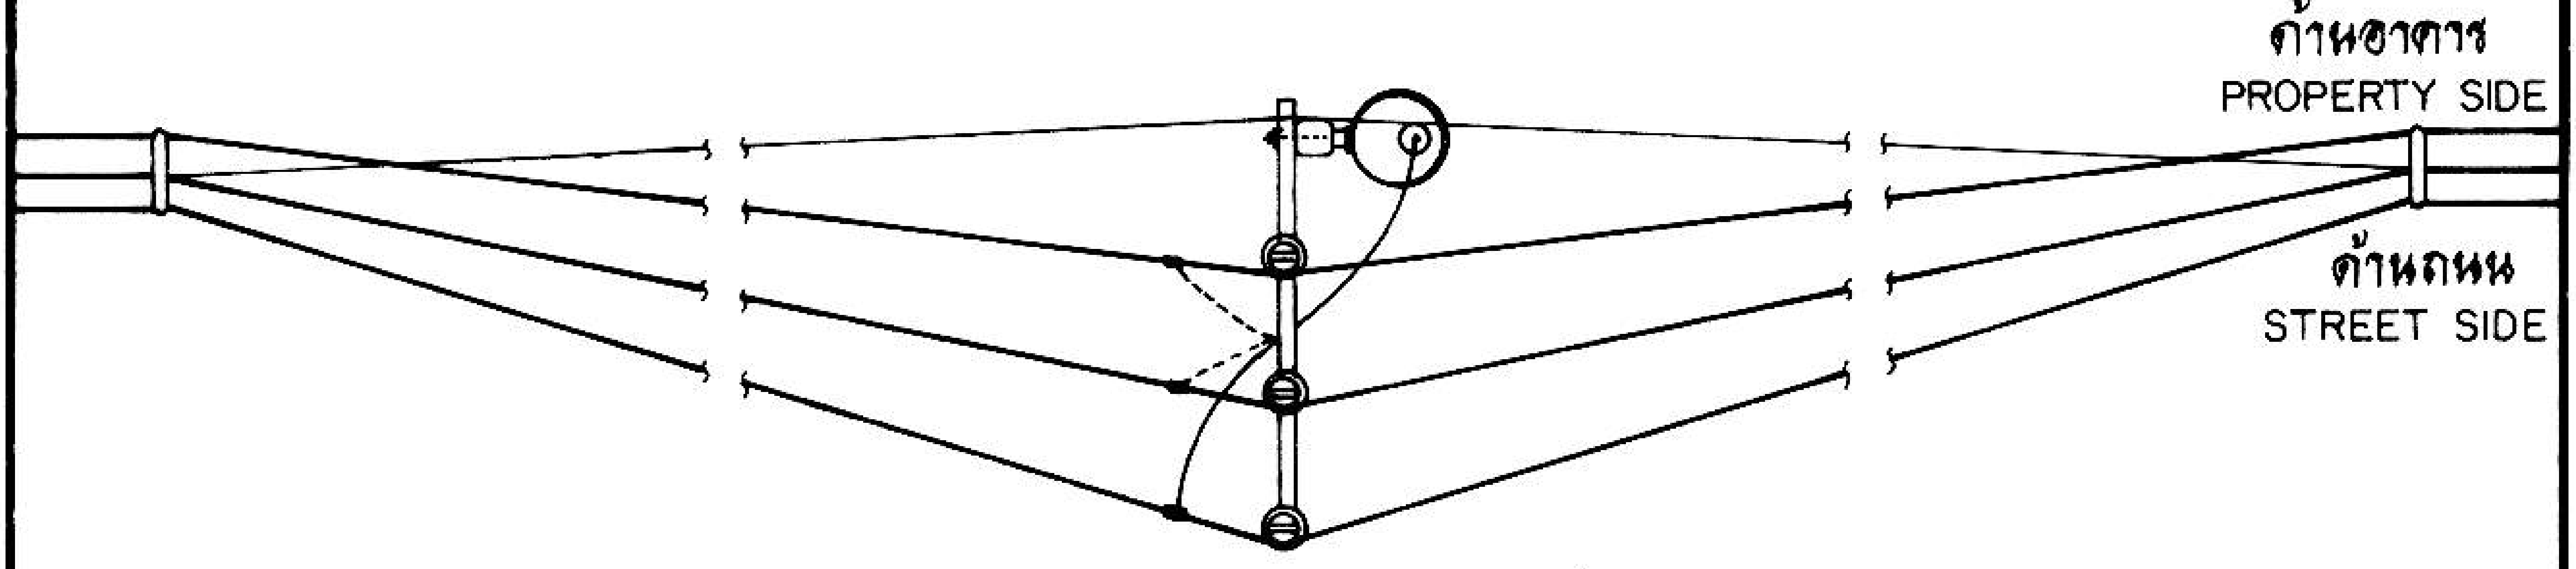

แบบ TYPE II สำหรับคอนแบบท้าวแขน FOR ALLEY ARM

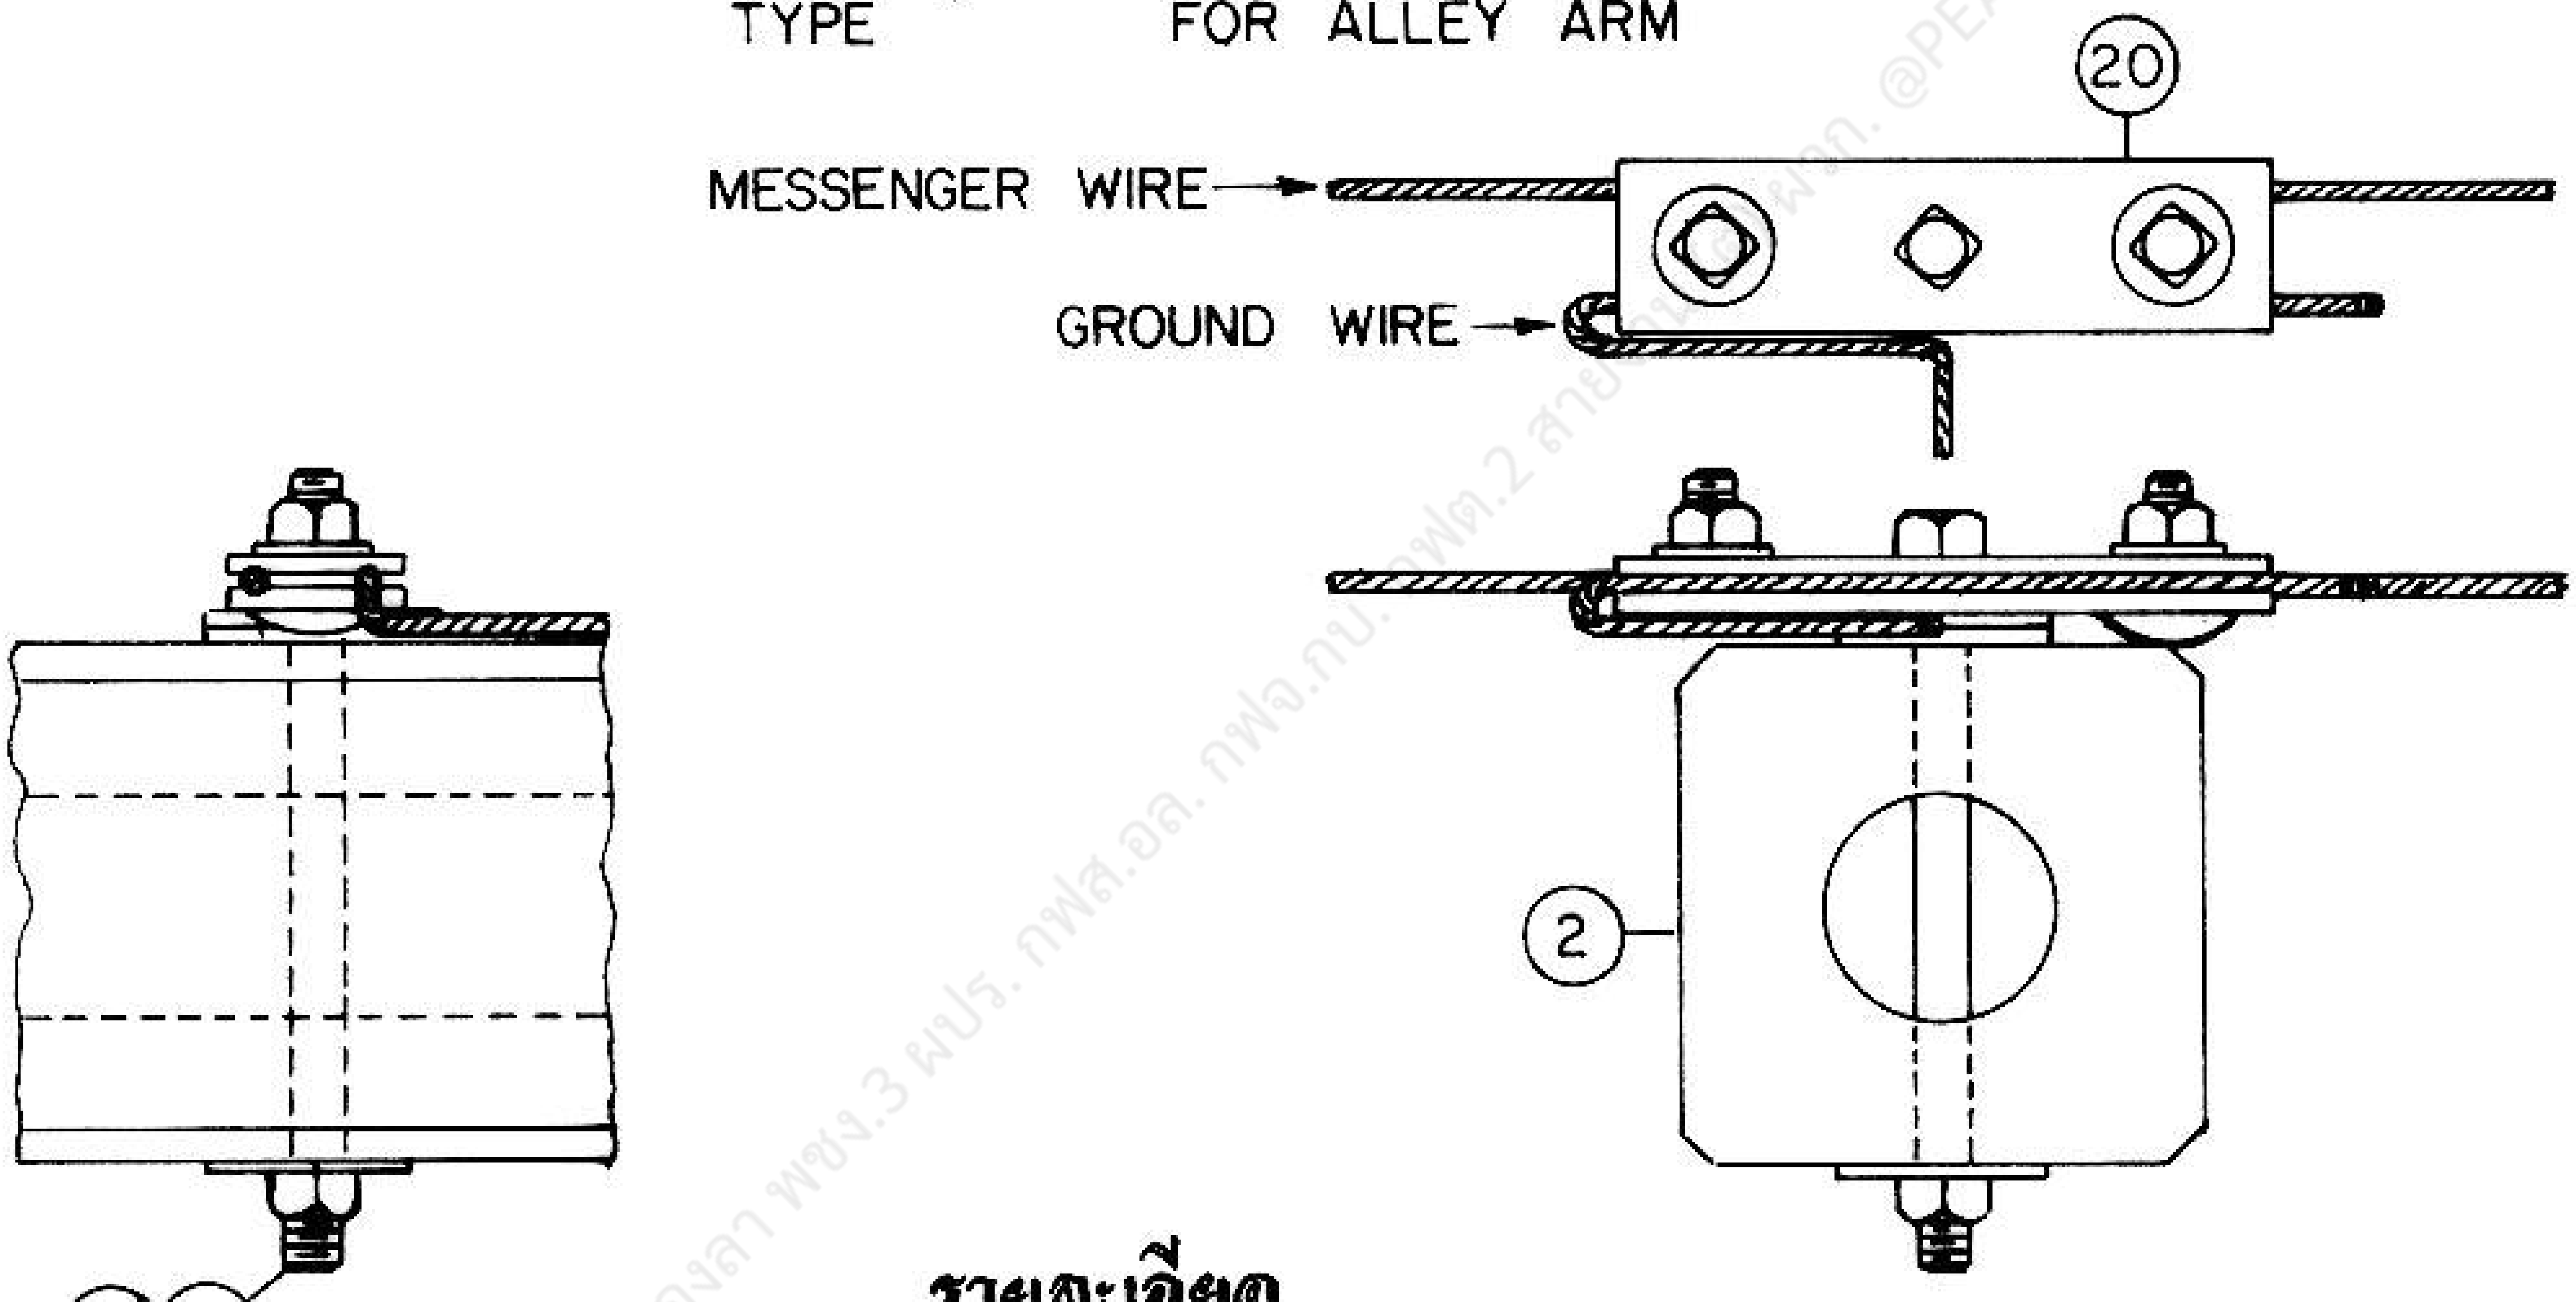

รายละเอียด DETAIL A

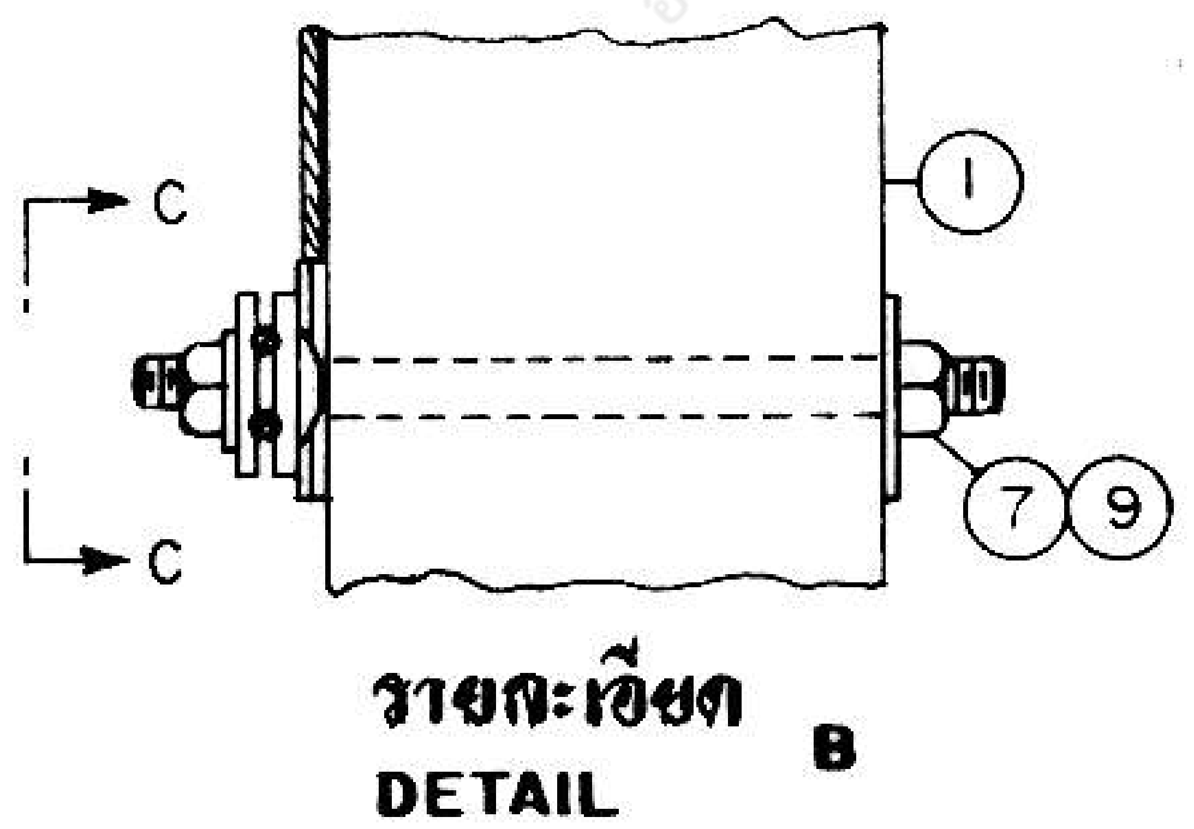

รายละเอียด DETAIL B

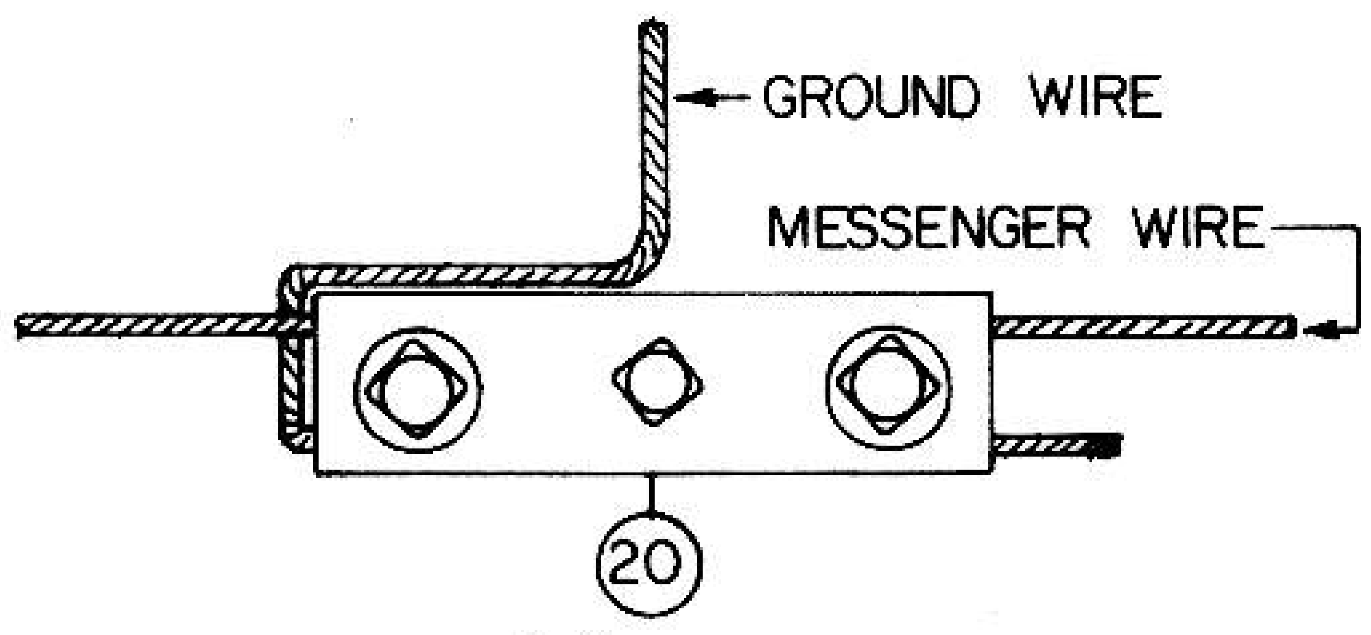

รูปตัด SECTION C–C

อดิวิทย์ ทองลา พชง.3 ผปร. กฟส.อล. กฟจ.กบ. กฟต.2 สาย[illegible] @PEA

กองวิศวกรรมไฟฟ้าและเครื่องกล
ฝ่ายวิศวกรรม
ผู้เขียน
ผู้สำรวจ
วิศวกร
หัวหน้าแผนก
ผู้อำนวยการกอง
ผู้อำนวยการฝ่าย
รองผู้ว่าการฝ่ายเทคนิค

การไฟฟ้าส่วนภูมิภาค

ผู้ว่าการ 30 ส.ค. 31

การติดตั้งหม้อแปลงซิงเกิลบูชชิ่ง 19 kV
กรณีสายเมนเป็นเคเบิลอากาศ

19 kV SINGLE BUSHING TRANSFORMER INSTALLATION
H.T. AERIAL CABLE PRIMARY MAIN LINE

ใช้แทนแบบ
ถูกแทนโดยแบบ
เขียนเสร็จวันที่ 17 ส.ค. 31
แก้แบบวันที่ 4 ก.ย. 35
มิติเป็น
มาตราส่วน
แบบเลขที่ SA1-015/31011
แผ่นที่ 3 ของจำนวน 6 แผ่น

29 ส.ค. 2531

การประกอบเลขที่ 3701 C
ASSEMBLY NO. 3701 C

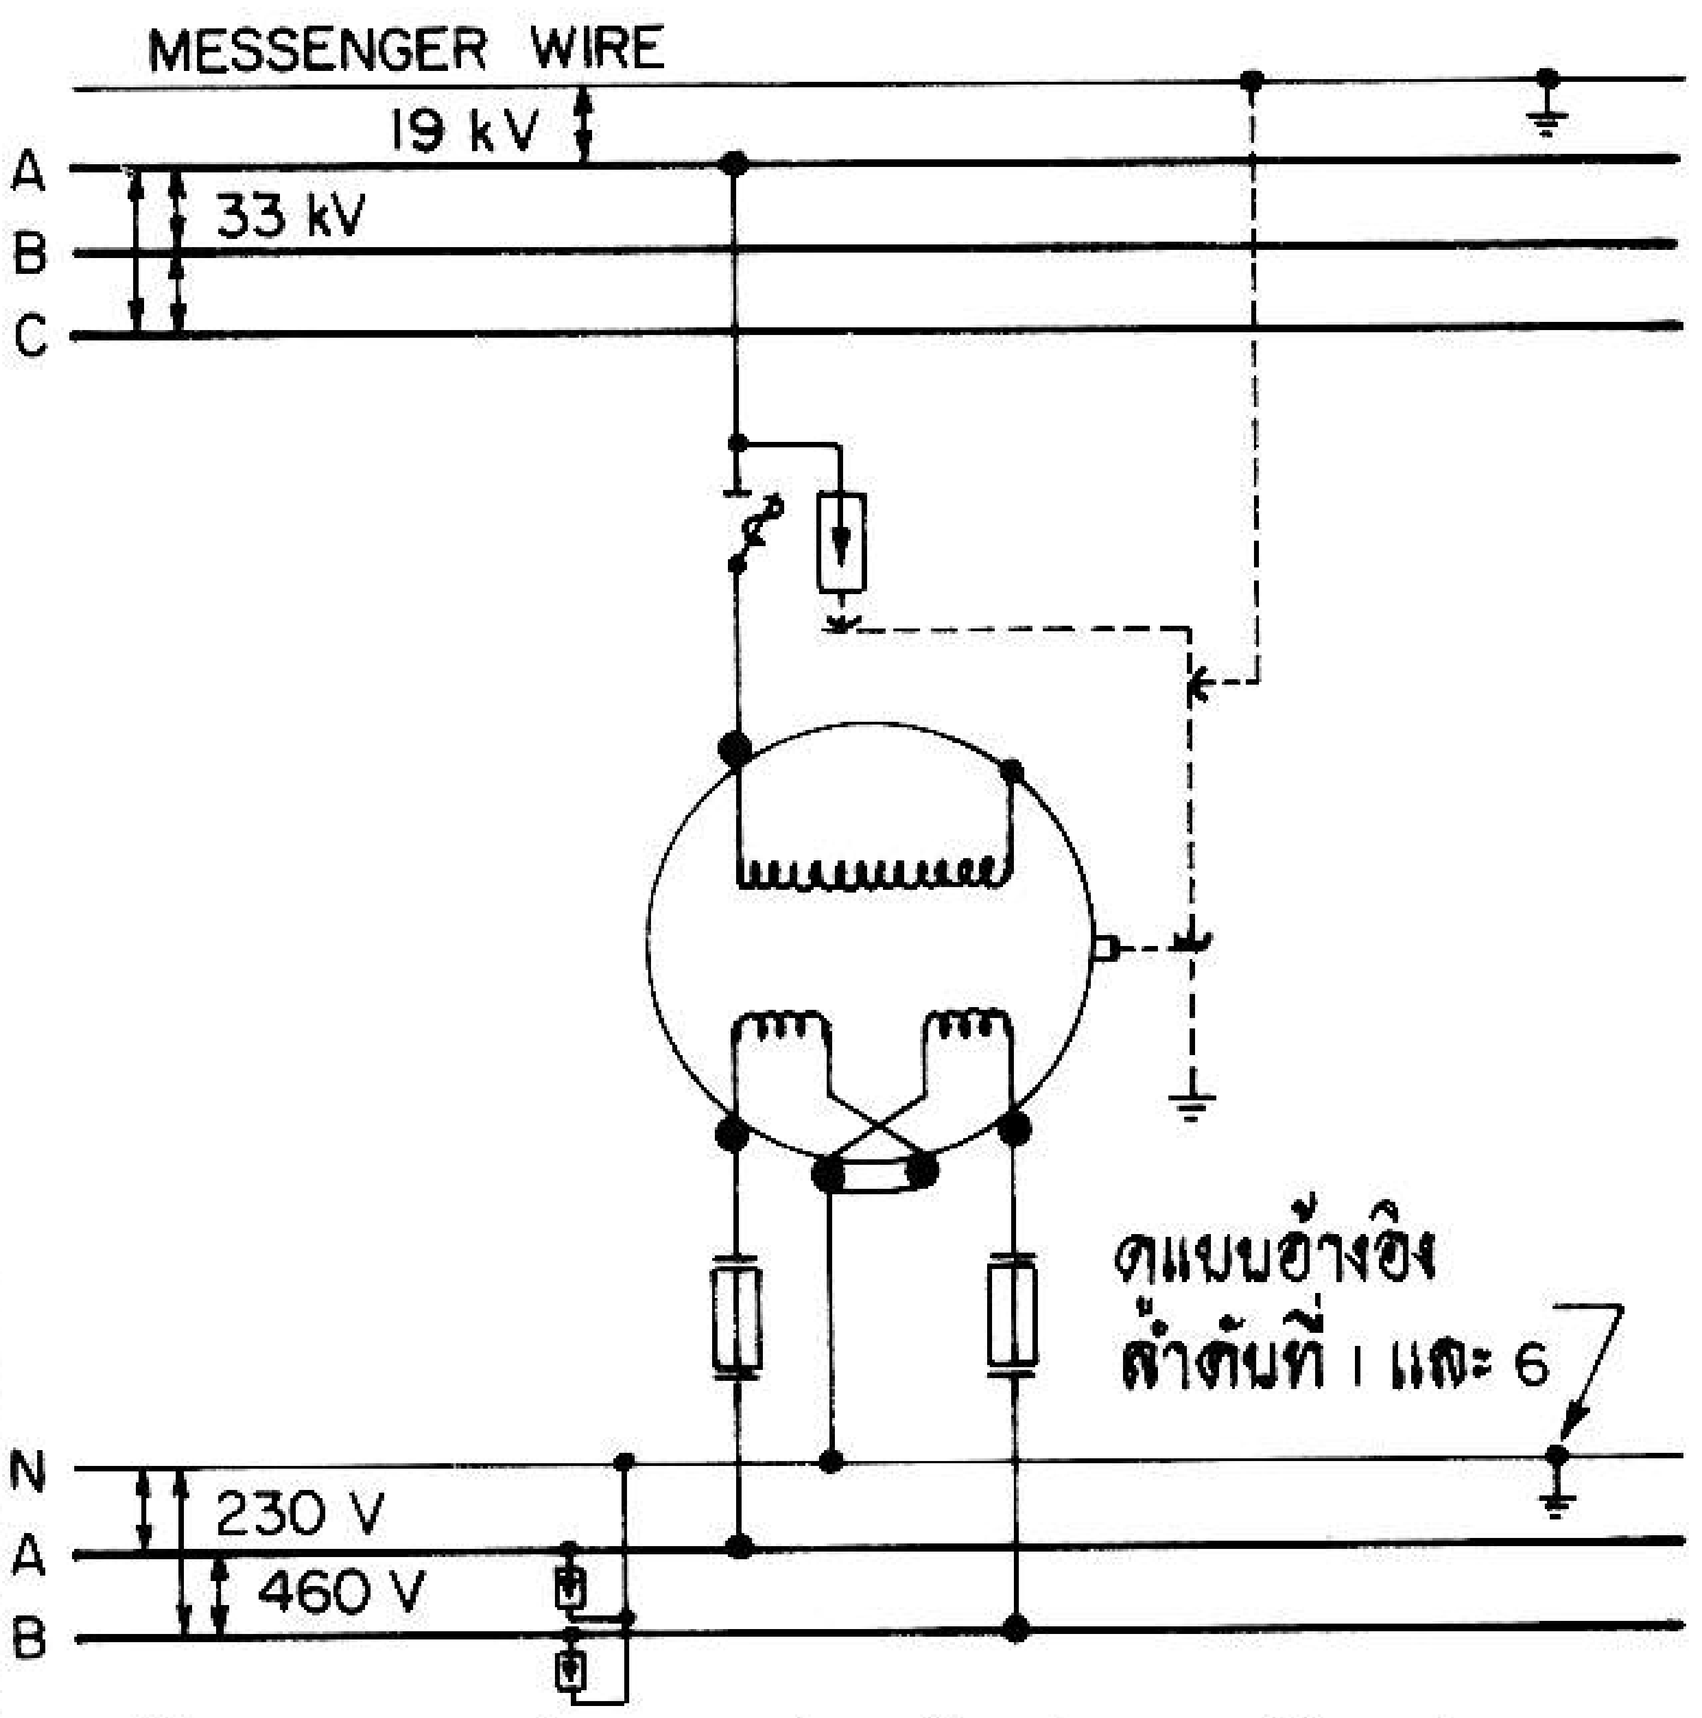

ไดอะแกรมแสดงการต่อหม้อแปลง 1 เฟส 3 สาย
1-PHASE 3-WIRE TRANSFORMER WIRING DIAGRAM

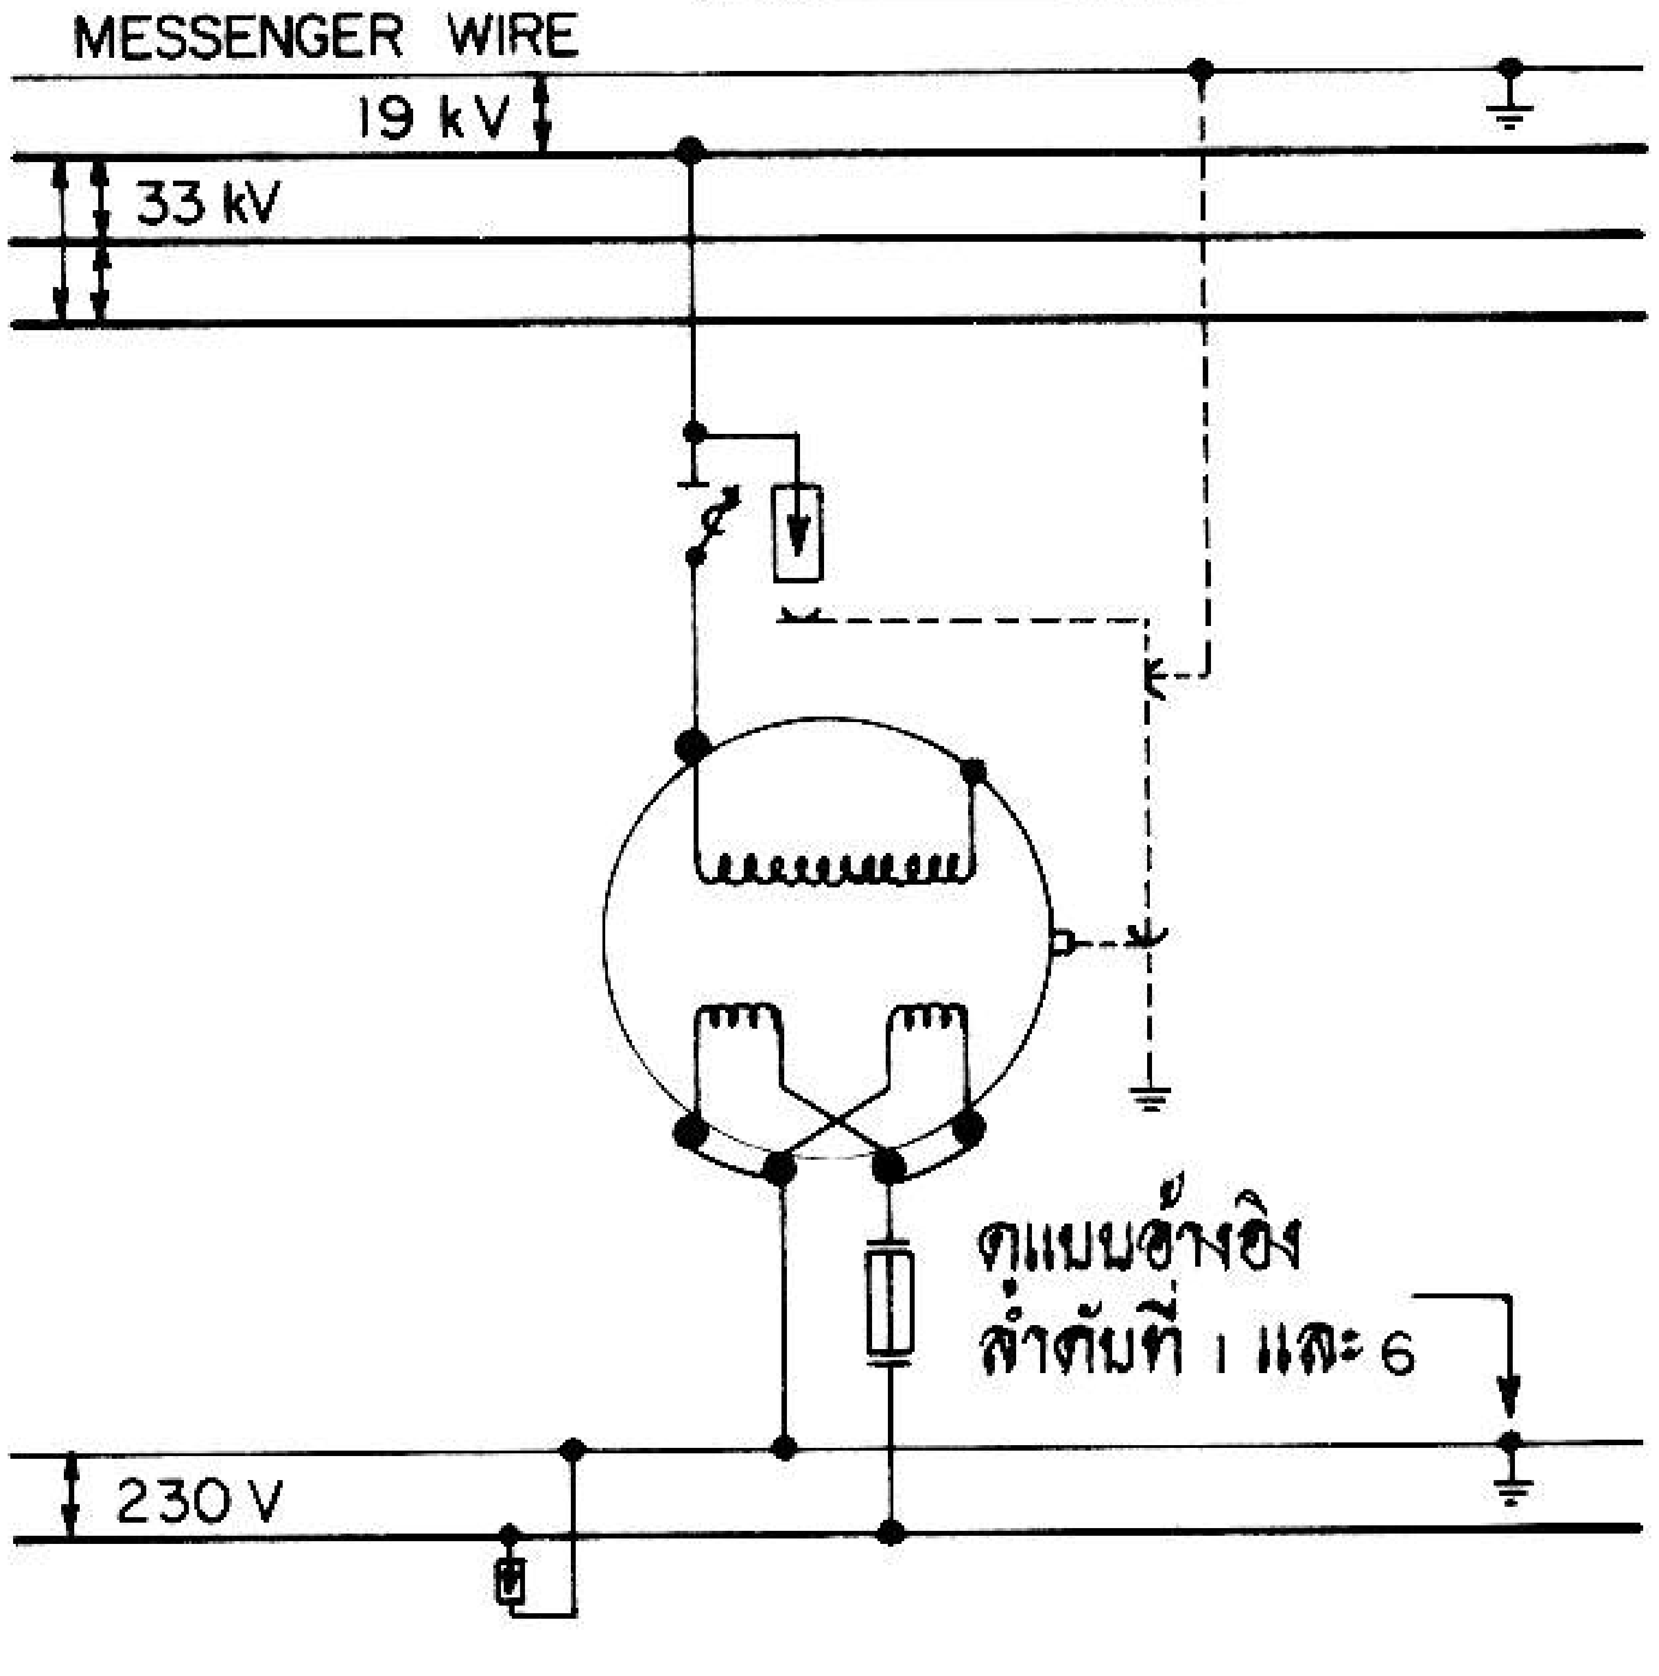

ไดอะแกรมแสดงการต่อหม้อแปลง 1 เฟส 2 สาย
1-PHASE 2-WIRE TRANSFORMER WIRING DIAGRAM

บัญชีวัสดุ
BILL OF MATERIAL

ลำดับที่ ITEM	รายละเอียด DESCRIPTION	จำนวน REQ'D		วัสดุเลขที่ MAT. NO.
		I	II	
1	เสาคอนกรีต 12 ม. POLE, CONCRETE 12 m LONG	1	1	00010003
2	คอน คอร. สปัน ขนาด 120 X 120 X 3,000 มม. CROSSARM, SPUN PRESTRESSED CONCRETE, 120 X 120 X 3,000 mm	2	2	00110002
3	เหล็กประกับคอน 40 X 6 X 1,000 มม. BRACE, FLAT, FOR CROSSARM, 40 X 6 X 1,000 mm	4	2	01200002
4	เหล็กประกับคอนแบบท้าวแขน 50 X 50 X 5 มม. ยาว 2,350 มม. BRACE, ALLEY ARM, 50 X 50 X 5 mm, 2,350 mm LONG	-	1	01200005
5	สลักเกลียว M 16 X 170 มม. BOLT, MACHINE, M 16 X 170 mm	4	2	01110201
6	สลักเกลียว M 16 X 200 มม. BOLT, MACHINE, M 16 X 200 mm	2	1	01110202
7	สลักเกลียว M 16 X 250 มม. BOLT, MACHINE, M 16 X 250 mm	3	5	01110203
8	สลักเกลียว M 16 X 350 มม. BOLT, MACHINE, M 16 X 350 mm	2	2	01110205
9	แหวนสี่เหลี่ยมแบน 52 X 52 X 4.5 มม. รู Ø 18 มม. มอก. 258 WASHER, SQUARE, FLAT, 52 X 52 X 4.5 mm, HOLE Ø 18 mm, TIS 258	15	14	01180100
10	แหวนสปริง M 16 มอก. 259 WASHER, LOCK, M 16, TIS 259	2	2	01180301

กองวิศวกรรมไฟฟ้าและเครื่องกล
ฝ่ายวิศวกรรม

ผู้เขียน
ผู้สำรวจ
วิศวกร
หัวหน้าแผนก
ผู้อำนวยการกอง
ผู้อำนวยการฝ่าย
รองผู้ว่าการฝ่ายเทคนิค

29 มี.ค. 2531

การไฟฟ้าส่วนภูมิภาค

ผู้ว่าการ 30 มี.ค. 31

การติดตั้งหม้อแปลงซิงเกิลบุชชิ่ง 19 kV
กรณีสายเมนเป็นเคเบิลอากาศ

19 kV SINGLE BUSHING TRANSFORMER INSTALLATION
H.T. AERIAL CABLE PRIMARY MAIN LINE

ใช้แทนแบบ
ถูกแทนโดยแบบ
เขียนเสร็จวันที่ 17 มี.ค. 31
แก้แบบวันที่ 4 ก.ย. 35
มิติเป็น
มาตราส่วน
แบบเลขที่ SAI-015/31011
แผ่นที่ 4 ของจำนวน 6 แผ่น

การประกอบเลขที่
ASSEMBLY NO. 3701 C

บัญชีวัสดุ
BILL OF MATERIAL

ลำดับที่ ITEM	รายละเอียด DESCRIPTION	จำนวน REQ'D I	II	วัสดุเลขที่ MAT. NO.
11	ลูกถ้วยก้านตรง 33 kV มอก. 279 แบบ ค (แบบ 56-3) พร้อมก้าน INSULATOR, PIN TYPE, 33 kV, TIS 279, TYPE C (CLASS 56-3); COMP. WITH PIN	3	3	03000002 03100001
12	ดรอพเอาท์ฟิวส์คัตเอาท์ หนึ่งอินซูเลเตอร์ 33 kV, 100 แอมป์ CUTOUT, FUSE, DROPOUT, SINGLE INSULATOR, 33 kV, 100 A	1	1	04010100
13	ล่อฟ้า 30 kV, 5 กิโลแอมป์ LIGHTNING ARRESTER, 30 kV, 5 kA	1	1	04000100
14	หม้อแปลงซิงเกิลบูชชิ่ง 33 GRDY/19/0.46-0.23 kV, 10-50 kVA TRANSFORMER, SINGLE BUSHING, 33 GRDY/19/0.46-0.23 kV, 10-50 kVA	1	1	05000200 - 05000203
15	สายอะลูมิเนียมหุ้มฉนวน PVC 750 V, 75°C มอก. 293 หรือหุ้มฉนวนแบบไม่เต็มพิกัด 33 kV ขนาด 35 ต.มม. CABLE, Al, PVC INSULATED, 750 V, 75°C, TIS 293 OR PARTIALLY INSULATED, 33 kV, 35 mm²	5 ม. m	5 ม. m	02070001 or 02060100
16	ลวดเหล็กตีเกลียว 50/7 ต.มม. พร้อมอุปกรณ์ยึด มอก. 404 WIRE, STEEL STRANDED, 50/7 mm², COMP. WITH FIXING ACCESS. TIS 404	23 ม. m	23 ม. m	01100004
17	ลวดอะลูมิเนียมกลม Ø 4 มม. ความยาวตามต้องการ TIE WIRE, Al, Ø 4 mm; LENGTH AS REQUIRED			02200002
18	สเตอร์รัพแคล้มป์ หรือเบลแคล้มป์ และฮอทไลน์แคล้มป์ ขนาดตามต้องการ CLAMP, STIRRUP OR BAIL; AND CLAMP, HOT LINE; SIZE AS REQUIRED	1	1	02330000-1 02330100
19	พี.จี. คอนเน็คเตอร์ สลักคู่ สำหรับสายอะลูมิเนียม 25-95 ต.มม. CONNECTOR, PARALLEL GROOVE, DOUBLE BOLT, Al, 25-95 mm²	1	1	02300102
20	กายแคล้มป์ สลัก 3 ตัว (ดูรายละเอียด A,B) CLAMP, GUY, TRIPLE BOLT (SEE DETAIL A, B)	1	1	02440102
21	ท่อ PVC แข็ง ขนาด Ø 20 มม. พร้อมอุปกรณ์ยึด แบบเลขที่ S02-015/19128 CONDUIT, RIGID PVC, Ø 20 mm; COMP. WITH FIXING ACCESS. DWG. NO. S02-015/19128	1	1	08040002 or 08040001
22	หลักดิน 60 X 60 X 5 มม. ยาว 2,000 มม. ROD, GROUND, 60 X 60 X 5 mm, 2,000 mm LONG	1	1	01220002
23	ยูแคล้มป์ สลัก 1 ตัว M 8 (ไวร์ โรป คลิพ) CLAMP, SINGLE U-BOLT, M 8 (WIRE ROPE CLIP)	4	4	01230000
24	PVC เทป กว้าง 19 มม. (ใช้ความยาว 2 ม. ต่อ 1 จุด) PVC TAPE, 19 mm WIDE (2 m LONG PER POINT)	ม้วน rolls	ม้วน rolls	02180002
	สำหรับการติดตั้งระบบจำหน่ายแรงต่ำ FOR LOW VOLTAGE SYSTEM INSTALLATION			
25	คอน คอร. ขนาด 100 X 100 X 1,500 มม. CROSSARM, PRESTRESS CONCRETE, 100 X 100 X 1,500 mm	1	1	00110000
26	เหล็กประกับคอน 30 X 6 X 760 มม. BRACE, FLAT, FOR CROSSARM, 30 X 6 X 760 mm	2	2	01200001
27	สลักเกลียว M 16 X 130 มม. BOLT, MACHINE, M 16 X 130 mm	2	2	01110200
28	สลักเกลียว M 16 X 250 มม. BOLT, MACHINE, M 16 X 250 mm	3	3	01110203
29	สลักเกลียว M 16 X 350 มม. BOLT, MACHINE, M 16 X 350 mm	1	1	01110205
30	แหวนสี่เหลี่ยมแบน 52 X 52 X 4.5 มม. รู Ø 18 มม. มอก. 258 WASHER, SQUARE, FLAT, 52 X 52 X 4.5 mm, HOLE Ø 18 mm, TIS 258	7	7	01180100

กองวิศวกรรมไฟฟ้าและเครื่องกล
ฝ่ายวิศวกรรม

ผู้เขียน
ผู้สำรวจ
วิศวกร
หัวหน้าแผนก
ผู้อำนวยการกอง
ผู้อำนวยการฝ่าย
รองผู้ว่าการฝ่ายเทคนิค

การไฟฟ้าส่วนภูมิภาค

ผู้ว่าการ 30 มิ.ย. 31

การติดตั้งหม้อแปลงซิงเกิลบูชชิ่ง 19 kV
กรณีสายเมนเป็นเคเบิลอากาศ

19 kV SINGLE BUSHING TRANSFORMER INSTALLATION
H.T. AERIAL CABLE PRIMARY MAIN LINE

ใช้แทนแบบ
ถูกแทนโดยแบบ
เขียนเสร็จวันที่ 17 มี.ค. 31
แก้แบบวันที่ 4 ก.ย. 35
มิติเป็น
มาตราส่วน
แบบเลขที่ SAI-015/31011
แผ่นที่ 5 ของจำนวน 6 แผ่น

การประกอบเลขที่ ASSEMBLY NO. **3701 C**

บัญชีวัสดุ
BILL OF MATERIAL

ลำดับที่ ITEM	รายละเอียด DESCRIPTION	จำนวน REQ'D I	 II	วัสดุเลขที่ MAT. NO.
31	PVC เทป กว้าง 19 มม. (ใช้ความยาว 2 ม. ต่อ 1 จุด) PVC TAPE, 19 mm WIRE (2 m LONG FOR POINT)	ม้วน rolls	ม้วน rolls	02180002
32	คอนเนคเตอร์ชนิดบีบ แบบ H สำหรับสายอะลูมิเนียม ขนาดตามต้องการ CONNECTOR, COMPRESSION, H TYPE, Al, SIZE AS REQUIRED	3	3	02320003 or 02320002
33	เหล็กจับขอบถังหม้อแปลง สำหรับยึดสายแรงต่ำ BRACKET, STEEL, FOR TRANSFORMER SECONDARY LEAD	2	2	05100003
34	หางปลาชนิดบีบ เจาะรูตามมาตรฐาน NEMA สำหรับสายอะลูมิเนียม 35-95 ต.มม. CABLE LUG, NEMA HOLE, COMPRESSION TYPE, Al, 35-95 mm^2	4	4	02420101 02420104
35	สายอะลูมิเนียมหุ้มฉนวน PVC 750 V, 75°C มอก. 293 ขนาดตามต้องการ CABLE, Al, PVC INSULATED, 750 V, 75°C, TIS 293; SIZE AS REQUIRED	16 ม. m	16 ม. m	02070001 - 02070004
36	แร็ค 3 X 200 มม. (3"X8") แบบหลังยื่น RACK, SECONDARY, MEDIUM PRESSED STEEL, 3X200 mm (3'X8'), EXT. BACK	1	1	03130001
37	ลูกรอกแรงต่ำ มอก. 227 แบบ ข (แบบ 53-2) INSULATOR, SPOOL TYPE, L.T., TIS 227, TYPE B (CLAS 53-2)	5	5	03030000
38	ฟิวส์สวิตช์ แรงต่ำ 1X400 แอมป์ 500 โวลต์ L.T. FUSE SWITCHS, 1X400 A, 500 V	2	2	04020100
39	ล่อฟ้า 250-500 โวลต์ 2.5-5.0 กิโลแอมป์ LIGHTNING ARRESTER, 250-500 V, 2.5-5.0 kA	2	2	04000300

	แบบอ้างอิง REFERENCE DRAWING	แบบเลขที่ DWG. NO.	การประกอบเลขที่ ASSEMBLY NO.
1	การต่อลงดินระบบแรงสูง และแรงต่ำ H.T. AND L.T. EARTHING SYSTEM	S02-015/20039	9701
2	การต่อสายแรงต่ำออกจากหม้อแปลง SECONDARY LEAD FROM TRANSFORMER	SA1-015/22011	0603
3	พื้นที่หน้าตัดสำหรับสายเป็นกลาง ระบบแรงต่ำ NOMINAL CROSS-SECTIONS FOR NEUTRAL, L.T. SYSTEM	S02-015/16036	0201
4	การติดตั้งล่อฟ้าแรงต่ำ และการต่อสายเป็นกลางลงดิน L.T. LIGHTNING ARRESTER INSTALLATION AND SECONDARY NEUTRAL GROUNDING	S02-015/19001	0401
5	การติดตั้งล่อฟ้าแรงต่ำ ในระบบจำหน่ายแรงต่ำ L.T. LIGHTNING ARRESTER INSTALLATION IN L.T. DISTRIBUTION LINE	SA1-015/22040	0402
6	การต่อสายเป็นกลางแรงต่ำลงดิน สำหรับหม้อแปลง และสายระบบจำหน่าย SECONDARY NEUTRAL EARTHING FOR TRANSFORMER AND DISTRIBUTION LINE	S02-015/20066	0403
7	คอนเนคเตอร์ชนิดบีบ แบบ H สำหรับใช้งานในระบบจำหน่ายแรงต่ำ COMPRESSION CONNECTOR, H-TYPE, USE IN L.T. DISTRIBUTION SYSTEM	SA1-015/26021	9530
8	ลักษณะการต่อสายแยกเข้าหม้อแปลง 1 เฟส แบบต่างๆ TYPICAL OF 1-Ø TRANSFORMER JUMPER TAPPING OF THE MAIN LINE	SA1-015/21058	9603
9	การต่อแยกเคเบิลอากาศแรงสูง โดยใช้เบล (สเตอร์รัพ) แคล้มป์ CLAMP, BAIL (STIRRUP) ASSEMBLY, FOR TAP LINE ON H.T. AERIAL CABLE	SA1-015/23045	9560

กองวิศวกรรมไฟฟ้าและเครื่องกล ฝ่ายวิศวกรรม	**การไฟฟ้าส่วนภูมิภาค**	ใช้แทนแบบ ถูกแทนโดยแบบ
ผู้เขียน ผู้สำรวจ วิศวกร หัวหน้าแผนก ผู้อำนวยการกอง ผู้อำนวยการฝ่าย	ผู้ว่าการ 30 มิ.ค. 31. การติดตั้งหม้อแปลงซิงเกิลบุชชิ่ง 19 kV กรณีสายเมนเป็นเคเบิลอากาศ	เขียนเสร็จวันที่ 17 มี.ค. 31 แก้แบบวันที่ 4 ก.ย. 35 มิติเป็น มาตราส่วน
รองผู้ว่าการฝ่ายเทคนิค	19 kV SINGLE BUSHING TRANSFORMER INSTALLATION H.T. AERIAL CABLE PRIMARY MAIN LINE	แบบเลขที่ SA1-015/31011 แผ่นที่ 6 ของจำนวน 6 แผ่น