
การประกอบเลขที่ ASSEMBLY NO. 3402

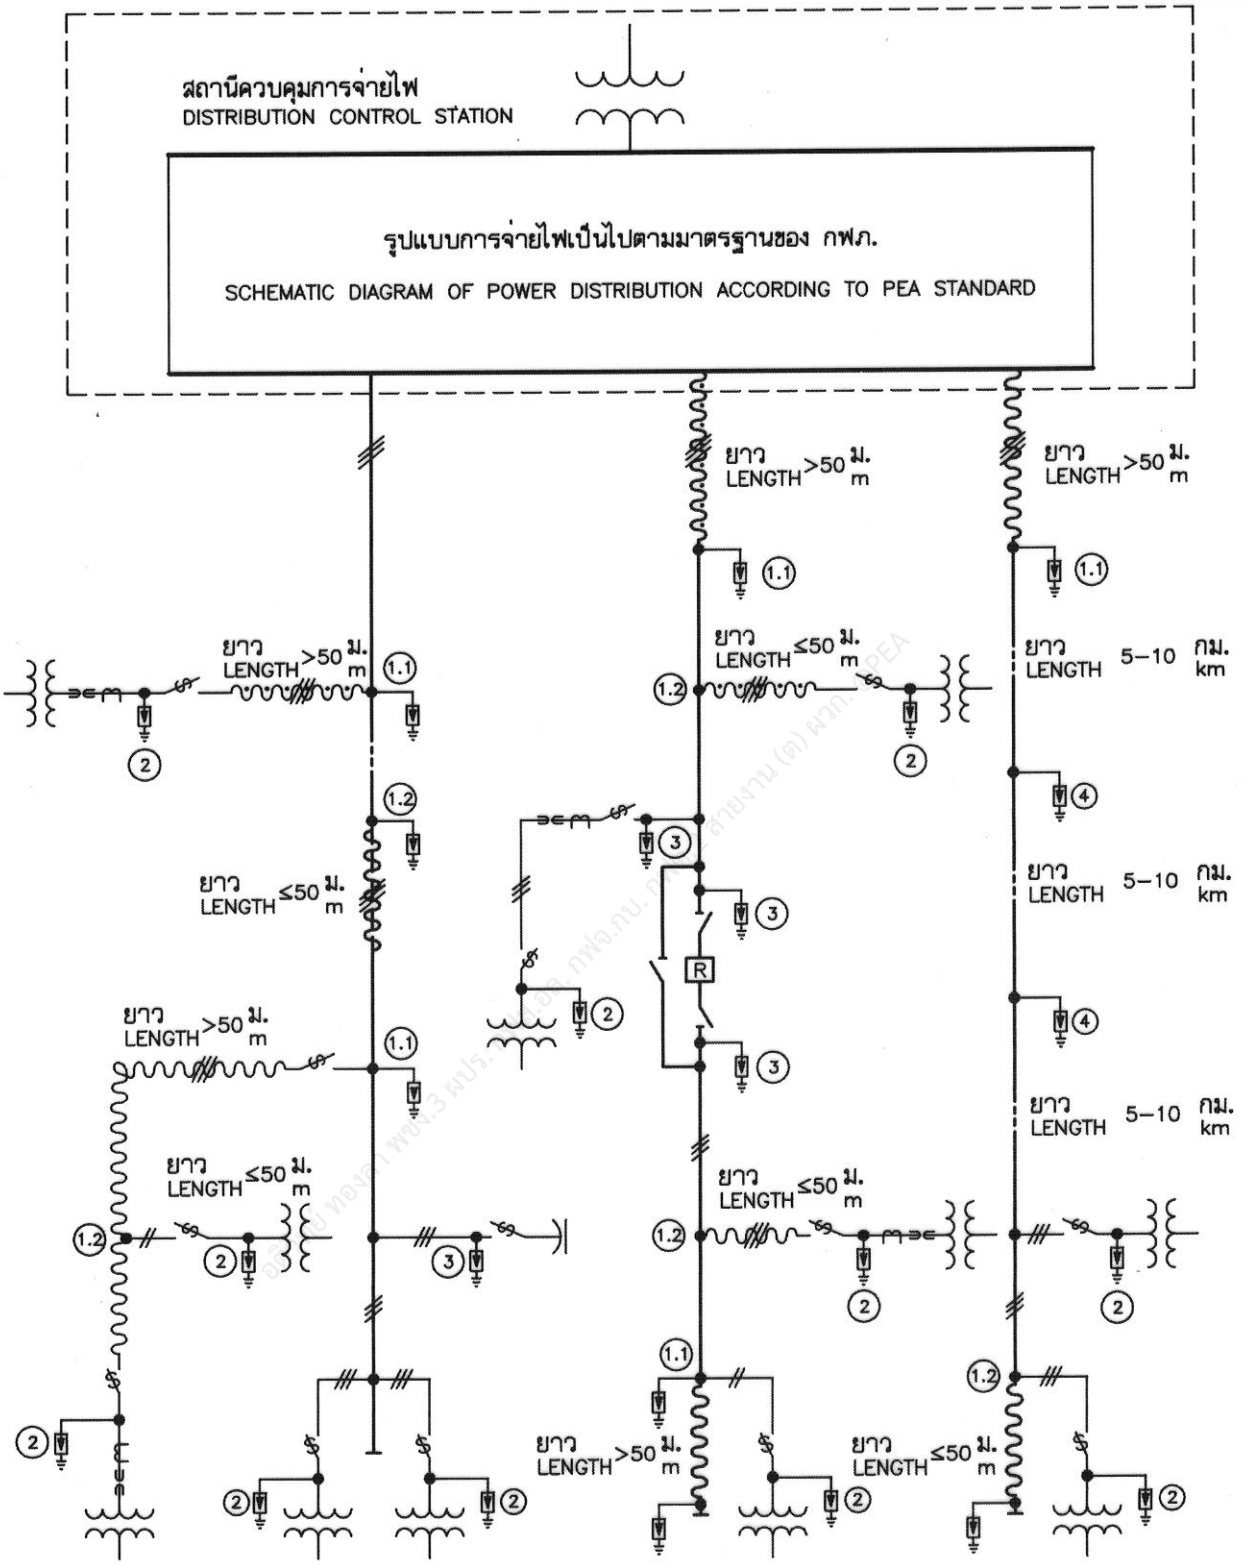

กองมาตรฐานระบบไฟฟ้า ฝ่ายวิศวกรรม	การไฟฟ้าส่วนภูมิภาค	ใช้แทนแบบ S02-015/19148 ถูกแทนโดยแบบ .....
ผู้เขียน ..นวพงศ์ นุตาดี..... ผู้สำรวจ ..... วิศวกร..นวพงศ์ นุตาดี..... หัวหน้าแผนก..... ผู้อำนวยการกอง..... ผู้อำนวยการฝ่าย.....	ผู้ว่าการ..... (ภพ)	เขียนเสร็จวันที่ 3 พ.ค. 2559 แก้แบบวันที่ ..... มิติเป็น..... มาตราส่วน.....
รองผู้ว่าการวิศวกรรม ..... (ภพ)	การติดตั้งกับดักเสิร์จแรงสูง ระบบ 33 kV 33 kV H.V. SURGE ARRESTER INSTALLATION	แบบเลขที่ SA2-015/59002 แผ่นที่ 1 ของจำนวน 2 แผ่น

การประกอบเลขที่ ASSEMBLY NO.	3402

การติดตั้งกับดักเสิร์จแรงสูง

เพื่อจำกัดแรงดันไฟฟ้าเกินพิกัด และป้องกันอุปกรณ์ไฟฟ้า ต้องติดตั้งกับดักเสิร์จแรงสูงตามลักษณะ และตำแหน่งต่างๆ ดังนี้

1. ที่ปลายสายเคเบิล ซึ่งติดตั้งต่อกับสายอากาศระบบจำหน่ายแรงสูง ดังต่อไปนี้

1.1 ถ้าสายเคเบิลมีความยาวมากกว่า 50 ม. ให้ติดตั้งกับดักเสิร์จแรงสูงที่ปลายสายเคเบิลทั้งสองข้าง

1.2 ถ้าสายเคเบิลมีความยาวน้อยกว่า หรือเท่ากับ 50 ม. ให้ติดตั้งกับดักเสิร์จแรงสูงที่ปลายสายเคเบิลเพียงด้านเดียว

2. ที่หม้อแปลง

3. ที่อุปกรณ์ไฟฟ้าในระบบจำหน่าย เช่น คะแปซิเตอร์ อุปกรณ์ของมิเตอร์แรงสูง และรีโคลสเซอร์

4. ที่สายระบบจำหน่ายแรงสูง 33 เควี ที่มีความยาวและในสายช่วงดังกล่าวไม่มีกับดักเสิร์จแรงสูงติดตั้งอยู่ (เป็นอุปกรณ์ ป้องกันอุปกรณ์ไฟฟ้า เช่น หม้อแปลง คะแปซิเตอร์ ฯลฯ) ให้พิจารณาติดตั้งกับดักเสิร์จแรงสูงเพิ่มเติมที่สายระบบจำหน่ายไว้ทุกๆ ระยะ 5-10 กม. ทำหน้าที่ป้องกันสายระบบจำหน่าย เพื่อลดปัญหาไฟดับและลูกถ้วยหรืออุปกรณ์ชำรุดจากฟ้าผ่า

H.V. SURGE ARRESTER INSTALLATION

TO LIMIT OVERVOLTAGES AND TO PROTECT THE EQUIPMENT H.V. SURGE ARRESTER SHALL BE INSTALLED AT THE FOLLOWING POSITIONS.

1. AT THE LINE END OF THE CABLE WHERE CABLES ARE CONNECTED WITH THE OVERHEAD LINE, AS FOLLOWS :

1.1 INSTALL THE ARRESTERS AT THE BOTH LINE ENDS OF THE CABLES, IF CABLES EXCEED 50 m IN LENGTH.

1.2 INSTALL THE ARRESTERS AT ONE SITE OF THE END OF CABLES, IF CABLES DO NOT EXCEED 50 m IN LENGTH.

2. AT TRANSFORMER STATIONS.

3. AT EQUIPMENT IN DISTRIBUTION SYSTEM SUCH AS CAPACITOR, H.V. METER AND RECLOSER.

4. FOR 33 kV LONG DISTRIBUTION LINE THAT IS NOT INSTALLED WITH ANY H.V. SURGE ARRESTER (AS PROTECTIVE EQUIPMENT OF TRANSFORMER, CAPACITOR etc.). H.V. LIGHTNING SURGE SHOULD BE ADDITIONALLY INSTALLED AT LINE PROTECTION IN EVERY 5-10 km INTERVAL LENGTH TO MINIMIZES SYSTEM OUTAGES FROM BREAKDOWN OF INSULATION BY LIGHTNING SURGE.

หมายเหตุ

1. ค่าความต้านทานดินของสายดิน ที่ต่อกับกับดักเสิร์จแรงสูงแต่ละจุดควรมีค่าไม่เกิน 5 โอห์ม แต่ในพื้นที่ยากแก่การต่อลงดินค่าความต้านทานดินของสายดินแต่ละจุด ยอมให้มีค่าไม่เกิน 25 โอห์ม

2. ขนาดพิกัดของกับดักเสิร์จแรงสูง ที่จะติดตั้งตามตำแหน่งต่างๆ ให้ดูจากแบบมาตรฐานการเลือกใช้กับดักเสิร์จแรงสูง แบบเลขที่ S02-015/17045 (การประกอบเลขที่ 3401)

NOTE

1. THE EARTH ELECTRODE RESISTANCE SHOULD NOT BE EXCEED 5 OHMS. BUT IN THE DIFFICULTY EARTHING AREA, PERMISSIBLY EARTH ELECTRODE RESISTANCE SHOULD NOT EXCEED 25 OHMS.

2. SEE THE APPLICATION OF H.V. SURGE ARRESTER DRAWING NO S02-015/17045 FOR SELECTING THE ARRESTER RATING (ASSEMBLY NO. 3401).

กองมาตรฐานระบบไฟฟ้า ฝ่ายวิศวกรรม	การไฟฟ้าส่วนภูมิภาค	ใช้แทนแบบ S02-015/19148 ถูกแทนโดยแบบ .....
ผู้เขียน นวพงศ์ นุตาดี ผู้สำรวจ ..... วิศวกร นวพงศ์ นุตาดี หัวหน้าแผนก ..... ผู้อำนวยการกอง ..... ผู้อำนวยการฝ่าย	ผู้ว่าการ	เขียนเสร็จวันที่ 3 พ.ค. 2559 แก้แบบวันที่ ..... มิติเป็น ..... มาตราส่วน .....
	การติดตั้งกับดักเสิร์จแรงสูง ระบบ 33 kV	
รองผู้ว่าการวิศวกรรม	33 kV H.V. SURGE ARRESTER INSTALLATION	แบบเลขที่ SA2-015/59002 แผ่นที่ 2 ของจำนวน 2 แผ่น