การประกอบเลขที่
ASSEMBLY NO. 3209

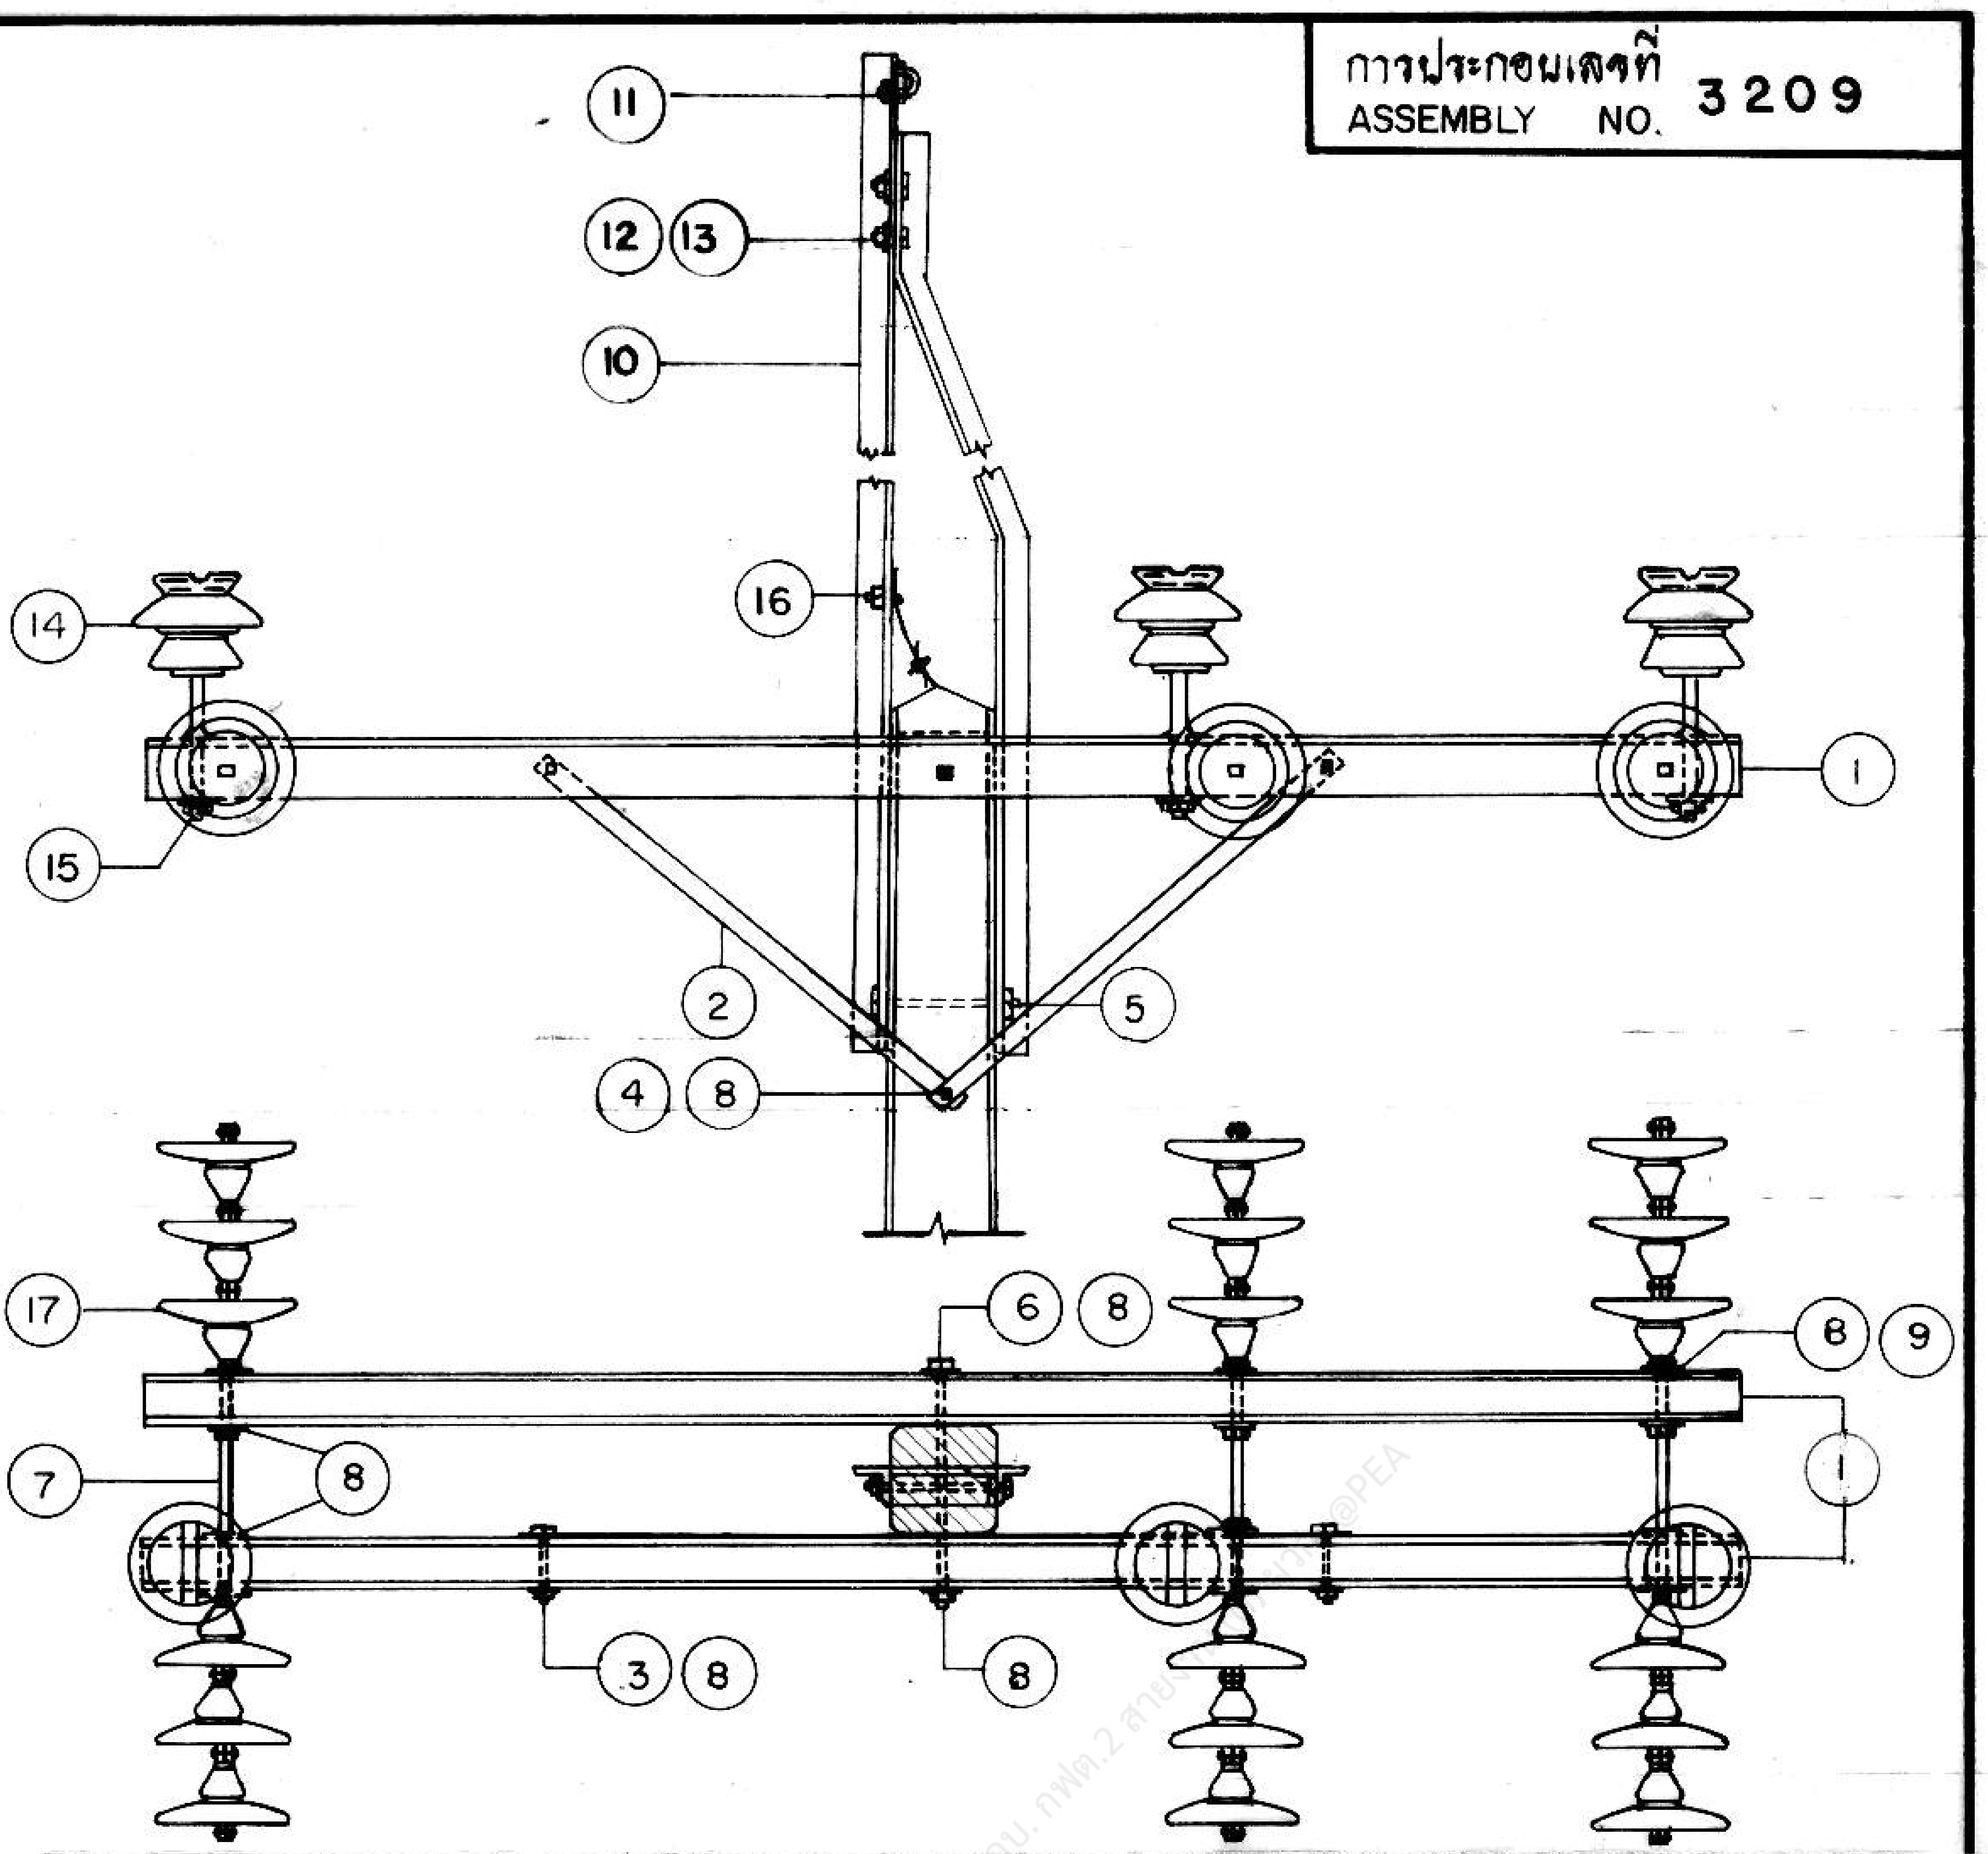

BILL OF MATERIAL			
ITEM	DESCRIPTION	REQ.D	MAT. NO.
1	ไม้คอนสายขนาด 100 X 120 X 3000 มม. CROSSARM (H.T.) WOOD, 100 X 120 X 3000 mm	2	00100003 (0101)
2	เหล็กประกับไม้คอน 40 X 6 X 1000 มม. BRACE, FLAT, FOR CROSSARM, 40 X 6 X 1000 mm	2	01200002 (0121)
3	สลักเกลียว M 16 X 130 มม. BOLT, MACHINE, M 16 X 130 mm	2	01110200 (0220)
4	สลักเกลียว M 16 X 200 มม. BOLT, MACHINE, M 16 X 200 mm	1	01110202 (0222)
5	สลักเกลียว M 16 X 250 มม. BOLT, MACHINE, M 16 X 250 mm	2	01110203 (0223)
6	สลักเกลียว M 16 X 400 มม. BOLT, MACHINE, M 16 X 400 mm	1	01110206 (0226)
7	สลักเกลียวห่วงกลม M 16 X 400 มม. BOLT, DOUBLE ARMING ROUND EYE M 16 X 400 mm	3	01130000 (0246)
8	แหวนเหลี่ยมแบนขนาด 52X52X4.5 มม. รู Ø 18 มม. มอก. 258 WASHER, SQUARE, FLAT, 52 X 52 X 4.5 mm HOLE Ø 18 mm TIS 258	17	01180100 (0355)

กองวิศวกรรมและวางแผน

ผู้เขียน
สถาปนิก
วิศวกร
หัวหน้าแผนก
ผู้อำนวยการกอง

รองผู้ว่าการฝ่ายเทคนิค

การไฟฟ้าส่วนภูมิภาค

ผู้ว่าการ

การประกอบไม้คอนคู่กับเสาคอนกรีต
ระบบ 33 kV., 3 เฟส, มุม 30°-60°

33kV, DOUBLE CROSSARM ASSEMBLY ON
CONCRETE POLE, 3-PHASE, 30°- 60°

ใช้แทนแบบ
ถูกแทนโดยแบบ
เขียนเสร็จวันที่ 5 พย. 12
แก้แบบวันที่
มิติเป็น มม.
มาตราส่วน 1:25

แบบเลขที่ I50-015/120341
แผ่นที่ 1 ของจำนวน 2 แผ่น

การประกอบเลขที่
ASSEMBLY NO. 3209

BILL OF MATERIAL

ITEM	DESCRIPTION	REQ. D	MAT. NO.
9	นัทรูปห่วง M 16 DIN 582 NUT, EYE, M 16 DIN 582	3	01180001 (0345)
10	เหล็กฉากรับสายล่อฟ้าทางโค้ง OVERHEAD GROUND WIRE CORNER BAYONET	1	01010007 (0129)
11	กราวด์ไวร์แคล้มป์แบบ J 1152 GROUND WIRE CLAMP J 1152	1	01230205 (0296)
12	สลักเกลียว M 12 X 35 มม. BOLT, MACHINE, M 12 X 35 mm	2	01110100 (0212)
13	แหวนสปริง M 12 มอก. 259 WASHER, LOCK, M12 TIS 259	2	01180300 (0364)
14	ลูกถ้วยก้านตรง 33 kV มอก. 279 แบบ ค (แบบ 56-3) INSULATOR, PIN TYPE, 33 kV TIS 279 TYPE C (CLASS 56-3)	3	03000002 (0409)
15	ก้านลูกถ้วยแรงสูง 33 kV PIN, INSULATOR	3	03100001 (0422)
16	ยูแคล้มป์ สลัก 1 ตัว M 8 (ไวร์โร้ป คลิ๊พ) CLAMP, SINGLE U-BOLT M 8 (WIRE ROPE CLIP)	2	01230000 (0165)
17	ลูกถ้วยแขวน มอก. 354 แบบ ง (แบบ 52-4) INSULATOR, SUSPENSION TYPE, TIS 354 TYPE D (CLASS 52-4)	18	03020002 (0415)

อดิวิทย์ ทองลา พชง.3 ผปร. กฟส.อล. กฟจ.กบ. กฟต.2 งาน (ต) ผวก. @PEA

กองวิศวกรรมและวางแผน
ผู้เขียน
สถาปนิก
วิศวกร
หัวหน้าแผนก
ผู้อำนวยการกอง
รองผู้ว่าการฝ่ายเทคนิค

การไฟฟ้าส่วนภูมิภาค
ผู้ว่าการ

การประกอบไม้คอนคู่กับเสาคอนกรีต
ระบบ 33 kV, 3 เฟส, มุม 30°-60°

33 kV, DOUBLE CROSSARM ASSEMBLY ON CONCRETE POLE, 3-PHASE, 30°-60°

ใช้แทนแบบ
ถูกแทนโดยแบบ
เขียนเสร็จวันที่ 5 พย. 12
แก้แบบวันที่
มิติเป็น
มาตราส่วน
แบบเลขที่ I50-015/120341
แผ่นที่ 2 ของจำนวน 2 แผ่น