การประกอบเลขที่ ASSEMBLY NO. **5205**

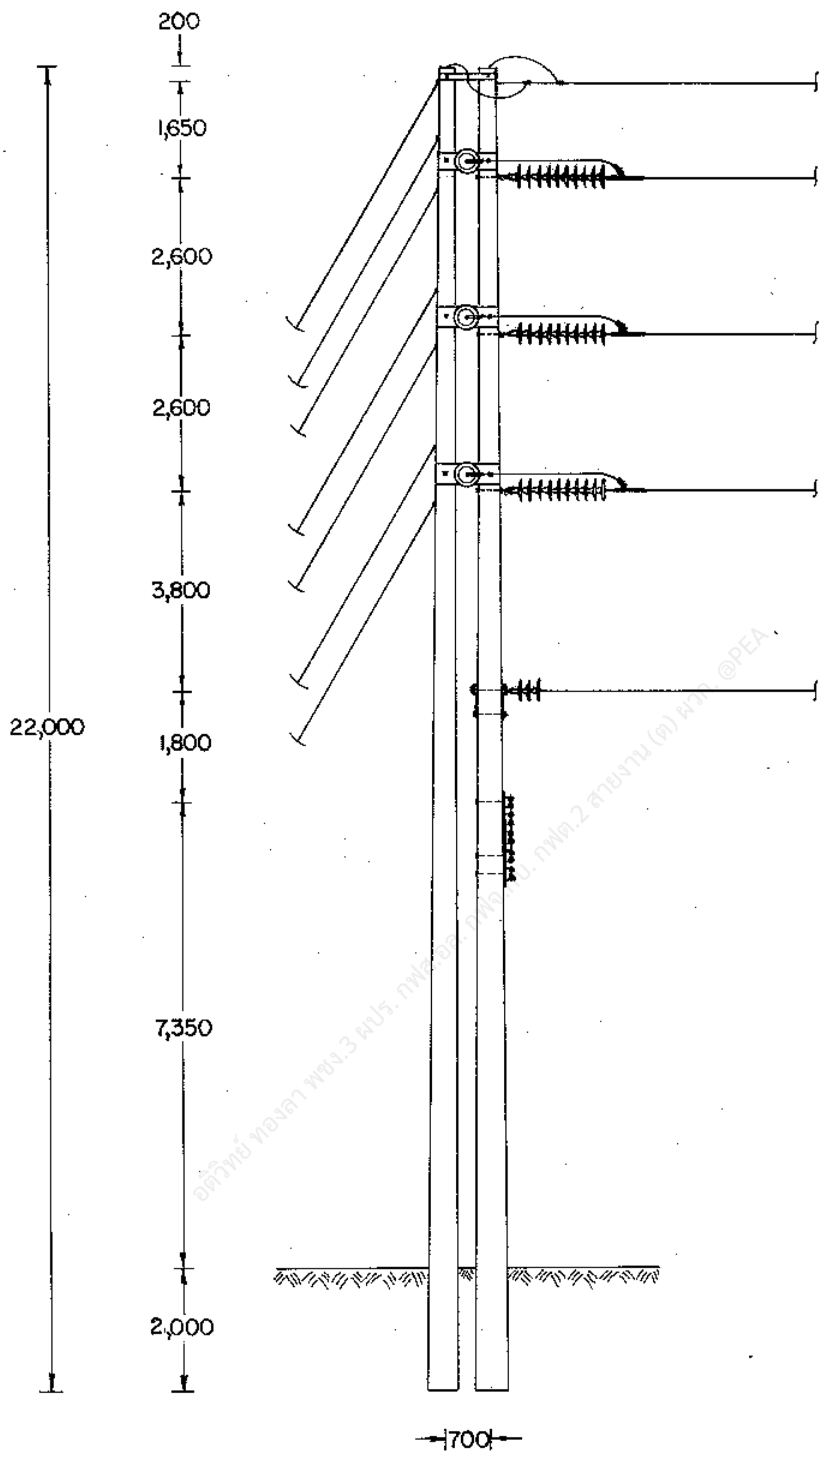

อดิวิทย์ ทองลา พชง.3 ผปร. กฟส.อ[illegible] กฟต.2 สายงาน (ต) ผวก. @PEA

กองวิศวกรรมไฟฟ้าและเครื่องกล
ฝ่ายวิศวกรรม

ผู้เขียน
ผู้ตรวจ
วิศวกร
หัวหน้าแผนก
หัวหน้ากอง
ผู้อำนวยการฝ่าย 23

รองผู้ว่าการฝ่ายเทคนิค

การไฟฟ้าส่วนภูมิภาค

ผู้ว่าการ 24 มิ.ย. 23

115 kV วงจรเดียว สายไฟฟ้าเดียว
เสาคู่สำหรับทางโค้ง 90°
แบบ SS-LA-2

115 kV SINGLE CIRCUIT SINGLE CONDUCTOR
DOUBLE POLE, 90° ANGLE STRUCTURE
TYPE SS — LA — 2

ใช้แทนแบบ
ถูกแทนโดยแบบ
เขียนเสร็จวันที่ 2 พ.ค. 23
แก้แบบวันที่
มิติเป็น มม.
มาตราส่วน 1 : 125

แบบเลขที่ SAI-015/23002
แผ่นที่ 1 ของจำนวน 3 แผ่น

19 มิ.ค. 2523

การประกอบเลขที่
ASSEMBLY NO. 5205

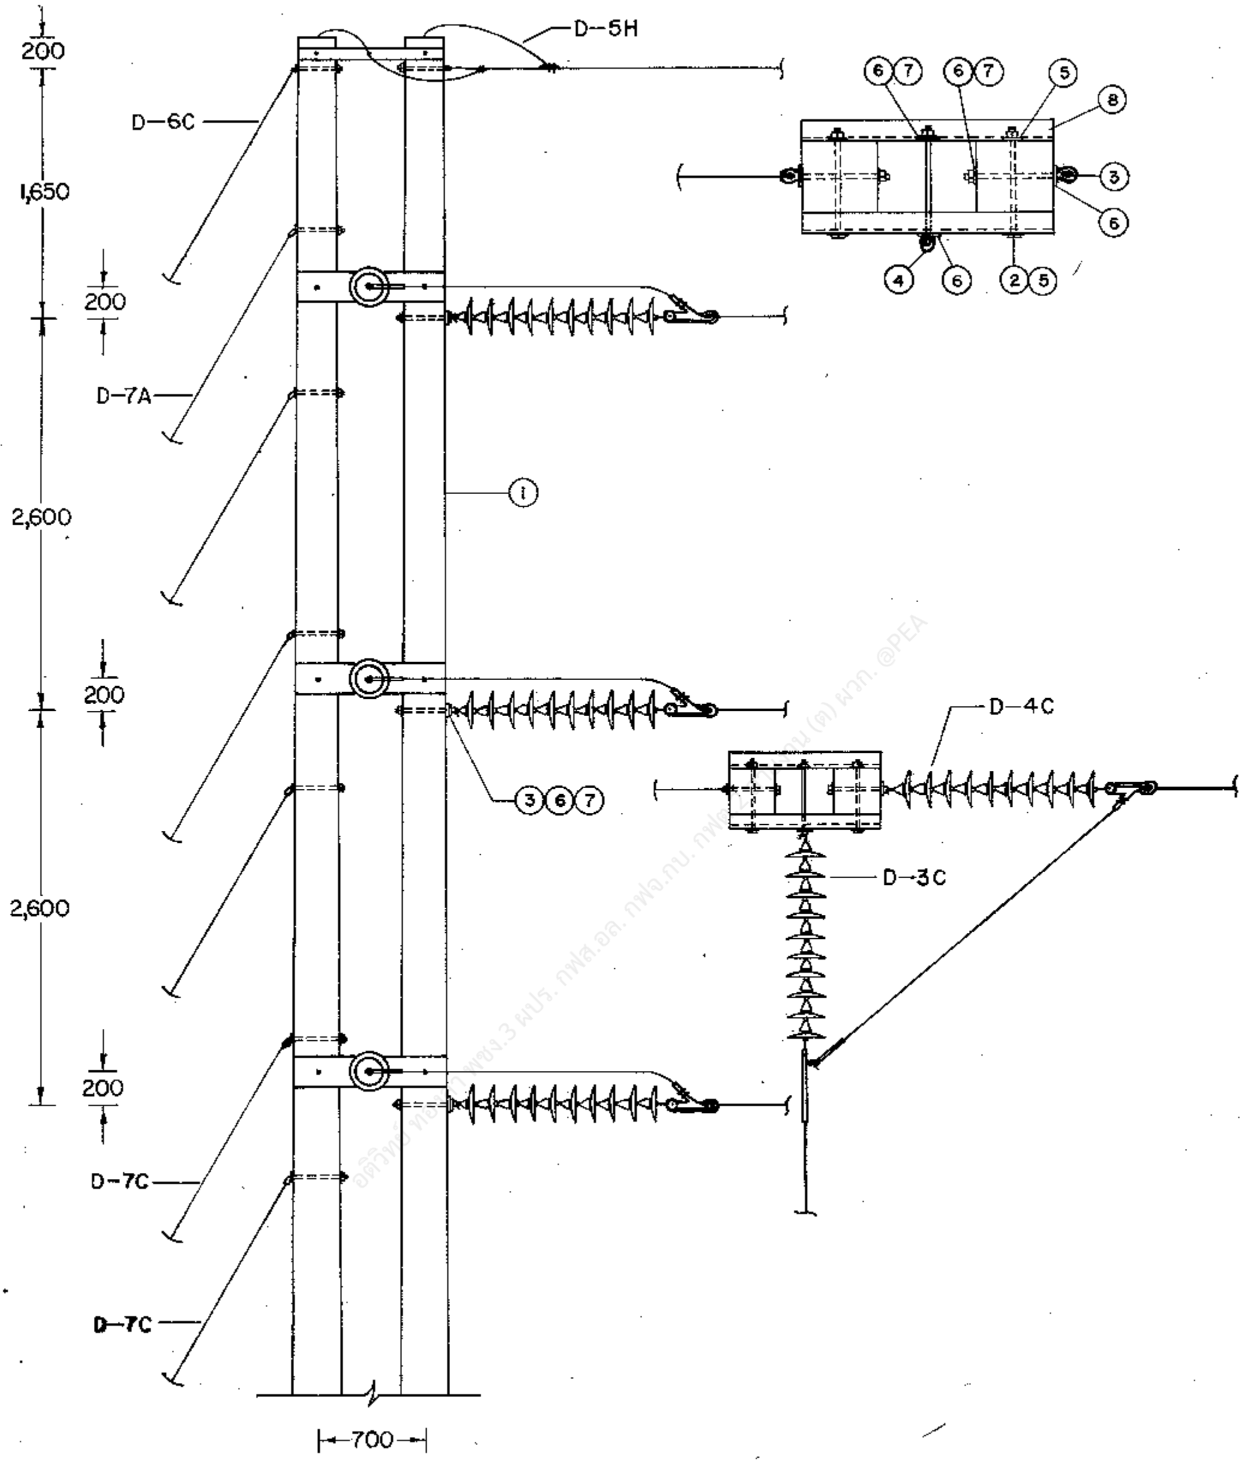
D-5H
⑥⑦
⑥⑦
⑤
⑧
③
⑥
④
⑥
②⑤
200
D-6C
1,650
200
D-7A
①
2,600
200
D-4C
③⑥⑦
D-3C
2,600
200
D-7C
D-7C
700

กองวิศวกรรมไฟฟ้าและเครื่องกล
ฝ่ายวิศวกรรม

ผู้เขียน
ผู้สำรวจ
วิศวกร
หัวหน้าแผนก ชัยรัต
หัวหน้ากอง
ผู้อำนวยการฝ่าย
รองผู้ว่าการฝ่ายเทคนิค

การไฟฟ้าส่วนภูมิภาค

ผู้ว่าการ ๒๔ มี.ค. ๒๓

115 kV วงจรเดี่ยว สายไฟฟ้าเดี่ยว
เสาคู่สำหรับทางโค้ง 90°
แบบ SS-LA-2

115 kV SINGLE CIRCUIT SINGLE CONDUCTOR
DOUBLE POLE, 90° ANGLE STRUCTURE
TYPE SS-LA-2

ใช้แทนแบบ
ถูกแทนโดยแบบ
เขียนเสร็จวันที่ 2 ม.ค. 23
แก้แบบวันที่ 15 ก.ย. 40
มิติเป็น มม.
มาตราส่วน 1 : 50
แบบเลขที่ SAI-015/23002
แผ่นที่ 2 ของจำนวน 3 แผ่น

การประกอบเลขที่ ASSEMBLY NO.	5205

บัญชีวัสดุ
BILL OF MATERIAL

ลำดับที่ ITEM	รายละเอียด DESCRIPTION	จำนวน REQ'D	วัสดุเลขที่ MAT. NO.
1	เสาคอนกรีต 22 ม. POLE, CONCRETE 22 m. LONG	2	00010011 (0041)
2	สลักเกลียว M 16 X 450 มม. BOLT, MACHINE, M 16 X 450 mm.	6	01110207 (0227)
3	สลักห่วงโอแวล M 20 X 350 มม. BOLT, OVAL EYE M 20 X 350 mm.	3	01150100 (0260)
4	สลักห่วงโอแวล M 20 X 450 มม. BOLT, OVAL EYE M 20 X 450 mm.	3	01150101 (0261)
5	แหวนสี่เหลี่ยมแบน 52X52X4.5 มม. รู Ø 18 มม. มอก. 258 WASHER, SQUARE, FLAT 52X52X4.5 mm. HOLE Ø 18 mm TIS. 258	12	01180100 (0355)
6	แหวนสี่เหลี่ยมแบน 62 X 62 X 6 มม. รู Ø 22 มม. มอก. 258 WASHER, SQUARE, FLAT 62 X 62 X 6 mm. HOLE Ø 22 mm. TIS 258	12	01180101 (0356)
7	แหวนสปริง M 20 มอก. 259 WASHER, LOCK, M 20, TIS. 259	6	01180302 (0366)
8	เหล็กรูปรางน้ำ 200 X 80 X 7.5 มม. ยาว 1,000 มม. STEEL CHANNEL 200 X 80 X 7.5 mm., 1,000 mm. LONG	6	01000400 (2675)

รายละเอียด.
DETAIL

D-3C	การประกอบลูกถ้วยแขวน SUSPENSION INSULATOR ASSEMBLY	3	
D-4C	การประกอบลูกถ้วยแขวน SUSPENSION INSULATOR ASSEMBLY	3	
D-5H	การต่อสายล่อฟ้า OVERHEAD GROUND WIRE CONNECTION	1	
D-6C	การประกอบสายยึดโยงลวดเหล็กตีเกลียว 50 ต.มม. STEEL STRANDED WIRE 50 mm² GUY ASSEMBLY	1	
D-7A	การประกอบสายยึดโยงลวดเหล็กตีเกลียว 95 ต.มม. STEEL STRANDED WIRE 95 mm² GUY ASSEMBLY	4	
D-7C	การประกอบสายยึดโยงลวดเหล็กตีเกลียว 95 ต.มม. STEEL STRANDED WIRE 95 mm² GUY ASSEMBLY	2	
D-9A	สมอบกคอนกรีต CONCRETE ANCHOR	1	
D-10B	ฐานรากเสา POLE FOUNDATION	1	

กองวิศวกรรมไฟฟ้าและเครื่องกล ฝ่ายวิศวกรรม	**การไฟฟ้าส่วนภูมิภาค**	ใช้แทนแบบ................ ถูกแทนโดยแบบ................
ผู้เขียน................ ผู้ตรวจ................ วิศวกร................ หัวหน้าแผนก................ หัวหน้ากอง................ ผู้อำนวยการฝ่าย................	ผู้ว่าการ................	เขียนเสร็จวันที่ 2 ม.ค. 23 แก้แบบวันที่ 15 ก.ย. 40 มิติเป็น................ มาตราส่วน................
	115 kV วงจรเดี่ยว สายไฟฟ้าเดี่ยว เสาคู่สำหรับทางโค้ง 90° แบบ SS-LA-2	
รองผู้ว่าการฝ่ายเทคนิค	115 kV SINGLE CIRCUIT SINGLE CONDUCTOR DOUBLE POLE, 90° ANGLE STRUCTURE TYPE SS—LA—2	แบบเลขที่ SAI-015/23002 แผ่นที่ 3 ของจำนวน 3 แผ่น

1 9 มี.ค. 2523