การประกอบเลขที่ 3415
ASSEMBLY NO.

OHGW.
ต้นกำเนิด SOURCE
โหลด LOAD
FOR BYPASS NORMALLY OPEN
SEE DETAIL A
BIRD GUARD
P.T.
รายละเอียด A
DETAIL A
OHGW
BYPASS SWITCH
SOURCE
LOAD
VACUUM SWITCH
CONTROL CABINET
P.T.
~ 2,000
2,500
300
550
2,050
500
1,000
300
650(550)*
500(510)*
4,700
(4,790)*
2,000
750
1,950
150
1,650
1,200
450
807
620


สัญลักษณ์ SYMBOL — แวคคิวอั่มสวิตช์ VACUUM SWITCH

* ระยะติดตั้งบนเสาคอนกรีตรุ่นเก่า

กองวิศวกรรมไฟฟ้าและเครื่องกล ฝ่ายวิศวกรรม	การไฟฟ้าส่วนภูมิภาค	ใช้แทนแบบ ถูกแทนโดยแบบ เขียนแบบวันที่ 22 ก.ย. 24 แก้แบบวันที่ มิติเป็น มม. มาตราส่วน 1 : 75
ผู้เขียน ผู้สำรวจ วิศวกร หัวหน้าแผนก หัวหน้ากอง ผู้อำนวยการฝ่าย รองผู้ว่าการฝ่ายเทคนิค	ผู้ว่าการ การติดตั้งแวคคิวอั่มสวิตช์ 33 kV บนเสาคู่ ในสายระบบจำหน่าย 33 kV VACUUM SWITCH INSTALLATION ON DOUBLE POLE IN DISTRIBUTION LINE	แบบเลขที่ SAI–015/24028 แผ่นที่ 1 ของจำนวน 4 แผ่น

15 ต.ค. 2524

การประกอบเลขที่ 3415
ASSEMBLY NO.

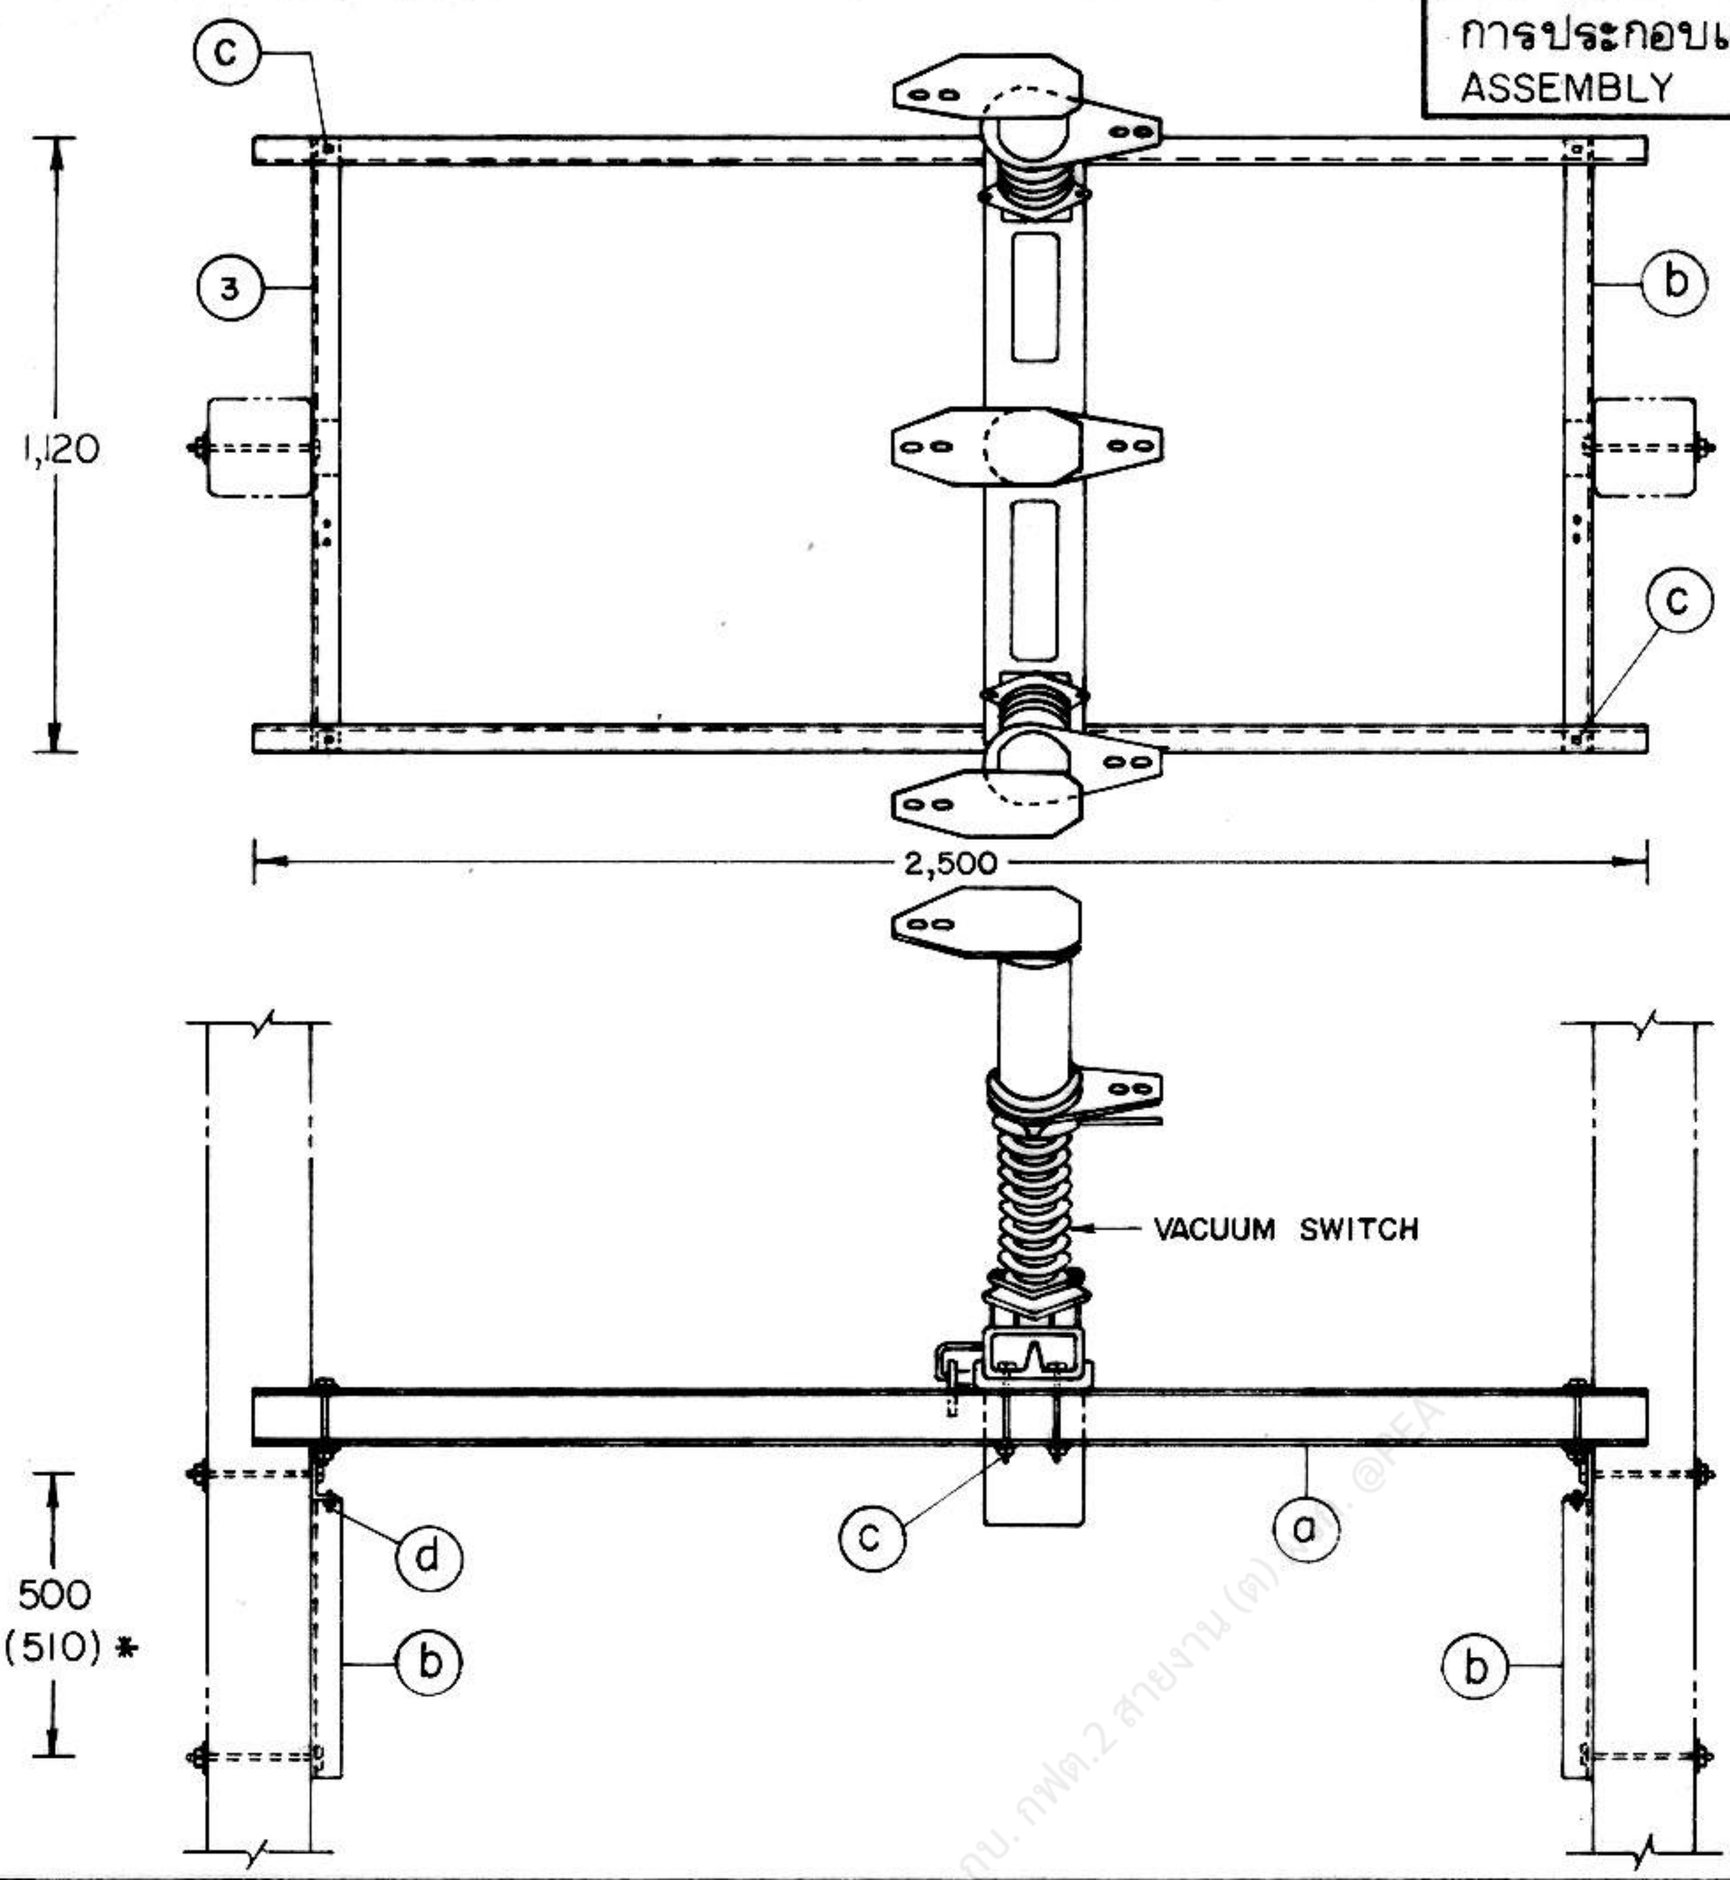

บัญชีวัสดุ
BILL OF MATERIAL

ลำดับที่ ITEM	รายละเอียด DESCRIPTION	จำนวน REQ'D	วัสดุเลขที่ MAT. NO.
a	เหล็กรูปรางน้ำ 100 X 50 X 5 มม. ยาว 2,500 มม. STEEL CHANNEL 100 X 50 X 5 mm, 2,500 mm LONG	2	—
b	เหล็กรูปรางน้ำ รับโครงเหล็ก ขนาด 100 X 50 X 5 มม. STEEL CHANNEL FOR SUPPORTING, 100 X 50 X 5 mm	2	—
c	สลักเกลียว M 16 X 40 มม. พร้อมแหวนสี่เหลี่ยมแบน 2 ตัว และแหวนสปริง 1 ตัว BOLT, MACHINE M 16 X 40 mm COMP. WITH 2 SQUARE WASHERS AND 1 SPRING WASHER	7	0220 0355 0365
d	ยูแคล้มป์ สลัก 1 ตัว M 8 CLAMP, SINGLE U—BOLT, M 8	2	0165

หมายเหตุ 1. โครงเหล็กทุกชิ้นให้อาบสังกะสี หรือทาด้วยสีกันสนิมแล้วทาทับด้วยสีเทา
2. ที่แขวนสำหรับ แวคคิวอั่มสวิตช์ 33 kV ผลิตภัณฑ์ JOSLYN แบบ VBM.

NOTES 1. ALL STEEL STRUCTURES SHALL BE GALVANIZED OR PAINTED WITH A PRIMER COAT AND GRAY WEATHER—RESISTANCE COATS.
2. HANGER FOR TYPE VBM JOSLYN 33 kV VACUUM SWITCH.

กองวิศวกรรมไฟฟ้าและเครื่องกล ฝ่ายวิศวกรรม	การไฟฟ้าส่วนภูมิภาค	ใช้แทนแบบ ถูกแทนโดยแบบ เขียนเสร็จวันที่ 22 ก.ย. 24 แก้แบบวันที่ มิติเป็น มม. มาตราส่วน 1 : 25
ผู้เขียน ผู้สำรวจ วิศวกร หัวหน้าแผนก หัวหน้ากอง ผู้อำนวยการฝ่าย	ผู้ว่าการ การติดตั้งแวคคิวอั่มสวิตช์ 33 kV บนเสาคู่ ในสายระบบจำหน่าย	
รองผู้ว่าการฝ่ายเทคนิค	33 kV VACUUM SWITCH INSTALLATION ON DOUBLE POLE IN DISTRIBUTION LINE	แบบเลขที่ SAI—015/24028 แผ่นที่ 2 ของจำนวน 4 แผ่น

15 ต.ค. 2524

การประกอบเลขที่ ASSEMBLY NO. 3415

บัญชีวัสดุ
BILL OF MATERIAL

ลำดับที่ ITEM	รายละเอียด DESCRIPTION	จำนวน REQ'D	วัสดุเลขที่ MAT. NO.
1	เสาคอนกรีต 12 ม. POLE, CONCRETE 12 m LONG	2	00010004
2	ไม้คอนสายแรงสูง 100 X 120 X 3,000 มม. CROSSARM, WOOD, H.T. 100 X 120 X 3,000 mm	5	00100003
3	เหล็กประกับไม้คอน 40 X 6 X 1,000 มม. BRACE, FLAT, FOR CROSSARM 40 X 6 X 1,000 mm	8	01200002
4	สลักเกลียว M 16 X 130 มม. BOLT, MACHINE, M 16 X 130 mm	8	01110200
5	สลักเกลียว M 16 X 200 มม. BOLT, MACHINE, M 16 X 200 mm	4	01110202
6	สลักเกลียว M 16 X 250 มม. BOLT, MACHINE, M 16 X 250 mm	10	01110203
7	สลักเกลียว M 16 X 300 มม. BOLT, MACHINE, M 16 X 300 mm	3	01110204
8	สลักเกลียว M 16 X 400 มม. BOLT, MACHINE, M 16 X 400 mm	1	01110206
9	สลักเกลียวห่วงกลม M 16 X 400 มม. BOLT, DOUBLE ARMING, ROUND EYE, M 16 X 400 mm	3	01130000
10	นัทรูปห่วง M 16 DIN 582 NUT, EYE, M 16 DIN 582	3	01180001
11	แหวนสี่เหลี่ยมแบน 52 X 52 X 4.5 มม. รู Ø 18 มม. มอก. 258 WASHER, SQUARE, FLAT 52 X 52 X 4.5 mm HOLE Ø 18 mm TIS 258	41	01180100
12	เหล็กฉากรับสายล่อฟ้า OVERHEAD GROUND WIRE BAYONET	1	01010006
13	กราวด์วายร์แคล้มป์ แบบ J 1152 GROUND WIRE CLAMP, J 1152	1	01230205
14	ยูแคล้มป์ สลัก 1 ตัว M 8 (ไวร์ โร้ป คลิ้พ) CLAMP, SINGLE U-BOLT M 8 (WIRE ROPE CLIP)	14	0123000
15	สเตรนแคล้มป์ สำหรับสายอะลูมิเนียม ขนาดตามต้องการ CLAMP, STRAIN, FOR Al, SIZE AS REQUIRED	6	03110000 - 03110101
16	พี จี. คอนเนคเตอร์ สำหรับสายอะลูมิเนียม 70-185 ต.มม. CONNECTOR, PARALLEL GROOVE, FOR Al 70-185 mm^2	7	02300103
17	ฮอทไลน์แคล้มป์ สำหรับสายอะลูมิเนียม CLAMP, HOT LINE, FOR Al CONDUCTOR	6	02330101
18	สเตอร์รัพแคล้มป์ หรือ เบลแคล้มป์ฮอทไลน์ สำหรับสายอะลูมิเนียม 70-185 ต.มม. CLAMP, STIRRUP OR BAIL, HOT LINE, FOR Al 70-185 mm^2	6	02330001
19	ลูกถ้วยก้านตรง 33 kV มอก. 279 แบบ ค (แบบ 56-3) พร้อมก้าน INSULATOR, PIN TYPE, 33 kV TIS 279 TYPE C (CLASS 56-3) WITH PIN	9	03000002 03100001
20	ลูกถ้วยแขวน มอก.354 แบบ ง (แบบ 52-4) INSULATOR, SUSPENSION TYPE, TIS 354 TYPE D (CLASS 52-4)	18	03020001


กองวิศวกรรมไฟฟ้าและเครื่องกล ฝ่ายวิศวกรรม	การไฟฟ้าส่วนภูมิภาค	ใช้แทนแบบ ถูกแทนโดยแบบ เขียนเสร็จวันที่ 22 ก.ย. 24 แก้แบบวันที่ มิติเป็น มาตราส่วน
ผู้เขียน ผู้สำรวจ วิศวกร หัวหน้าแผนก หัวหน้ากอง ผู้อำนวยการฝ่าย	ผู้ว่าการ การติดตั้งแวคคิวอั่มสวิทช์ 33 kV บนเสาคู่ ในสายระบบจำหน่าย	
รองผู้ว่าการฝ่ายเทคนิค	33 kV VACUUM SWITCH INSTALLATION ON DOUBLE POLE IN DISTRIBUTION LINE	แผนเลขที่ SAI-015/24028 แผ่นที่ 3 รวมจำนวน 4 แผ่น

15 ต.ค. 2524

การประกอบเลขที่ 3415
ASSEMBLY NO.

บัญชีวัสดุ
BILL OF MATERIAL

ลำดับที่ ITEM	รายละเอียด DESCRIPTION	จำนวน REQ'D	วัสดุเลขที่ MAT. NO.
21	ล่อฟ้า 30 kV, 5 กิโลแอมป์ LIGHTNING ARRESTER, 30 kV, 5 kA	6	04000100
22	สวิทช์ธรรมดาหนึ่งขา 33 kV, 600 แอมป์ SWITCH, DISCONNECTING, SINGLE POLE, 33 kV, 600 A	3	04050100
23	เคเบิลอากาศอะลูมิเนียม 33 kV ขนาด 120 ต.มม. หรือขนาดตามต้องการ CABLE, AERIAL, Al 33 kV, 1X120 mm^2 OR SIZE AS REQ'D	30 ม. m.	02050102
24	เทปพันเคเบิลอากาศแรงสูง ELECTRICAL SPLICING TAPE, FOR H.T. AERIAL CABLE	3 ม้วน rolls	02180003
25	เทปไฟฟ้า PVC หรือเทปไฟฟ้ายางซิลิโคน PVC PLASTIC OR SILICONE RUBBER ELECTRICAL TAPE	10 ม. m.	02180002 or 02180004
26	ลายอะลูมิเนียมเปลือย ขนาด 50 ต.มม. มอก. 85 CONDUCTOR, Al 50 mm^2 TIS 85	5 ม. m.	02010002
27	ลวดเหล็กตีเกลียว 50/7 ต.มม. มอก. 404 WIRE, STEEL STRANDED, 50/7 mm^2 TIS 404	48 ม. m.	01100004
28	หลักดิน 60X60X5 มม. ยาว 2 ม. ROD, GROUND 60X60X5 mm 2 m LONG	2	01220002
29	ท่อ PVC แข็ง ขนาด 20 X 2500 มม. พร้อมอุปกรณ์ติดตั้ง แบบเลขที่ S02-015/19128 PIPE, RIGID PVC. 20X2,500 mm COMP. WITH FIXER DWG. NO. S02-015/19128	2	08040001
30	แวคคิวอั่มสวิตช์ สามเฟส, 33 kV, 400 แอมป์ พร้อม พีที 33,000/230 โวลต์ 0.5 kVA คอนโทรลเคเบิล และตู้อุปกรณ์ควบคุม VACUUM SWITCH, THREE-PHASE, 33 kV, 400 A COMPLETE WITH PT. 33,000/230 V, 0.5 kVA, CONTROL CABLE AND CONTROL CABINET	1 ชุด set	—
31	ที่แขวนแวคคิวอั่มสวิตช์กับเสาคู่ (ผลิตภัณฑ์ JOSLYN) รายละเอียดดูแบบแผ่นที่ 2 DOUBLE POLE MOUNTING FRAME FOR VACUUM SWITCH (FOR MANUFACTURER : JOSLYN) SEE DETAIL IN DWG. SHEET 2	1	—
32	แป้นไม้รองรับตู้อุปกรณ์ควบคุม ขนาด 60X40X2 ซม. CONTROL CABINET PLATE (HARD WOOD) SURFACE FINISHED, SIZE 60X40X2 Cm	1	—

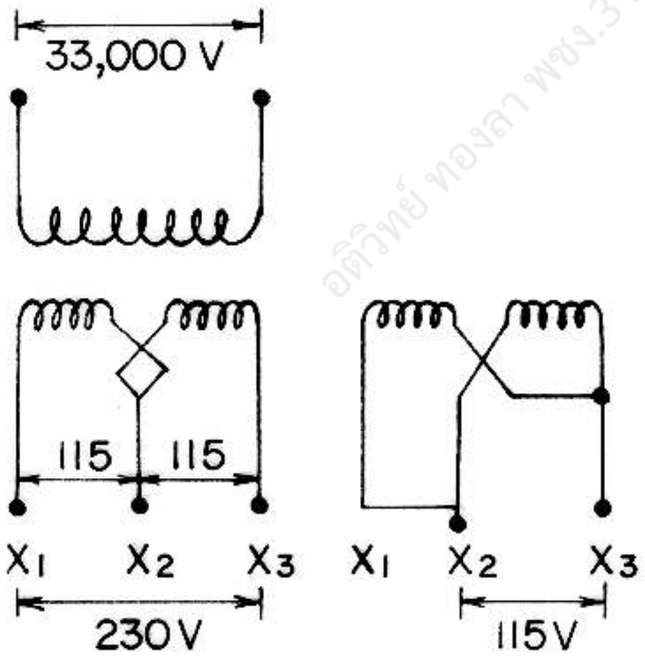

ไดอะแกรมการต่อ พีที. 33,000-230/115 V
CONNECTION DIAGRAM OF PT. 33,000-230/115 V

หมายเหตุ แวคคิวอั่มสวิตช์ เป็นอุปกรณ์ตัดตอนในระบบจำหน่ายแรงสูง มีรายละเอียดการใช้งานเช่นเดียวกับ ออยล์สวิตช์

NOTE VACUUM SWITCH IS HT. SWITCHING EQUIPMENT WHICH CAN BE USED THE SAME APPLICATION AS OIL SWITCH.

กองวิศวกรรมไฟฟ้าและเครื่องกล ฝ่ายวิศวกรรม	การไฟฟ้าส่วนภูมิภาค	ใช้แทนแบบ ถูกแทนโดยแบบ
ผู้เขียน ผู้สำรวจ วิศวกร หัวหน้าแผนก หัวหน้ากอง ผู้อำนวยการฝ่าย	ผู้ว่าการ การติดตั้งแวคคิวอั่มสวิตช์ 33 kV บนเสาคู่ ในสายระบบจำหน่าย	เขียนเสร็จวันที่ 22 ก.ย. 24 แก้แบบวันที่ มิติเป็น มาตราส่วน
รองผู้ว่าการฝ่ายเทคนิค 15 ต.ค. 2524	33 kV VACUUM SWITCH INSTALLATION ON DOUBLE POLE IN DISTRIBUTION LINE	แบบเลขที่ SAI-015/24028 แผ่นที่ 4 ของจำนวน 4 แผ่น