การประกอบเลขที่ ASSEMBLY NO. 5 2 6 0 B

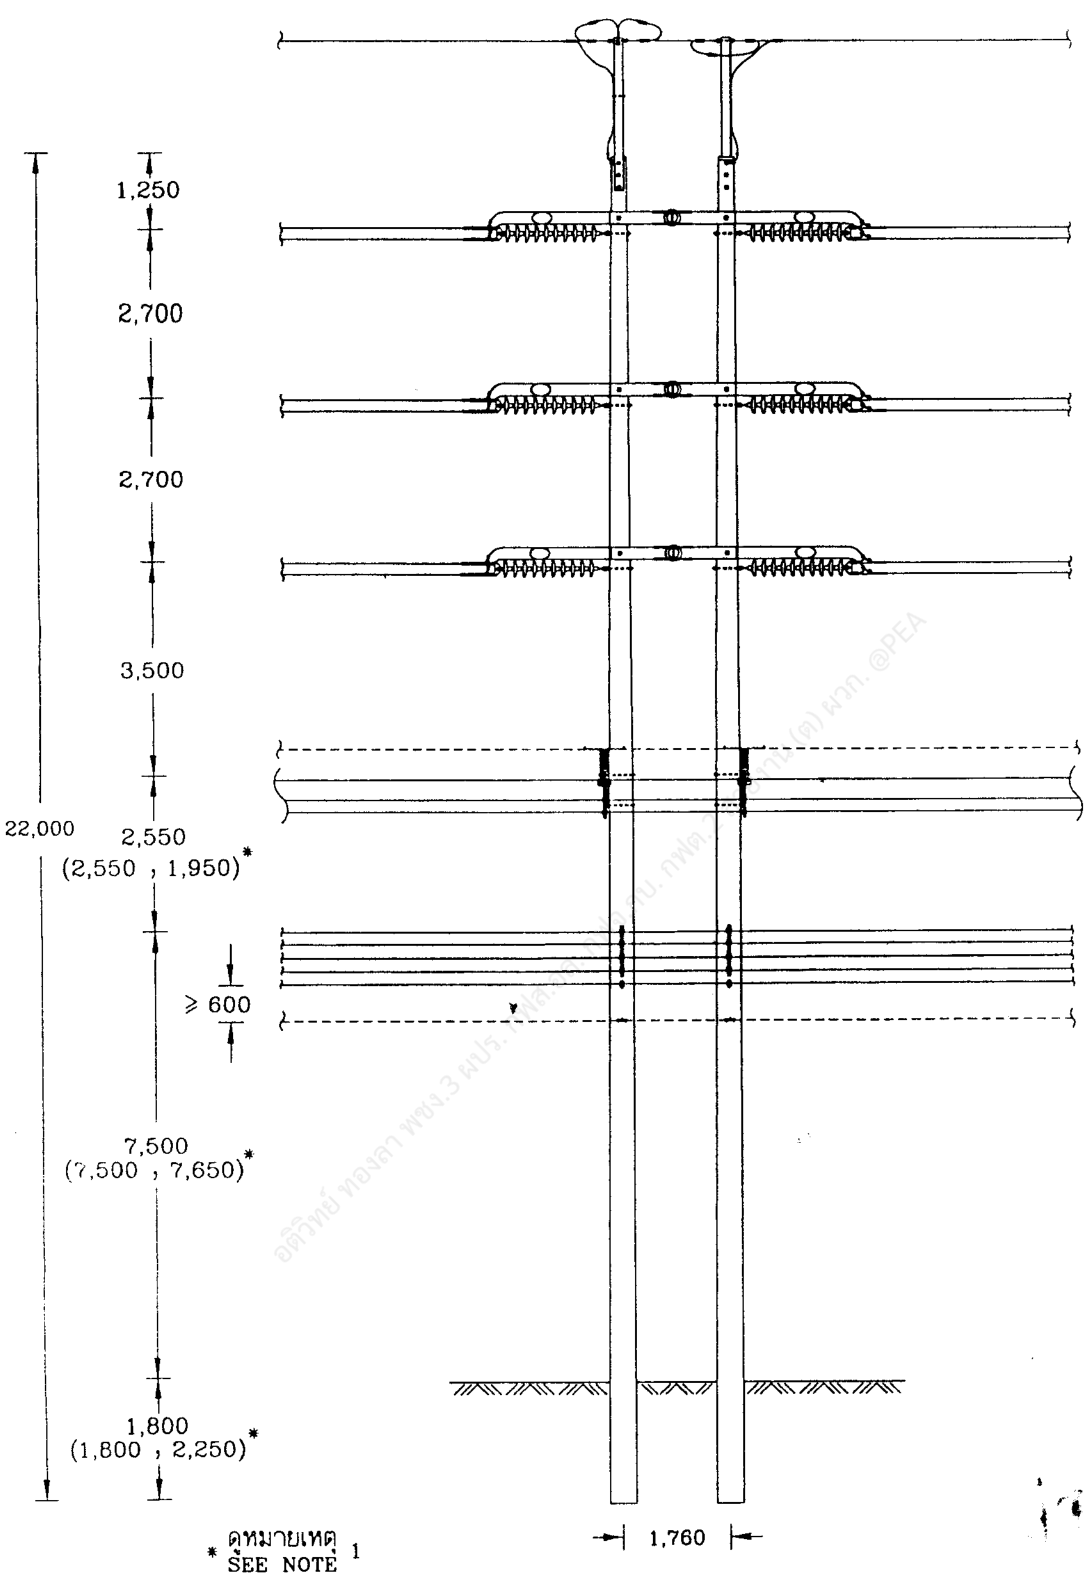

* ดูหมายเหตุ 1
SEE NOTE 1

อติวิทย์ ทองลา พชง.3 ผปร. กฟส.อต. กฟฉ.สบ. กฟต.2 [illegible] (ต) ผวก. @PEA

กองมาตรฐานระบบไฟฟ้า
ฝ่ายมาตรฐานและความปลอดภัย

การไฟฟ้าส่วนภูมิภาค

ใช้แทนแบบ ....
ถูกแทนโดยแบบ ....
ผู้เขียน ...สมชาย...........
ผู้สำรวจ......................
วิศวกร.........................
หัวหน้าแผนก..................
ผู้อำนวยการกอง...............
ผู้อำนวยการฝ่าย...............
ผู้ว่าการ.........................
เขียนเสร็จวันที่ 1 มิ.ย. 2552
แก้แบบวันที่ ....
มิติเป็น ....มิลลิเมตร.......
มาตราส่วน ..1:125.......

115 kV วงจรเดี่ยว สายไฟฟ้าคู่
เสาคู่ (ชนิดมีกราวด์เพลทในเสา)
สำหรับแยกสาย ในพื้นที่จำกัด
แบบ SD-TL-2

115 kV SINGLE CIRCUIT DOUBLE CONDUCTOR
DOUBLE POLE (WITH GROUND PLATE IN POLE),
TAP LINE STRUCTURE IN LIMITED AREAS
TYPE SD-TL-2

รองผู้ว่าการวางแผนและพัฒนาระบบไฟฟ้า
....

แบบเลขที่ SA1-015/52006
แผ่นที่ 1 ของจำนวน 4 แผ่น

การประกอบเลขที่ ASSEMBLY NO. 5 2 6 0 B

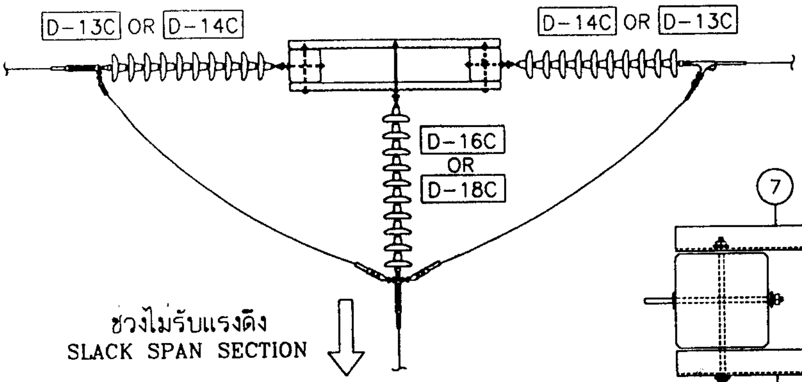

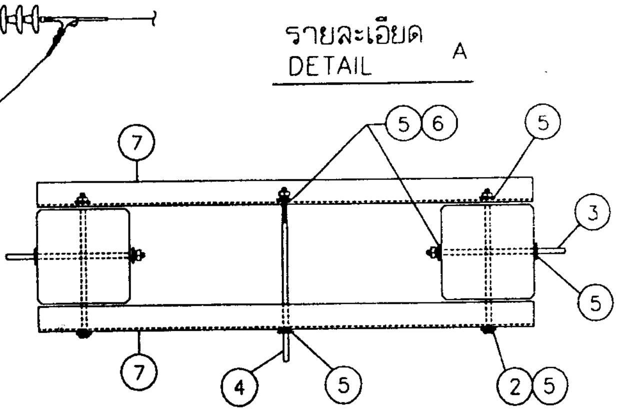

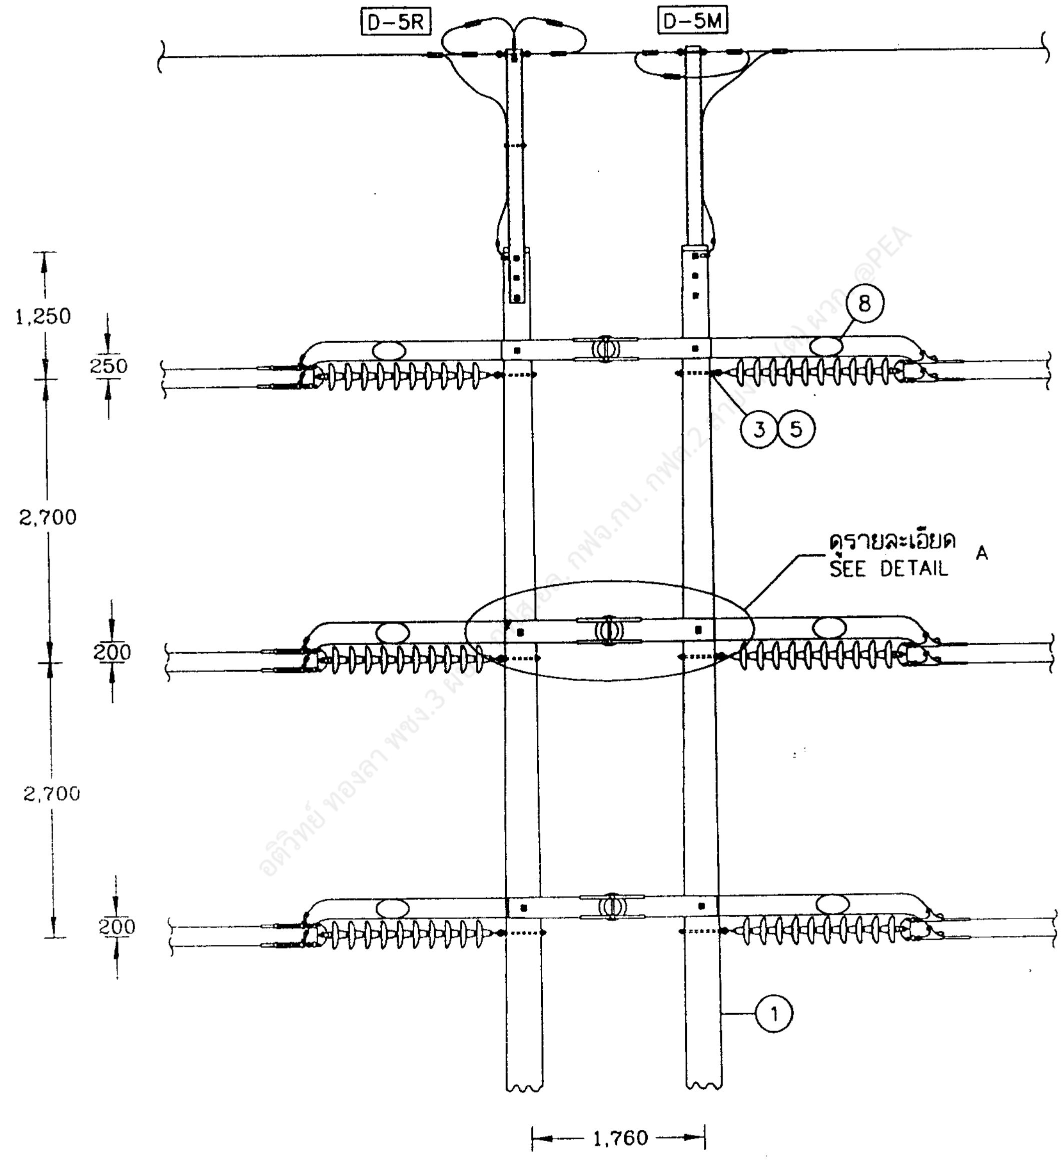

กองมาตรฐานระบบไฟฟ้า ฝ่ายมาตรฐานและความปลอดภัย	การไฟฟ้าส่วนภูมิภาค	ใช้แทนแบบ .... ถูกแทนโดยแบบ ....
ผู้เขียน ...สมชาย... ผู้สำรวจ .... วิศวกร .... หัวหน้าแผนก .... ผู้อำนวยการกอง .... ผู้อำนวยการฝ่าย	ผู้ว่าการ	เขียนเสร็จวันที่ 1 มิ.ย. 2552 แก้แบบวันที่ .... มิติเป็น มิลลิเมตร มาตราส่วน 1:75
	115 kV วงจรเดี่ยว สายไฟฟ้าคู่ เสาคู่ (ชนิดมีกราวด์เพลทในเสา) สำหรับแยกสาย ในพื้นที่จำกัด แบบ SD-TL-2	
รองผู้ว่าการวางแผนและพัฒนาระบบไฟฟ้า	115 kV SINGLE CIRCUIT DOUBLE CONDUCTOR DOUBLE POLE (WITH GROUND PLATE IN POLE), TAP LINE STRUCTURE IN LIMITED AREAS TYPE SD-TL-2	แบบเลขที่ SA1-015/52006 แผนที่ 2 ของจำนวน 4 แผ่น

การประกอบเลขที่ ASSEMBLY NO.	5 2 6 0 B

บัญชีวัสดุ
BILL OF MATERIAL

ลำดับที่ ITEM	รายละเอียด DESCRIPTION	จำนวน REQ.D	วัสดุเลขที่ MAT. NO.
1	เสา คอร. ยาว 22.00 ม. ชนิดมีกราวด์เพลทในเสา POLE, CONCRETE, 22.00 m LONG, WITH GROUND PLATE IN POLE	2	1000010015
2	สลักเกลียว M 20x450 มม. BOLT, MACHINE, M 20x450 mm	6	1010110302
3	สลักห่วงโอแวล M 20x350 มม. BOLT, OVAL EYE, M 20x350 mm	6	1010150100
4	สลักห่วงโอแวล M 20x450 มม. BOLT, OVAL EYE, M 20x450 mm	3	1010150101
5	แหวนสี่เหลี่ยมแบน 62x62x6 มม. รู ø22 มม. มอก.258 WASHER, SQUARE, FLAT 62x62x6 mm, HOLE ø22 mm, TIS 258	30	1010180101
6	แหวนสปริง M 20 มอก. 259 WASHER, LOCK, M 20, TIS 259	9	1010180302
7	เหล็กรูปรางน้ำ 200x80x7.5 มม. ยาว 2,000 มม. มอก.1227 STEEL CHANNEL, 200x80x7.5 mm, 2,000 mm LONG, TIS 1227	6	1010000403
8	ปรีฟอร์มแยกสาย SPACER, HELICAL, ROD, PREFORMED	6	1020240000

รายละเอียด
DETAIL

D-13C	การประกอบลูกถ้วยแขวน SUSPENSION INSULATOR ASSEMBLY	3	
D-14C	การประกอบลูกถ้วยแขวน SUSPENSION INSULATOR ASSEMBLY	3	
D-16C OR D-18C	การประกอบลูกถ้วยแขวน (ใช้สำหรับวงจรแยกสายที่เป็นสายไฟฟ้าคู่) SUSPENSION INSULATOR ASSEMBLY (FOR DOUBLE CONDUCTOR TAP LINE)	3	
	การประกอบลูกถ้วยแขวน (ใช้สำหรับวงจรแยกสายที่เป็นสายไฟฟ้าเดี่ยว) SUSPENSION INSULATOR ASSEMBLY (FOR SINGLE CONDUCTOR TAP LINE)	3	
D-5M	การประกอบสายล่อฟ้า OVERHEAD GROUND WIRE ASSEMBLY	1	
D-5R	การประกอบสายล่อฟ้า OVERHEAD GROUND WIRE ASSEMBLY	1	
D-10B	ฐานรากเสา (ใช้แบบเลขที่ SA1-015/52007 (การประกอบเลขที่ 5687L)) POLE FOUNDATION (USE DWG.NO. SA1-015/52007 (ASSEMBLY NO. 5687L))	1	
D-25	การต่อลงดิน GROUNDING	1	

กองมาตรฐานระบบไฟฟ้า ฝ่ายมาตรฐานและความปลอดภัย	การไฟฟ้าส่วนภูมิภาค	ใช้แทนแบบ .... ถูกแทนโดยแบบ ....
ผู้เขียน สมชาย ผู้สำรวจ .... วิศวกร .... หัวหน้าแผนก .... ผู้อำนวยการกอง .... ผู้อำนวยการฝ่าย	ผู้ว่าการ .... 115 kV วงจรเดี่ยว สายไฟฟ้าคู่ เสาคู่ (ชนิดมีกราวด์เพลทในเสา) สำหรับแยกสาย ในพื้นที่จำกัด แบบ SD-TL-2	เขียนเสร็จวันที่ 1 มิ.ย. 2552 แก้แบบวันที่ .... มิติเป็น .... มาตราส่วน ....
รองผู้ว่าการวางแผนและพัฒนาระบบไฟฟ้า	115 kV SINGLE CIRCUIT DOUBLE CONDUCTOR DOUBLE POLE (WITH GROUND PLATE IN POLE), TAP LINE STRUCTURE IN LIMITED AREAS TYPE SD-TL-2	แบบเลขที่ SA1-015/52006 แผ่นที่ 3 ของจำนวน 4 แผ่น

การประกอบเลขที่
ASSEMBLY NO. 5 2 6 0 B

หมายเหตุ

1.* กรณีก่อสร้างในพื้นที่เขตทางหลวงให้ใช้ค่าระยะห่างตามแนวดิ่งในวงเล็บ (มีทางเท้า , ไม่มีทางเท้า) โดยดูรายละเอียดเพิ่มเติมในแบบเลขที่ SA1-015/52007 (การประกอบเลขที่ 5687L)
2. การใช้งาน ให้ดูแบบเลขที่ SA1-015/47010 (การประกอบเลขที่ 5162)
3. หลักเกณฑ์การใช้ลูกถ้วยแรงสูงระบบสายส่ง 115 kV ให้ดูแบบเลขที่ SA1-015/50001 (การประกอบเลขที่ 5163)

NOTES

1.* IN CASE OF CONSTRUCTION IN HIGHWAY AREA, USE A VERTICAL CLEARANCE VALUE IN THE PARENTHESIS (HAVE PAVEMENT , NO PAVEMENT) . FOR ADDITIONAL DETAIL, SEE DWG NO. SA1-015/52007 (ASSEMBLY NO. 5687L) .
2. APPLICATION, SEE DWG. NO. SA1-015/47010 (ASSEMBLY NO. 5162) .
3. RULE FOR H.V. INSULATOR APPLICATION, SEE DWG. NO. SA1-015/50001 (ASSEMBLY NO. 5163)

อดิวิทย์ ทองลา พชง.3 ผปร. กฟส.อล. กฟจ.กบ. กฟต.2 สายงาน (ต) ผวก. @PEA

กองมาตรฐานระบบไฟฟ้า
ฝ่ายมาตรฐานและความปลอดภัย

ผู้เขียน สมชาย
ผู้สำรวจ
วิศวกร
หัวหน้าแผนก
ผู้อำนวยการกอง
ผู้อำนวยการฝ่าย

รองผู้ว่าการวางแผนและพัฒนาระบบไฟฟ้า

การไฟฟ้าส่วนภูมิภาค

ผู้ว่าการ

115 kV วงจรเดี่ยว สายไฟฟ้าคู่
เสาคู่ (ชนิดมีกราวด์เพลทในเสา)
สำหรับแยกสาย ในพื้นที่จำกัด
แบบ SD-TL-2

115 kV SINGLE CIRCUIT DOUBLE CONDUCTOR
DOUBLE POLE (WITH GROUND PLATE IN POLE),
TAP LINE STRUCTURE IN LIMITED AREAS
TYPE SD-TL-2

ใช้แทนแบบ
ถูกแทนโดยแบบ
เขียนเสร็จวันที่ 1 มิ.ย. 2552
แก้แบบวันที่
มิติเป็น
มาตราส่วน

แบบเลขที่ SA1-015/52006
แผ่นที่ 4 ของจำนวน 4 แผ่น