การประกอบเลขที่
ASSEMBLY NO. 5267

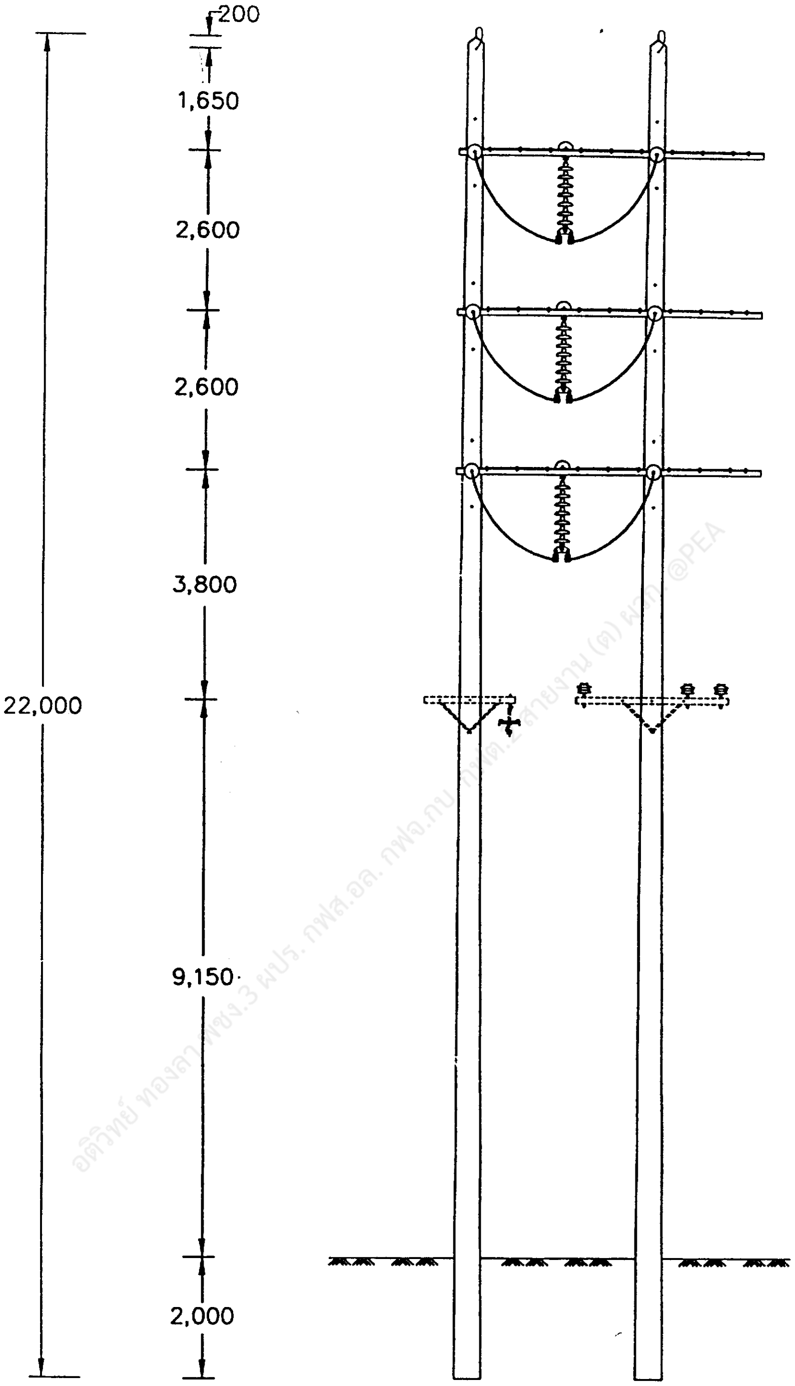

อดิวิทย์ ทองลา ผชง.3 ผปร. กฟส.อล. กฟจ.กบ. กฟต.2 สายงาน (ต) ผวก. @PEA

กองวิศวกรรมไฟฟ้าและเครื่องกล
ฝ่ายวิศวกรรม

การไฟฟ้าส่วนภูมิภาค

ผู้เขียน ....สมนึก สาคร...
ผู้สำรวจ....................
วิศวกร....................
หัวหน้าแผนก.........(แทน)
ผู้อำนวยการกอง..........
ผู้อำนวยการฝ่าย..........

ผู้ว่าการ.........................(แทน)........................

รองผู้ว่าการเทคนิคและบริการ
..........................(แทน)

115 kV วงจรเดี่ยว สายไฟฟ้าคู่ โครงสร้างเสาคู่
แบบ H-FRAME สำหรับทางตรง ก่อนต้นเสาโครงสร้างเหล็ก
แบบ SD-HF-2

115 kV SINGLE CIRCUIT DOUBLE CONDUCTOR, H-FRAME
TANGENT STRUCTURE ADJACENT TO STEEL TOWER
TYPE SD-HF-2

ใช้แทนแบบ ....
ถูกแทนโดยแบบ ....
เขียนเสร็จวันที่ 26 ม.ค. 2543
แก้แบบวันที่ ....
มิติเป็น มิลลิเมตร
มาตราส่วน 1:125
แบบเลขที่ SA1-015/43001
แผ่นที่ 1 ของจำนวน 5 แผ่น

การประกอบเลขที่
ASSEMBLY NO. 5287

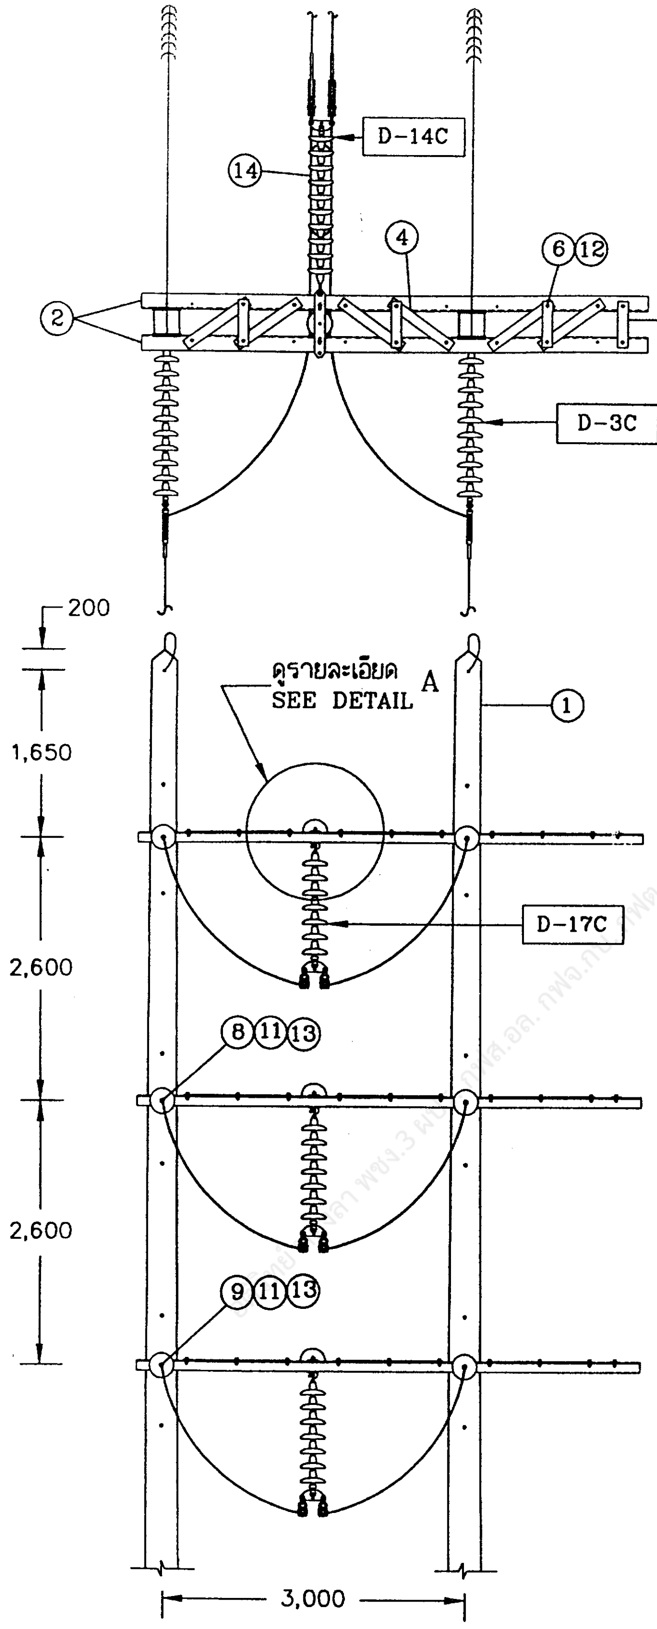
D-14C
14
4
6 12
2
3
D-3C
200
1,650
2,600
2,600
ดูรายละเอียด
SEE DETAIL A
1
D-17C
8 11 13
9 11 13
3,000

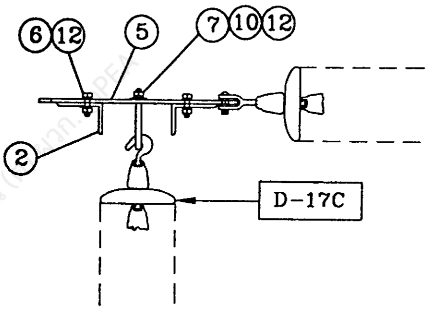
6 12
5
7 10 12
2
D-17C

รายละเอียด
DETAIL A

กองวิศวกรรมไฟฟ้าและเครื่องกล
ฝ่ายวิศวกรรม

การไฟฟ้าส่วนภูมิภาค

ผู้เขียน ....สมนึก สาคร....
ผู้สำรวจ ....
วิศวกร ....
หัวหน้าแผนก .... (แทน)
ผู้อำนวยการกอง ....
ผู้อำนวยการฝ่าย ....
รองผู้ว่าการเทคนิคและบริการ
.... (แทน)

ผู้ว่าการ .... (แทน) ....

115 kV วงจรเดี่ยว สายไฟฟ้าคู่ โครงสร้างเสาคู่
แบบ H-FRAME สำหรับทางตรง ก่อนต้นเสาโครงสร้างเหล็ก
แบบ SD-HF-2

115 kV SINGLE CIRCUIT DOUBLE CONDUCTOR, H-FRAME
TANGENT STRUCTURE ADJACENT TO STEEL TOWER
TYPE SD-HF-2

ใช้แทนแบบ ....
ถูกแทนโดยแบบ ....
เขียนเสร็จวันที่ 26 ม.ค. 2543
แก้แบบวันที่ ....
มิติเป็น ....มิลลิเมตร....
มาตราส่วน ....1:75....
แบบเลขที่ SA1-015/43001
แผ่นที่ 2 ของจำนวน 5 แผ่น

การประกอบเลขที่
ASSEMBLY NO. 5257

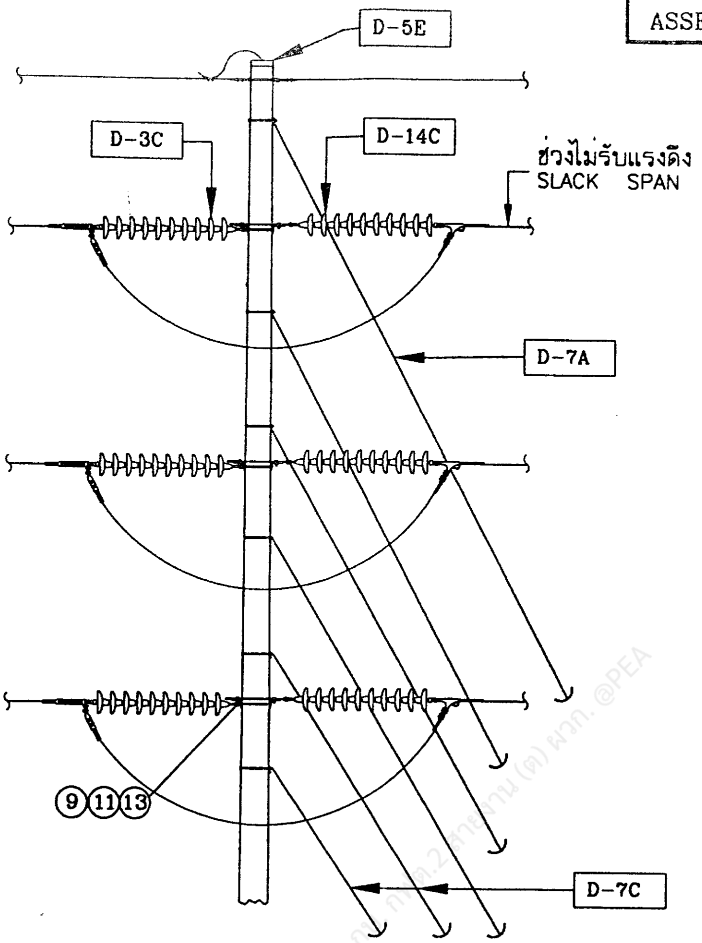
D-5E
D-3C
D-14C
ช่วงไม่รับแรงดึง
SLACK SPAN
D-7A
⑨⑪⑬
D-7C

SIDE VIEW

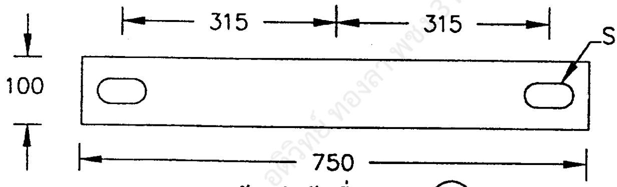
315
315
SLOT 18x68
100
750

วัสดุลำดับที่
MATERIAL ITEM ④

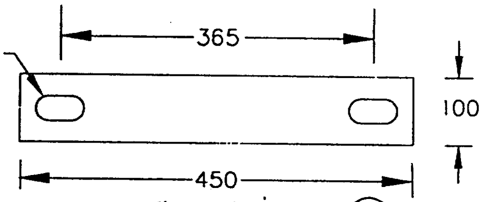

วัสดุลำดับที่
MATERIAL ITEM ③

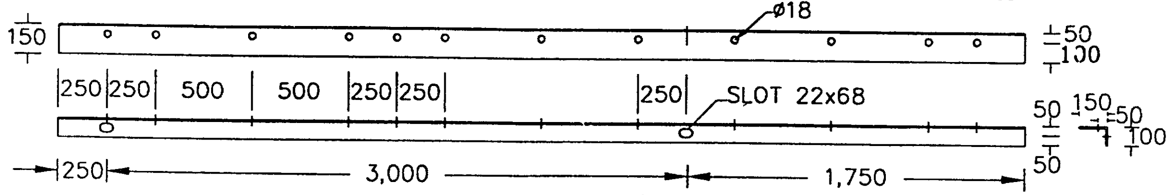
150
ø18
50
100
250
250
500
500
250
250
250
SLOT 22x68
50
150
50
100
50
250
3,000
1,750

วัสดุลำดับที่
MATERIAL ITEM ②

กองวิศวกรรมไฟฟ้าและเครื่องกล
ฝ่ายวิศวกรรม

การไฟฟ้าส่วนภูมิภาค

ผู้เขียน.....สมนึก...สาคร..
ผู้สำรวจ..................
วิศวกร....................
หัวหน้าแผนก........(แทน)
ผู้อำนวยการกอง.............
ผู้อำนวยการฝ่าย.............
รองผู้ว่าการเทคนิคและบริการ
.....................(แทน)

ผู้ว่าการ..............................(แทน)..................

115 kV วงจรเดี่ยว สายไฟฟ้าคู่ โครงสร้างเสาคู่
แบบ H-FRAME สำหรับทางตรง ก่อนต้นเสาโครงสร้างเหล็ก
แบบ SD-HF-2

115 kV SINGLE CIRCUIT DOUBLE CONDUCTOR,H-FRAME
TANGENT STRUCTURE ADJACENT TO STEEL TOWER
TYPE SD-HF-2

ใช้แทนแบบ ....
ถูกแทนโดยแบบ ....
เขียนเสร็จวันที่ 26 ม.ค.2543
แก้แบบวันที่ ....
มิติเป็น.....มิลลิเมตร.....
มาตราส่วน..............
แบบเลขที่SA1-015/43001
แผ่นที่ 3 ของจำนวน 5 แผ่น

การประกอบเลขที่
ASSEMBLY NO. 5287

บัญชีวัสดุ
BILL OF MATERIAL

ลำดับที่ ITEM	รายละเอียด DESCRIPTION	จำนวน REQ'D	วัสดุเลขที่ MAT. NO.
1	เสาคอนกรีต 22 เมตร POLE, CONCRETE, 22 m LONG	2	00010011
2	คอนสายแบบเหล็กฉาก ขนาด 150x100x12 มม. ยาว 5.00 ม. มอก.1227 CROSSARM,STEEL ANGLE,150x100x12 mm.,5.00 m. LONG TIS.1227	6	00120003
3	แผ่นเหล็ก ขนาด 6x100x450 มม. PLATE, STEEL 6x100x450 mm	12	01030002
4	แผ่นเหล็ก ขนาด 6x100x750 มม. PLATE, STEEL 6x100x750 mm	18	01030004
5	แผ่นเหล็กยื่นสองปลาย ขนาด 12x100x760 มม. PLATE, STEEL DOUBLE ARMING 12x100x760 mm	3	01030102
6	สลักเกลียวหัวหกเหลี่ยม เอ็ม 16x75 มม. BOLT, MACHINE, HEXAGON, M.16x75 mm	48	01110400
7	สลักห่วงโอเวล เอ็ม 16x150 มม. BOLT, OVAL EYE M.16x150 mm	3	01150000
8	สลักห่วงโอเวล เอ็ม 20x350 มม. BOLT, OVAL EYE M.20x350 mm	4	01150100
9	สลักห่วงโอเวล เอ็ม 20x450 มม. BOLT, OVAL EYE M.20x450 mm	2	01150101
10	แหวนสี่เหลี่ยมแบน 52x52x4.5 มม. รู ø18 มม. มอก. 258 WASHER, SQUARE, FLAT, 52x52x4.5 mm, HOLE. ø18 mm, TIS 258	3	01180100
11	แหวนสี่เหลี่ยมแบน 62x62x6 มม. รู ø22 มม. มอก. 258 WASHER, SQUARE, FLAT, 62x62x6 mm, HOLE. ø22 mm, TIS 258	12	01180101
12	แหวนรองแบบสปริง ขนาดระบุ 16 มม. ประเภทใช้งานทั่วไป มอก. 259 WASHER, LOCK, SPRING, SIZE 16 mm, GENERAL PURPOSE, TIS 259	51	01180301
13	แหวนรองแบบสปริง ขนาดระบุ 20 มม. ประเภทใช้งานทั่วไป มอก. 259 WASHER, LOCK, SPRING, SIZE 20 mm, GENERAL PURPOSE, TIS 259	6	01180302
14	ปรีฟอร์มแยกสาย สำหรับสายอลูมิเนียม 400 ต.มม. SPACER,HELICAL ROD,PREFORMED,FOR AL 400 sq.mm.	3	02240000

กองวิศวกรรมไฟฟ้าและเครื่องกล
ฝ่ายวิศวกรรม

การไฟฟ้าส่วนภูมิภาค

ผู้เขียน.....สมนึก...สาคร..
ผู้สำรวจ.....................
วิศวกร.......................
หัวหน้าแผนก.........(แทน)
ผู้อำนวยการกอง...............
ผู้อำนวยการฝ่าย..............

ผู้ว่าการ.......................(แทน).............

115 kV วงจรเดี่ยว สายไฟฟ้าคู่ โครงสร้างเสาคู่
แบบ H-FRAME สำหรับทางตรง ก่อนต้นเสาโครงสร้างเหล็ก
แบบ SD-HF-2

รองผู้ว่าการเทคนิคและบริการ
.........................(แทน)

115 kV SINGLE CIRCUIT DOUBLE CONDUCTOR,H-FRAME
TANGENT STRUCTURE ADJACENT TO STEEL TOWER
TYPE SD-HF-2

ใช้แทนแบบ ....
ถูกแทนโดยแบบ ....
เขียนเสร็จวันที่ 26 ม.ค.2543
แก้แบบวันที่ ....
มิติเป็น.......–.........
มาตราส่วน......–.........
แบบเลขที่SA1–015/43001
แผ่นที่.4.ของจำนวน.5.แผ่น

การประกอบเลขที่
ASSEMBLY NO. **5287**

รายละเอียด DETAIL			
D-3C	การประกอบลูกถ้วยแขวน SUSPENSION INSULATOR ASSEMBLY	6	
D-14C	การประกอบลูกถ้วยแขวน SUSPENSION INSULATOR ASSEMBLY	3	
D-17C	การประกอบลูกถ้วยแขวน SUSPENSION INSULATOR ASSEMBLY	3	
D-5E	การต่อสายล่อฟ้า OVERHEAD GROUND WIRE CONNECTION	2	
D-7A	การประกอบสายยึดโยงลวดเหล็กตีเกลียว 95 ต.มม. STEEL STRANDED WIRE CONNECTION 95 mm GUY ASSEMBLY	8	
D-7C	การประกอบสายยึดโยงลวดเหล็กตีเกลียว 95 ต.มม. STEEL STRANDED WIRE CONNECTION 95 mm GUY ASSEMBLY	4	
D-9B	สมอบกคอนกรีต ตามแบบเลขที่ IB1-015/240027 การประกอบเลขที่ 5652 CONCRETE ANCHOR ACCORDING TO DWG.IB1-015/240027 (ASS. NO. 5652)	2	
D-10A*	ฐานรากเสา ตามแบบเลขที่ IB1-015/240025 การประกอบเลขที่ 5668 POLE FOUNDATION IB1-015/240025 (ASS. NO. 5668)	2	

ธิติวิทย์ ทองสา พชง.3 ฝปร. กฟส.อล. [illegible] กฟต.2 สายงาน (ต) ผวก. @PEA

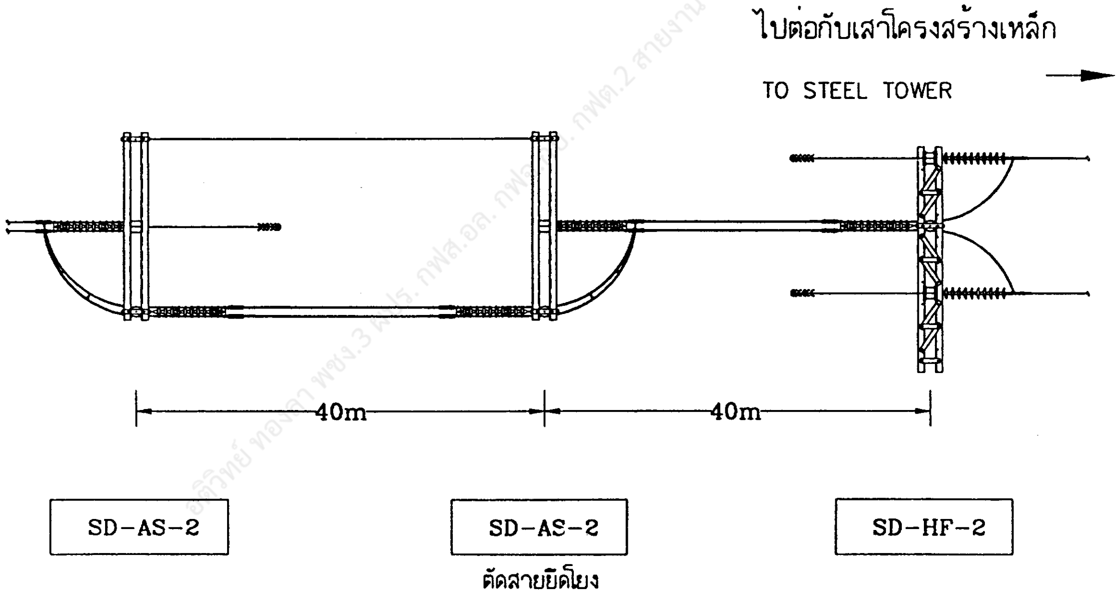

* สามารถเปลี่ยนได้ตามความเหมาะสม
CAN BE CHANGED TO SUIT

กองวิศวกรรมไฟฟ้าและเครื่องกล ฝ่ายวิศวกรรม	การไฟฟ้าส่วนภูมิภาค	ใช้แทนแบบ .... ถูกแทนโดยแบบ ....
ผู้เขียน.....สมนึก...สาครู.. ผู้สำรวจ................... วิศวกร................... หัวหน้าแผนก............(แทน) ผู้อำนวยการกอง........... ผู้อำนวยการฝ่าย...........	ผู้ว่าการ.......................(แทน)	เขียนเสร็จวันที่ 26 ม.ค.2543 แก้แบบวันที่ ....
	115 kV วงจรเดี่ยว สายไฟฟ้าคู่ โครงสร้างเสาคู่ แบบ H-FRAME สำหรับทางตรง ก่อนต้นเสาโครงสร้างเหล็ก แบบ SD-HF-2	มิติเป็น.....มิลลิเมตร..... มาตราส่วน...-...........
รองผู้ว่าการเทคนิคและบริการ ....(แทน)	115 kV SINGLE CIRCUIT DOUBLE CONDUCTOR,H-FRAME TANGENT STRUCTURE ADJACENT TO STEEL TOWER TYPE SD-HF-2	แบบเลขที่ SA1-015/43001 แผ่นที่ 5 ของจำนวน 5 แผ่น