การประกอบเลขที่
ASSEMBLY NO. 5216

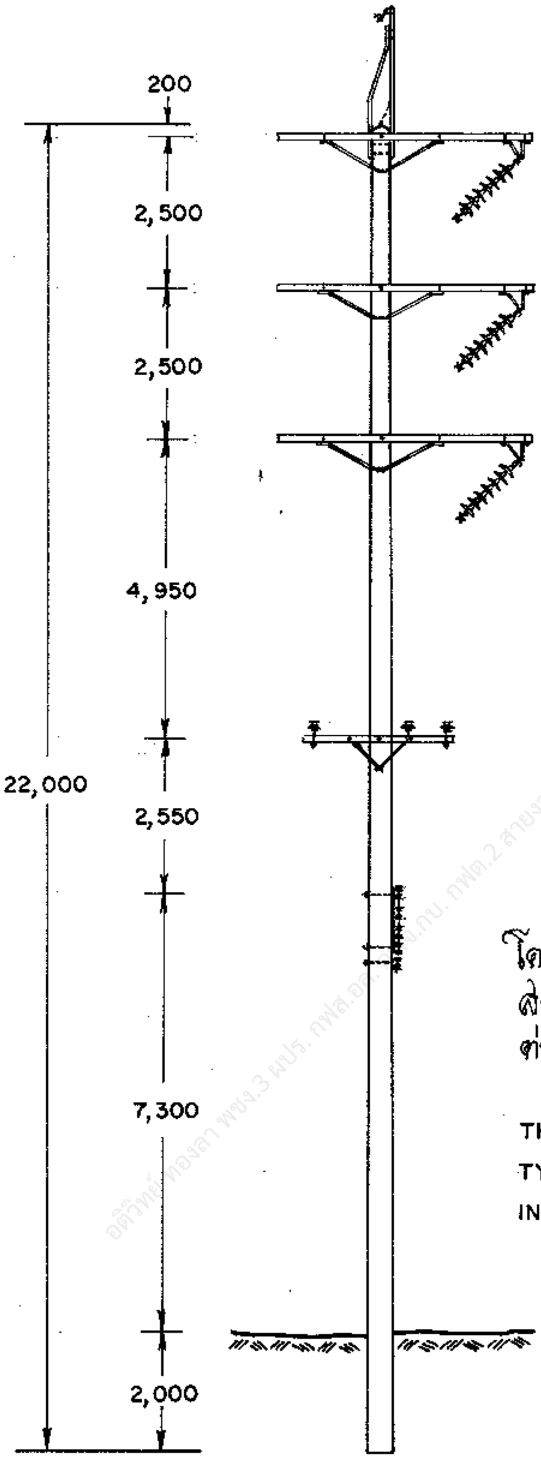

โครงสร้างนี้ ใช้งานได้เช่นเดียวกับโครงสร้าง แบบ SS–SA–1 (โครงสร้างแตกต่างกันที่วัสดุรายการที่ ② และ ⑨)

THIS STRUCTURE IS USED AS SS–SA–1 TYPE STRUCTURE (MATERIAL DIFFERENCE IN ITEM ② AND ⑨ FOR EACH STRUCTURE)

อติวิทย์ ทองลา พชง.3 ผปร. กฟส.อล. ผข.กน. กฟต.2 สายงาน (ต) ผวก. @PEA

กองวิศวกรรมไฟฟ้าและเครื่องกล
ฝ่ายวิศวกรรม

ผู้เขียน สพทอ.
ผู้ตรวจ
วิศวกร
หัวหน้าแผนก
ผู้อำนวยการกอง
ผู้อำนวยการฝ่าย (แทน)

รองผู้ว่าการฝ่ายเทคนิค

การไฟฟ้าส่วนภูมิภาค

ผู้ว่าการ 20 พ.ย. 2538 (แทน)

115 kV วงจรเดี่ยว สายไฟฟ้าเดี่ยว
เสาสำหรับทางโค้ง
แบบ SS–SA–3

115 kV SINGLE CIRCUIT SINGLE CONDUCTOR
SMALL ANGLE STRUCTURE
TYPE SS–SA–3

ใช้แทนแบบ
ถูกแทนโดยแบบ
เขียนเสร็จวันที่ 28 ก.ค. 35
แก้แบบวันที่ 27 ก.ค. 38
มิติเป็น มิลลิเมตร
มาตราส่วน 1 : 125

แบบเลขที่ SAI-015/35026
แผ่นที่ 1 ของจำนวน 3 แผ่น

การประกอบเลขที่ ASSEMBLY NO. **5216**

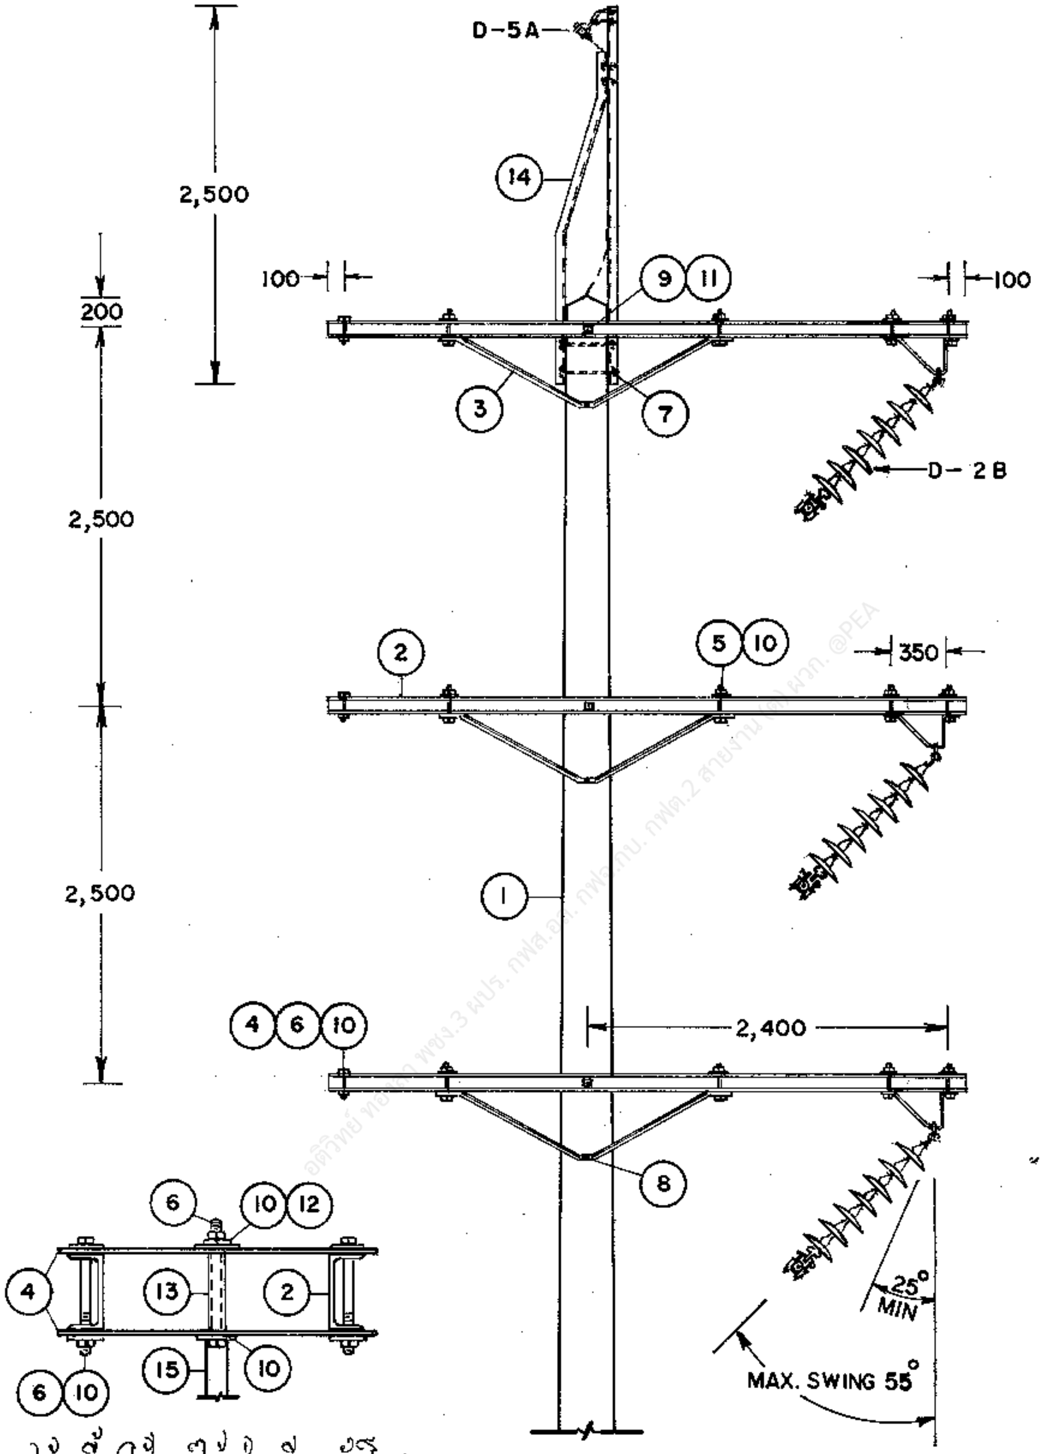
D-5A
14
2,500
100
100
200
9
11
3
7
D-2B
2,500
2
5
10
350
1
2,500
4
6
10
2,400
8
6
10
12
4
13
2
15
10
6
10
25°
MIN
MAX. SWING 55°

โครงสร้างนี้ ใช้งานได้เช่นเดียวกับโครงแบบ SS-SA-1
THIS STRUCTURE IS USED AS SS-SA-1 TYPE STRUCTURE

กองวิศวกรรมไฟฟ้าและเครื่องกล
ฝ่ายวิศวกรรม

ผู้เขียน
ผู้สำรวจ
วิศวกร
หัวหน้าแผนก
ผู้อำนวยการกอง
ผู้อำนวยการฝ่าย

รองผู้ว่าการฝ่ายเทคนิค

การไฟฟ้าส่วนภูมิภาค

ผู้ว่าการ
7 ก.พ. 2539

115 kV วงจรเดี่ยว สายไฟฟ้าเดี่ยว
เสาสำหรับทางโค้ง
แบบ SS-SA-3

115 kV SINGLE CIRCUIT SINGLE CONDUCTOR
SMALL ANGLE STRUCTURE
TYPE SS-SA-3

ใช้แทนแบบ
ถูกแทนโดยแบบ
เขียนเสร็จวันที่ 28ก.ค.35
แก้แบบวันที่ 27 ต.ค.38
มิติเป็น มิลลิเมตร
มาตราส่วน 1:10, 1:50
แบบเลขที่ SAI-015/35026
แผ่นที่ 2 ของจำนวน 3 แผ่น

การประกอบเลขที่ 5216
ASSEMBLY NO. 5216

บัญชีวัสดุ
BILL OF MATERIAL

ลำดับที่ ITEM	รายละเอียด DESCRIPTION	จำนวน REQ'D	วัสดุเลขที่ MAT. NO.
1	เสาคอนกรีต 22 มม. POLE, CONCRETE 22 m LONG	1	00010011 (0041)
2	คอนสายแบบเหล็ก รูปรางน้ำ ขนาด 100X50X5 มม. ยาว 4.20 ม. มอก. 116 CROSSARM, STEEL, CHANNEL 100X50X5 mm, 4.20 m LONG, TIS 116	6	
3	เหล็กฉากรับคอนสาย ขนาด 50X50X6 มม. ช่วงกว้าง 1,800 มม. ดรอพ 450 มม. BRACE, ANGLE STEEL, 50X50X6 mm, 1,800 mm, WIDE 450 mm, DROP	6	00120007 (0119)
4	แผ่นเหล็ก ขนาด 6X100X450 มม. PLATE, STEEL 6X100X450 mm	18	01030002 (0143)
5	สลักเกลียว M 16X130 มม. BOLT, MACHINE, M 16X130 mm	12	01110200 (0220)
6	สลักเกลียว M 16X170 มม. BOLT, MACHINE, M 16X170 mm	24	01110201 (0221)
7	สลักเกลียว M 16X300 มม. BOLT, MACHINE, M 16X300 mm	4	01110204 (0224)
8	สลักเกลียว M 16X350 มม. BOLT, MACHINE, M 16X350 mm	2	01110205 (0225)
9	สลักเกลียว M 20X350 มม. BOLT, MACHINE, M 20X350 mm	3	01110300
10	แหวนสี่เหลี่ยมแบน 52X52X4.5 มม. รู Ø 18 มม. มอก. 258 WASHER, SQUARE FLAT 52X52X4.5 mm, HOLE Ø 18 mm, TIS 258	60	01180100 (0355)
11	แหวนสี่เหลี่ยมแบน 62X62X6 มม. รู Ø 22 มม. มอก. 258 WASHER, SQUARE FLAT 62X62X6 mm, HOLE Ø 22 mm, TIS 258	6	01180101 (0356)
12	แหวนสปริง M 16 มอก. 259 WASHER, LOCK, M 16, TIS 259	6	01180301 (0365)
13	ท่อเหล็ก ชื่อขนาด 20 มม. หนา 2.65 มม. ยาว 100 มม. มอก. 277 ประเภท 2 PIPE, IRON, DIA 20 mm I.D., 2.65 mm THICKNESS, 100 mm LONG TIS 277 TYPE 2	6	01050000 (0905)
14	เหล็กฉากรับสายล่อฟ้าทางโค้ง OVERHEAD GROUND WIRE CORNER BAYONET	1	01010005 (0136)
15	ที่แขวนลูกถ้วยทางโค้ง BRACKET, CORNER SUSPENSION	3	03140012 (0489)

รายละเอียด
DETAIL

D-2B	การประกอบลูกถ้วยแขวน SUSPENSION INSULATOR ASSEMBLY	3	
D-5A	การต่อสายล่อฟ้า OVERHEAD GROUND WIRE CONNECTION	1	
D-10A	ฐานรากเสา POLE FOUNDATION	1	

กองวิศวกรรมไฟฟ้าและเครื่องกล
ฝ่ายวิศวกรรม

ผู้เขียน สมพง.
ผู้ตรวจ
วิศวกร
หัวหน้าแผนก
ผู้อำนวยการกอง
ผู้อำนวยการฝ่าย

รองผู้ว่าการฝ่ายเทคนิค

การไฟฟ้าส่วนภูมิภาค

ผู้ว่าการ 2[illegible] 2535

115 kV วงจรเดี่ยว สายไฟฟ้าเดี่ยว
เสาสำหรับทางโค้ง
แบบ SS-SA-3

115 kV SINGLE CIRCUIT SINGLE CONDUCTOR
SMALL ANGLE STRUCTURE
TYPE SS-SA-3

ใช้แทนแบบ
ถูกแทนโดยแบบ
เขียนเสร็จวันที่ 28 ต.ค. 35
แก้แบบวันที่ 27 ต.ค. 38
มิติเป็น —
มาตราส่วน —

แบบเลขที่ SAI-015/35026
แผ่นที่ 3 ของจำนวน 3 แผ่น