การประกอบเลขที่ ASSEMBLY NO. 3220

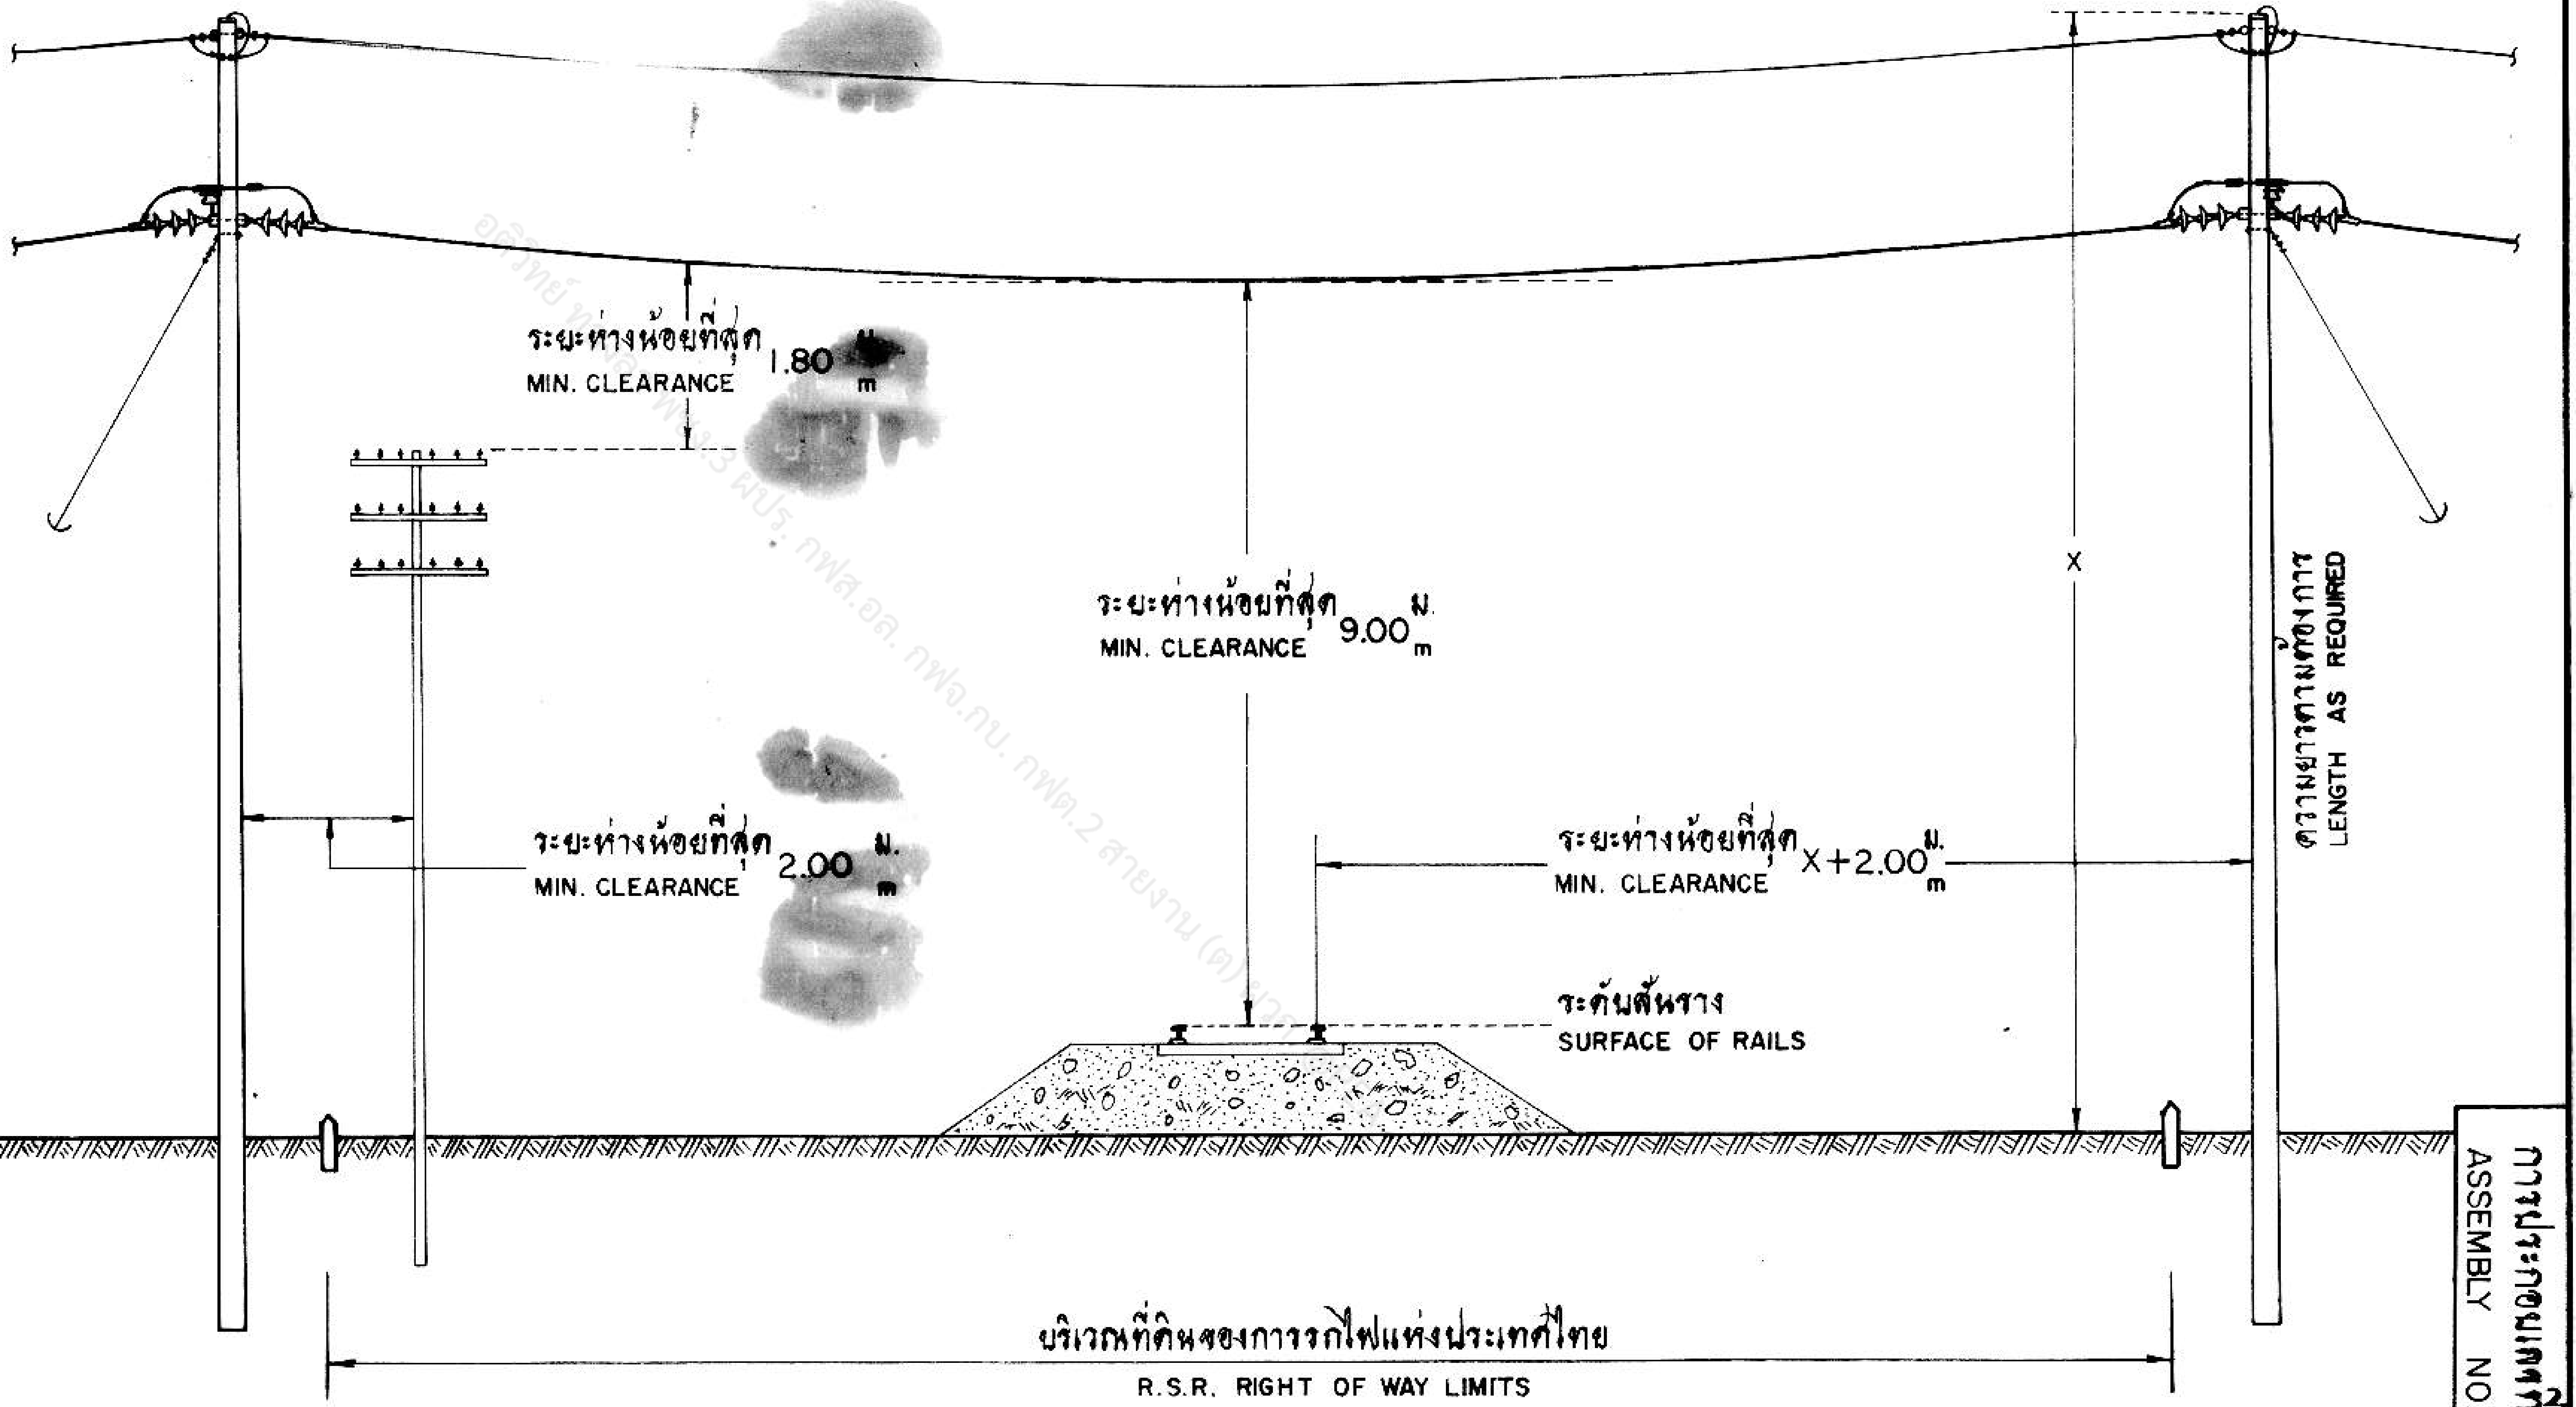
ระยะห่างน้อยที่สุด MIN. CLEARANCE 1.80 ม. m
ระยะห่างน้อยที่สุด MIN. CLEARANCE 9.00 ม. m
ระยะห่างน้อยที่สุด MIN. CLEARANCE 2.00 ม. m
ระยะห่างน้อยที่สุด MIN. CLEARANCE X+2.00 ม. m
ระดับสันราง SURFACE OF RAILS
X
ความยาวตามต้องการ LENGTH AS REQUIRED
บริเวณที่ดินของการรถไฟแห่งประเทศไทย
R.S.R. RIGHT OF WAY LIMITS

หมายเหตุ 1 ขนาดสายต่ำสุด :

อะลูมิเนียม	95 ต.มม.
อะลูมิเนียมแกนเหล็ก	35/6 ต.มม.
อะลูมิเนียมอัลลอย	35 ต.มม.

2 ถ้าระยะระหว่างเสาไม่เกิน 50ม. ใช้สายอะลูมิเนียม ขนาดไม่ต่ำกว่า 50 ต.มม.ได้

NOTES 1 MIN. CONDUCTOR SIZE :

Al	95 mm^2
ACSR	35/6 mm^2
Al-ALLOY	35 mm^2

2 MIN. Al CONDUCTOR SIZE SHALL BE REDUCED TO 50 mm^2 IF SPAN DOES NOT EXCEED 50 m

กองวิศวกรรม

ผู้เขียน
สถาปนิก
วิศวกร
หัวหน้าแผนก
ผู้อำนวยการกอง
รองผู้ว่าการฝ่ายเทคนิค

การไฟฟ้าส่วนภูมิภาค

ผู้ว่าการ ร. ร 8 ก.ค. 15

การพาดสายแรงสูง 33 kV ข้ามทางรถไฟ

33 kV LINE ACROSS THE RAILROAD

ใช้แทนแบบ 150-015/08095
ถูกแทนโดยแบบ •
เขียนเสร็จวันที่ 16 ก.ย. 19
แก้แบบวันที่
มิติเป็น –
มาตราส่วน –
แบบเลขที่ S02-015/19141
แผ่นที่ 1 ของจำนวน 1 แผ่น