
การประกอบเลขที่ 3230
ASSEMBLY NO.

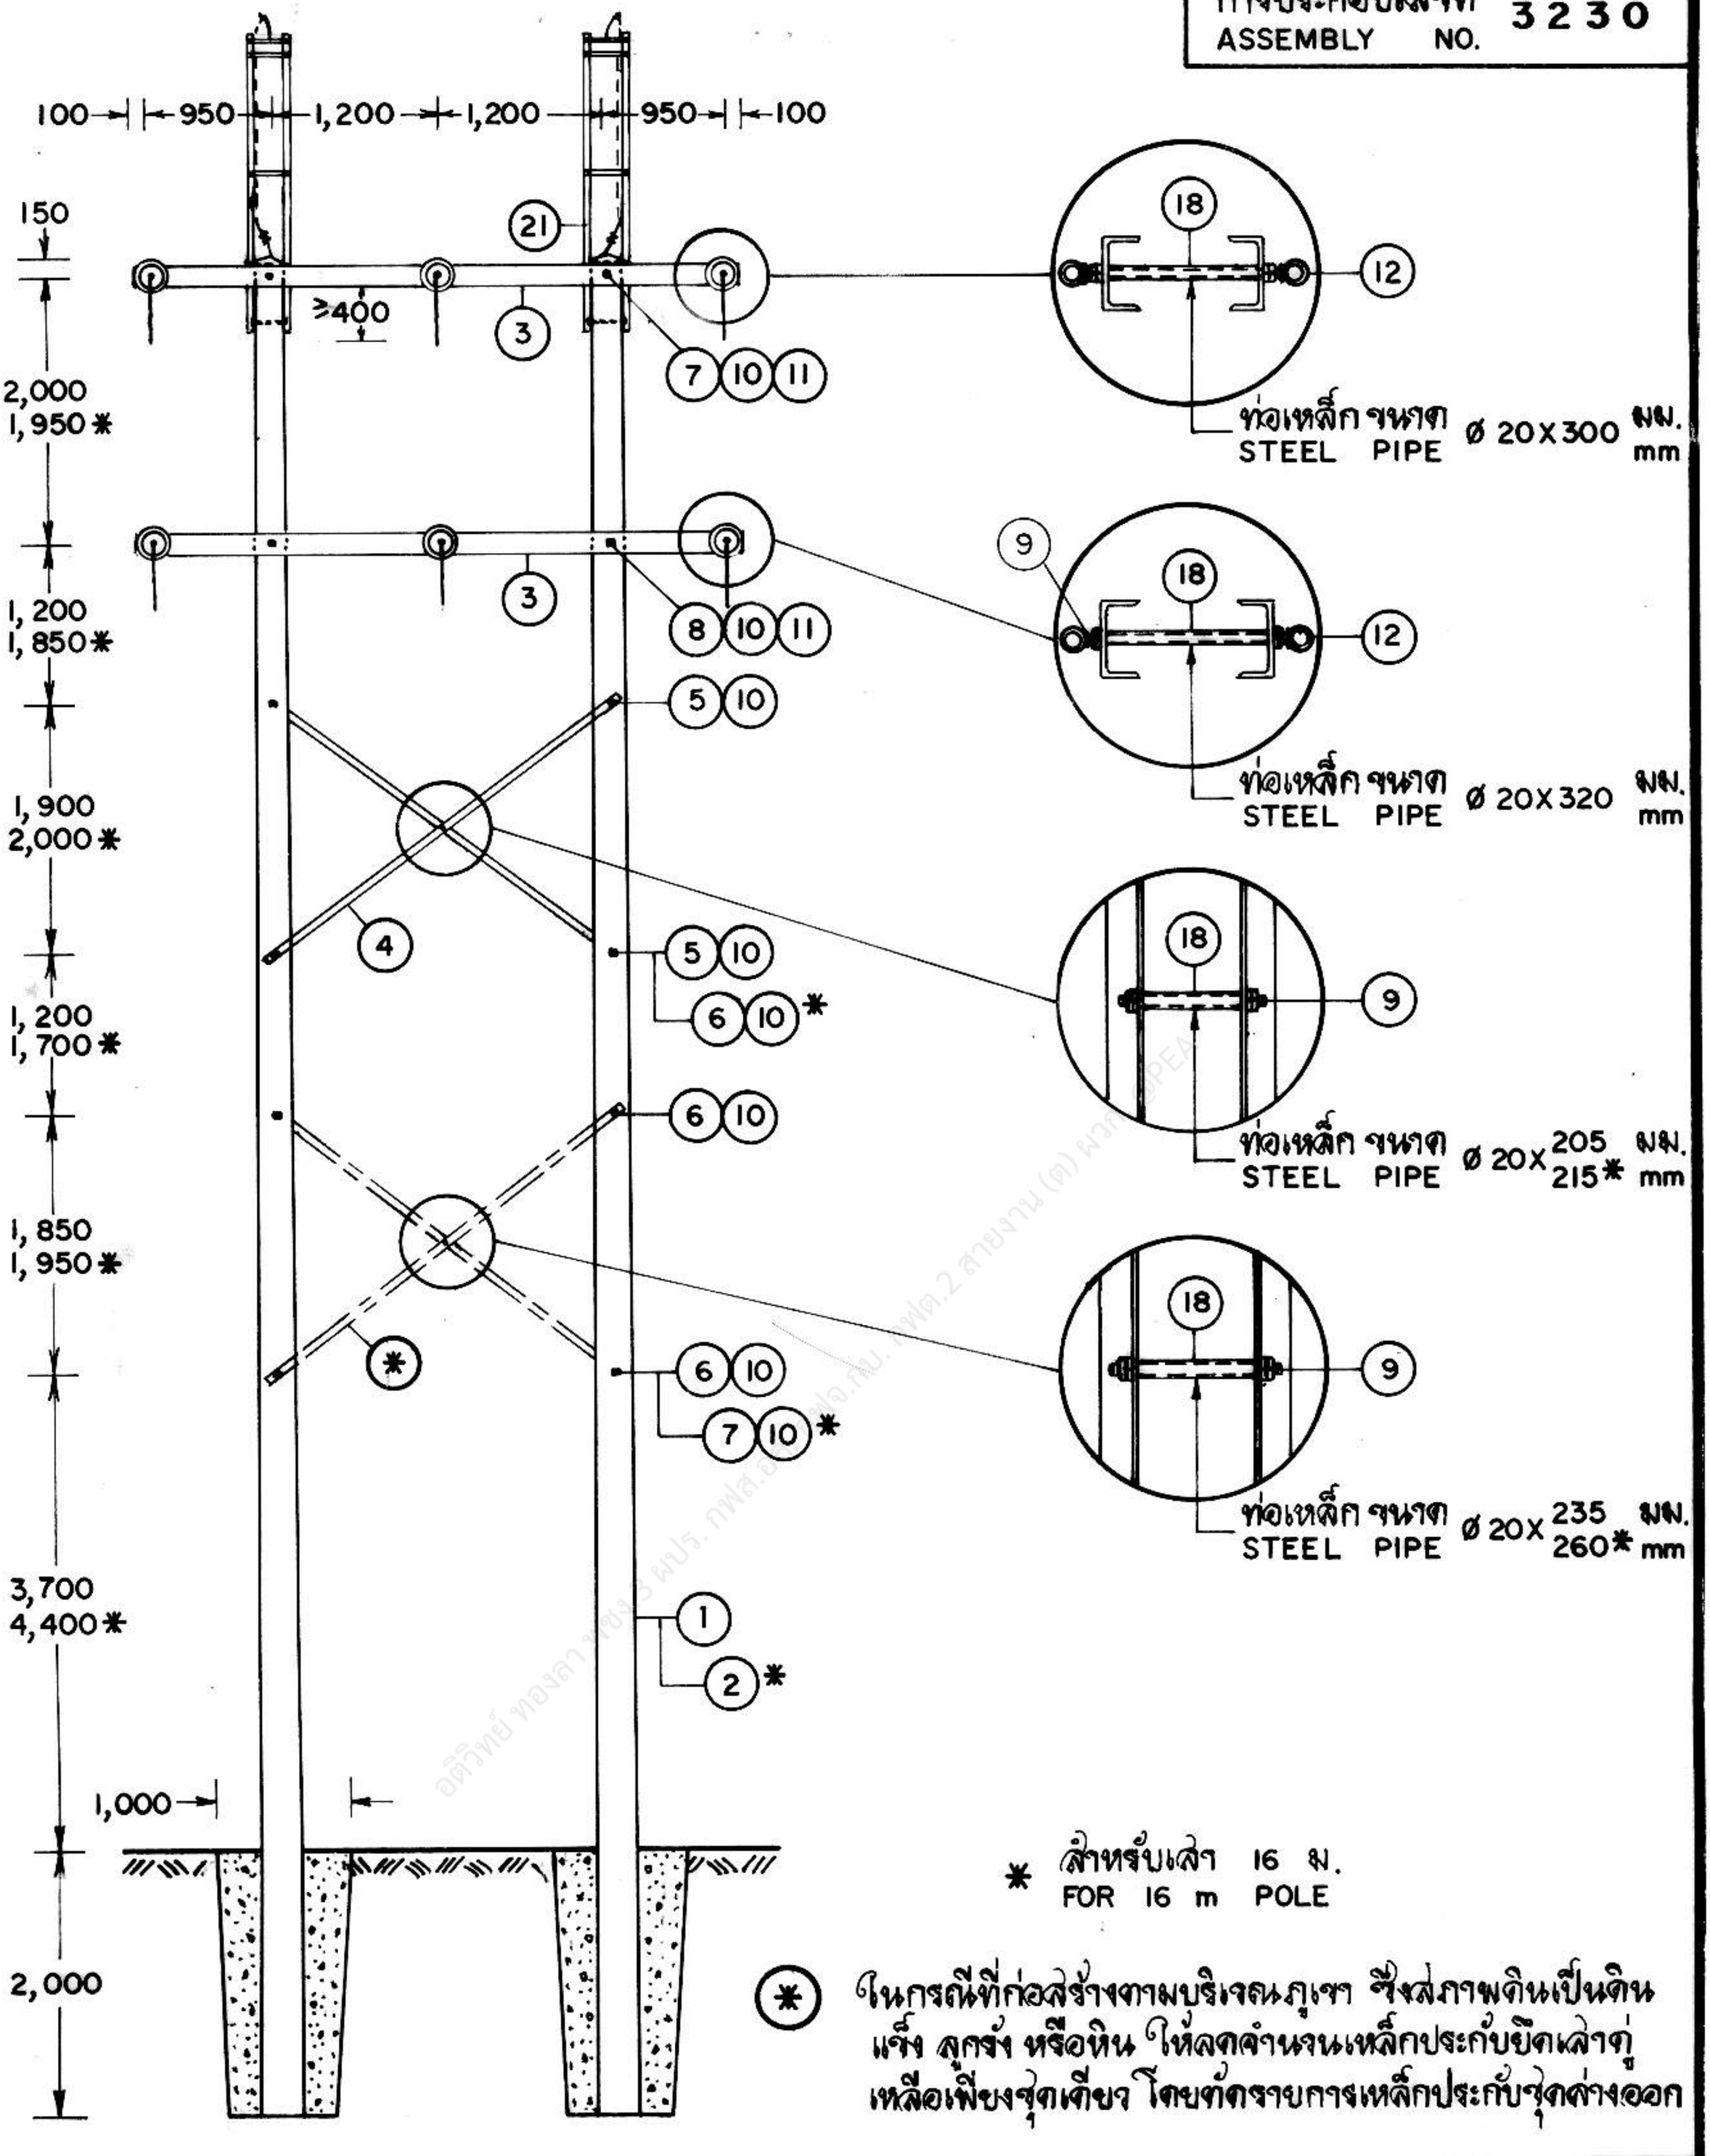


* สำหรับเสา 16 ม.
FOR 16 m POLE

(*) ในกรณีที่ก่อสร้างตามบริเวณภูเขา ซึ่งสภาพดินเป็นดินแข็ง ลูกรัง หรือหิน ให้ลดจำนวนเหล็กประกับยึดเสาคู่เหลือเพียงชุดเดียว โดยตัดรายการเหล็กประกับชุดล่างออก


กองวิศวกรรมไฟฟ้าและเครื่องกล ฝ่ายวิศวกรรม	**การไฟฟ้าส่วนภูมิภาค**	ใช้แทนแบบ ..... ถูกแทนโดยแบบ ..... เขียนเสร็จวันที่ 7 ก.ย. 33 แก้แบบวันที่ ..... มิติเป็น มิลลิเมตร มาตราส่วน 1 : 75
ผู้เขียน ... ผู้ตรวจ ..... วิศวกร ..... หัวหน้าแผนก ..... ผู้อำนวยการกอง ..... ผู้อำนวยการฝ่าย	ผู้จ่าการ ..... มาตรฐานการก่อสร้าง ระบบ 33 kV 2 วงจร ช่วง 120–200 ม. 33 kV, 2-CIRCUIT STANDARD CONSTRUCTION SPAN 120–200 m	แบบเลขที่ SAI-015/33035 แผ่นที่ 1 ของจำนวน 4 แผ่น
รองผู้จ่าการฝ่ายเทคนิค		

15 มี.ค. 2534


กากประกอบเลขที่ 3230
ASSEMBLY NO.

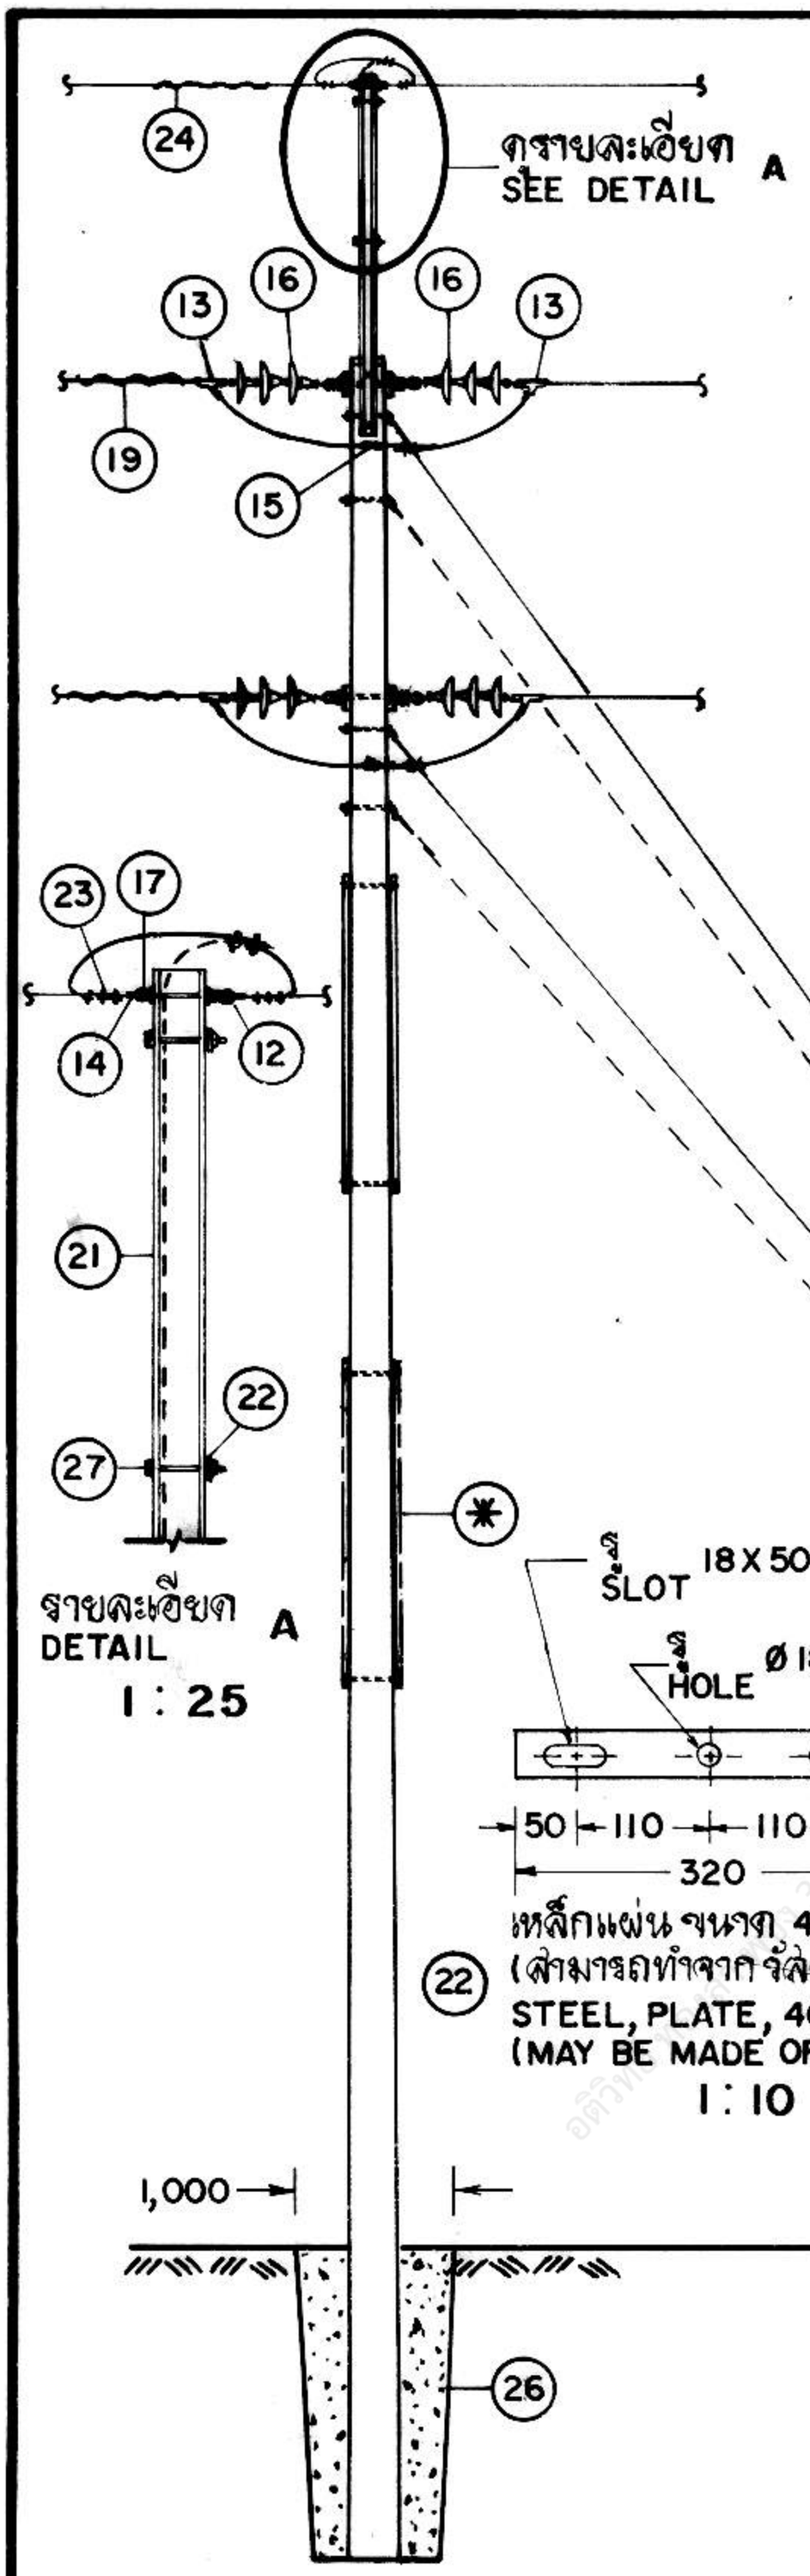

ชนิดของสายไฟฟ้า TYPE OF CONDUCTOR	พ.ท.หน้าตัดระบุ ตร.มม. NOMINAL CROSS-SECTION AREA mm^2	จำนวนสายยึดโยง ลวดเหล็กชุบสังกะสี ขนาด 95 ตร.มม. NO. OF GUY WIRE SETS (STEEL STRANDED)
อะลูมิเนียมเปลือย BARE ALUMINIUM	185	6
อะลูมิเนียมแกนเหล็ก ACSR	50/8	4
	95/15, 120/20	6
	185/30	8
อะลูมิเนียมผสม ALUMINIUM-ALLOY	50	4
	95, 120	6
	185	8

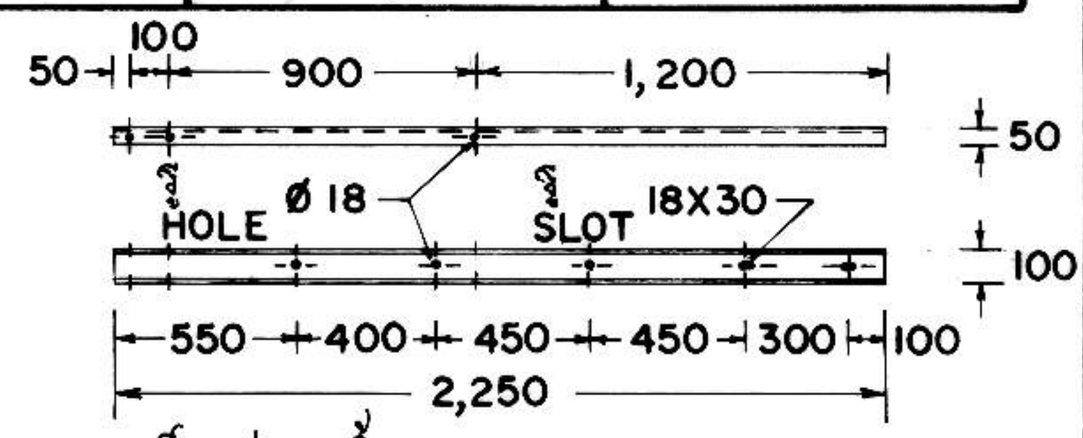


21 เหล็กรูปรางน้ำ ขนาด 100X50X5 มม. ยาว 2.25 ม.
(สามารถทำจากวัสดุเลขที่ 6012 ได้)
CHANNEL STEEL, 100X50X5 mm, 2.25m LONG
(MAY BE MADE OF MAT. NO. 6012)
1 : 40

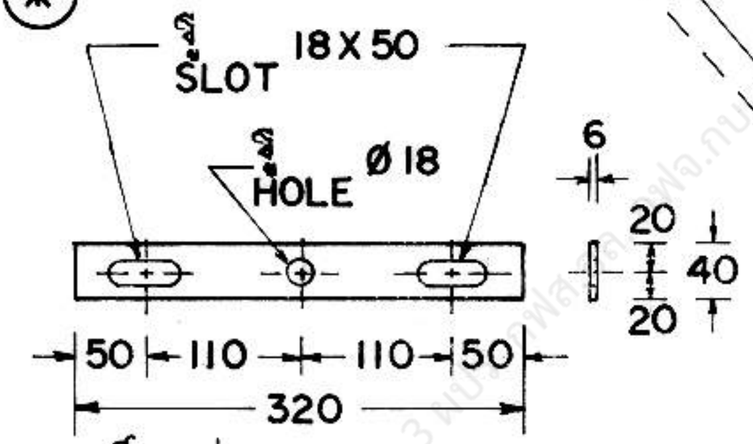


22 เหล็กแผ่น ขนาด 40X6X320 มม.
(สามารถทำจากวัสดุเลขที่ 0121 ได้)
STEEL, PLATE, 40X6X320 mm
(MAY BE MADE OF MAT. NO. 0121)
1 : 10

จำนวนสายยึดโยง ดูตารางข้างบน
NO. OF GUY WIRES SEE TABLE ABOVE

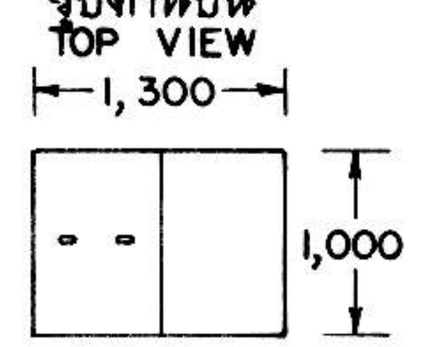

สมอบกคอนกรีต
CONCRETE ANCHOR

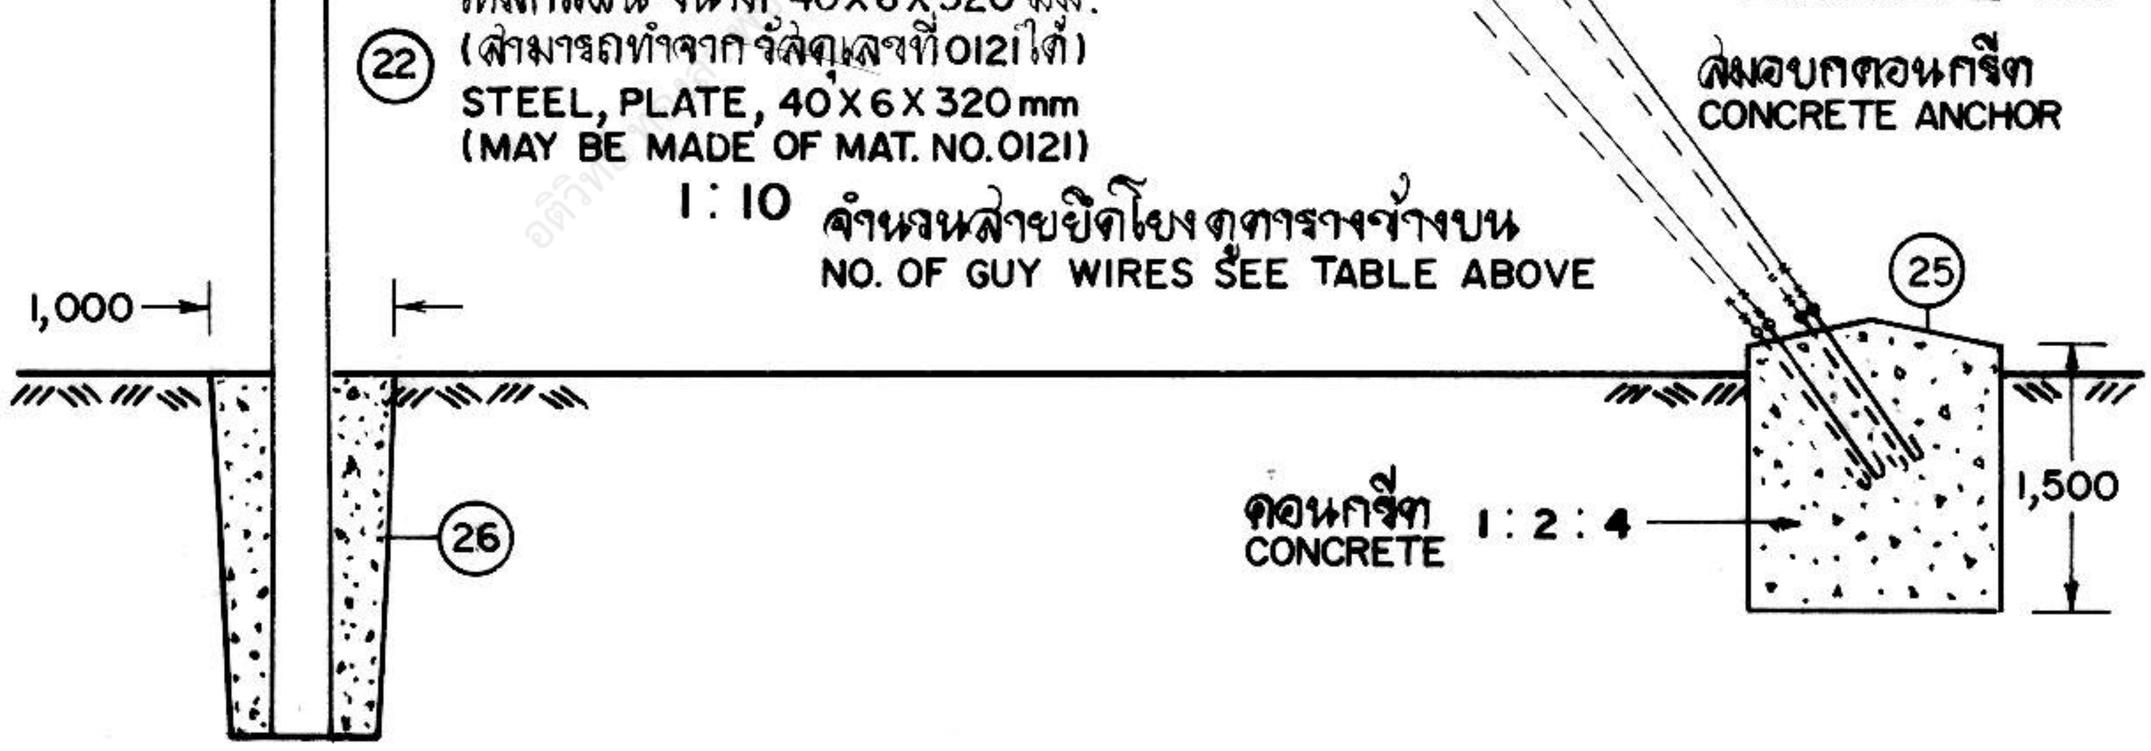

กองวิศวกรรมไฟฟ้าและเครื่องกล ฝ่ายวิศวกรรม	**การไฟฟ้าส่วนภูมิภาค**	ใช้แทนแบบ ---------- ถูกแทนโดยแบบ ---------- เขียนเสร็จวันที่ 7 ก.ย. 33 แก้แบบวันที่ ---------- มิติเป็น มิลลิเมตร มาตราส่วน 1 : 10, 1 : 75
ผู้เขียน [illegible] ผู้สำรวจ ---------- วิศวกร [illegible] หัวหน้าแผนก [illegible] ผู้อำนวยการกองฯ [illegible] ผู้อำนวยการฝ่าย [illegible]	ผู้จ่าการ [illegible]	
รองผู้จ่าการฝ่ายเทคนิค ----------	มาตรฐานการก่อสร้าง ระบบ 33 kV 2 วงจร ช่วง 120-200 ม. 33kV, 2-CIRCUIT STANDARD CONSTRUCTION SPAN 120-200 m	แบบเลขที่ SAI-015/33035 แผ่นที่ 2 ของจำนวน 4 แผ่น

16 M.A. 2534

การประกอบเลขที่ ASSEMBLY NO. **3230**

บัญชีวัสดุ
BILL OF MATERIAL

ลำดับที่ ITEM	รายละเอียด DESCRIPTION	จำนวน REQ'D I	จำนวน REQ'D II	วัสดุเลขที่ MAT. NO.
1	เสาคอนกรีต 14 ม. POLE, CONCRETE, 14 m LONG	2	—	00010006 (0036)
2	เสาคอนกรีต 16 ม. POLE, CONCRETE, 16 m LONG	—	2	00010008 (0038)
3	เหล็กรูปรางน้ำ ขนาด 150X75X6.5 มม.ยาว 4.50 ม. (น้ำหนัก 18.6 กก./ม.) STEEL, CHANNEL, 150X75X6.5 mm, 4.50 m LONG (WEIGHT 18.6 kg/m)	4	4	01000302 (0114)
4	เหล็กฉาก ขนาด 75X75X6 มม.ยาว 3.50 ม. (น้ำหนัก 6.87 กก./ม.) STEEL, ANGLE, 75X75X6 mm, 3.50 m LONG (WEIGHT 6.87 kg/m)	4 (2)	4 (2)	01010100 (0123)
5	สลักเกลียว M 16X250 มม. BOLT, MACHINE, M 16X250 mm	8	6	01110203 (0223)
6	สลักเกลียว M 16X300 มม. BOLT, MACHINE, M 16X300 mm	4 (—)	4 (2)	01110204 (0224)
7	สลักเกลียว M 16X350 มม. BOLT, MACHINE, M 16X350 mm	2	4 (2)	01110205 (0225)
8	สลักเกลียว M 16X400 มม. BOLT, MACHINE, M 16X400 mm	2	2	01110206 (0226)
9	สลักเกลียวทลอด M 16X400 มม. BOLT, DOUBLE ARMING, M 16X400 mm	8 (7)	8 (7)	01120000 (0243)
10	แหวนสี่เหลี่ยมแบน 52X52X4.5 มม.รู Ø 18 มม. มอก. 258 WASHER, SQUARE, FLAT, 52X52X4.5 mm, HOLE Ø 18 mm, TIS 258	16 (12)	16 (12)	01180100 (0355)
11	แหวนสปริง M 16 มอก. 259 WASHER, LOCK, M 16, TIS 259	4	4	01180301 (0365)
12	นัทรูปห่วง M 16 DIN 582 NUT, EYE, M 16, DIN 582	14	14	01180001 (0345)
13	สเตรนแคลัมป์ สำหรับสายอะลูมิเนียม สายอะลูมิเนียมแกนเหล็ก และสายอะลูมิเนียมเกือ CLAMP, STRAIN, FOR Al, ACSR AND Al-ALLOY CONDUCTOR, SIZE AS REQUIRED	12	12	03110000 03110101
14	กายทิมเบิล สำหรับสายยึดโยง 50-95 ต.มม. THIMBLE, GUY, FOR STEEL WIRE 50-95 mm²	4	4	01210304 (0150)
15	พีจี.คอนเนคเตอร์ 3 สลัก สำหรับสายอะลูมิเนียม CONNECTOR, PARALLEL GROOVE, TRIPLE BOLT, FOR Al	12	12	02300103 02300104
16	ลูกถ้วยแขวน แบบ ง (แบบ 52-4) มอก. 354 INSULATOR, SUSPENSION, TYPE D (CLASS 52-4) TIS 354	36	36	03020002 (0145)
17	สลักห่วงกลม M 16X200 มม. BOLT, ROUND EYE, M 16X200 mm	2	2	01140001 (0253)
18	ท่อเหล็ก ขนาด Ø 20 มม. STEEL PIPE, Ø 20 mm	8 (7)	8 (7)	—
19	ไวเบรชั่นแดมเปอร์ แบบสไปแรล VIBRATION DAMPER, SPIRAL	6	6	02200101 02200103
20	สายยึดโยง GY-32 (ลวดเหล็กตีเกลียว 95 ต.มม. ไม่รวมสมอบก) GUY GY-32 (STEEL STRANDED WIRE 95 mm², ANCHOR NOT INCLUDED)	4-8	4-8	—

กองวิศวกรรมไฟฟ้าและเครื่องกล
ฝ่ายวิศวกรรม

ผู้เขียน อนทอ.
ผู้ตรวจ
วิศวกร
หัวหน้าแผนก
ผู้อำนวยการกอง
ผู้อำนวยการฝ่าย

รองผู้ว่าการฝ่ายเทคนิค

การไฟฟ้าส่วนภูมิภาค

ผู้ว่าการ

มาตรฐานการก่อสร้างระบบ 33 kV 2 วงจร
ช่วง 120-200 ม.

33 kV, 2-CIRCUIT STANDARD CONSTRUCTION
SPAN 120-200 m

ใช้แทนแบบ
ถูกแทนโดยแบบ
เขียนแล้วเสร็จวันที่ 7 ก.ย. 33
แก้แบบจนที่
มิติเป็น
มาตราส่วน

แบบเลขที่ SAI-015/33035
แผ่นที่ 3 จากจำนวน 4 แผ่น

16 มี.ค. 2534

การประกอบเลขที่ ASSEMBLY NO. 3230

บัญชีวัสดุ BILL OF MATERIAL

ลำดับที่ ITEM	รายละเอียด DESCRIPTION	จำนวน REQ'D I	จำนวน REQ'D II	รหัสเลขที่ MAT. NO.
21	เหล็กรูปรางน้ำ ขนาด 100X50X5 มม. ยาว 2.25 ม. STEEL, CHANNEL, 100X50X5 mm, 2.25 m LONG	4	4	—
22	เหล็กแผ่น ขนาด 40X6X320 มม. STEEL, PLATE, 40X6X320 mm	12	12	—
23	ยูแคลมป์ สลัก 1 ตัว M 8 CLAMP, SINGLE U-BOLT, M 8	20	20	01230000 (0165)
24	ไวเบรชั่นแดมเปอร์ แบบสไปแรล สำหรับลวดเหล็กตีเกลียว 25 ต.มม. VIBRATION DAMPER, SPIRAL, FOR STEEL STRANDED 25 mm^2	2	2	02200100 (0903)
25	สมอบกคอนกรีต 1.00X1.30X1.50 ม. (คอนกรีต 1 : 2 : 4) CONCRETE ANCHOR 1.00X1.30X1.50 m (CONCRETE 1 : 2 : 4)	2	2	—
26	คอนกรีต 1 : 3 : 5 CONCRETE 1 : 3 : 5	ลบ.ม. 4 m^3	ลบ.ม. 4 m^3	—
27	สลักเกลียว M 16X130 มม. BOLT, MACHINE, M 16X130 mm	12	12	

บัญชีวัสดุ สดมภ์ I สำหรับเสาคอนกรีต 14 ม., สดมภ์ II สำหรับเสาคอนกรีต 16 ม. และจำนวนในวงเล็บใช้สำหรับกรณีก่อสร้างตามบริเวณภูเขา ซึ่งสภาพดินเป็นดินแข็ง ลูกรัง หรือหิน

หมายเหตุ

1. ระยะห่างที่ปลอดภัยในการก่อสร้างทางไฟฟ้า ดูแบบเลขที่ SO2-015/17068 (การประกอบเลขที่ 9301)
2. สายไฟฟ้าต้องมีระดับดจากสูงเหนือยอดของต้นไม้ใหญ่น้อยกว่า 2.10 ม.
3. ระยะช่วงเสา สำหรับสายไฟฟ้า :
   อะลูมิเนียมเปลือย 185 ต.มม. ระยะช่วงเสาไม่เกิน 150 ม. (สำหรับสายขนาดอื่นไม่สมควรใช้)
   อะลูมิเนียมแกนเหล็ก อะลูมิเนียมอัลลอย ระยะช่วงเสาเกิน 100 ม.
4. อุปกรณ์ที่เป็นเหล็ก เจาะรูขนาด ø 18X50 มม. อาบ—สังกะสี หรือทาด้วยสีกันสนิม
5. ในกรณีสภาพดินอ่อนให้ใช้เสาตอม่อ หรือฐานคอนกรีตสำหรับเสาไฟฟ้า
6. ระยะระหว่างสมอบกกับโครงสร้างเสา ประมาณ 8.50 ม.
7. ระยะหย่อนยานของสายไฟฟ้าทุกเส้น :
   อย่างน้อย 5 ม. (สำหรับสายอะลูมิเนียมแกนเหล็ก 185/30 ต.มม. : อย่างน้อย 6 ม.)
8. การประกอบไวเบรชั่นแดมเปอร์ ดูแบบเลขที่ SAI-015/22019 (การประกอบเลขที่ 9557)

NOTES

1. SAFETY CLEARANCES FOR ELECTRICAL CONSTRUCTION, SEE DWG. NO. SO2-015/17068 (ASSEMBLY NO. 9301).
2. CONDUCTORS SHALL BE ABOVE TOP OF TREES OF NOT LESS THAN 2.10 m .
3. LIMITING SPAN FOR CONDUCTOR :
   BARE ALUMINIUM CONDUCTOR 185 mm^2, SPAN NOT EXCEED 150 m (OTHER SIZE DO NOT ALLOW).
   ACSR, ALUMINIUM ALLOY, SPAN EXCEED 100 m .
4. DRILL Ø 18X50 mm FOR STEEL PARTS AND SHALL BE GALVANIZED OR COATED WITH RUST-RESISTING PAINT .
5. FOR BAD SOIL CONDITION, STUB POLE OR CONCRETE FOUNDATION FOR CONCRETE POLE SHALL BE USED .
6. DISTANCE BETWEEN ANCHOR AND POLE STRUCTURE IS APPROX. 8.50 m .
7. SAG OF ALL CONDUCTORS :
   MIN. 5 m (BUT FOR ACSR 185/30 mm^2 : MIN. 6 m).
8. VIBRATION DAMPER ASSEMBLY, SEE DWG. NO. SAI-015/22019 (ASSEMBLY NO. 9557) .

กองวิศวกรรมไฟฟ้าและเครื่องกล ฝ่ายวิศวกรรม	**การไฟฟ้าส่วนภูมิภาค**	ใช้แทนแบบ _____ ถูกแทนโดยแบบ _____ เขียนเสร็จวันที่ 7 ก.ย. 33 แก้แบบวันที่ _____ มิติเป็น _____ มาตราส่วน _____
ผู้เขียน [illegible] ผู้ลำดวก _____ วิศวกร [illegible] หัวหน้าแผนก [illegible] ผู้อำนวยการกอง [illegible] ผู้อำนวยการฝ่าย [illegible]	ผู้จ่าการ _____	
รองผู้จ่าการฝ่ายเทคนิค	มาตรฐานการก่อสร้าง ระบบ 33 kV 2 วงจร ช่วง 120-200 ม. 33 kV, 2-CIRCUIT STANDARD CONSTRUCTION SPAN 120-200 m	แบบเลขที่ SAI-015/33035 แผ่นที่ 4 ของจำนวน 4 แผ่น

15 มี.ค. 2534