การประกอบเลขที่ ASSEMBLY NO.	3212 A

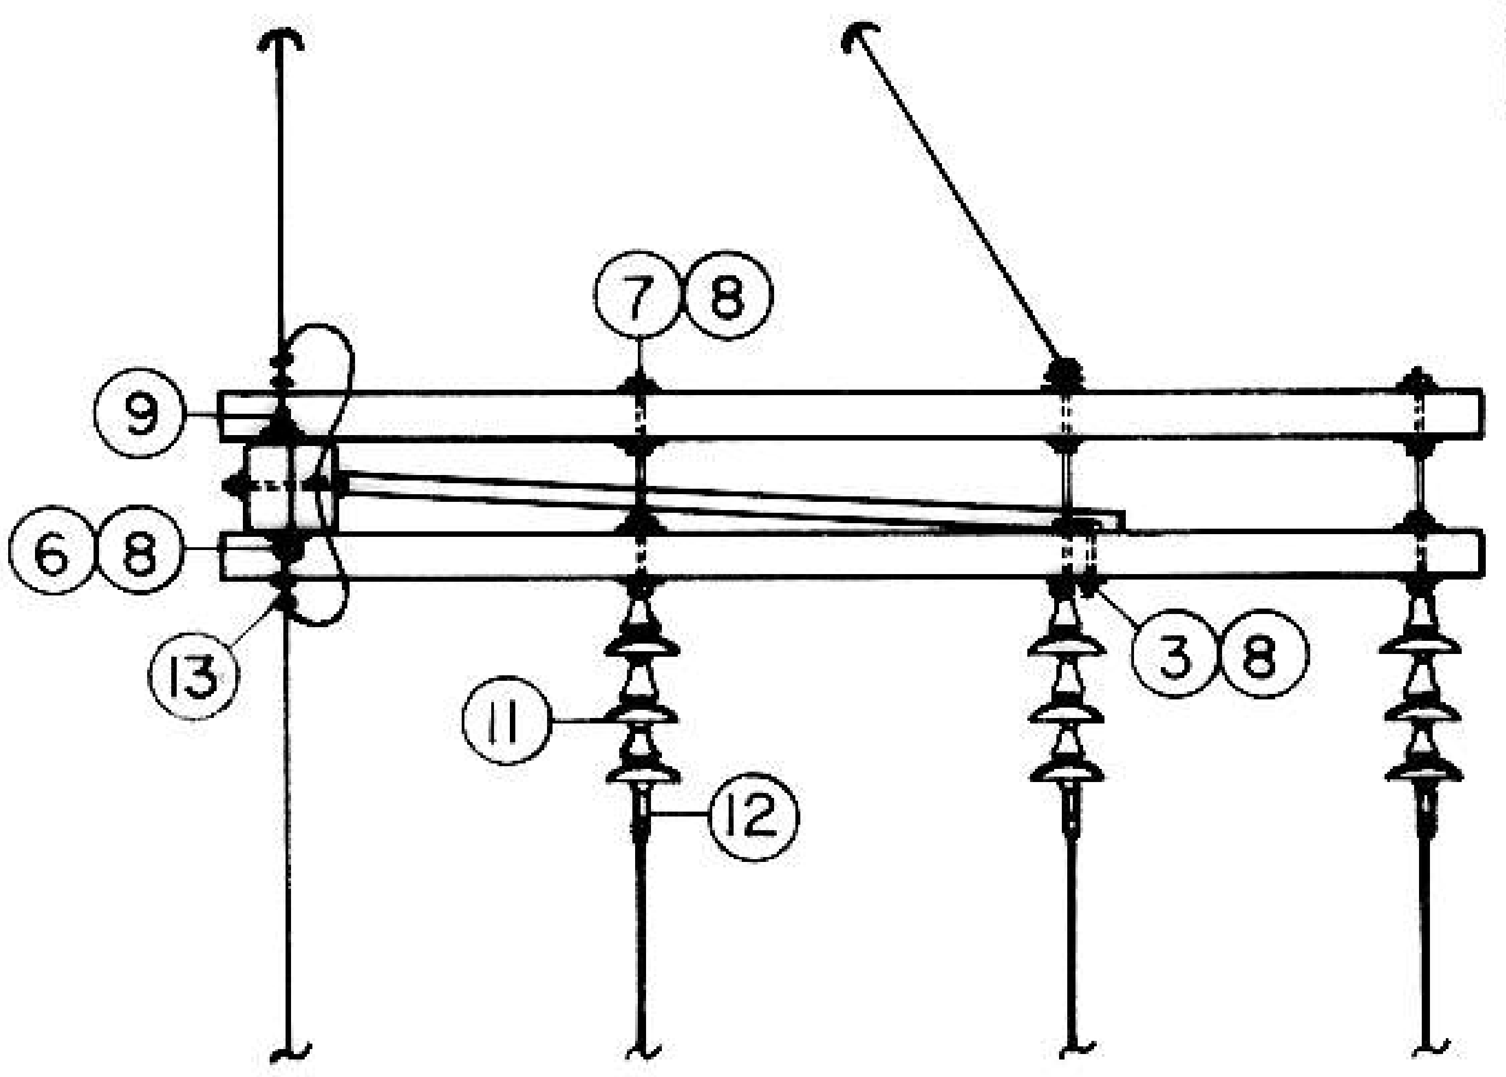

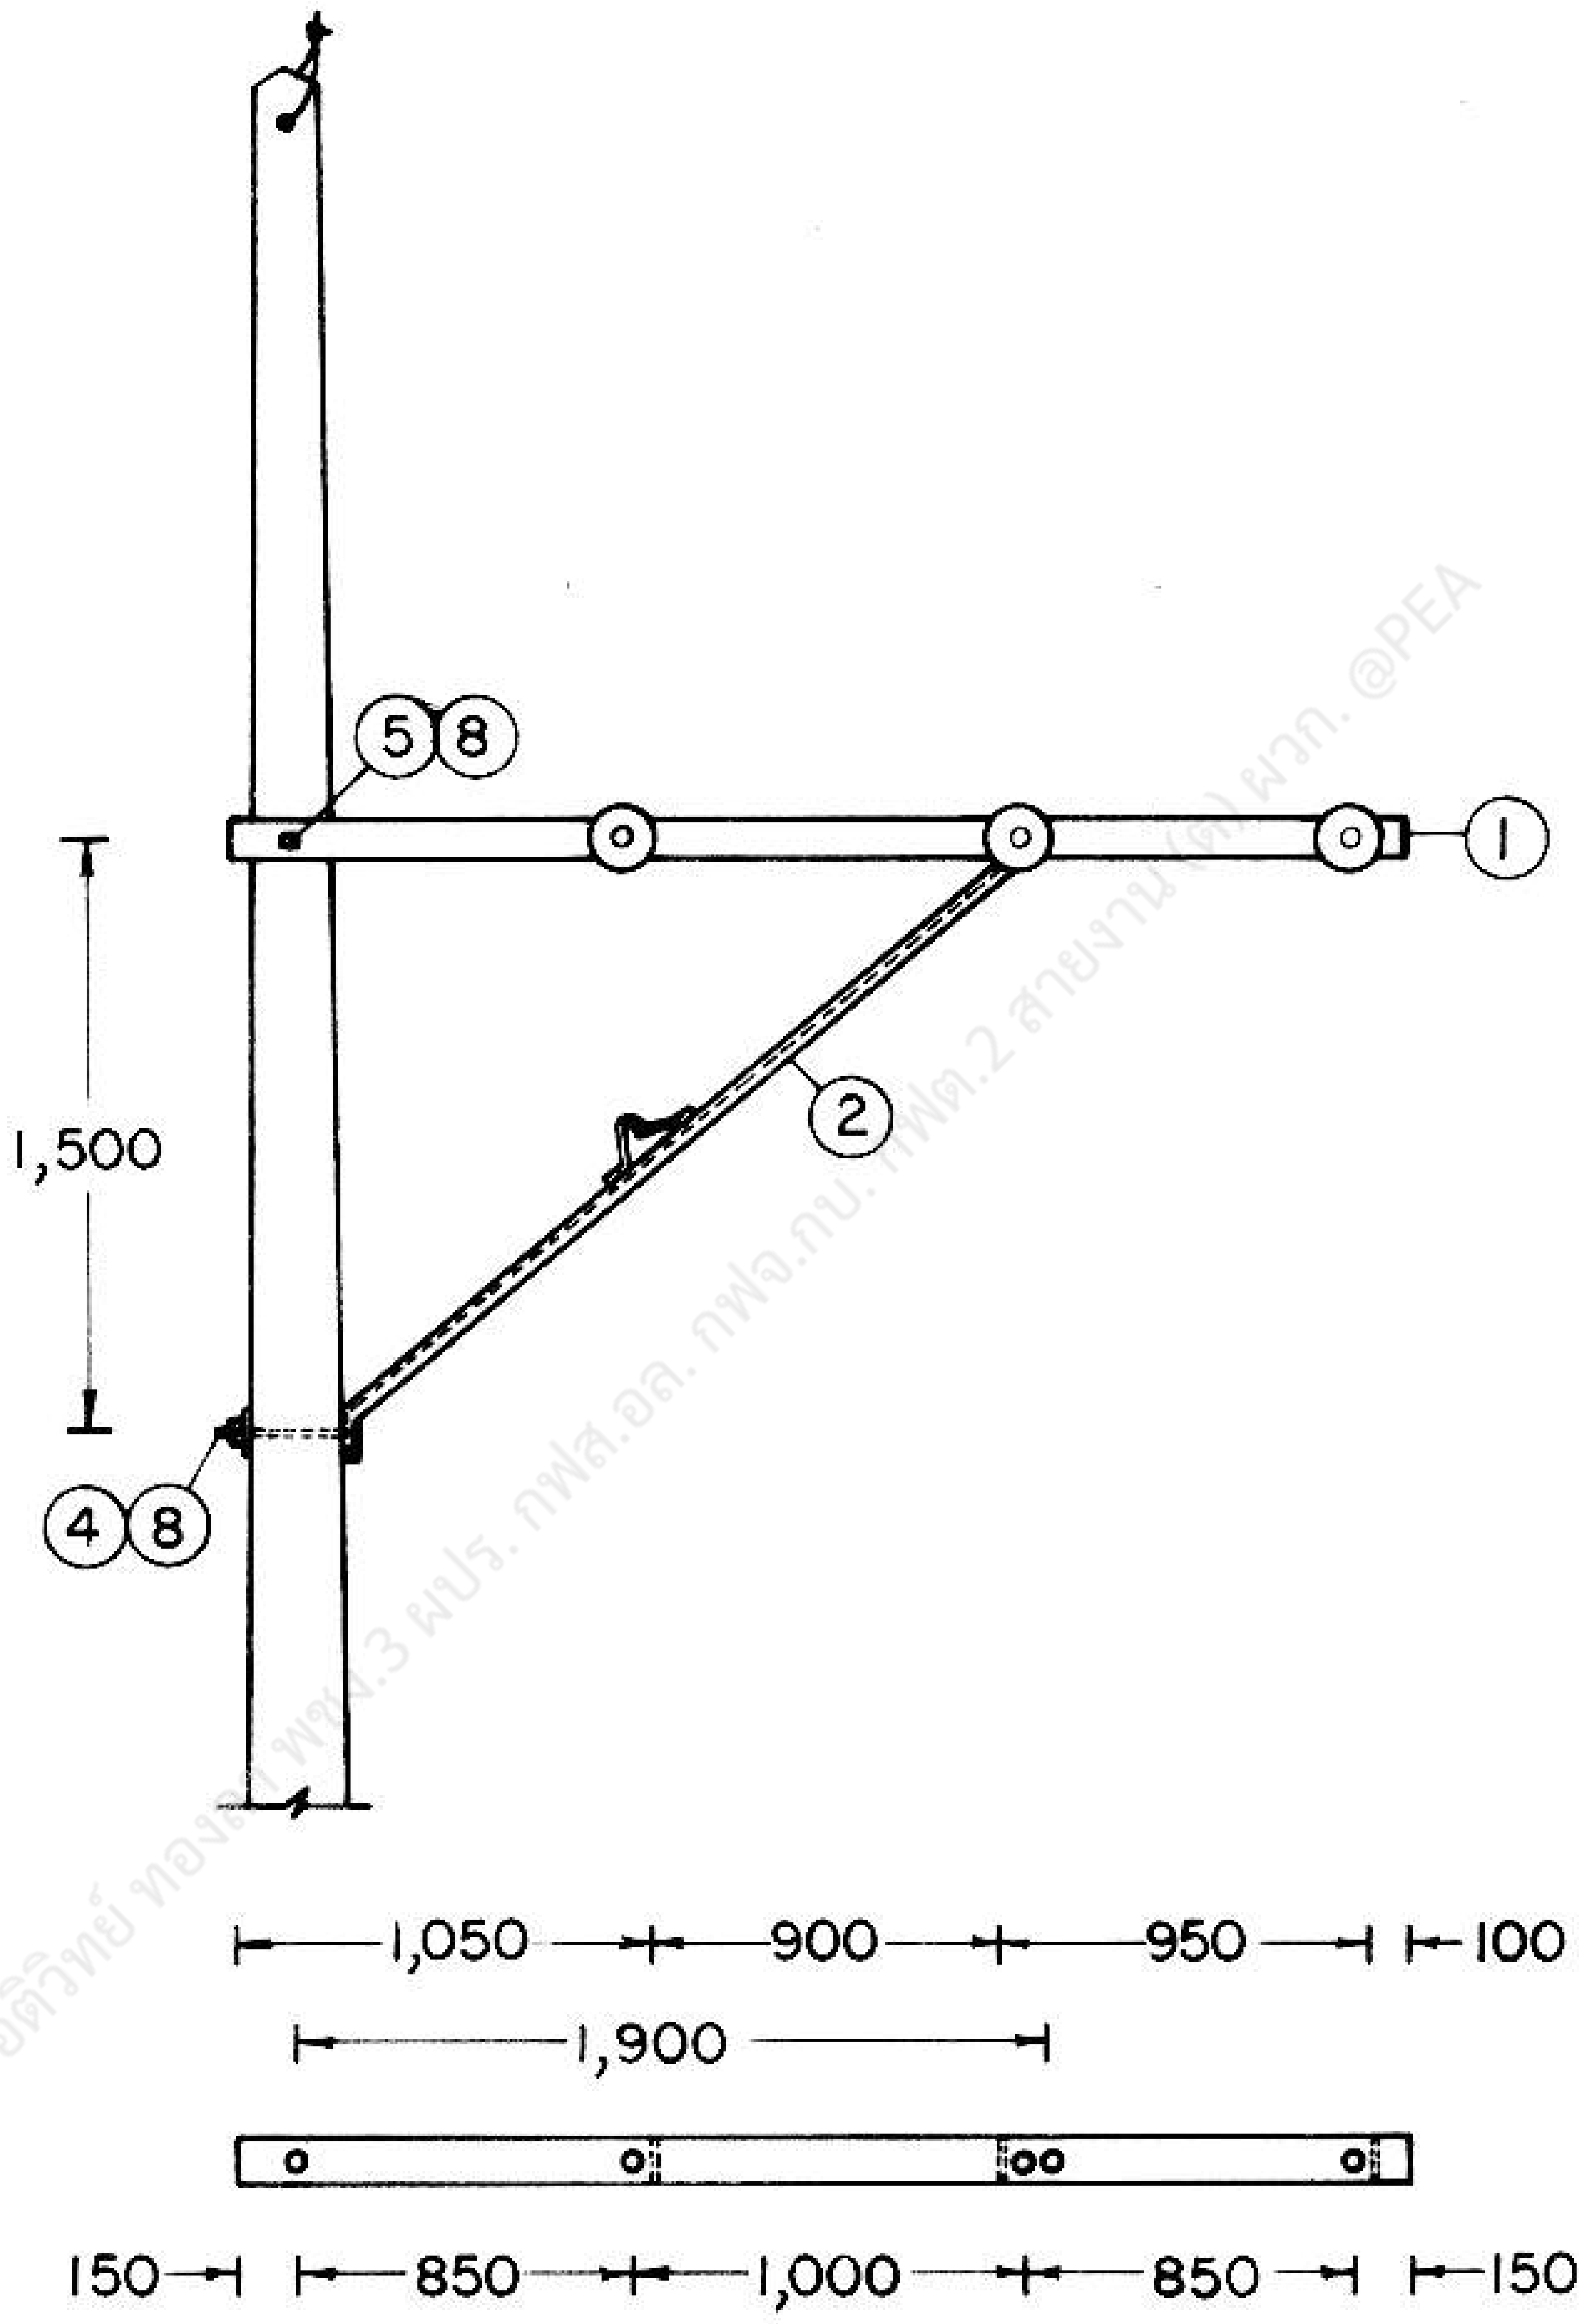

แบบที่ 1 สำหรับการก่อสร้างเข้าปลายสายเสาต้นสุดท้าย
TYPE 1 FOR DEADEND POLE CONSTRUCTION

อดิวิทย์ ทองอด พชน.3 ผปร. กฟส.อล. กฟจ.กบ. ฟพต.2 สายงาน (ต) ผวก. @PEA

กองวิศวกรรมไฟฟ้าและเครื่องกล ฝ่ายวิศวกรรม	การไฟฟ้าส่วนภูมิภาค	ใช้แทนแบบ ถูกแทนโดยแบบ
ผู้เขียน ผู้สำรวจ วิศวกร หัวหน้าแผนก ชัยรัตน์ หัวหน้ากอง ผู้อำนวยการฝ่าย	ผู้ว่าการ 13 ธ.ค.๒๑	เขียนเสร็จวันที่ 13 พ.ย. 21 แก้แบบวันที่
	การติดตั้งอุปกรณ์ที่เสาเข้าปลายสายแบบก้าวแขน ระบบ 33 kV	มิติเป็น มม. มาตราส่วน 1 : 50
รองผู้ว่าการฝ่ายเทคนิค	DEADEND CONSTRUCTION ON ALLEY ARM 33 kV SYSTEM	แบบเลขที่ SAI-015/21068 แผ่นที่ 1 ของจำนวน 3 แผ่น

การประกอบเลขที่
ASSEMBLY NO. **3212 A**

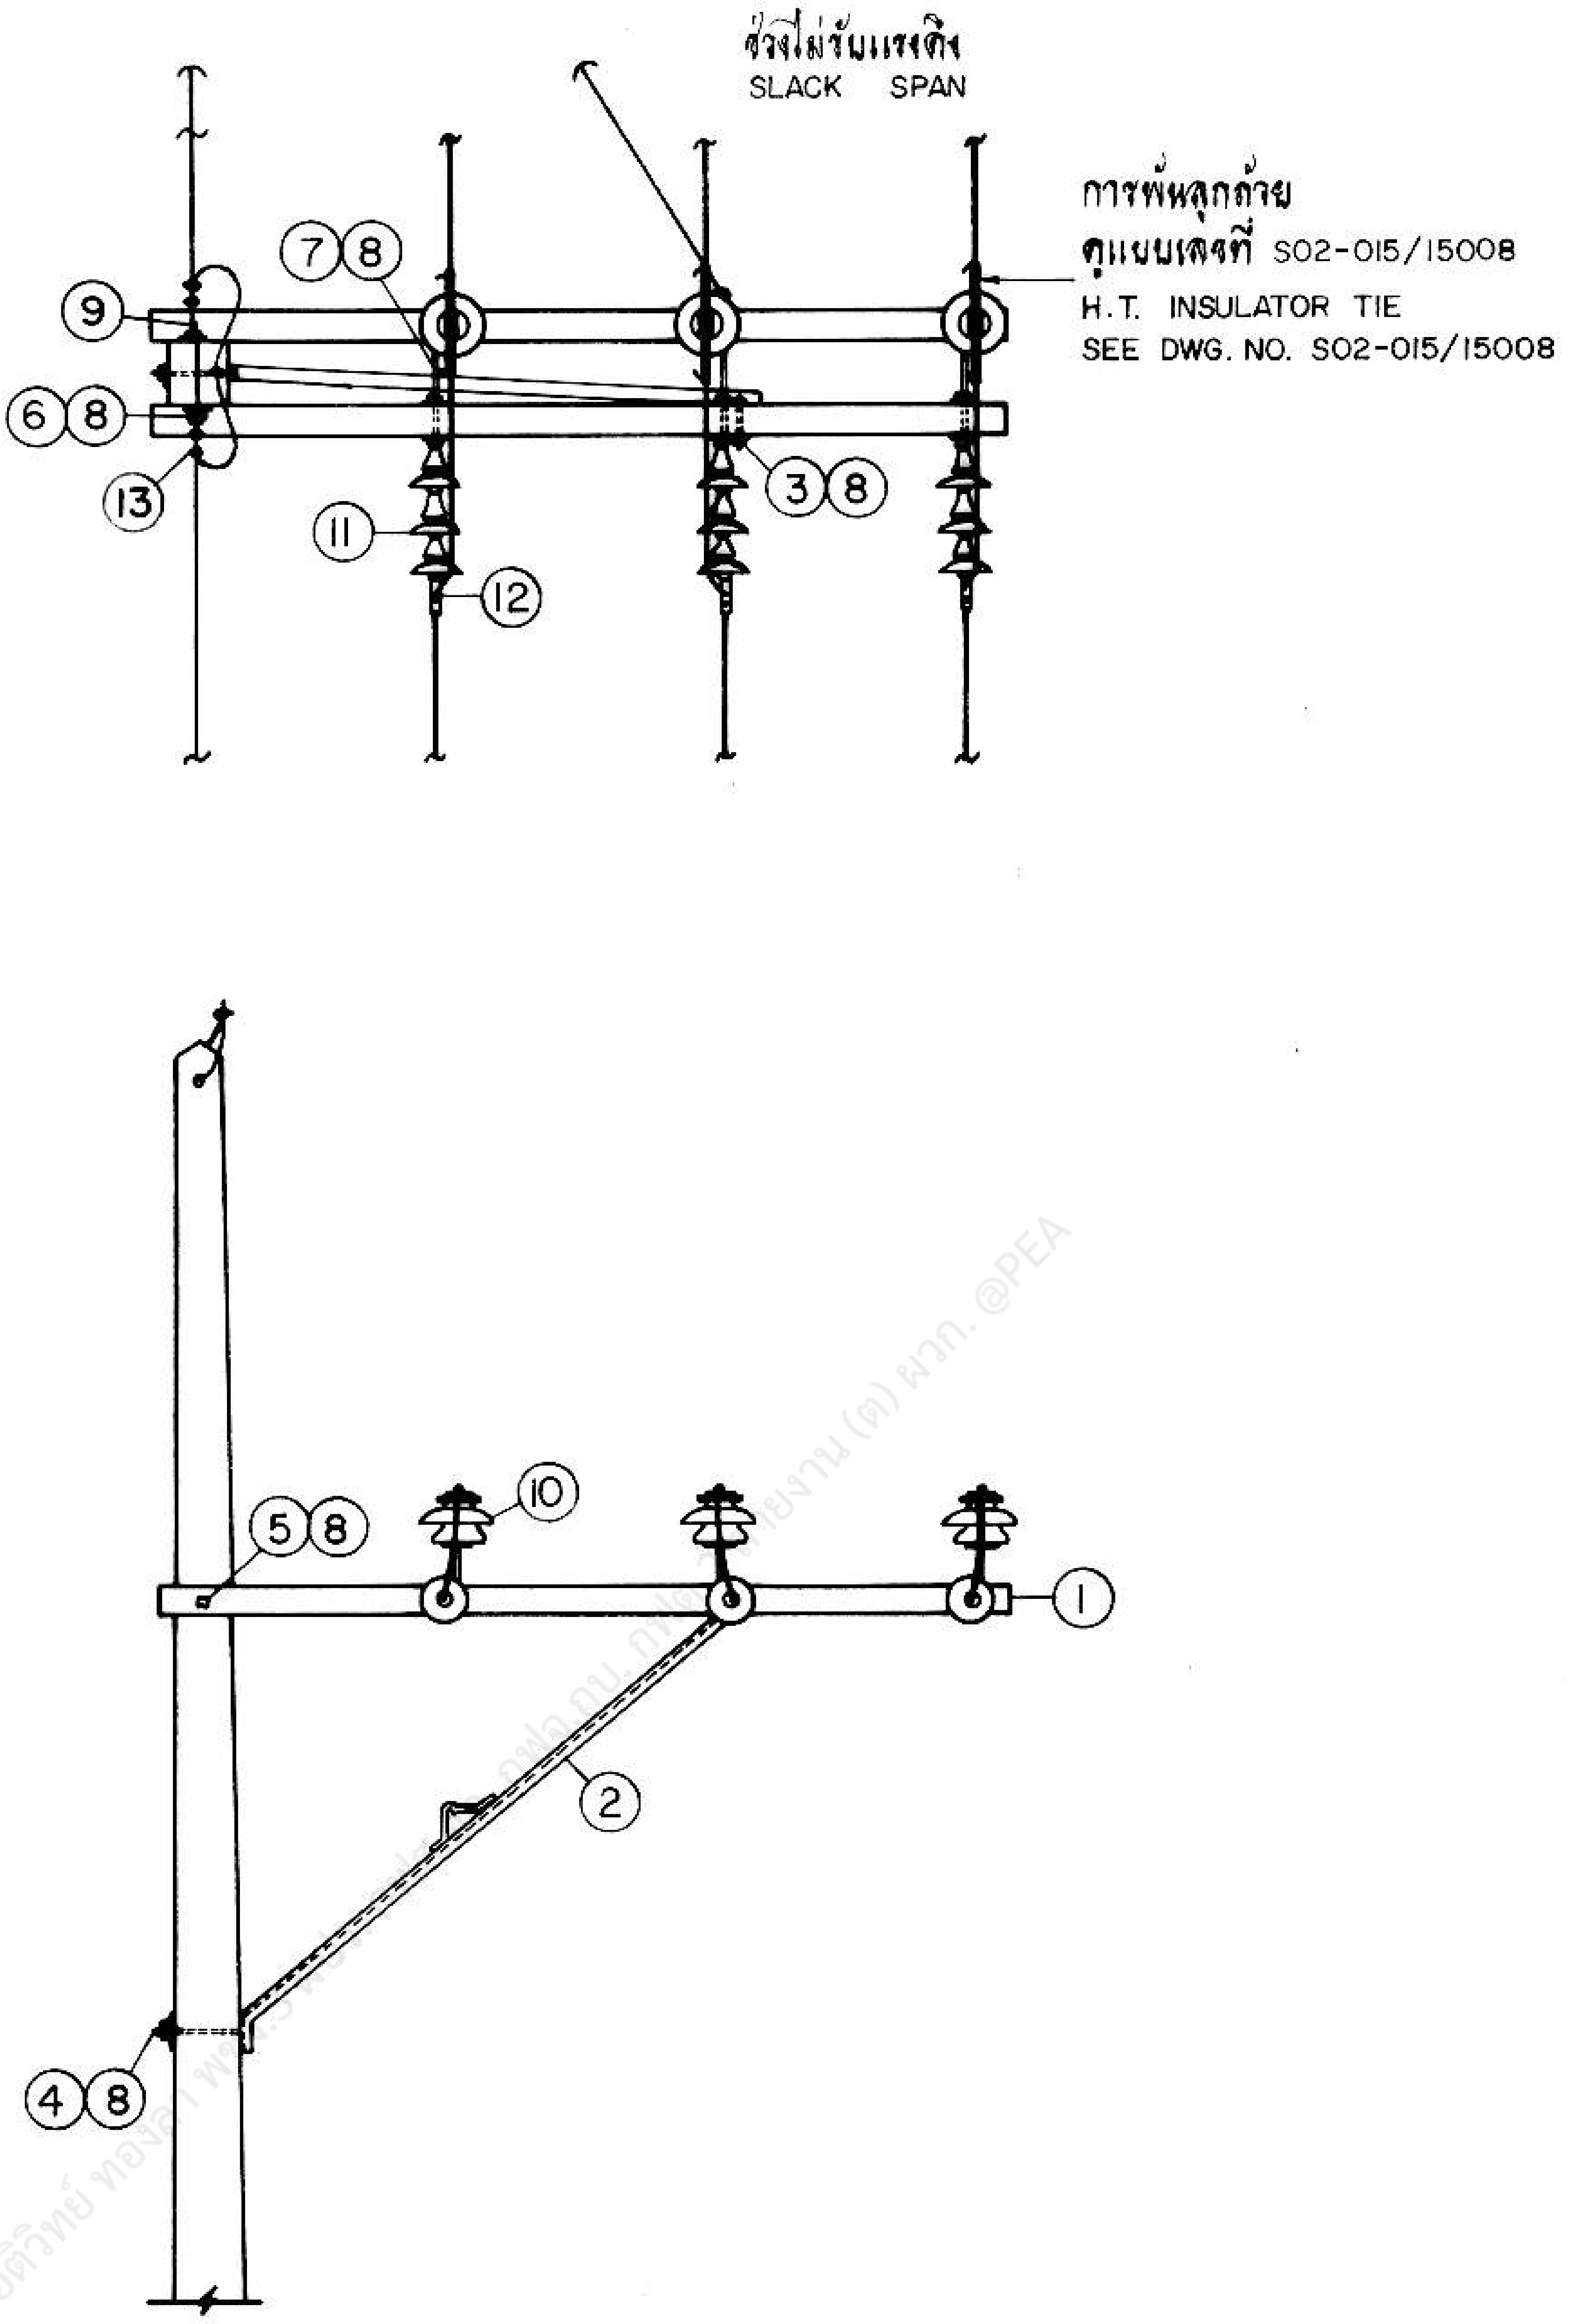

แบบที่ 2 สำหรับการก่อสร้างช่วงไม่รับแรงดึง
TYPE 2 FOR SLACK SPAN CONSTRUCTION

กองวิศวกรรมไฟฟ้าและเครื่องกล ฝ่ายวิศวกรรม	**การไฟฟ้าส่วนภูมิภาค**	ใช้แทนแบบ ถูกแทนโดยแบบ
ผู้เขียน ผู้สำรวจ วิศวกร หัวหน้าแผนก ชัยรัตน์ หัวหน้ากอง ผู้อำนวยการฝ่าย	ผู้ว่าการ 13 ธ.ค. 21	เขียนเสร็จวันที่ 13 พ.ย. 21 แก้แบบวันที่ มิติเป็น มม. มาตราส่วน 1 : 50
	การติดตั้งอุปกรณ์ที่เสาเจ้าปลายสายแบบท้าวแขน ระบบ 33 kV	
รองผู้ว่าการฝ่ายเทคนิค	DEADEND CONSTRUCTION ON ALLEY ARM 33 kV SYSTEM	แบบเลขที่ SAI-015/21068 แผ่นที่ 2 ของจำนวน 3 แผ่น

การประกอบเลขที่
ASSEMBLY NO. 3212 A

บัญชีวัสดุ
BILL OF MATERIAL

ลำดับที่ ITEM	รายละเอียด DESCRIPTION	จำนวน REQ'D 1	จำนวน REQ'D 2	วัสดุเลขที่ MAT. NO.
1	ไม้คอนสายแรงสูง 100 X 120 X 3,000 มม. CROSSARM, WOOD, H.T. 100 X 120 X 3,000 mm	2	2	00100003 (0101)
2	เหล็กประกับไม้คอนแบบท้าวแขน 50 X 50 X 5 มม. ยาว 2,350 มม. BRACE, ALLEY ARM 50 X 50 X 5 mm 2,350 mm LONG	1	1	01200005 (0125)
3	สลักเกลียว M 16 X 130 มม. BOLT, MACHINE, M 16 X 130 mm	1	1	01110200 (0220)
4	สลักเกลียว M 16 X 250 มม. BOLT, MACHINE, M 16 X 250 mm	1	1	01110203 (0223)
5	สลักเกลียว M 16 X 450 มม. BOLT, MACHINE, M 16 X 450 mm	1	1	01110207 (0227)
6	สลักห่วงกลม M 16 X 200 มม. BOLT, ROUND EYE, M 16 X 200 mm	1	1	01140001 (0253)
7	สลักเกลียวห่วงกลม 16 X 450 มม. BOLT, DOUBLE ARMING, ROUND EYE, M 16 X 450 mm	3	3	01130001 (0247)
8	แหวนสี่เหลี่ยมแบน 52 X 52 X 4.5 มม. รู Ø 18 มม. มอก. 258 WASHER, SQUARE, FLAT 52 X 52 X 4.5 mm HOLE Ø 18 mm TIS 258	18	18	01180100 (0355)
9	นัทรูปห่วง M 16 DIN 582 NUT, EYE M 16 DIN 582	-	1	01180001 (0345)
10	ลูกถ้วยก้านตรง 33 kV มอก. 279 แบบ ค (แบบ 56-3) พร้อมก้าน INSULATOR, PIN TYPE, 33 kV TIS 279 TYPE C (CLASS 56-3) COMP. WITH PIN	-	3	03000002 03100001
11	ลูกถ้วยแขวน มอก. 354 แบบ ง (แบบ 52-4) INSULATOR, SUSPENSION TYPE, TIS 354 TYPE D (CLASS 52-4)	9	9	03020002 (0415)
12	สเตรนแคล้มป์ สำหรับสายอะลูมิเนียม และอะลูมิเนียมแกนเหล็ก ขนาดตามต้องการ CLAMP, STRAIN, FOR Al AND ACSR SIZE AS REQUIRED	3	3	03110000 03110101
13	ยูแคล้มป์ สลัก 1 ตัว M 8 (ไวร์ โร้ป คลิ๊พ) CLAMP, SINGLE U-BOLT M 8 (WIRE ROPE CLIP)	2	2	01230000 (0165)

กองวิศวกรรมไฟฟ้าและเครื่องกล
ฝ่ายวิศวกรรม

ผู้เขียน
ผู้สำรวจ
วิศวกร
หัวหน้าแผนก
หัวหน้ากอง
ผู้อำนวยการฝ่าย
รองผู้ว่าการฝ่ายเทคนิค

การไฟฟ้าส่วนภูมิภาค

ผู้ว่าการ 13 ธ.ค. 21

การติดตั้งอุปกรณ์ที่เสาเข้าปลายสายแบบท้าวแขน
ระบบ 33 kV

DEADEND CONSTRUCTION ON ALLEY ARM
33 kV SYSTEM

ใช้แทนแบบ
ถูกแทนโดยแบบ
เขียนเสร็จวันที่ 13 พ.ย. 21
แก้แบบวันที่
มิติเป็น
มาตราส่วน

แบบเลขที่ SAI-015/21068
แผ่นที่ 3 ของจำนวน 3 แผ่น