การประกอบเลขที่ ASSEMBLY NO. 0302

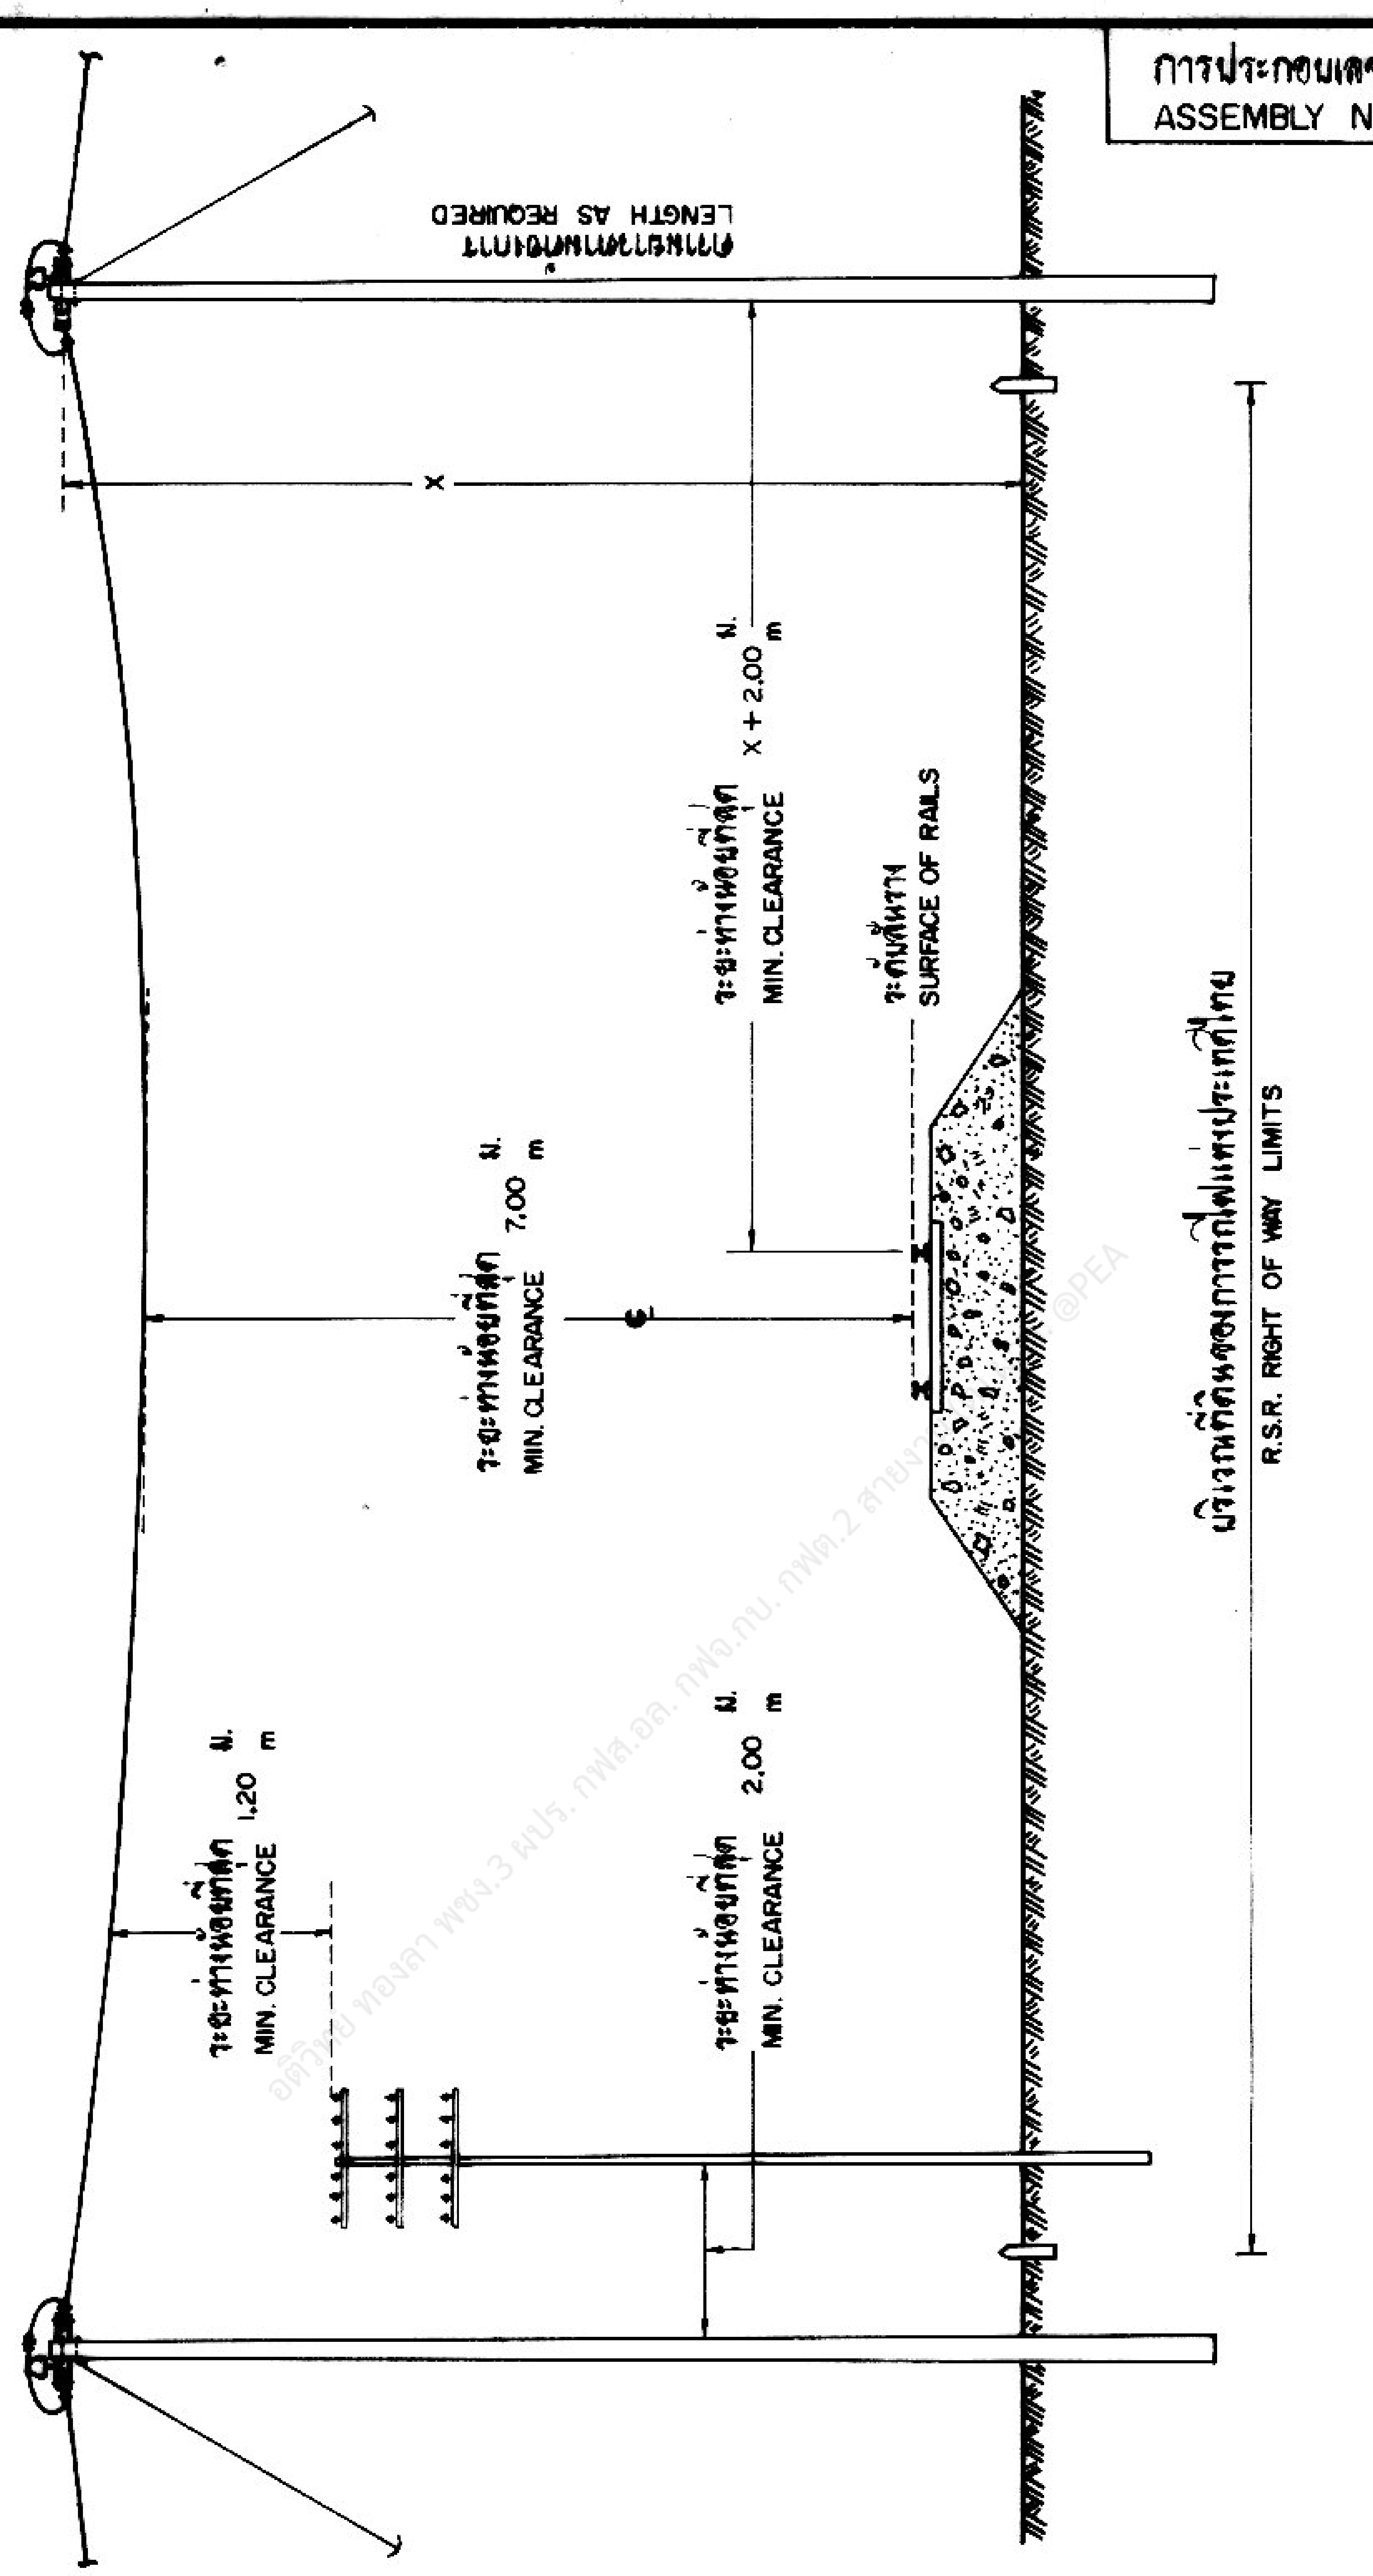
ความยาวตามต้องการ
LENGTH AS REQUIRED
X
ระยะห่างน้อยที่สุด MIN. CLEARANCE X + 2.00 ม. m
ระดับสันราง SURFACE OF RAILS
ระยะห่างน้อยที่สุด MIN. CLEARANCE 7.00 ม. m
ระยะห่างน้อยที่สุด MIN. CLEARANCE 1.20 ม. m
ระยะห่างน้อยที่สุด MIN. CLEARANCE 2.00 ม. m
บริเวณที่ดินของการรถไฟแห่งประเทศไทย
R.S.R. RIGHT OF WAY LIMITS

หมายเหตุ : ขนาดสายอะลูมิเนียมต่ำสุด 35 ต.มม. และระยะห่างระหว่างเสาสูงสุดไม่เกิน 50 ม.

NOTE : THE MINIMUM ALUMINIUM CONDUCTOR SIZE IS 35 mm² AND SPAN DOES NOT EXCEED 50 m.

อดิวิชย์ ทองลา พชง.3 ผปร. กฟส.อล. กฟจ.กบ. กฟต.2 สายงาน... @PEA

กองวิศวกรรมไฟฟ้าและเครื่องกล
ฝ่ายวิศวกรรม

ผู้เขียน
ผู้สำรวจ
วิศวกร
หัวหน้าแผนก
หัวหน้ากอง
ผู้อำนวยการฝ่าย
รองผู้ว่าการฝ่ายเทคนิค

การไฟฟ้าส่วนภูมิภาค

ผู้ว่าการ

12 ต.ค. 2520

การพาดสายแรงต่ำ ไม่เกิน 1 kV ข้ามทางรถไฟ
สำหรับสายเปลือย

L.T. LINE 1 kV OR LESS ACROSS THE RAILROAD
FOR BARE CONDUCTORS

ใช้แทนแบบ I50-015/080147
ถูกแทนโดยแบบ
เขียนเสร็จวันที่ 5 ต.ค. 20
แก้แบบวันที่
มิติเป็น
มาตราส่วน
แบบเลขที่ SAI-015/20022
แผ่นที่ 1 ของจำนวน 1 แผ่น